



INDICE

PLANOS ARQUITECTONICOS

- A-1.0 – INDICE Y UBICACION Y PLANTA DE TECHOS
- A-1.1 – PLANTA ARQUITECTONICA DE CONJUNTO
- A-1.2 – PLANTA ARQUITECTONICA PRIMER NIVEL
- A-1.3 – PLANTA ARQUITECTONICA SEGUNDO NIVEL
- A-2.1 – ELEVACION FRONTAL Y LATERAL DERECHO
- A-2.2 – ELEVACION POSTERIOR Y LATERAL IZQUIERDO
- A-3.1 – SECCION A-A’ Y B-B’

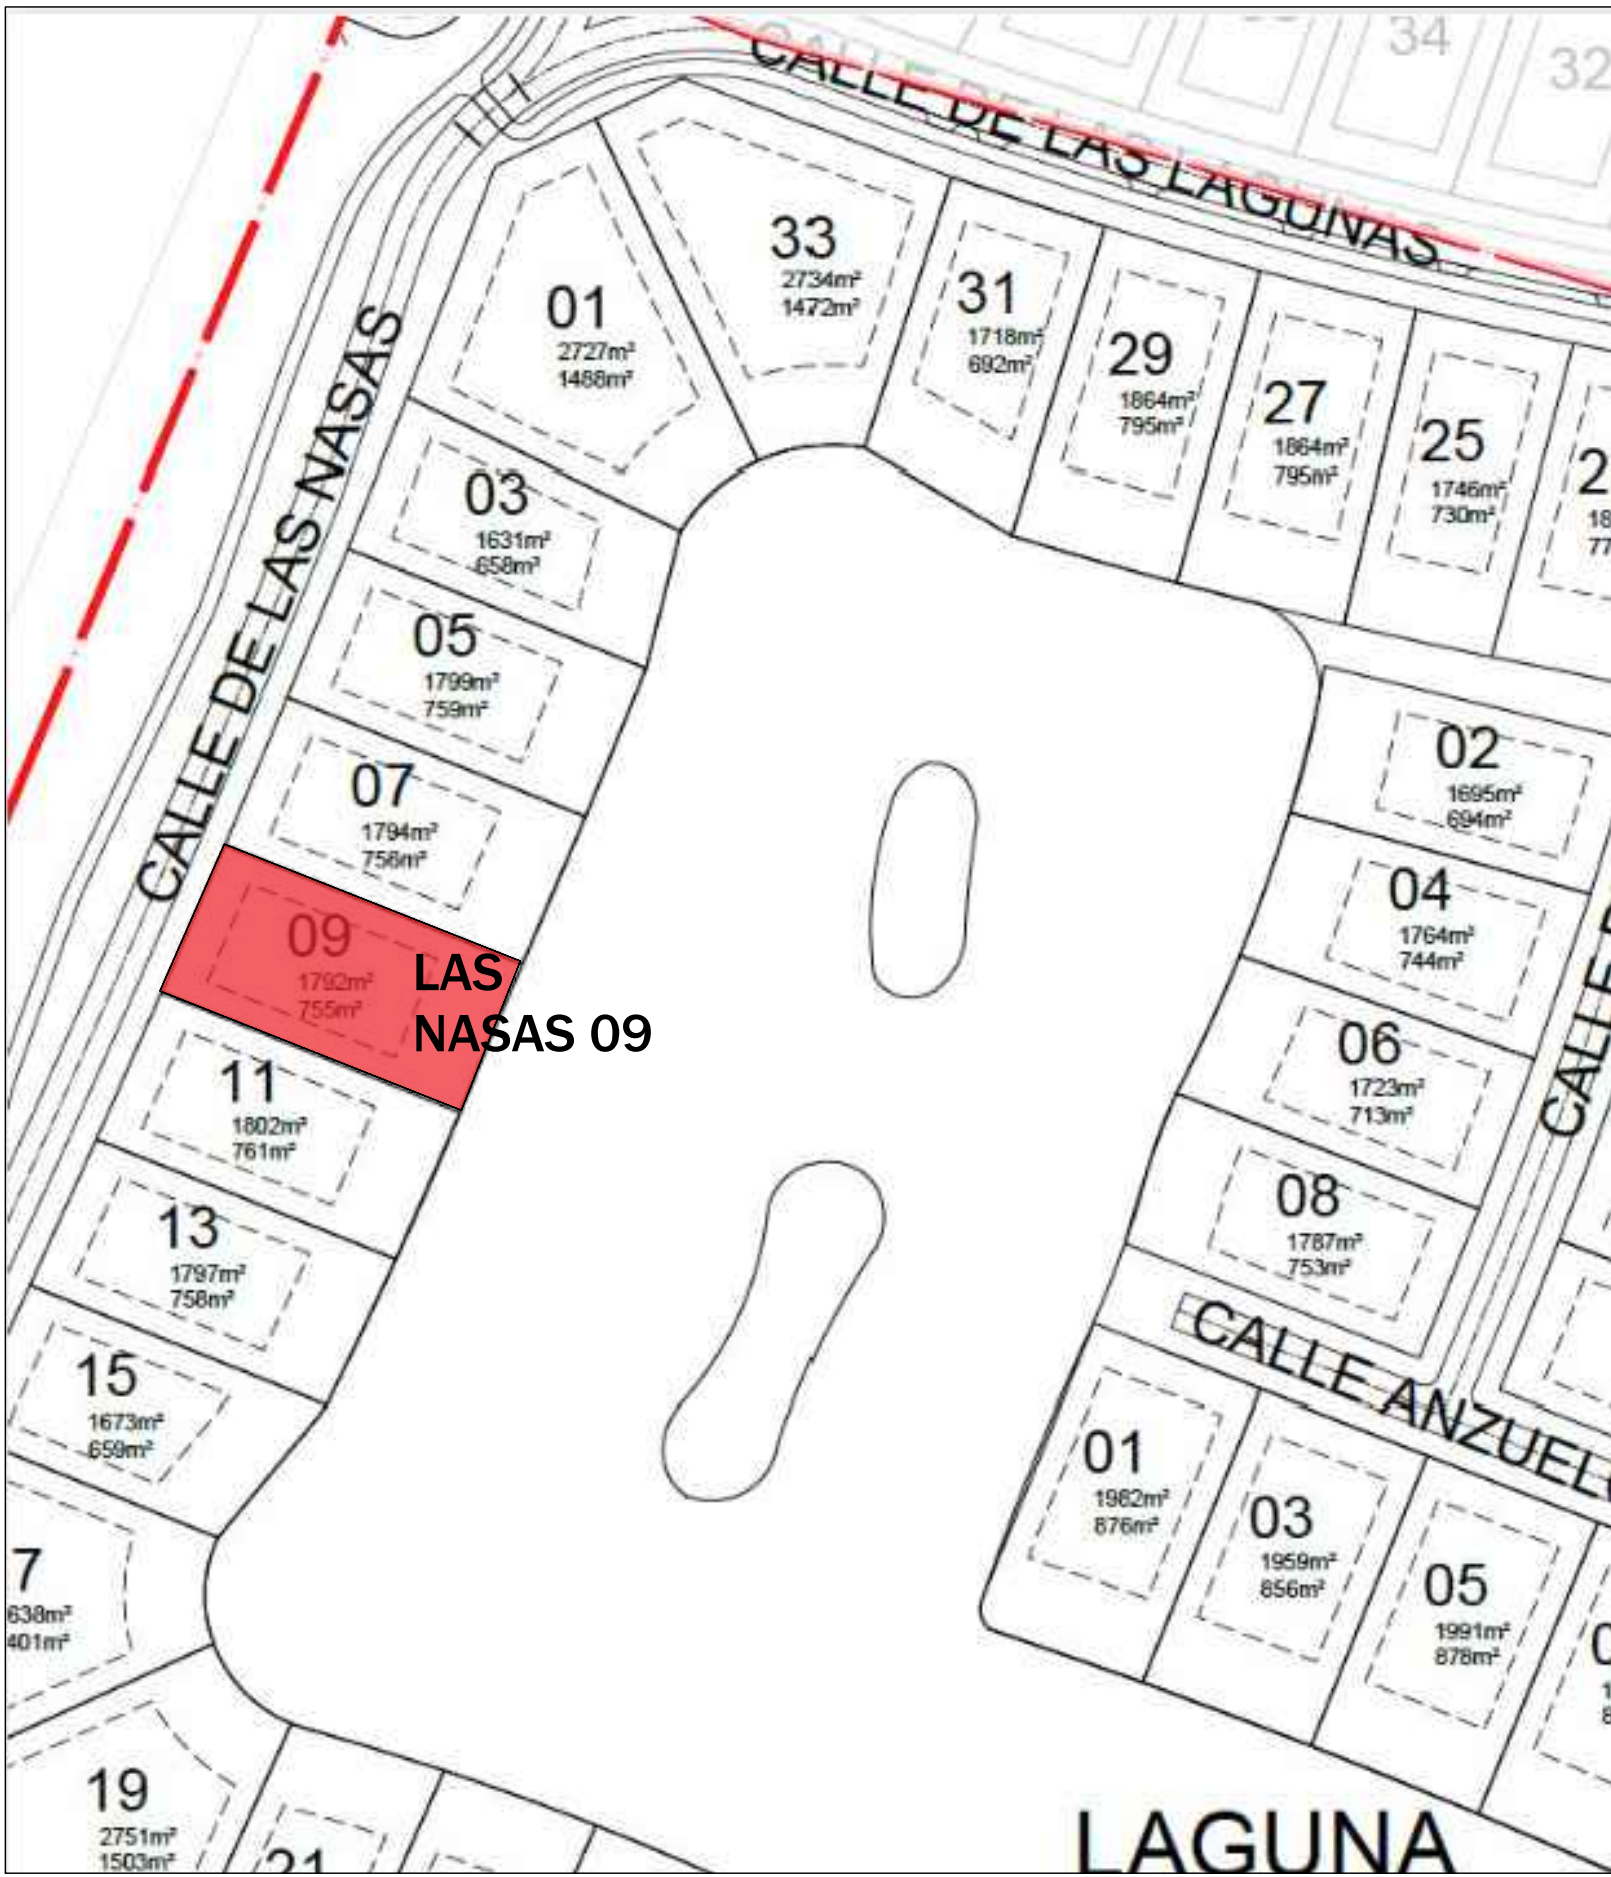

UBICACION LAS NASAS 09
PUNTACANA

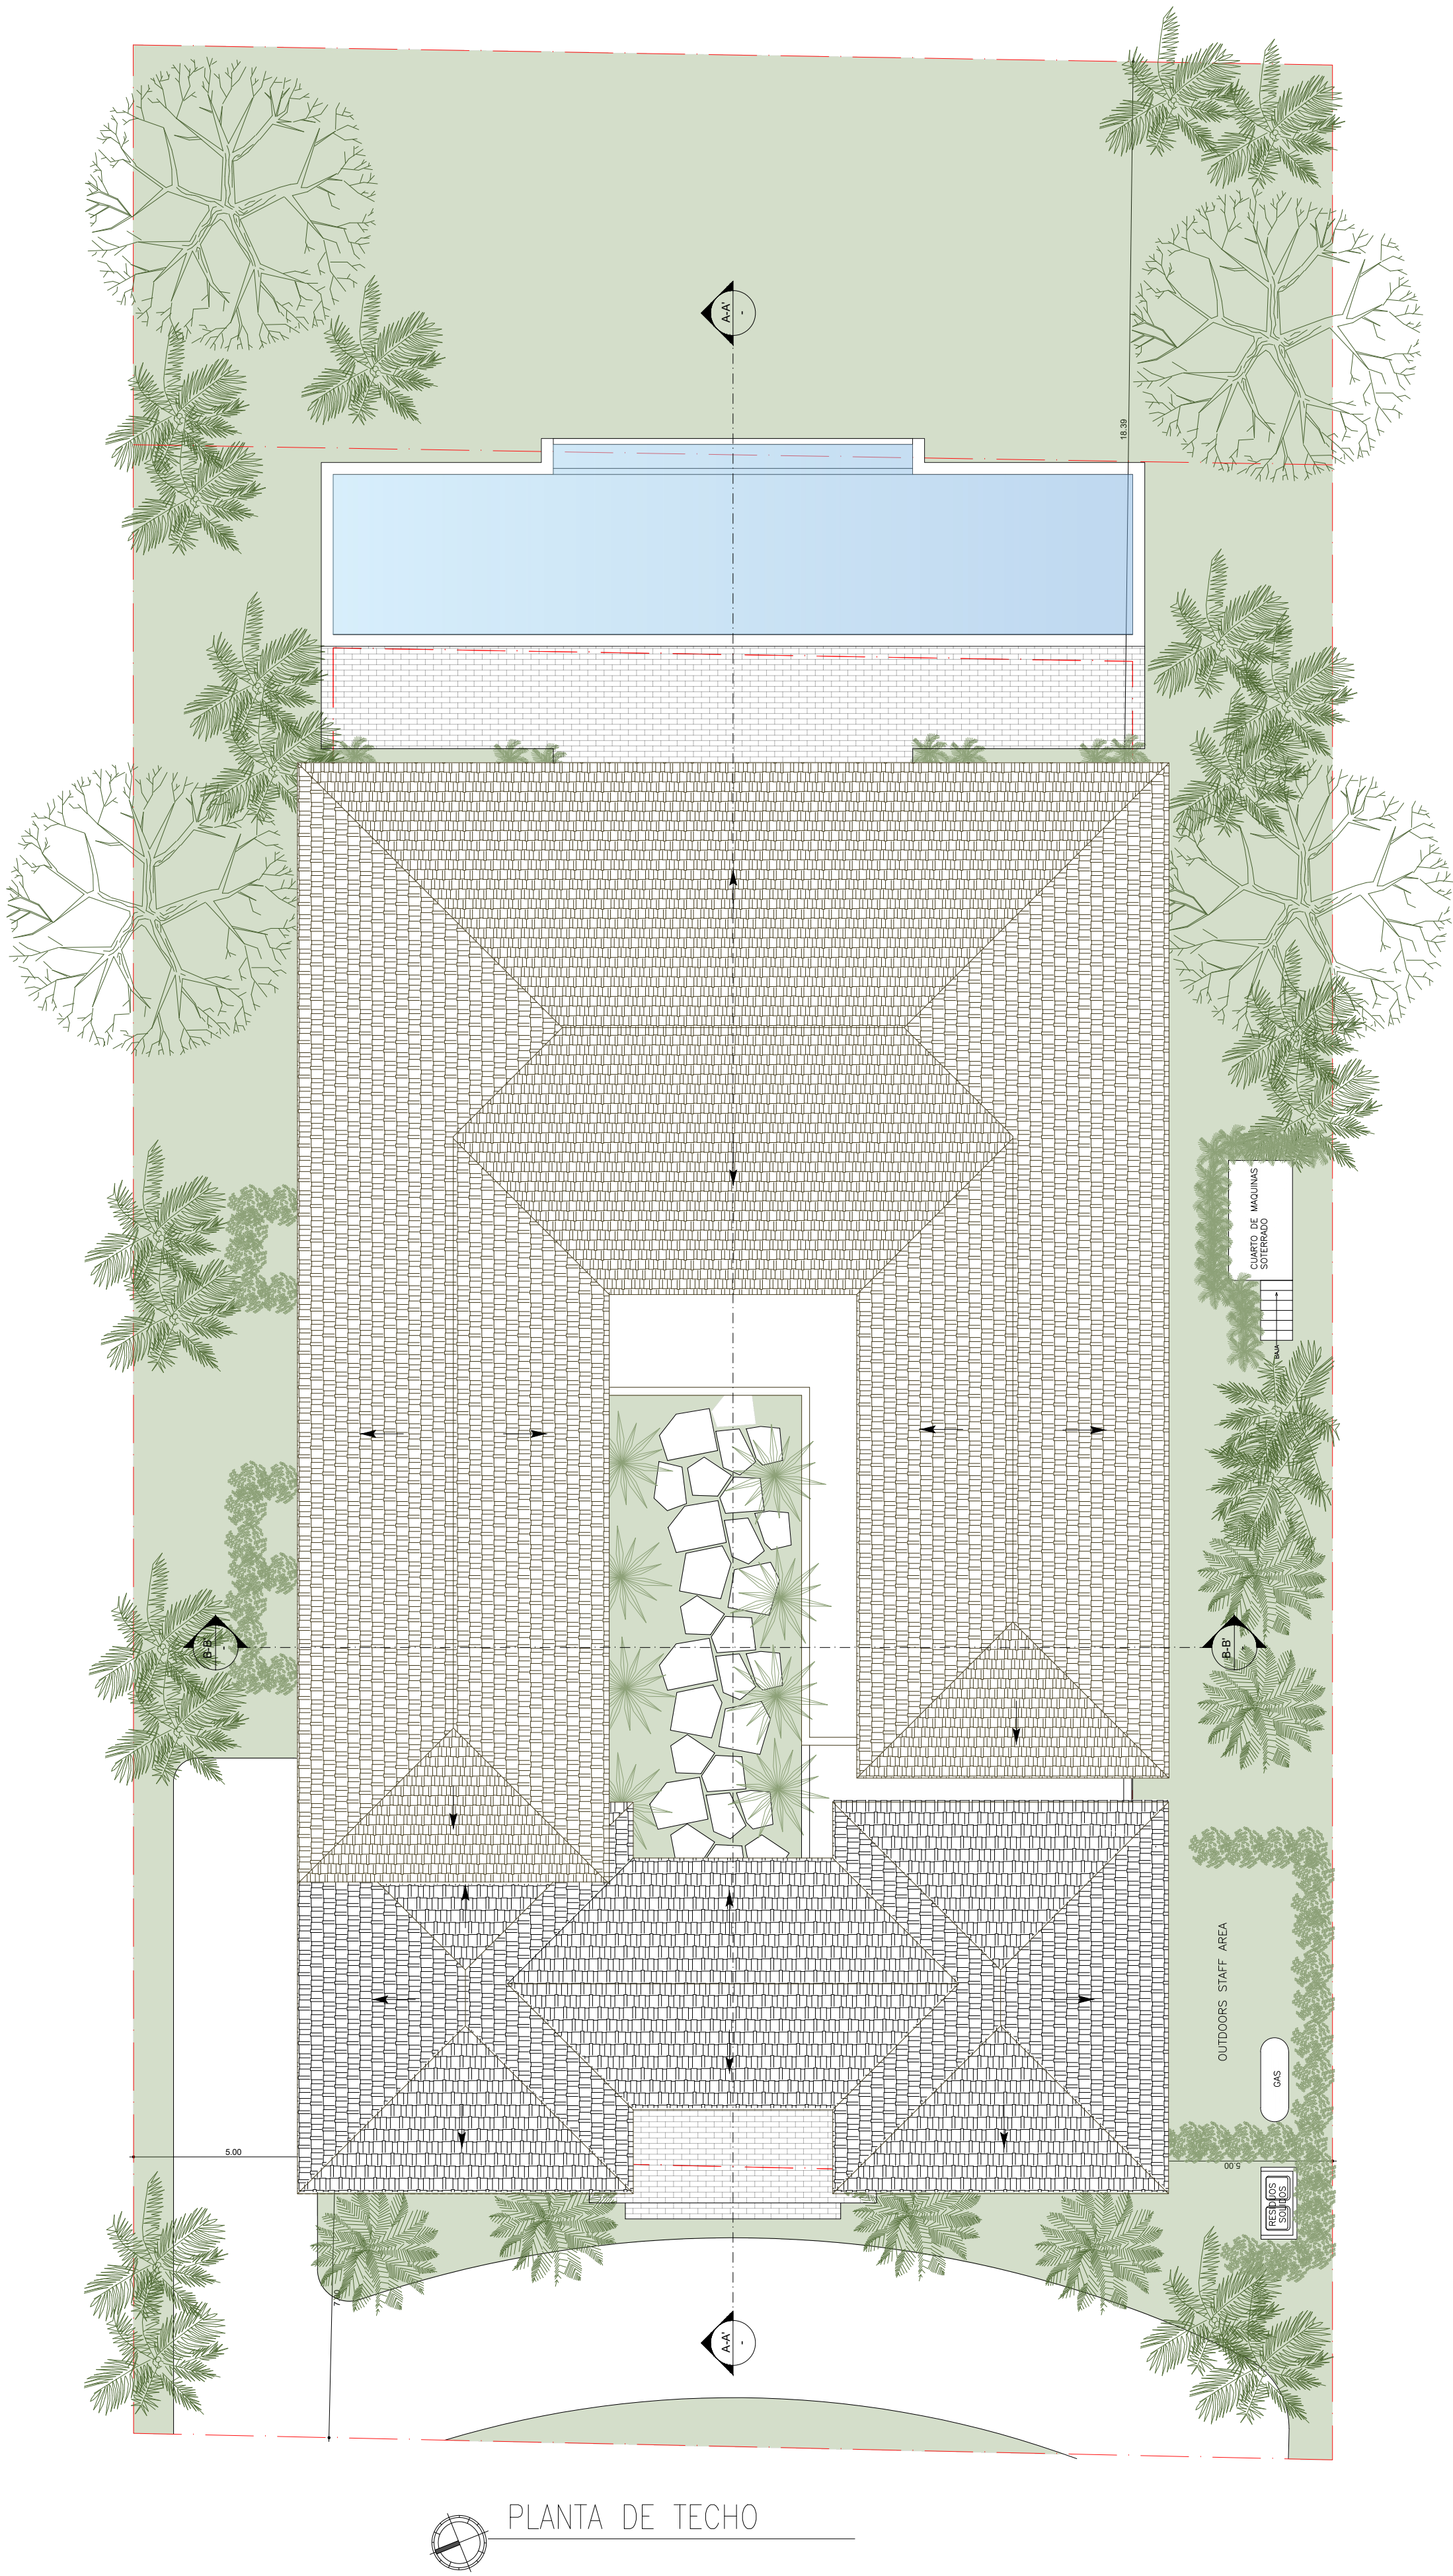

Galerías Puntacana 65
Puntacana Village
La Altagracia, República Dominicana
Tel: 809 831 0903
Cels: 809 350 1696 / 809 753 2262
E: desanglesabreuarquitectos@gmail.com

PROYECTO:

CASA ERNA
LAS NASAS 09

UBICACION:

LAS NASAS
PUNTACANA RESORT & CLUB

PROPIETARIO:

MR. JON KNAPP
MRS. MELISSA RACITI

FIRMA:

DISEÑO ARQ:

ARQ. MARIO E. DESANGLES
CODIA: 12067

ARQ. JANET ABREU DESANGLES

COLABORACION: ARQ. LADDY Y. BERROA
ARQ. MARIA C. FABIAN

DISEÑO INTERIOR:

DISEÑO ESTRUCTURAL:

DISEÑO SANITARIO:

DISEÑO ELECTRICO:

RESPONSABLE DE OBRA:

DISCIPLINA: PLANOS ARQUITECTONICOS

TIPOLOGIA: INDICE, UBICACION
Y PLANTA DE TECHO

ESCALA:

—

Nº DE HOJA:

A-1.0

FECHA:

NOV 2025



Galerías Puntacana 65
Puntacana Village
La Altagracia, República Dominicana
Tel: 809 831 0903
Cels: 809 350 1696 / 809 753 2262
E: desanglesabreuarquitectos@gmail.com

PROYECTO:

CASA ERNA
LAS NASAS 09

UBICACION:

LAS NASAS
PUNTACANA RESORT & CLUB

PROPIETARIO:

MR. JON KNAPP
MRS. MELISSA RACITI

FIRMA:

DISEÑO ARQ:

ARQ. MARIO E. DESANGLES
CODIA: 12067

ARQ. JANET ABREU DESANGLES

COLABORACION: ARQ. LADDY Y. BERROA
ARQ. MARIA C. FABIAN

DISEÑO INTERIOR:

DISEÑO ESTRUCTURAL:

DISEÑO SANITARIO:

DISEÑO ELECTRICO:

RESPONSABLE DE OBRA:

DISCIPLINA: PLANOS ARQUITECTONICOS

TIPOLOGIA: PLANTA ARQUITECTONICA
DE CONJUNTO

ESCALA:


1:100

Nº DE HOJA:

A-1.1


FECHA:

NOV 2025

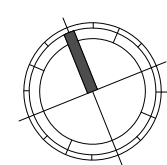

PLANTA ARQUITECTONICA PRIMER NIVEL

ESC. 1:75

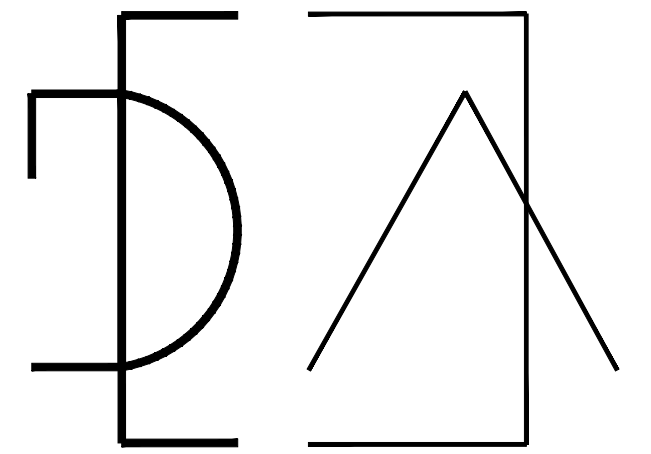

DESANGLES ABREU

Galerías Puntacana 65
Puntacana Village
La Altagracia, República Dominicana
Tel: 809 831 0903
Cels: 809 350 1696 / 809 753 2262
E: desanglesabreuarquitectos@gmail.com

PROYECTO:

CASA ERNA
LAS NASAS 09

UBICACION:

LAS NASAS
PUNTACANA RESORT & CLUB

PROPIETARIO:

MR. JON KNAPP
MRS. MELISSA RACITI

FIRMA:

DISEÑO ARQ:

ARQ. MARIO E. DESANGLES
CODIA: 12067

ARQ. JANET ABREU DESANGLES

COLABORACION: ARQ. LADDY Y. BERROA
ARQ. MARIA C. FABIAN

DISEÑO INTERIOR:

DISEÑO ESTRUCTURAL:

DISEÑO SANITARIO:

DISEÑO ELECTRICO:

RESPONSABLE DE OBRA:



DISCIPLINA: PLANOS ARQUITECTONICOS

TIPOLOGIA: PLANTA ARQUITECTONICA
PRIMER NIVEL

ESCALA:
1:75

Nº DE HOJA:
A-1.2

FECHA:
NOV 2025

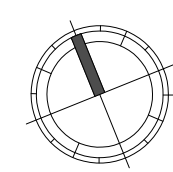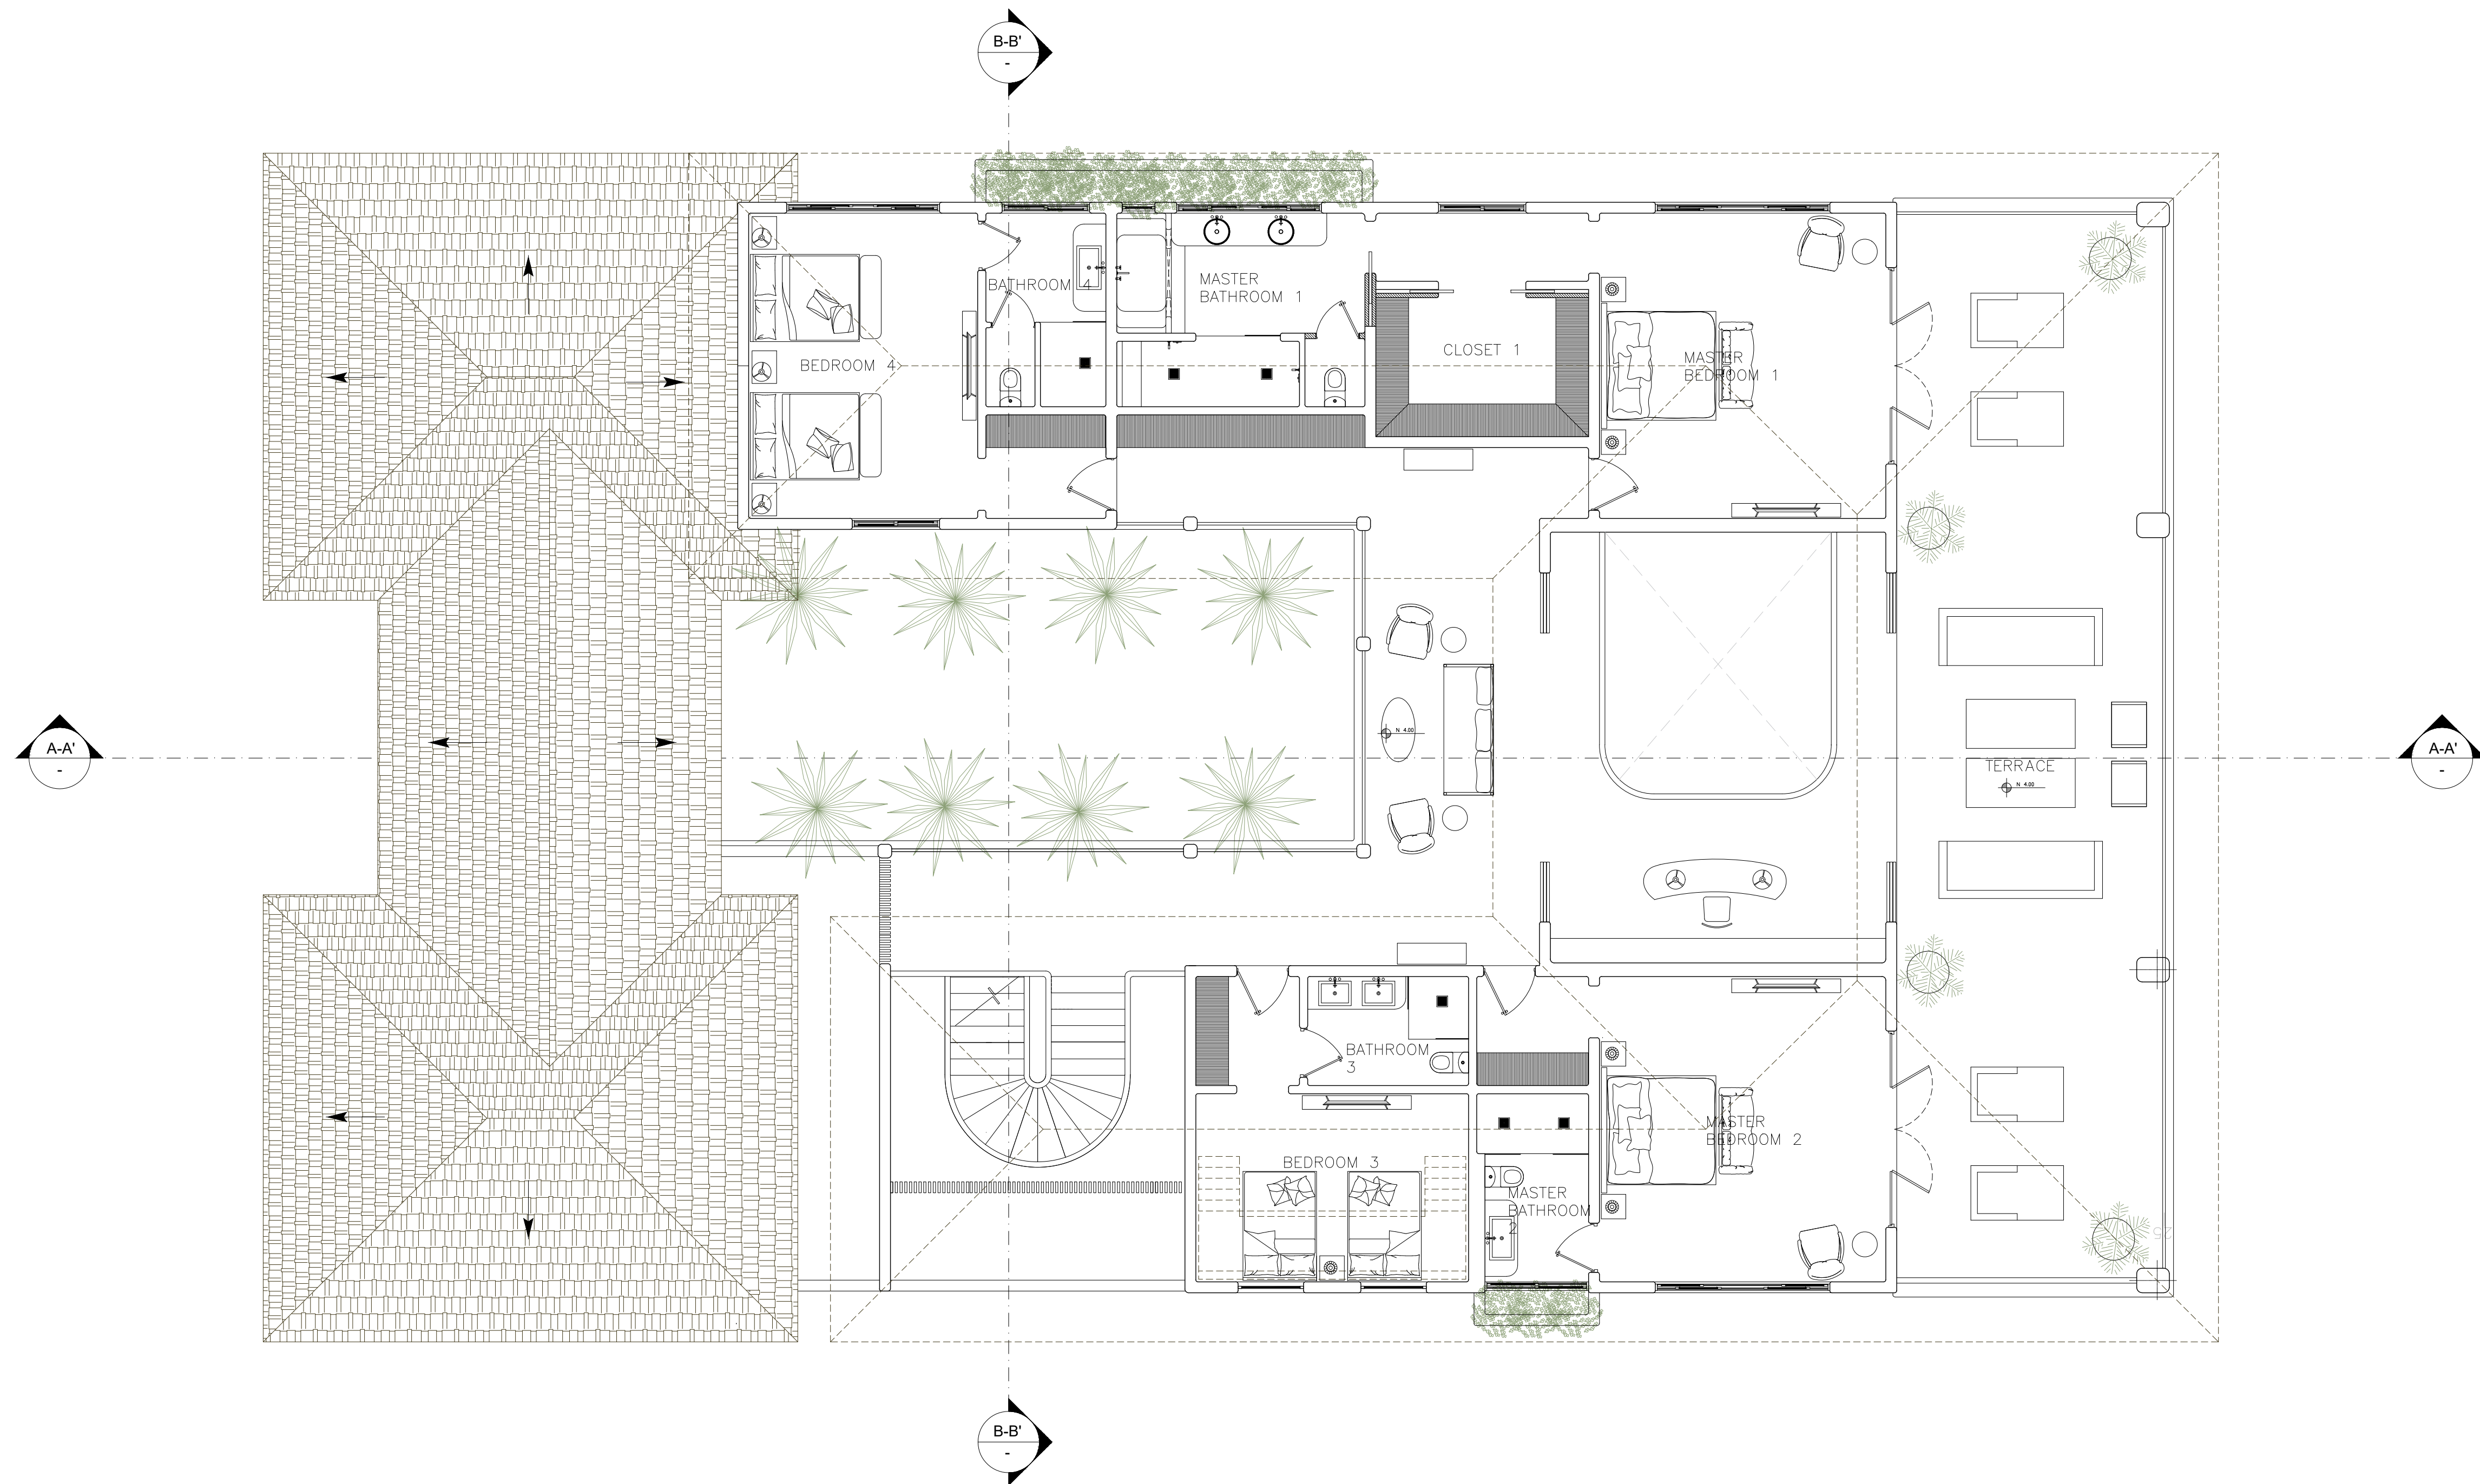

PLANTA ARQUITECTONICA SEGUNDO NIVEL
ESC. 1:75



Galerías Puntacana 65
Puntacana Village
La Altagracia, República Dominicana
Tel: 809 831 0903
Cels: 809 350 1696 / 809 753 2262
E: desanglesabreuarquitectos@gmail.com

PROYECTO:

CASA ERNA
LAS NASAS 09

UBICACION:

LAS NASAS
PUNTACANA RESORT & CLUB

PROPIETARIO:

MR. JON KNAPP
MRS. MELISSA RACITI

FIRMA:

DISEÑO ARQ:

ARQ. MARIO E. DESANGLES
CODIA: 12067

ARQ. JANET ABREU DESANGLES

COLABORACION: ARQ. LADDY Y. BERROA
ARQ. MARIA C. FABIAN

DISEÑO INTERIOR:

DISEÑO ESTRUCTURAL:

DISEÑO SANITARIO:

DISEÑO ELECTRICO:

RESPONSABLE DE OBRA:


DISCIPLINA: PLANOS ARQUITECTONICOS

TIPOLOGIA: PLANTA ARQUITECTONICA
SEGUNDO NIVEL

ESCALA:
1:75


Nº DE HOJA:
A-1.3

FECHA:
NOV 2025

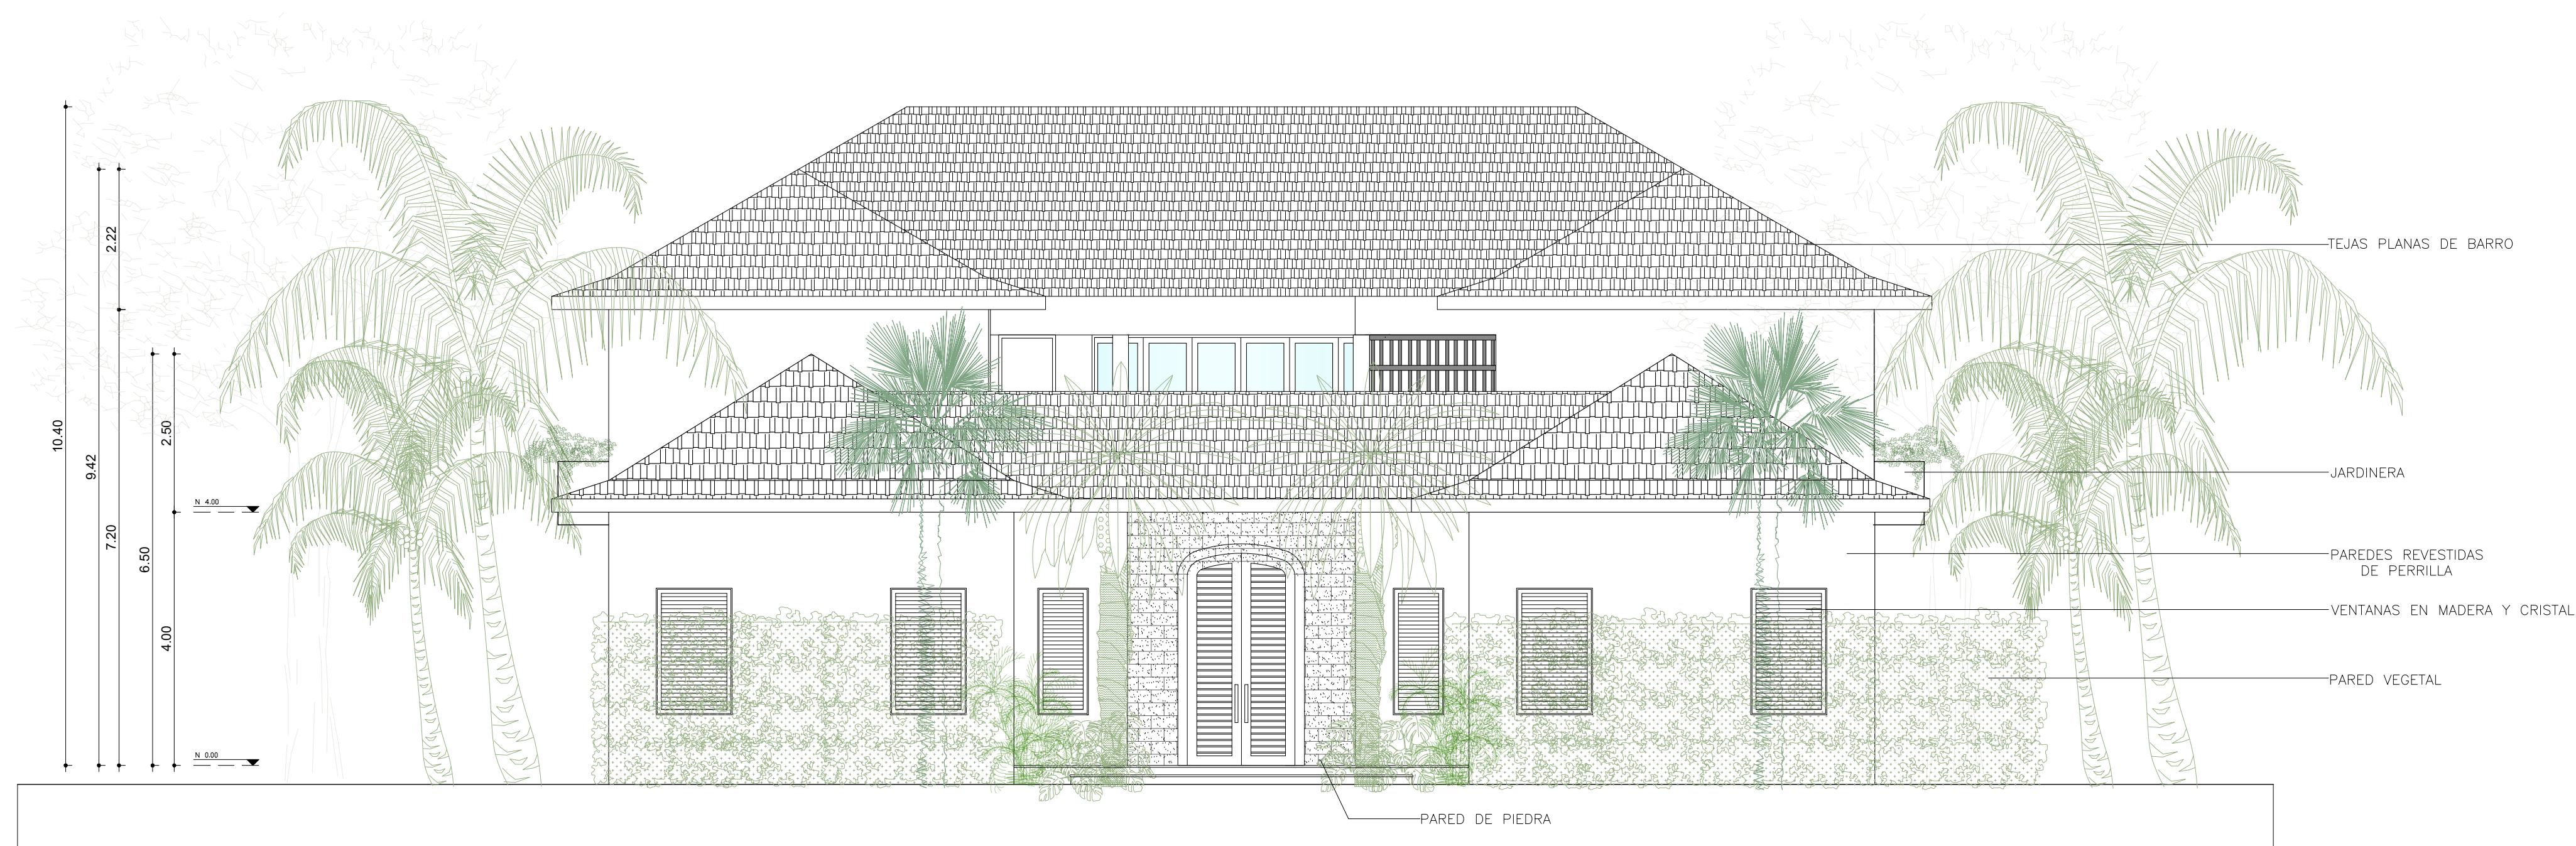

ELEVACION FRONTAL

ESC. 1:75

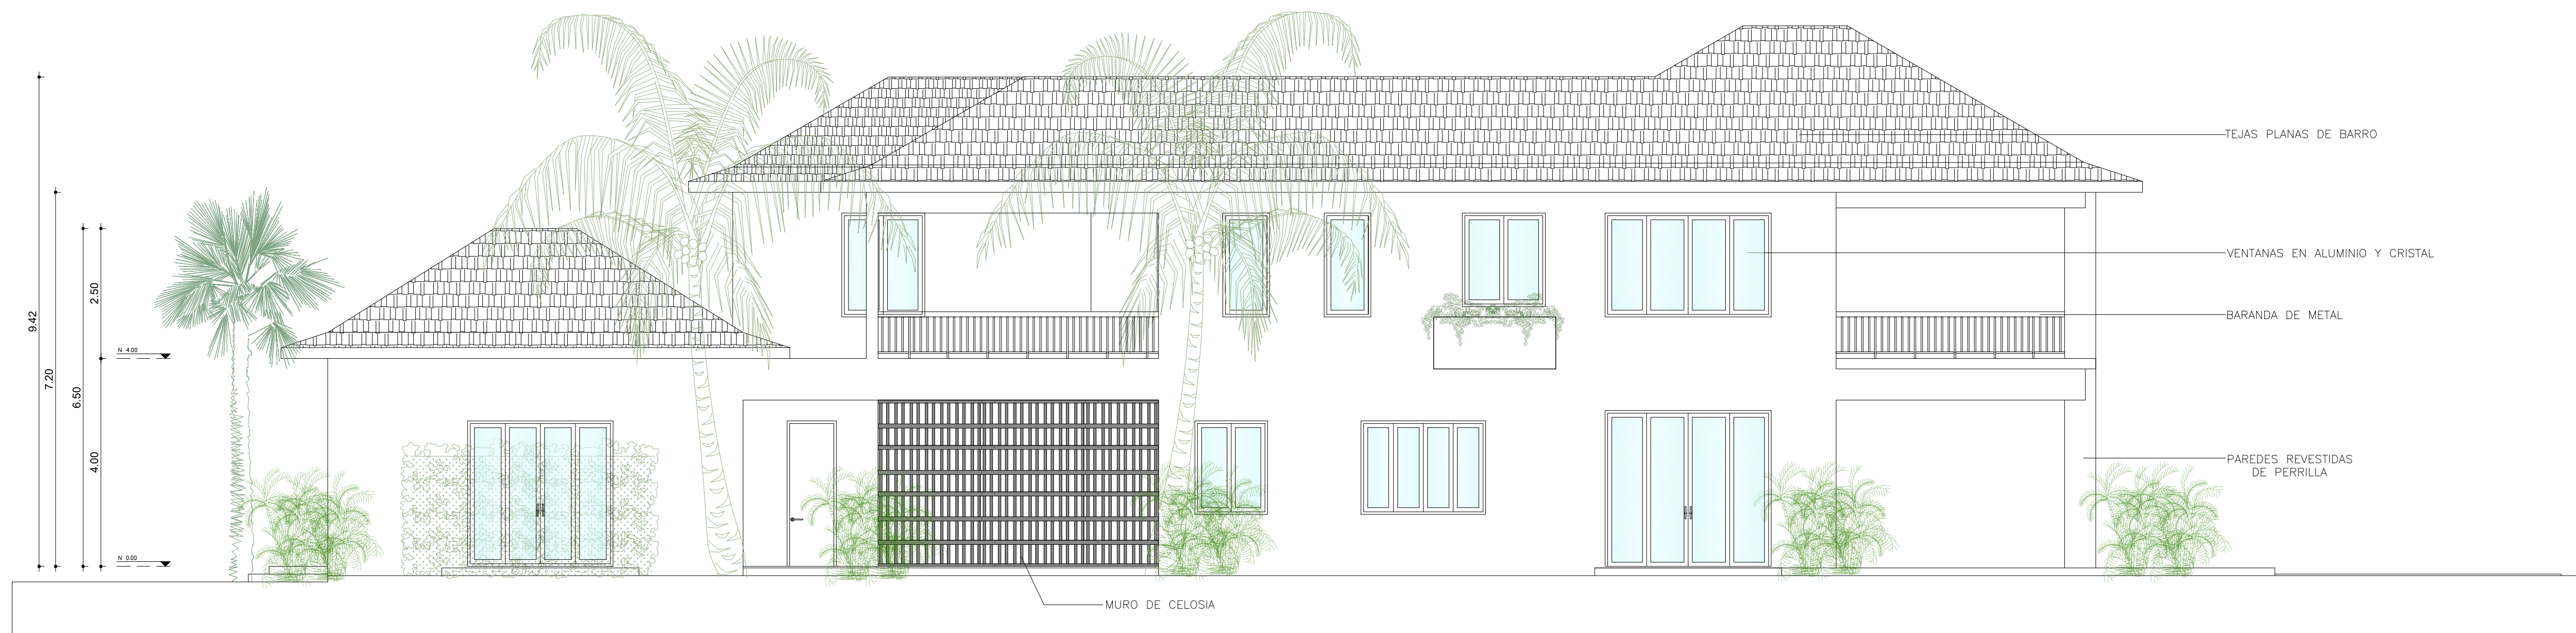

ELEVACION LATERAL DERECHO

ESC. 1:75



Galerías Puntacana 65
Puntacana Village
La Altagracia, República Dominicana
Tel: 809 831 0903
Cels: 809 350 1696 / 809 753 2262
E: desanglesabreuarquitectos@gmail.com

PROYECTO:

CASA ERNA
LAS NASAS 09

UBICACION:

LAS NASAS
PUNTACANA RESORT & CLUB

PROPIETARIO:

MR. JON KNAPP
MRS. MELISSA RACITI

FIRMA:

DISEÑO ARQ:

ARQ. MARIO E. DESANGLES
CODIA: 12067

ARQ. JANET ABREU DESANGLES

COLABORACION: ARQ. LADDY Y. BERROA
ARQ. MARIA C. FABIAN

DISEÑO INTERIOR:

DISEÑO ESTRUCTURAL:

DISEÑO SANITARIO:

DISEÑO ELECTRICO:

RESPONSABLE DE OBRA:

DISCIPLINA: PLANOS ARQUITECTONICOS

TIPOLOGIA: ELEVACIONES

ESCALA:
1:75


Nº DE HOJA:
A-2.1

FECHA:
NOV 2025



ELEVACION POSTERIOR

ESC. 1:75

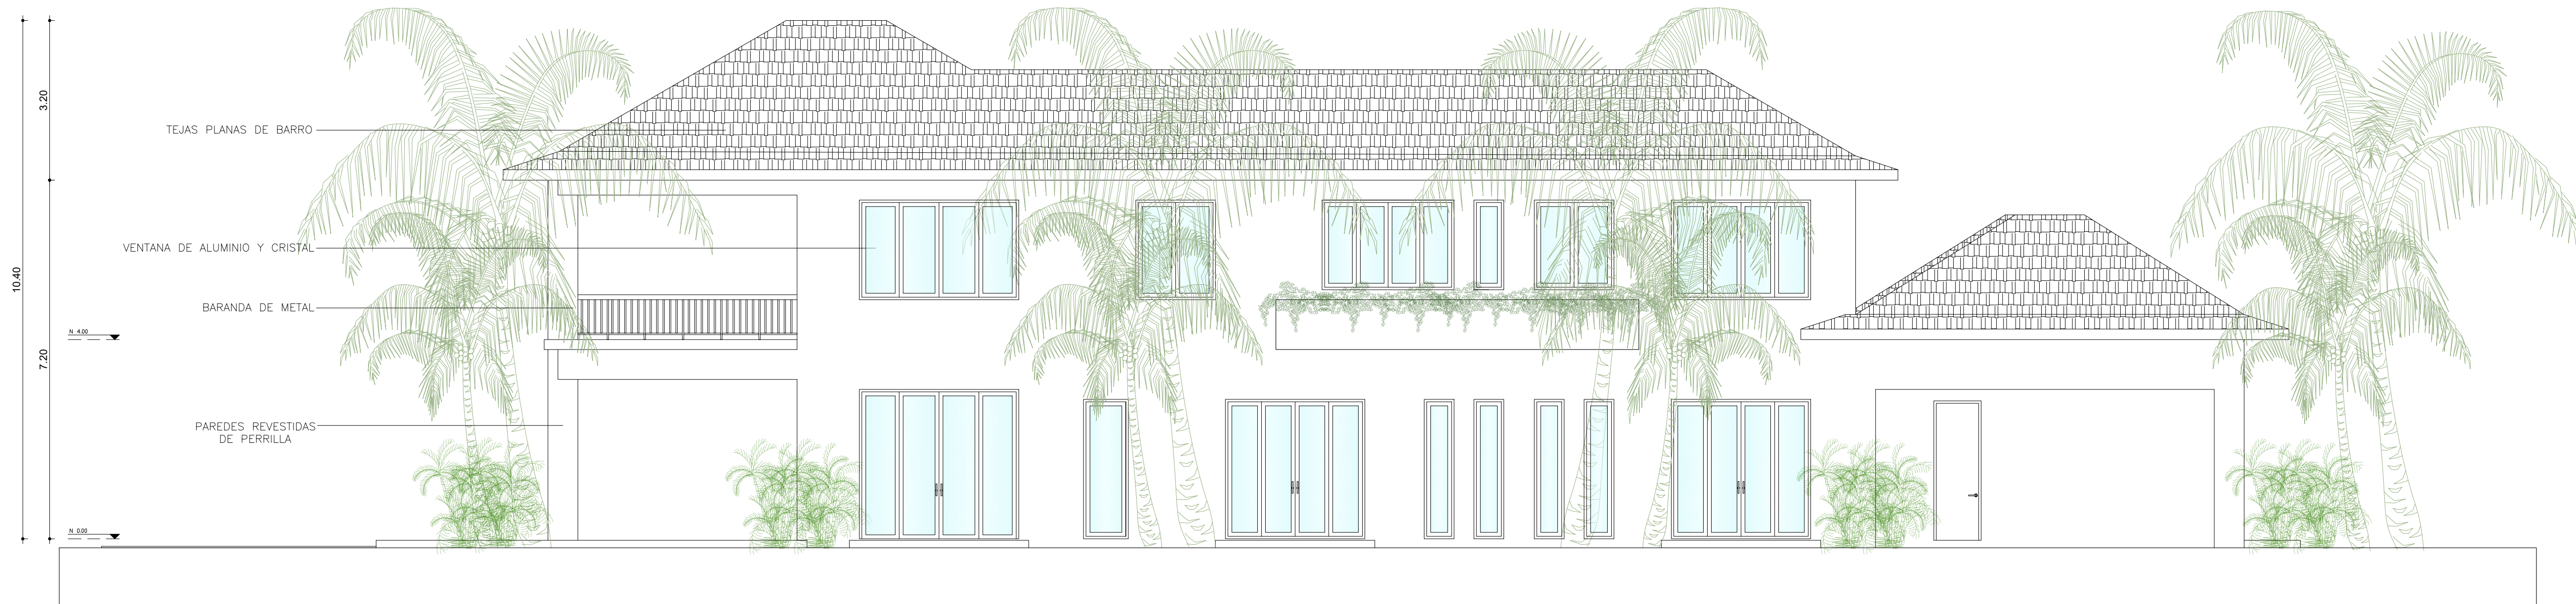

ELEVACION LATERAL IZQUIERDO

ESC. 1:75



Galerías Puntacana 65
Puntacana Village
La Altagracia, República Dominicana
Tel: 809 831 0903
Cels: 809 350 1696 / 809 753 2262
E: desanglesabreuarquitectos@gmail.com

PROYECTO:

CASA ERNA
LAS NASAS 09

UBICACION:

LAS NASAS
PUNTACANA RESORT & CLUB

PROPIETARIO:

MR. JON KNAPP
MRS. MELISSA RACITI

FIRMA:

DISEÑO ARQ:

ARQ. MARIO E. DESANGLES
CODIA: 12067

ARQ. JANET ABREU DESANGLES

COLABORACION: ARQ. LADDY Y. BERROA
ARQ. MARIA C. FABIAN

DISEÑO INTERIOR:

DISEÑO ESTRUCTURAL:

DISEÑO SANITARIO:

DISEÑO ELECTRICO:

RESPONSABLE DE OBRA:


DISCIPLINA: PLANOS ARQUITECTONICOS

TIPOLOGIA: ELEVACIONES

ESCALA:
1:75

Nº DE HOJA:
A-2.2

FECHA:
NOV 2025

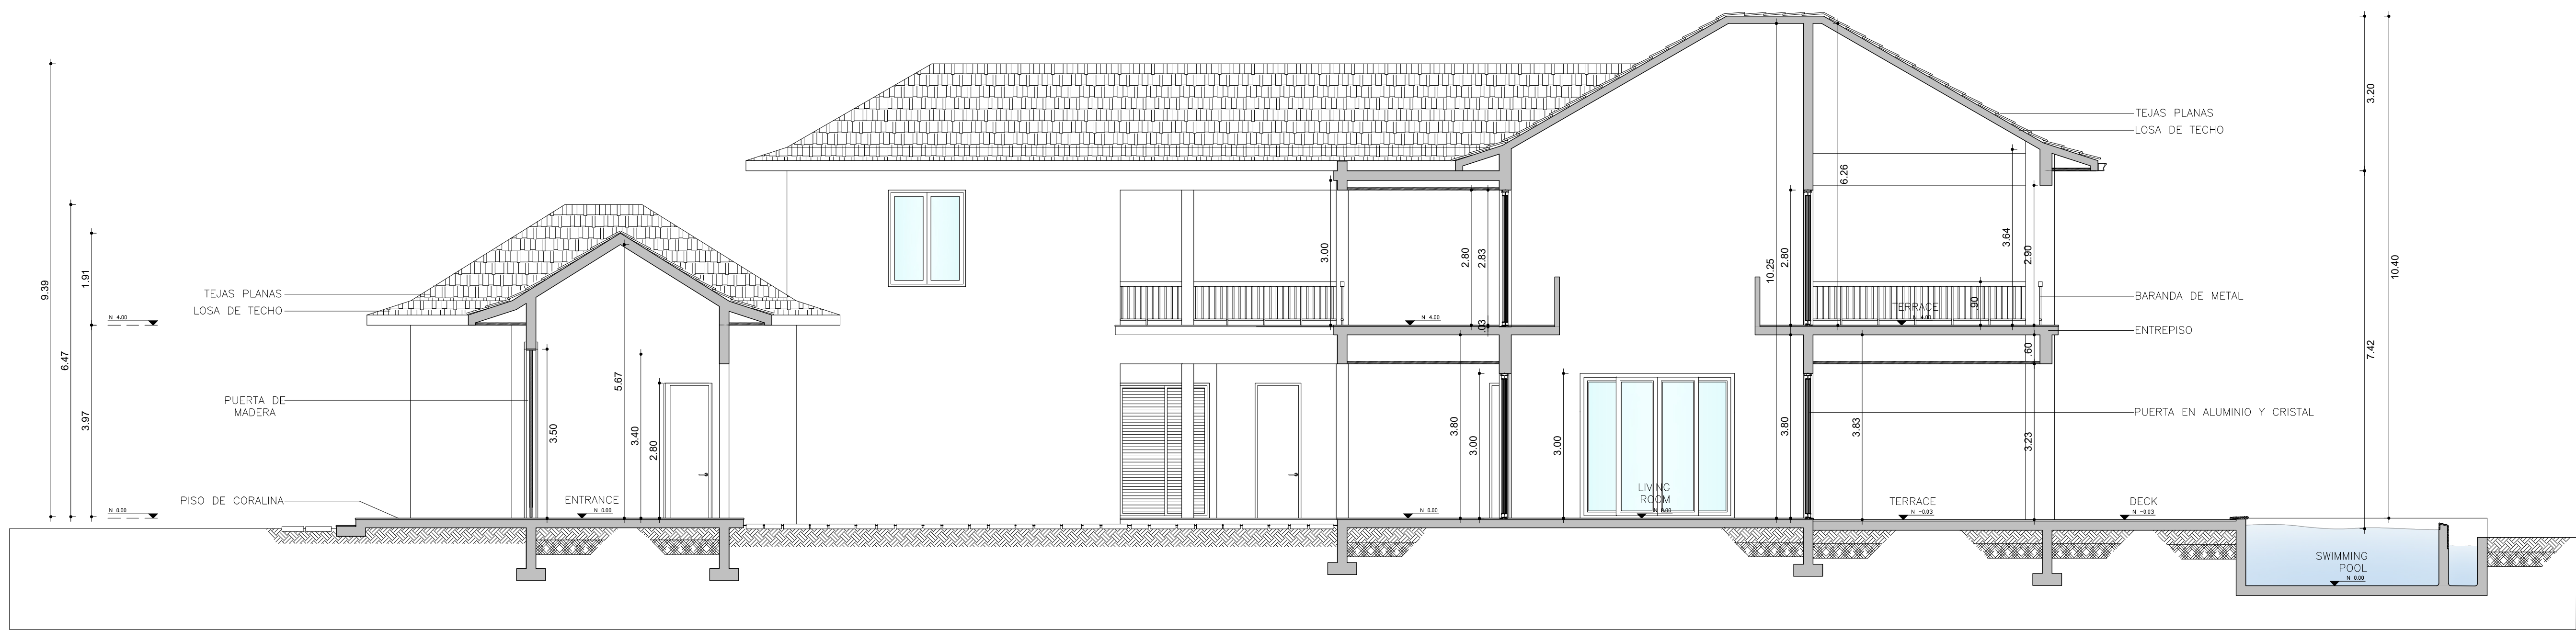

SECCION A-A'
ESC. 1:75



SECCION B-B'
ESC. 1:75



Galerías Puntacana 65
Puntacana Village
La Altagracia, República Dominicana
Tel: 809 831 0903
Cels: 809 350 1696 / 809 753 2262
E: desanglesabreuarquitectos@gmail.com

PROYECTO:

CASA ERNA
LAS NASAS 09

UBICACION:

LAS NASAS
PUNTACANA RESORT & CLUB

PROPIETARIO:

MR. JON KNAPP
MRS. MELISSA RACITI

FIRMA:

DISEÑO ARQ:

ARQ. MARIO E. DESANGLES
CODIA: 12067

ARQ. JANET ABREU DESANGLES

COLABORACION: ARQ. LADDY Y. BERROA
ARQ. MARIA C. FABIAN

DISEÑO INTERIOR:

DISEÑO ESTRUCTURAL:

DISEÑO SANITARIO:

DISEÑO ELECTRICO:

RESPONSABLE DE OBRA:

DISCIPLINA: PLANOS ARQUITECTONICOS

TIPOLOGIA: SECCIONES

ESCALA:

1:75

Nº DE HOJA:

A-3.1

FECHA:

NOV 2025