

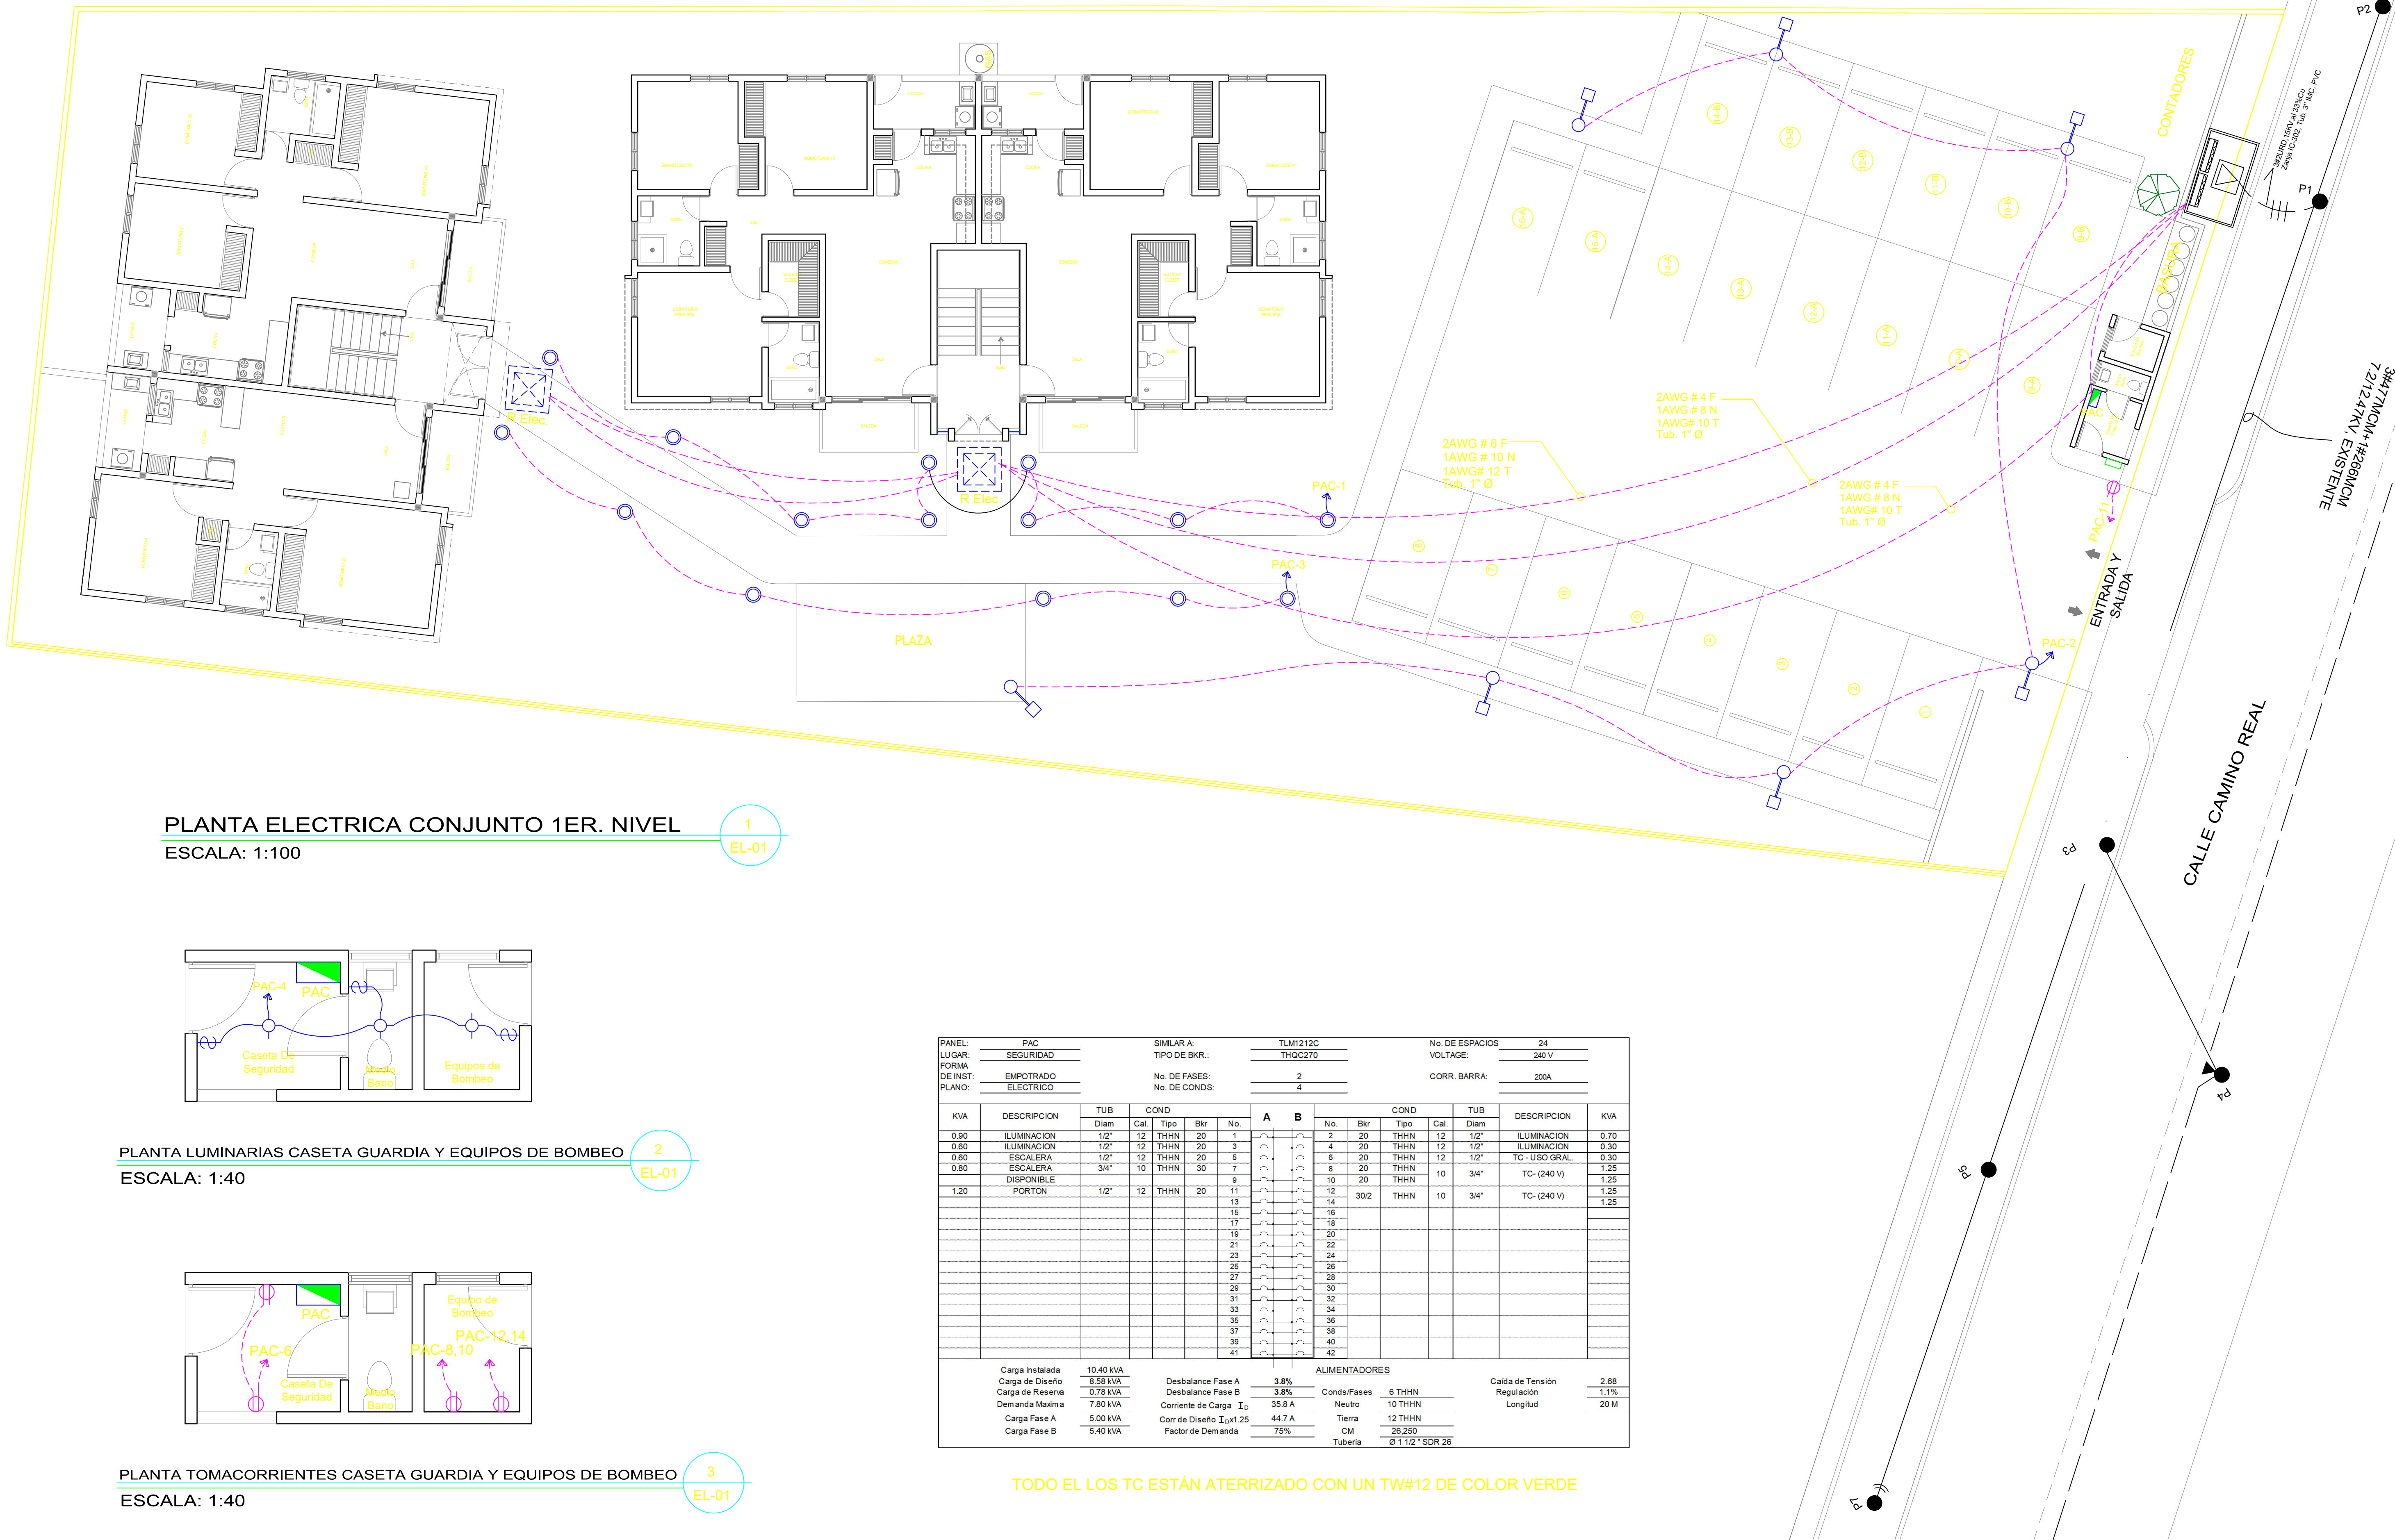


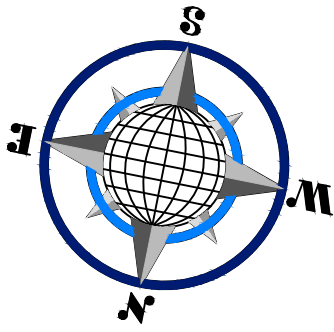


PLANTA ELECTRICA CONJUNTO 1ER. NIVEL
ESCALA: 1:100

1
EL-01

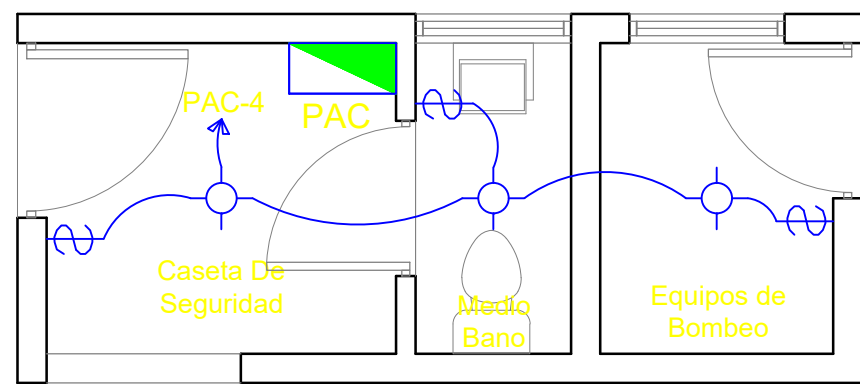

PLANTA LUMINARIAS CASETA GUARDIA Y EQUIPOS DE BOMBEO
ESCALA: 1:40

2
EL-01

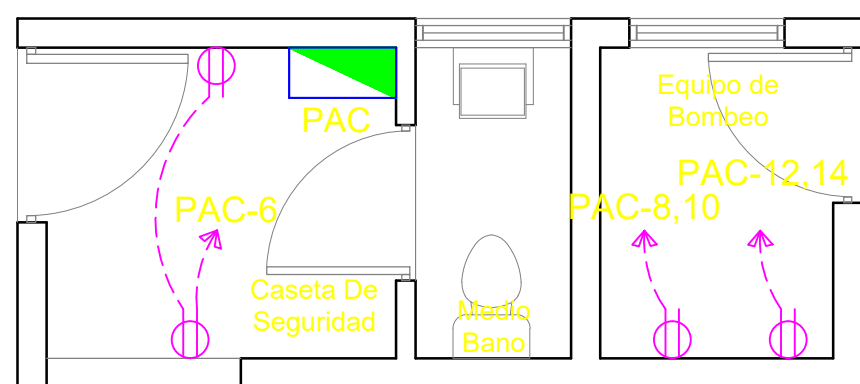

PLANTA TOMACORRIENTES CASETA GUARDIA Y EQUIPOS DE BOMBEO
ESCALA: 1:40

3
EL-01

PANEL: PAC		SIMILAR A:		TLM1212C		No. DE ESPACIOS: 24									
LUGAR: SEGURIDAD		TIPO DE BKR.:		THG270		VOLTAGE: 240 V									
FORMA: EMPOTRADO		No. DE FASES:		2		CORR. BARRA: 200A									
DE INST: ELECTRICO		No. DE CONDS:		4											
PLANO:															
KVA	DESCRIPCION	TUB		COND		A		B		COND		TUB		DESCRIPCION	KVA
		Diam	Cal. Tipo	Bkr	No.			No.	Bkr	Typo	Cal.	Diam			
0.80	ILUMINACION	1/2"	12	THHN	20	1		2	20	THHN	12	1/2"		ILUMINACION	0.70
0.80	ILUMINACION	1/2"	12	THHN	20	3		4	20	THHN	12	1/2"		ILUMINACION	0.30
0.80	ESCALERA	1/2"	12	THHN	20	5		6	20	THHN	12	1/2"		TC- USO GRAL.	0.30
0.80	ESCALERA	3/4"	10	THHN	30	7		8	20	THHN	10	3/4"		TC- (240 V)	1.25
						9		10	20	THHN					1.25
1.20	PORTON	1/2"	12	THHN	20	11		12	30/2	THHN	10	3/4"		TC- (240 V)	1.25
						13		14							1.25
						15		16							
						17		18							
						19		20							
						21		22							
						23		24							
						25		26							
						27		28							
						29		30							
						31		32							
						33		34							
						35		36							
						37		38							
						39		40							
						41		42							
		</													

TODO EL LOS TC ESTÁN ATERORIZADO CON UN TW#12 DE COLOR VERDE



diaz melo & asocs.
ARQUITECTOS
Presidente Billini # 12, Bani, R.D. 522-4989
E-mail: diazmelo@hotmail.com

COLABORACION:



ARQUITECTURA DIGITAL
DISEÑOS-CONSTRUCCION-DIGITACION
COMPROMETIDOS CON SU TIEMPO
C/JUAN SANCHEZ RAMIREZ #56,
LOCAL 5 ZONA UASD TEL:221-5400

PROPIETARIO:

GRUPO EMPRESARIAL
BANILEJO S.R.L.
GEBSA

PROYECTISTAS:

DISEÑO ARQUITECTONICO:
DIAZMELO & ASOCS.

Arq. ISMAEL DIAZ MELO
Codia: 9604

DISEÑO SANITARIO:

Arq. HAMLET TEJEDA
Codia: 18303

DISEÑO ESTRUCTURAL:

ING. ODELIN TEJEDA
Codia: 23937

DISEÑO ELECTRICO:

ING. VILLYS SANCHEZ
Codia: 19060

CONTENIDO:

PLANTA ELECTRICA
1ER. NIVEL CONJUNTO

PROYECTO:

RESIDENCIAL GEBSA IV

Fecha: MAYO/2018

UBICACION:


SOMBREIRO, BANI, PROV. PERAVIA

Ref.: Acad 2000

Hoja No.

Escala: INDICADA


NOTAS:
TODAS LAS TERMINACIONES Y/O CAMBIOS EN EL SET DE DOCUMENTOS
CONSTRUCTIVOS DEBERAN SER APROBADOS POR EL SUPERVISOR
PREVIAMENTE A SU APLICACION EN LA OBRA
TODAS LAS MEDIDAS DE HUECOS Y DE SUPERFICIE A SER REVESTIDAS
SERAN RECTIFICADAS PREVIA FABRICACION DE LOS CORRIENTES O LA
O LA INSTALACION DE LOS RECURBIMIENTOS
LAS TERMINACIONES Y / O DETALLES NO ESPECIFICADOS SERAN
DEFINIDOS ENTRE
EL DUEÑO Y EL AUTOR DEL PROYECTO
EL CONTRATISTA NO PODRA TOMAR DECISIONES
INCONSULTAS RESPECTO VARIACIONES EN EL CONTENIDO
DE ESTE DOCUMENTO
LOS PLANOS ARQUITECTONICOS MANDARAN RESPECTO A LOS DEMAS A
ANTE CUALQUIER
DIFERENCIA, PRIMARA LA INFORMACIONCONTENIDA EN LOS MISMOS


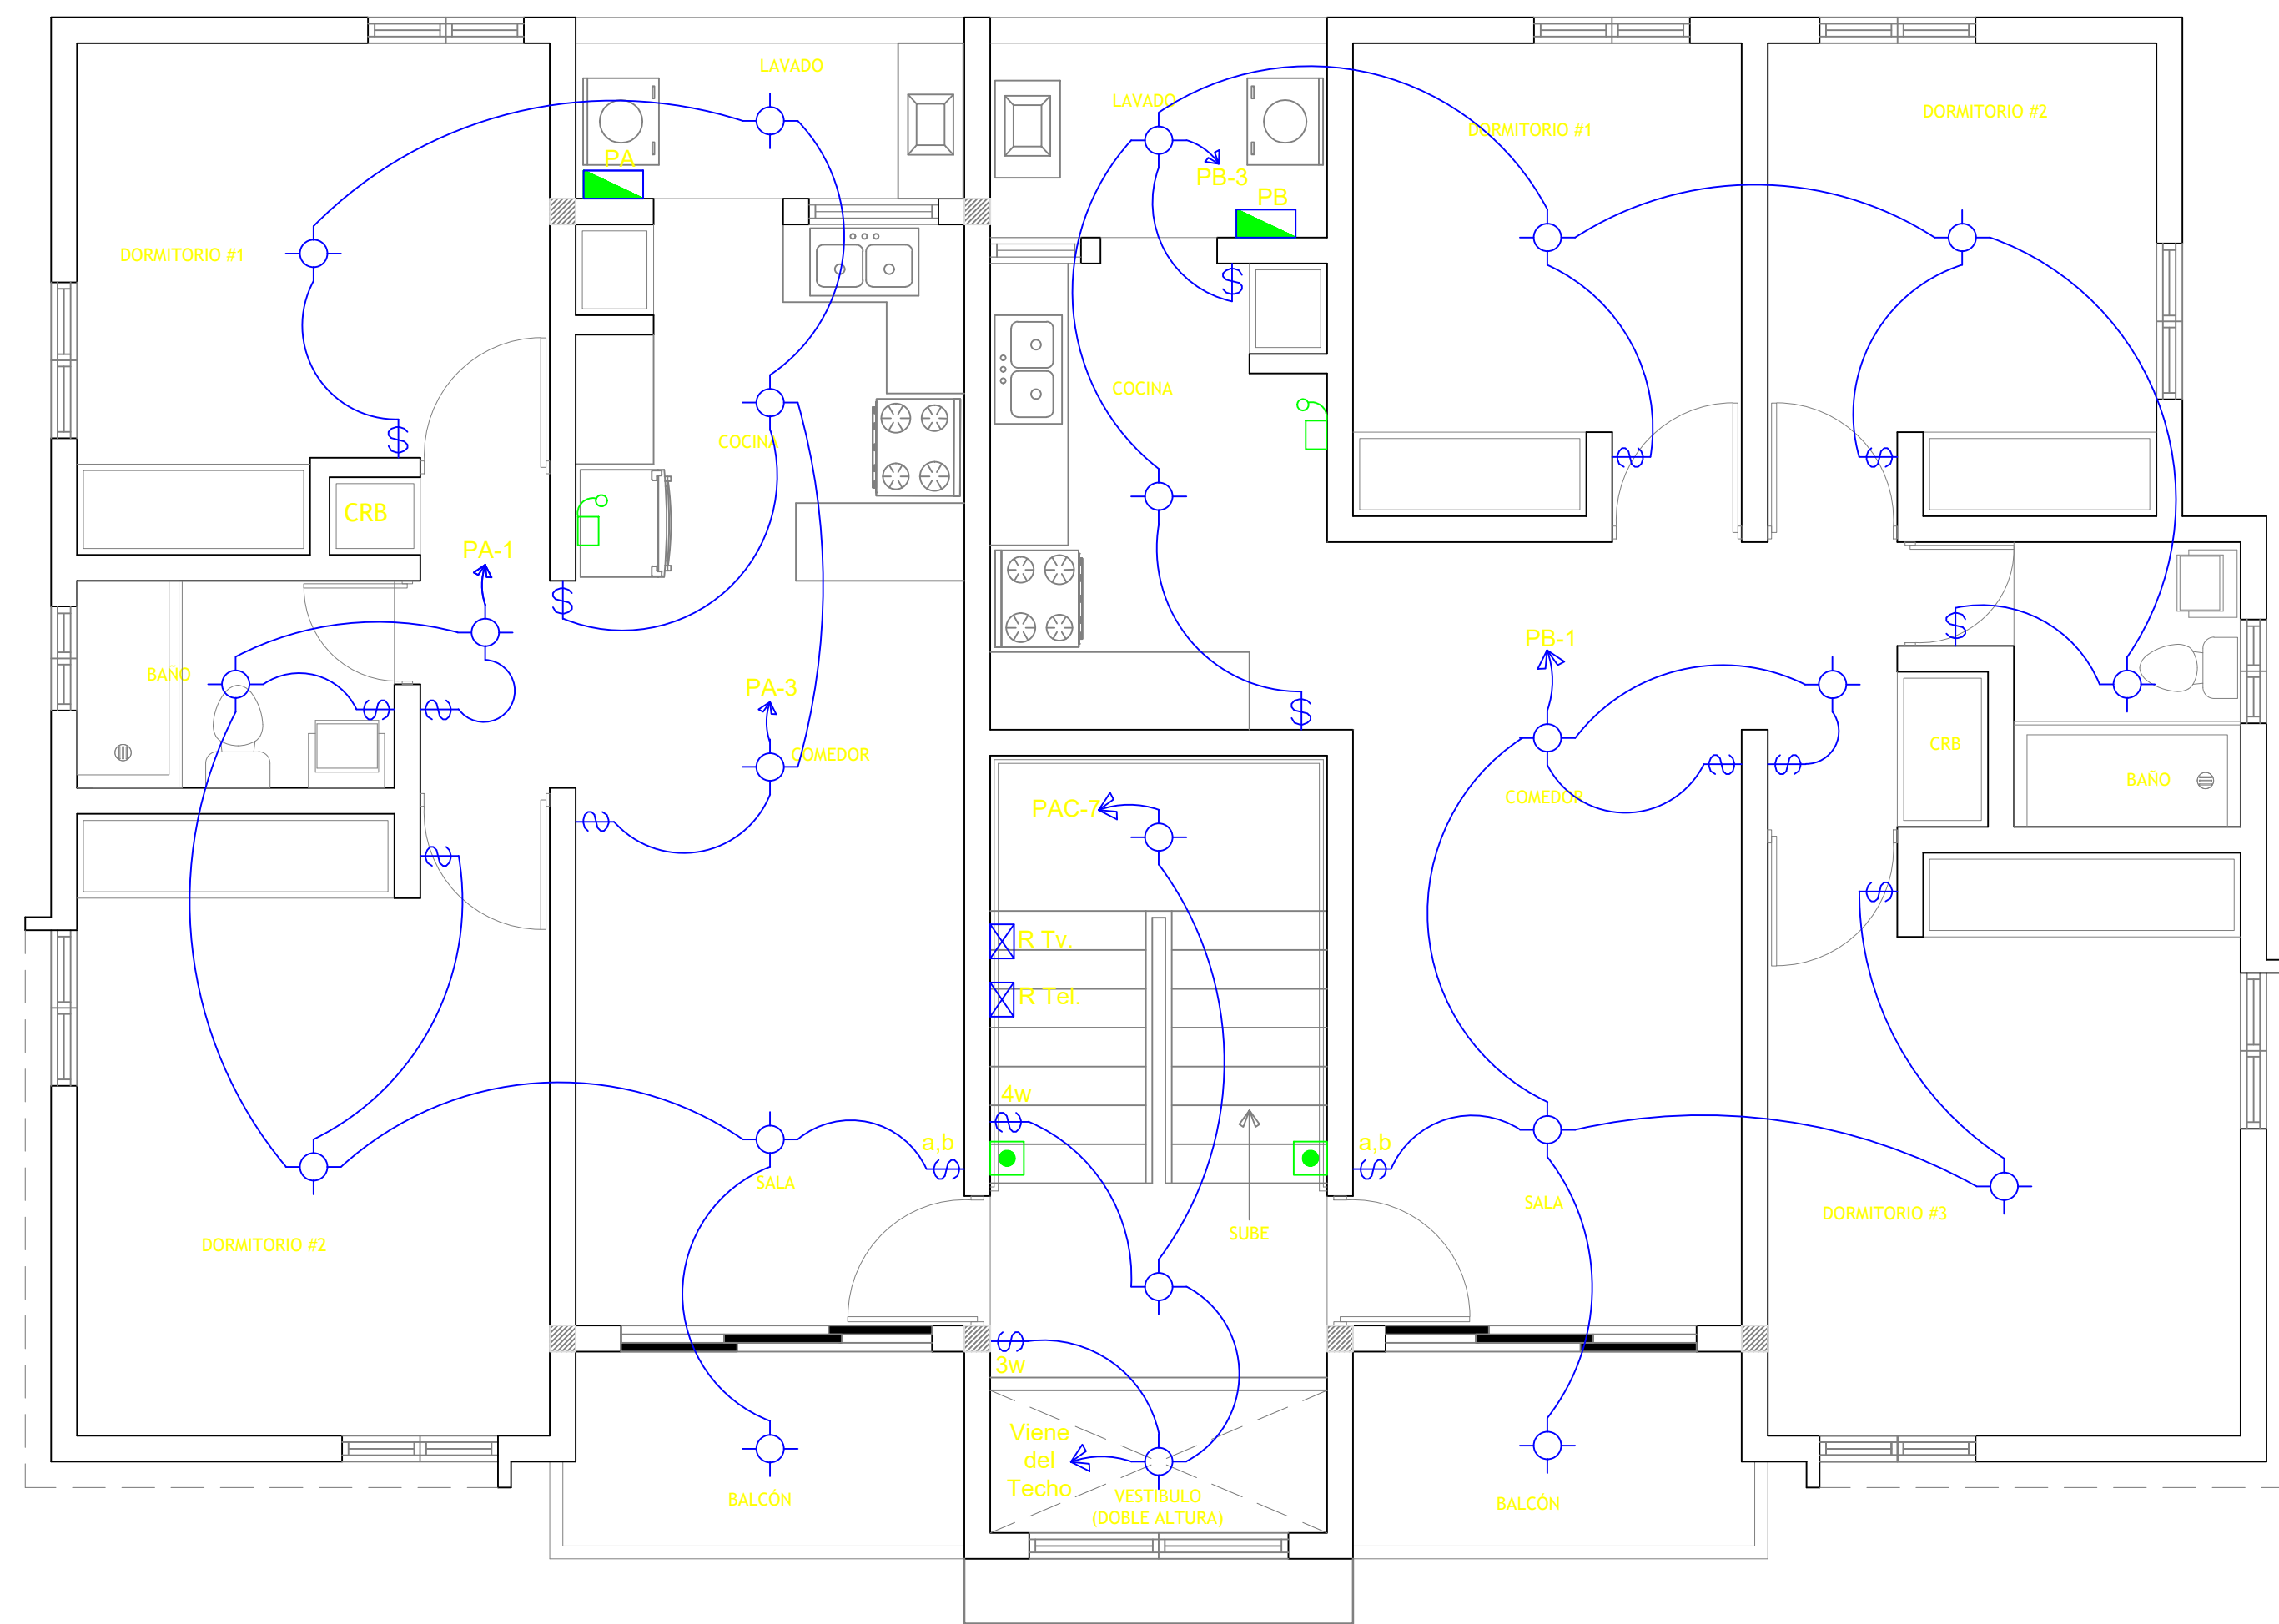


PANEL:	PB	SIMILAR A:	TLM1212C	No. DE ESPACIOS:	24
LUGAR:	LAVADO	TIPO DE BKR.:	THQC270	VOLTAGE:	240 V
FORMA					
DE INST:	EMPOTRADO	No. DE FASES:	2	CORR. BARRA:	200A
PLANO:	ELECTRICO	No. DE CONDS:	4		

KVA	DESCRIPCION	COND					A	B	COND				TUB	DESCRIPCION	KVA
		Diam	Cal.	Tipo	Bkr	No.			No.	Bkr	Tipo	Cal.			
0.50	ILUMINACION	1/2"	12	THHN	20	1			2	20	THHN	12	1/2"	DISPONIBLE	
0.50	ILUMINACION	1/2"	12	THHN	20	3			4	20	THHN	12	1/2"	TC - USO GRAL.	1.05
0.60	NEVERA	1/2"	12	THHN	20	5			6	20	THHN	12	1/2"	TC - USO GRAL.	1.05
1.50	TSM	3/4"	10	THHN	30	7			8	20	THHN	10	3/4"	TC - (240 V)	1.25
1.50	CALENTADOR	3/4"	10	THHN	30	9			10	20	THHN		1.25		
1.20	LAVADORA	3/4"	10	THHN	20	11			12			10	3/4"	TC - (240 V)	1.25
0.15	BAÑO	1/2"	12	THHN	20	13			14	30/2	THHN		1.25		
						15			16	30/2	THHN	10	3/4"	TC - (240 V)	1.25
						17			18						1.25
						19			20						
						21			22						
						23			24						
						25			26						
						27			28						
						29			30						
						31			32						
						33			34						
						35			36						
						37			38						
						39			40						
						41			42						

Carga Instalada	15.55 kVA			ALIMENTADORES			
Carga de Diseño	12.83 kVA	Desbalance Fase A	2.9%	Conds/Fases	4 THHN	Caída de Tensión	2.52
Carga de Reserva	1.17 kVA	Desbalance Fase B	2.9%	Neutro	8 THHN	Regulación	1.1%
Demanda Maxima	11.66 kVA	Corriente de Carga I _D	53.5 A	Tierra	10THHN	Longitud	20 M
Carga Fase A	7.55 kVA	Corr de Diseño I _D X1.25	66.8 A	CM	41.740		
Carga Fase B	8.00 kVA	Factor de Demanda	75%	Tubería	Ø 1 1/2 " SDR 26		

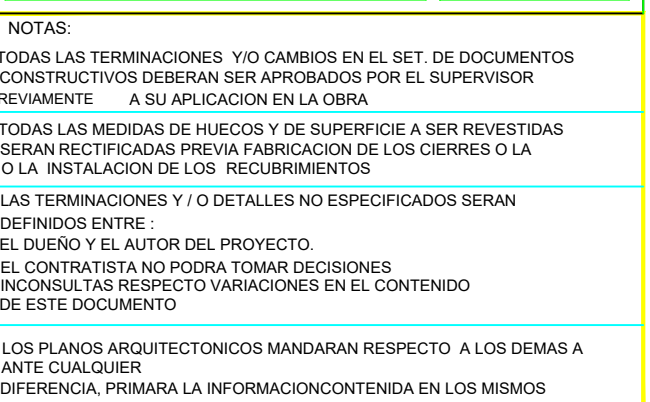

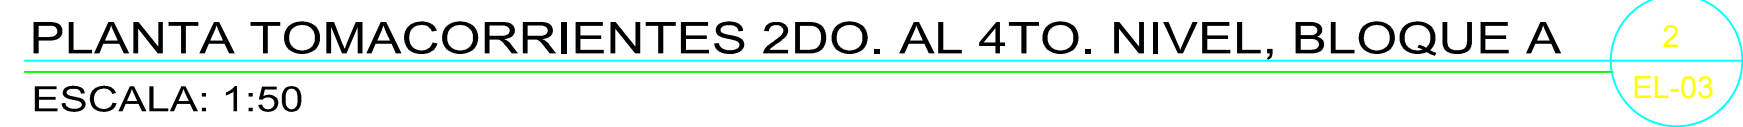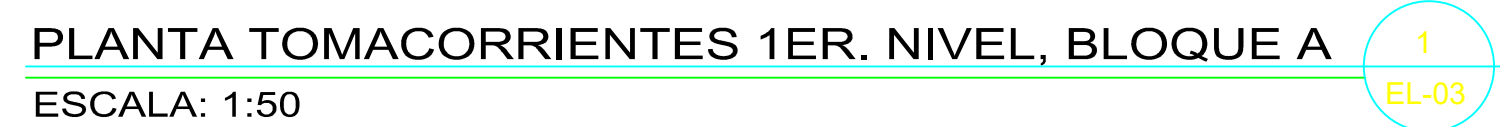

PROPIETARIO :
GRUPO EMPRESARIAL
BANILEJO S.R.L.
GEBSA

Arq. ISMAEL DIAZ MELO
Codia: 9604

Arq. HAMLET TEJEDA
Codia: 18303

ING. ODELIN TEJEDA
Codia: 239

ING. VILLYS SANCHEZ

Codia: 1906

PLANTAS TOMACORRIENTES

BLOQUE A

PROYECTO:
RESIDENCIAL GBSA IV

UBICACION:

BANI, PROV. PERAVIA

Ref.: Acad 2000

Escala: INDICADA

Hoja No.


NOTAS:

• TODAS LAS TERMINACIONES Y/O CAMBIOS EN EL SET DE DOCUMENTOS CONSTRUCTIVOS DEBERAN SER APROBADOS POR EL SUPERVISOR PREVIAMENTE A SU APLICACION EN LA OBRA

• TODAS LAS MEDIDAS DE HUECOS Y DE SUPERFICIE A SER REVESTIDAS SERAN RECTIFICADAS POR HECHO PARA FABRICACION DE LOS CIERRES O LA O.L.A. INSTALACION DE LOS REQUERIMIENTOS


• LAS TERMINACIONES Y / O DETALLES NO ESPECIFICADOS SERAN DEFINIDOS ENTRE:
EL DUEÑO Y EL AUTOR DEL PROYECTO.
EL CONTRATISTA NO PODRA TOMAR DECISIONES INCONSULTAS RESPECTO VARIACIONES EN EL CONTENIDO DE ESTE DOCUMENTO

• LOS PLANOS ARQUITECTONICOS MANDARAN RESPECTO A LOS DEMAS A ANTE CUALQUIER DIFERENCIA, PRIMARA LA INFORMACION CONTENIDA EN LOS MISMOS

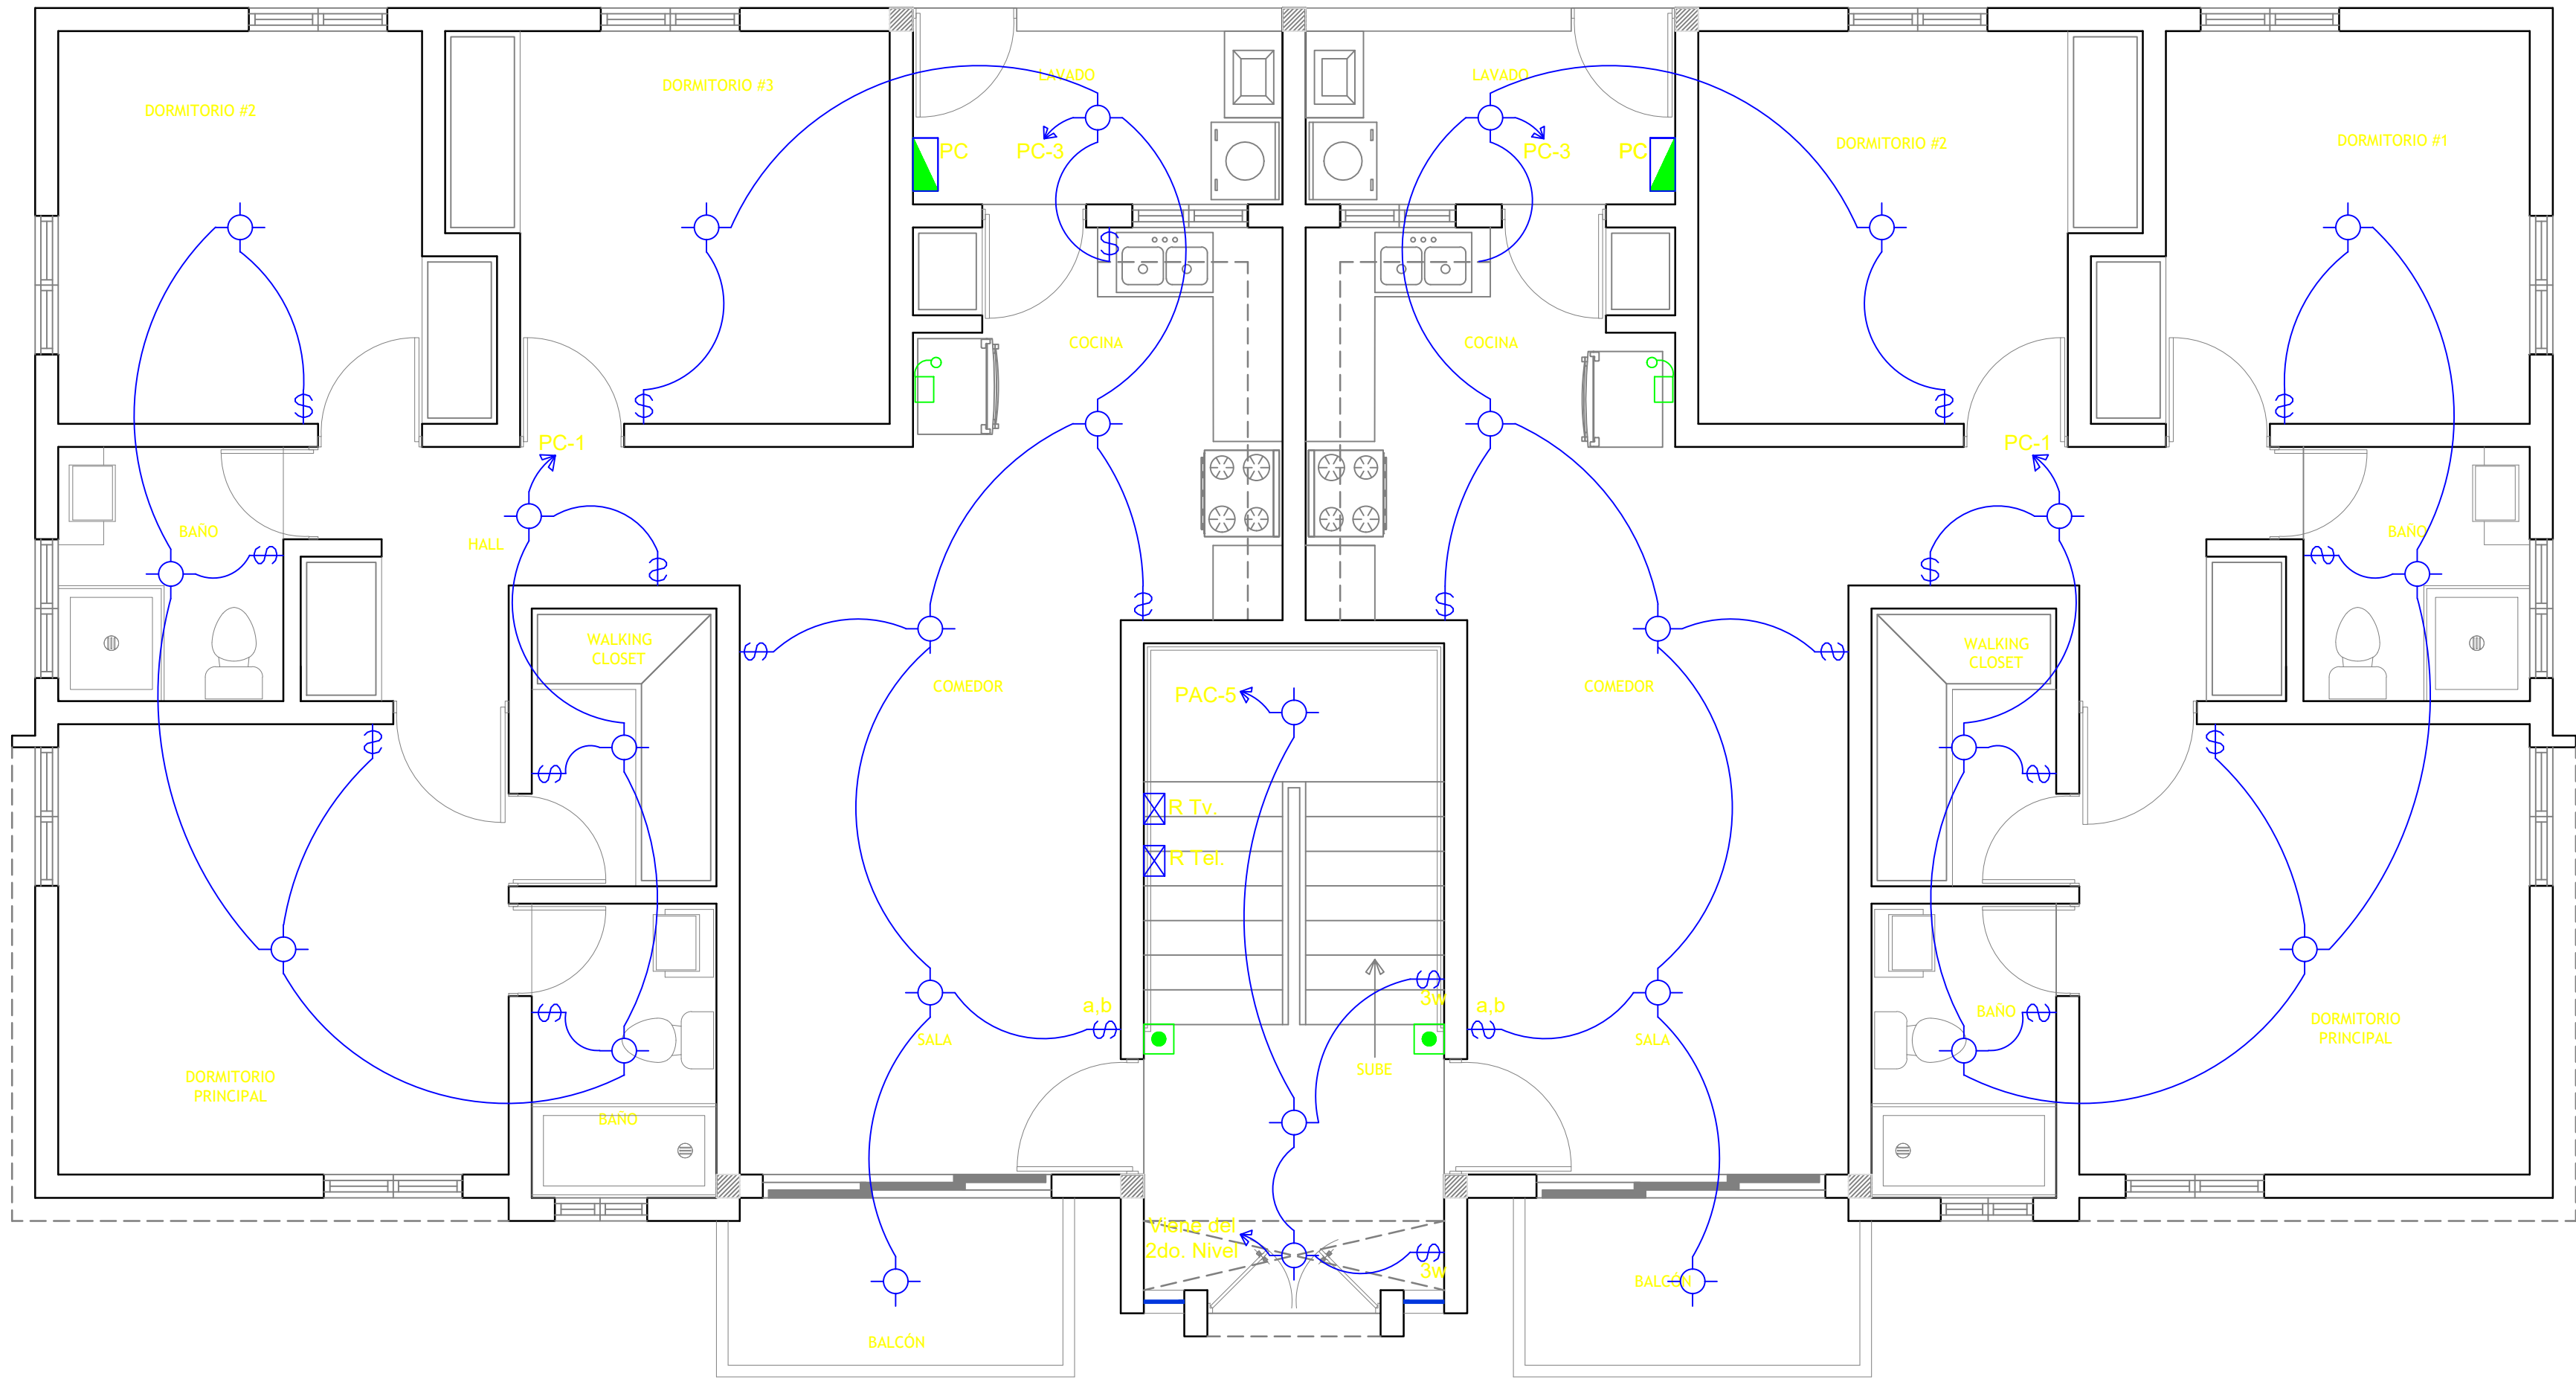

PLANTA LUMINARIAS 1ER. NIVEL, BLOQUE B
ESCALA: 1:75

1
EL-04

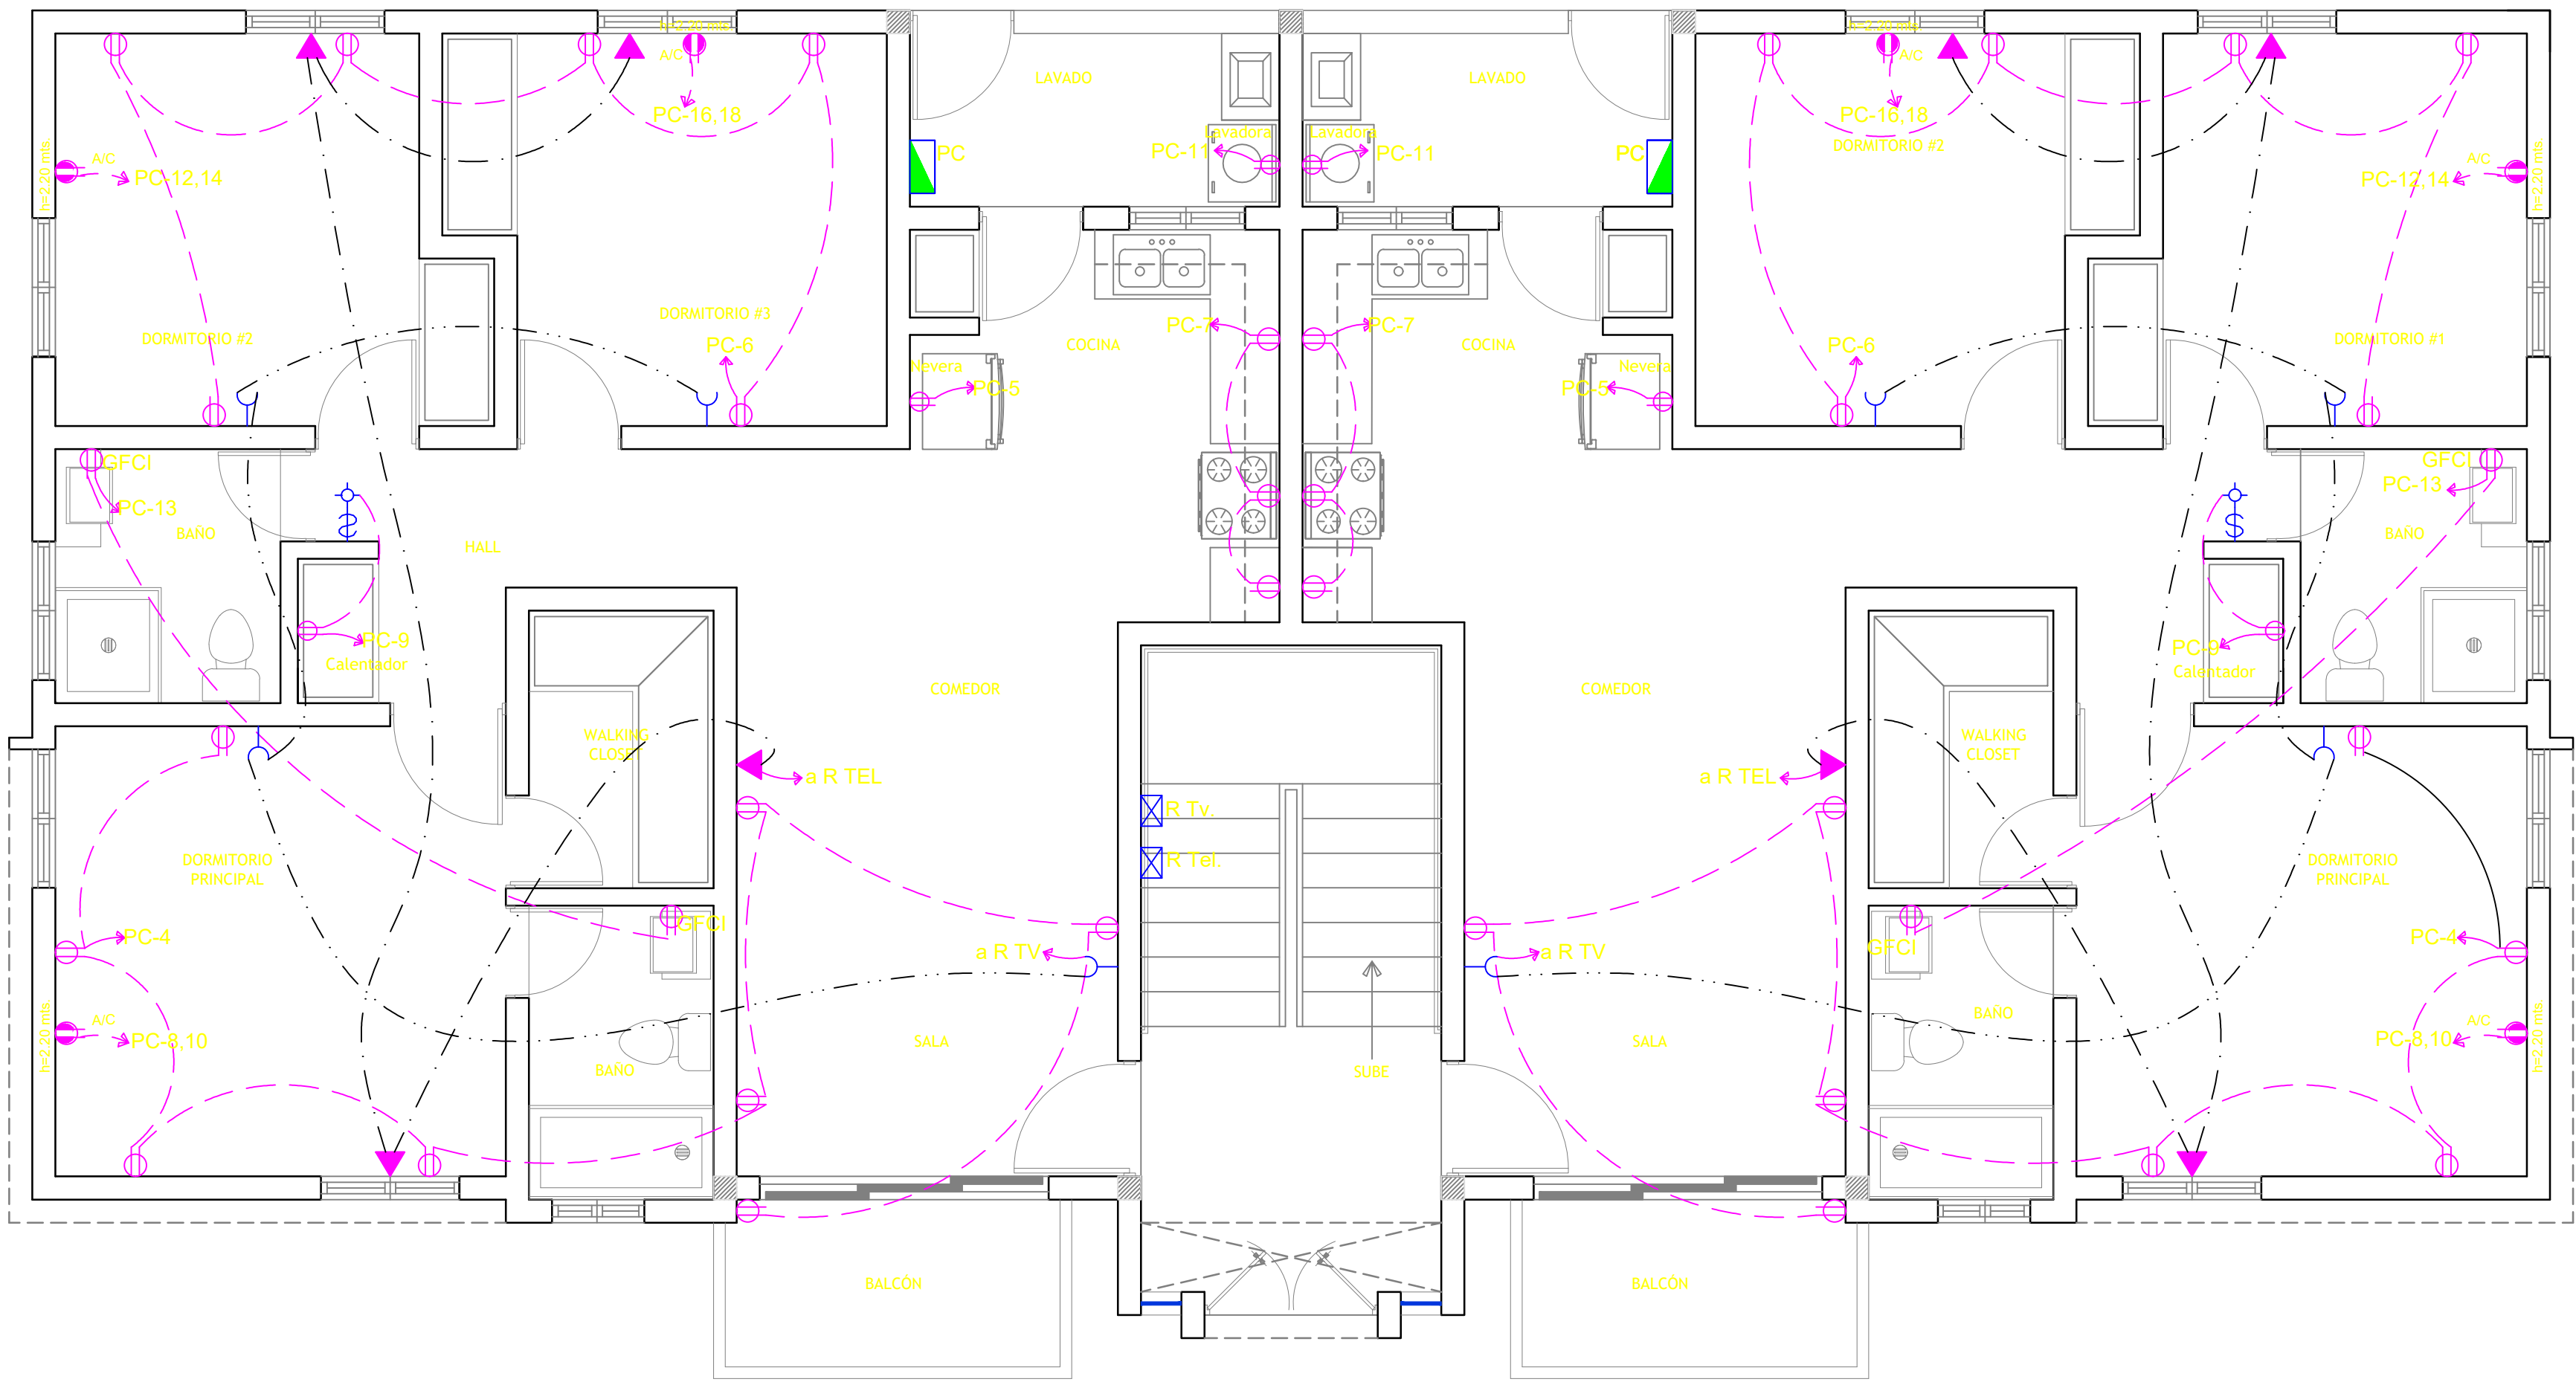

PLANTA TOMACORRIENTES 1ER. NIVEL, BLOQUE B
ESCALA: 1:50

2
EL-04

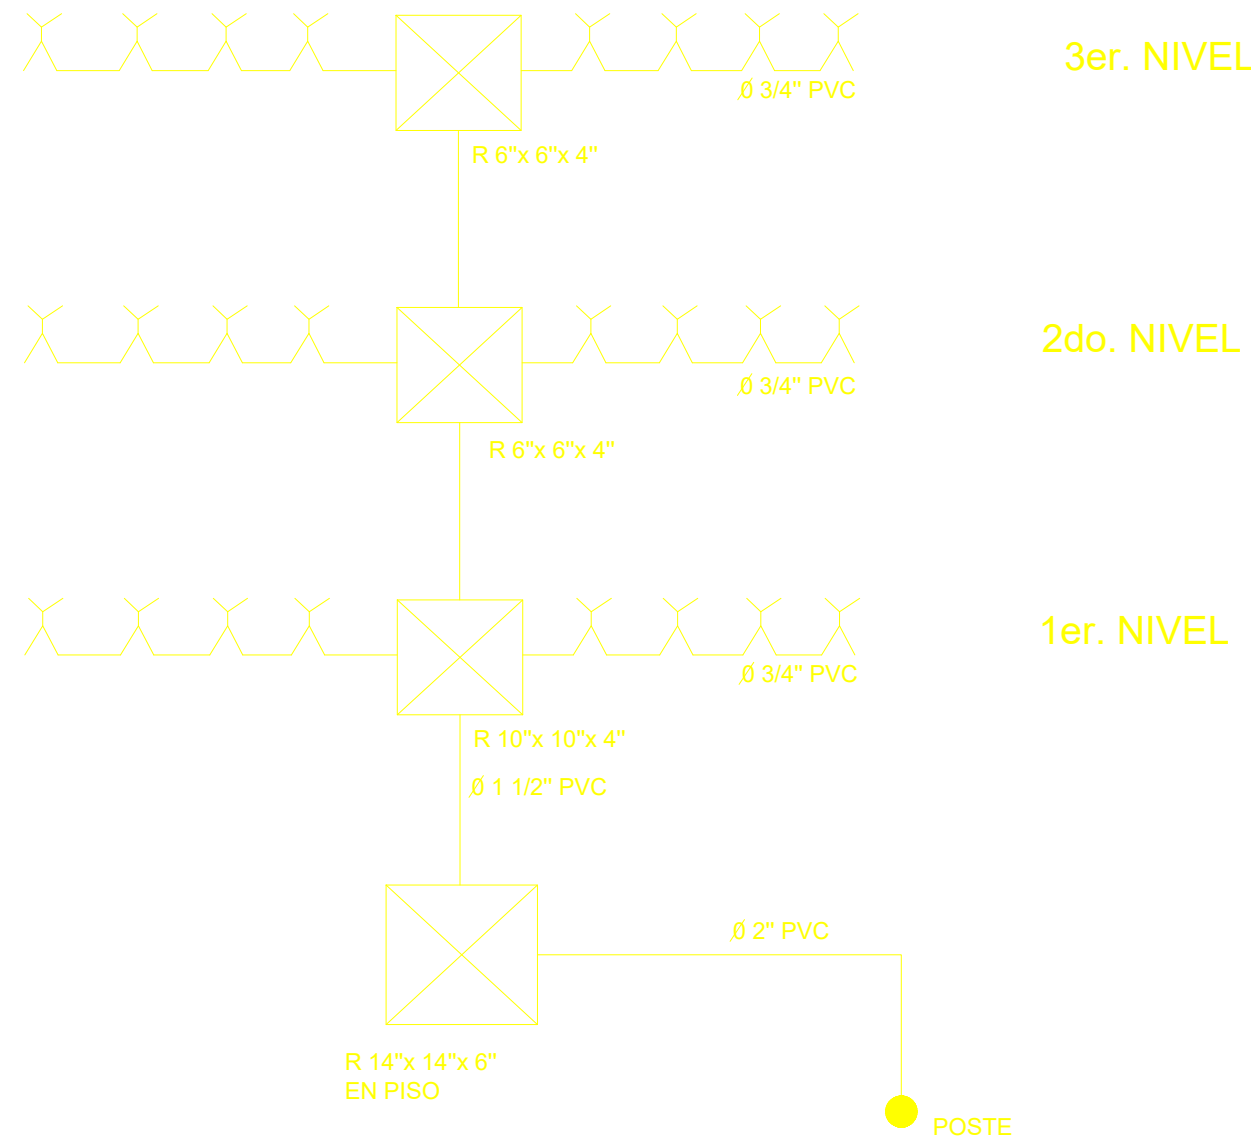


DIAGRAMA VERTICAL DE ANTENA BLOQUE B

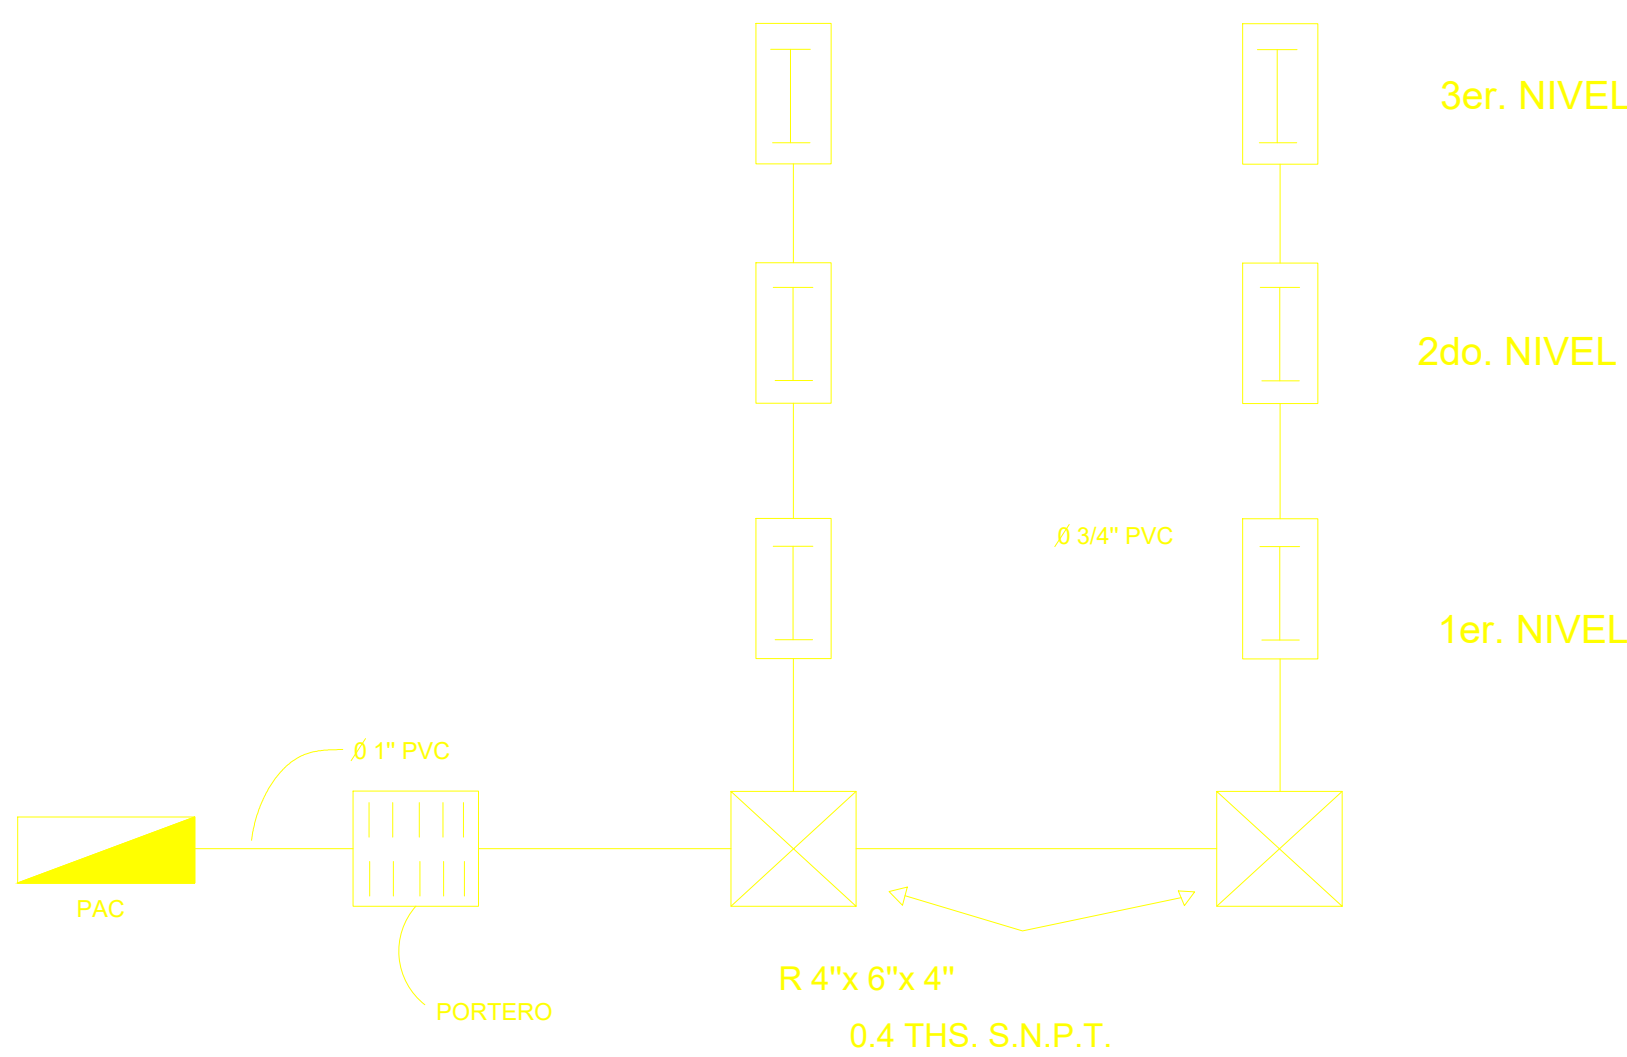


DIAGRAMA VERTICAL DE INTERCOM BLOQUE B

LEYENDA ELECTRICA

- POSTE DE CONCRETO DE 35 PIES
- \$ SALIDA DE INTERRUPTOR SENCILLO
- \$ab SALIDA DE INTERRUPTOR DOBLE
- \$3w SALIDA DE INTERRUPTOR DE TRES VIAS
- ⊕ SALIDA DE INTERRUPTOR DOBLE
- ⊕ SALIDA DE INTERRUPTOR DE TRES VIAS
- ▼ SALIDA DE TELEFONO
- ↓ SALIDA DE ANTENA
- SALIDA DE INTERCOM
- SALIDA DE INTERCOM
- SALIDA DE CAMPANA DE TIMBRE
- PANEL DE DISTRIBUCION ELECTRICO
- PANEL DE DISTRIBUCION ELECTRICO
- ⊗ PANEL DE DISTRIBUCION ELECTRICO
- CONDUCTOR EMPOTRADO EN EL TECHO Y/O PANEL
- CONDUCTOR EMPOTRADO EN EL TECHO Y/O PANEL
- (WU) MEDIDOR ELECTRICO
- ~ TRANSFORMADOR ELECTRICO
- S CUT OUT



diazmeo & asocs.
ARQUITECTOS
Presidente Billini # 12, Bani, R.D. 522-4989
E-mail: diazmeo@hotmail.com

COLABORACION:



ARQUITECTURA DIGITAL
DISEÑOS-CONSTRUCCION-DIGITACION
COMPROMETIDOS CON SU TIEMPO
C/JUAN SANCHEZ RAMIREZ #56,
LOCAL 5 ZONA UASD TEL:221-5400

PROPIETARIO:

GRUPO EMPRESARIAL
BANILEJO S.R.L.
GEBSA

PROYECTISTAS:

DISEÑO ARQUITECTONICO:

DIAZMELO & ASOCS.

Arq. ISMAEL DIAZ MELO

Codia: 9604

DISEÑO SANITARIO:

Arq. HAMLET TEJEDA

Codia: 18303

DISEÑO ESTRUCTURAL:

ING. ODELIN TEJEDA

Codia: 23937

DISEÑO ELECTRICO:

ING. VILLYS SANCHEZ

Codia: 19060

CONTENIDO:

PLANTAS, LUMINARIAS Y
TOMACORRIENTES
1ER. NIVEL BLOQUE B

PROYECTO:

RESIDENCIAL GEBSA IV

Fecha:

MAYO/2018

UBICACION:

BANI, PROV. PERAVIA


Ref.:

Acad 2000

Hoja No.


Escala: INDICADA

NOTAS:
TODAS LAS TERMINACIONES Y/O CAMBIOS EN EL SET DE DOCUMENTOS CONSTRUCTIVOS DEBERAN SER APROBADOS POR EL SUPERVISOR PREVIAMENTE A SU APLICACION EN LA OBRA.
TODAS LAS MEDIDAS DE HUECOS Y DE SUPERFICIE A SER REVESTIDAS SERAN RECTIFICADAS PREVIA FABRICACION DE LOS CORRES O LA O LA INSTALACION DE LOS RECURBIMIENTOS.
LAS TERMINACIONES Y/O DETALLES NO ESPECIFICADOS SERAN DEFINIDOS ENTRE EL DUEÑO Y EL AUTOR DEL PROYECTO.
EL CONTRATISTA NO PODRA TOMAR DECISIONES INCONSULTAS RESPECTO A VARIACIONES EN EL CONTENIDO DE ESTE DOCUMENTO.
LOS PLANOS ARQUITECTONICOS MANDARAN RESPECTO A LOS DEMAS A ANTE CUALQUIER DIFERENCIA, PRIMARA LA INFORMACIONCONTENIDA EN LOS MISMOS

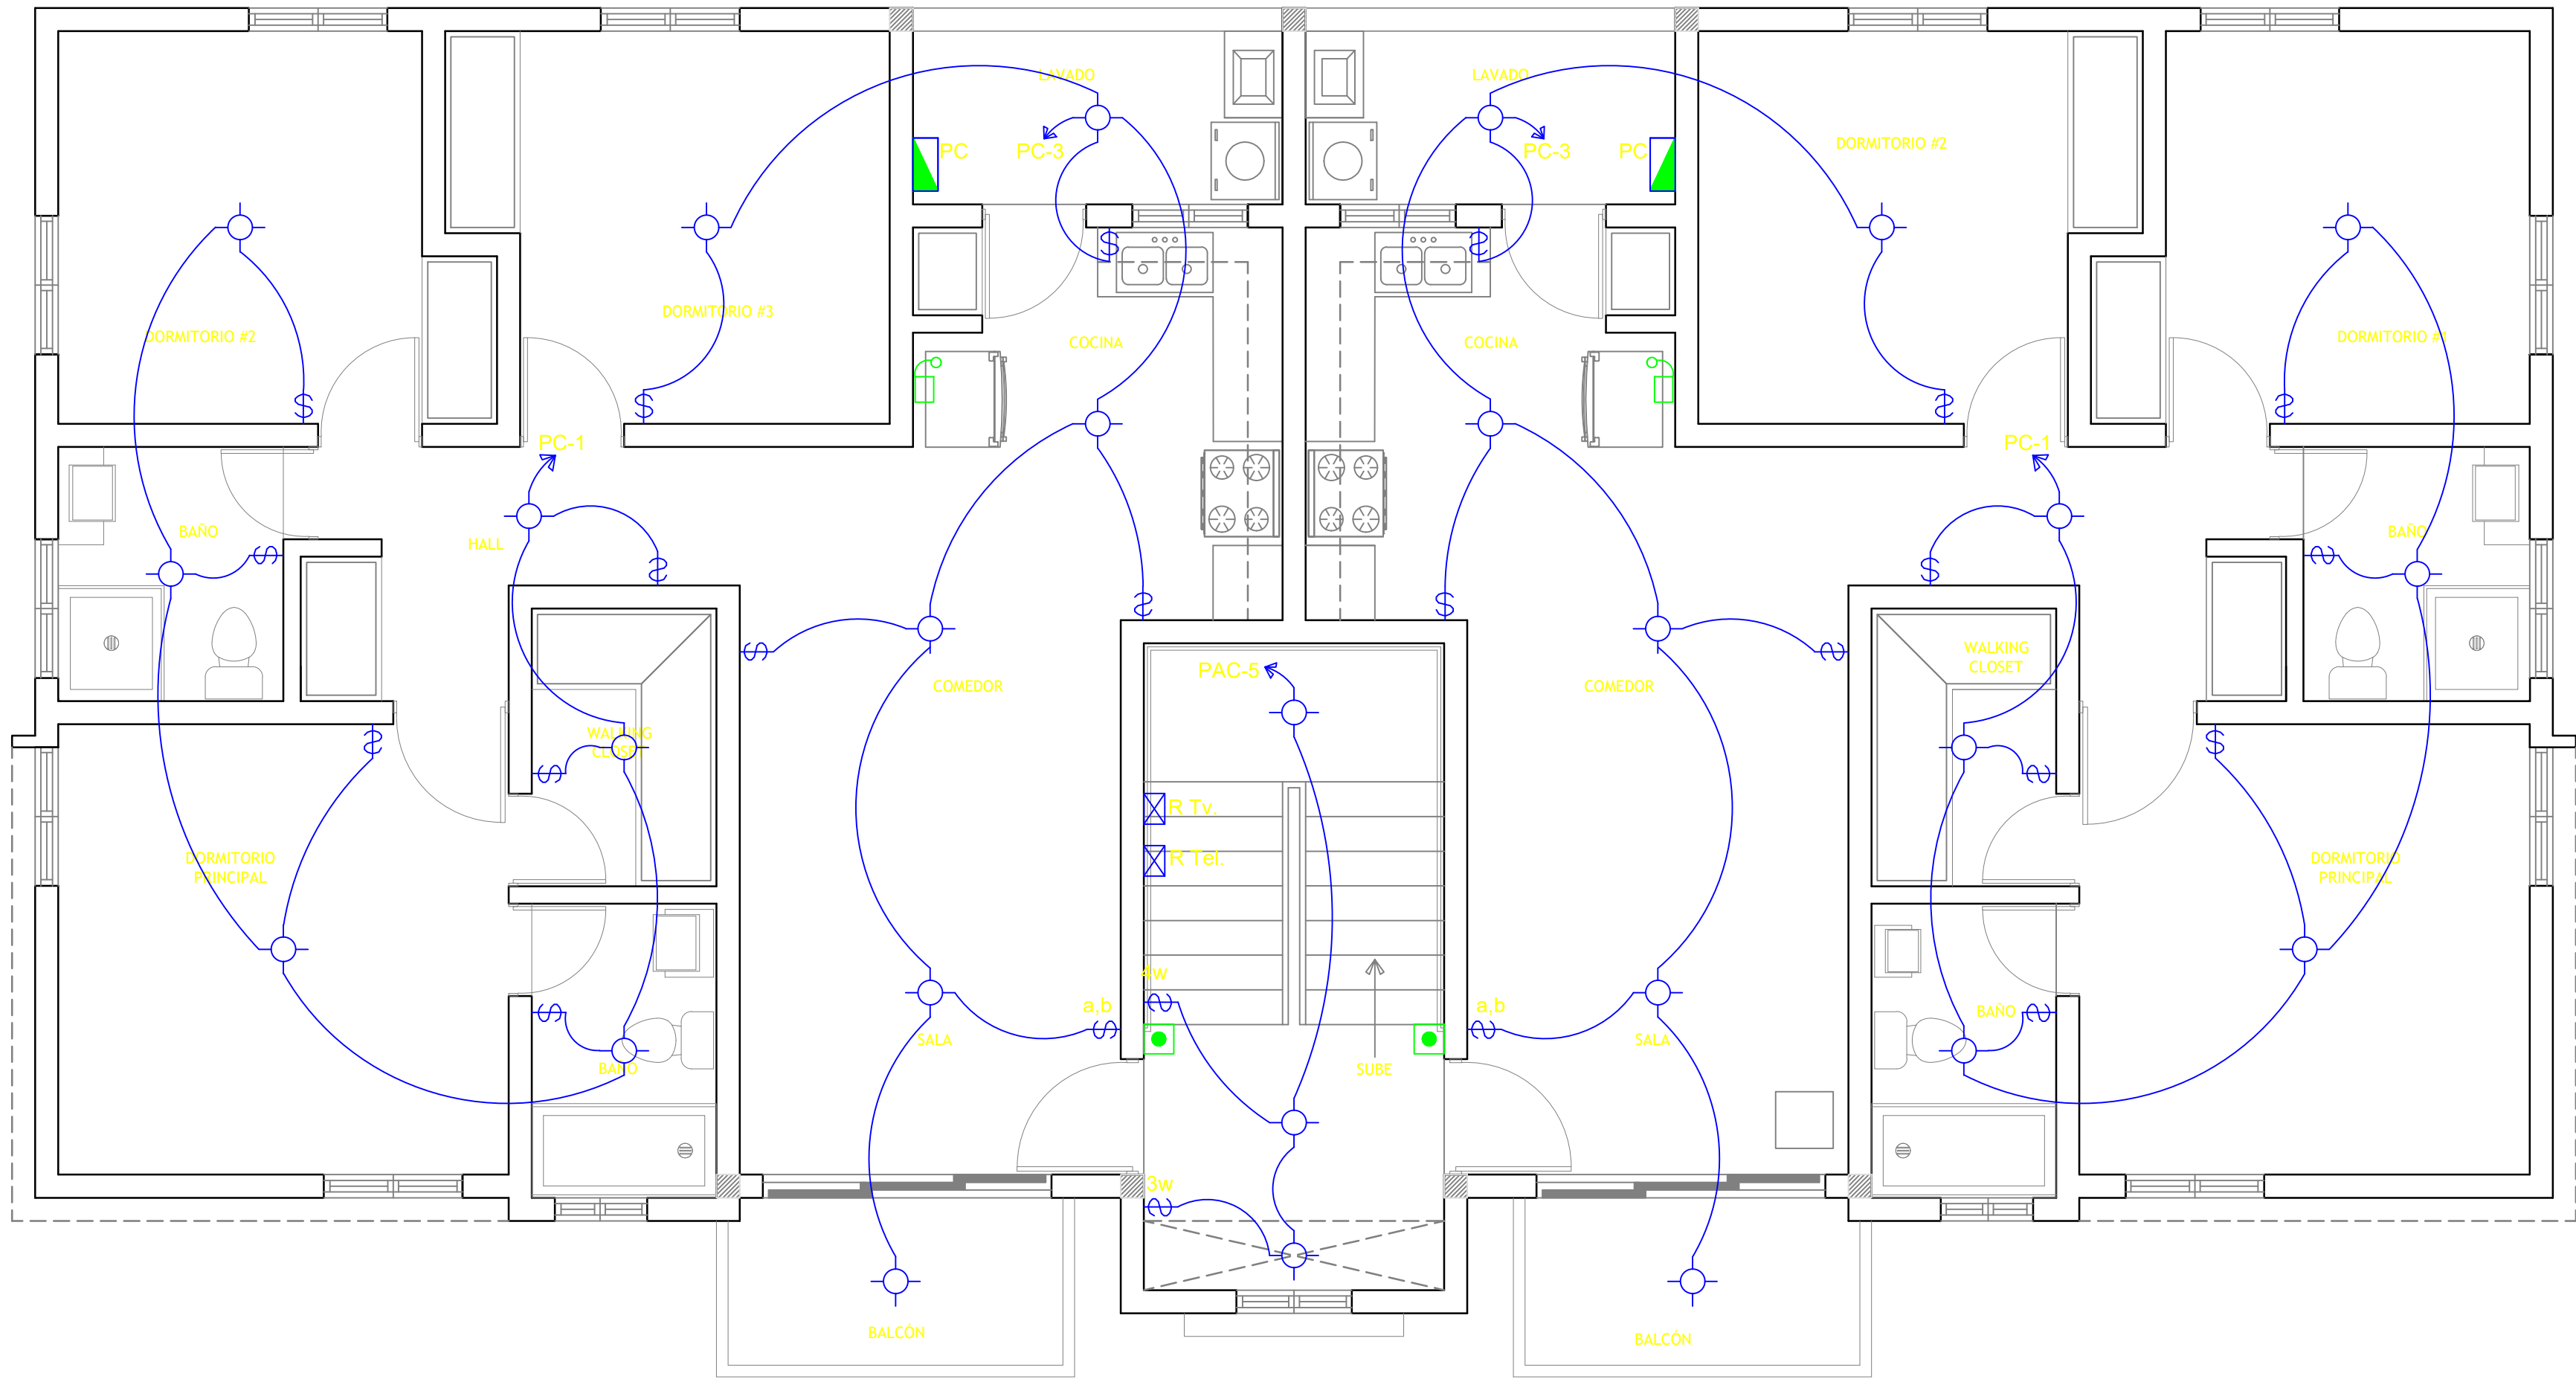

PLANTA LUMINARIAS 2DO. NIVEL, BLOQUE B
ESCALA: 1:50

1
EL-05

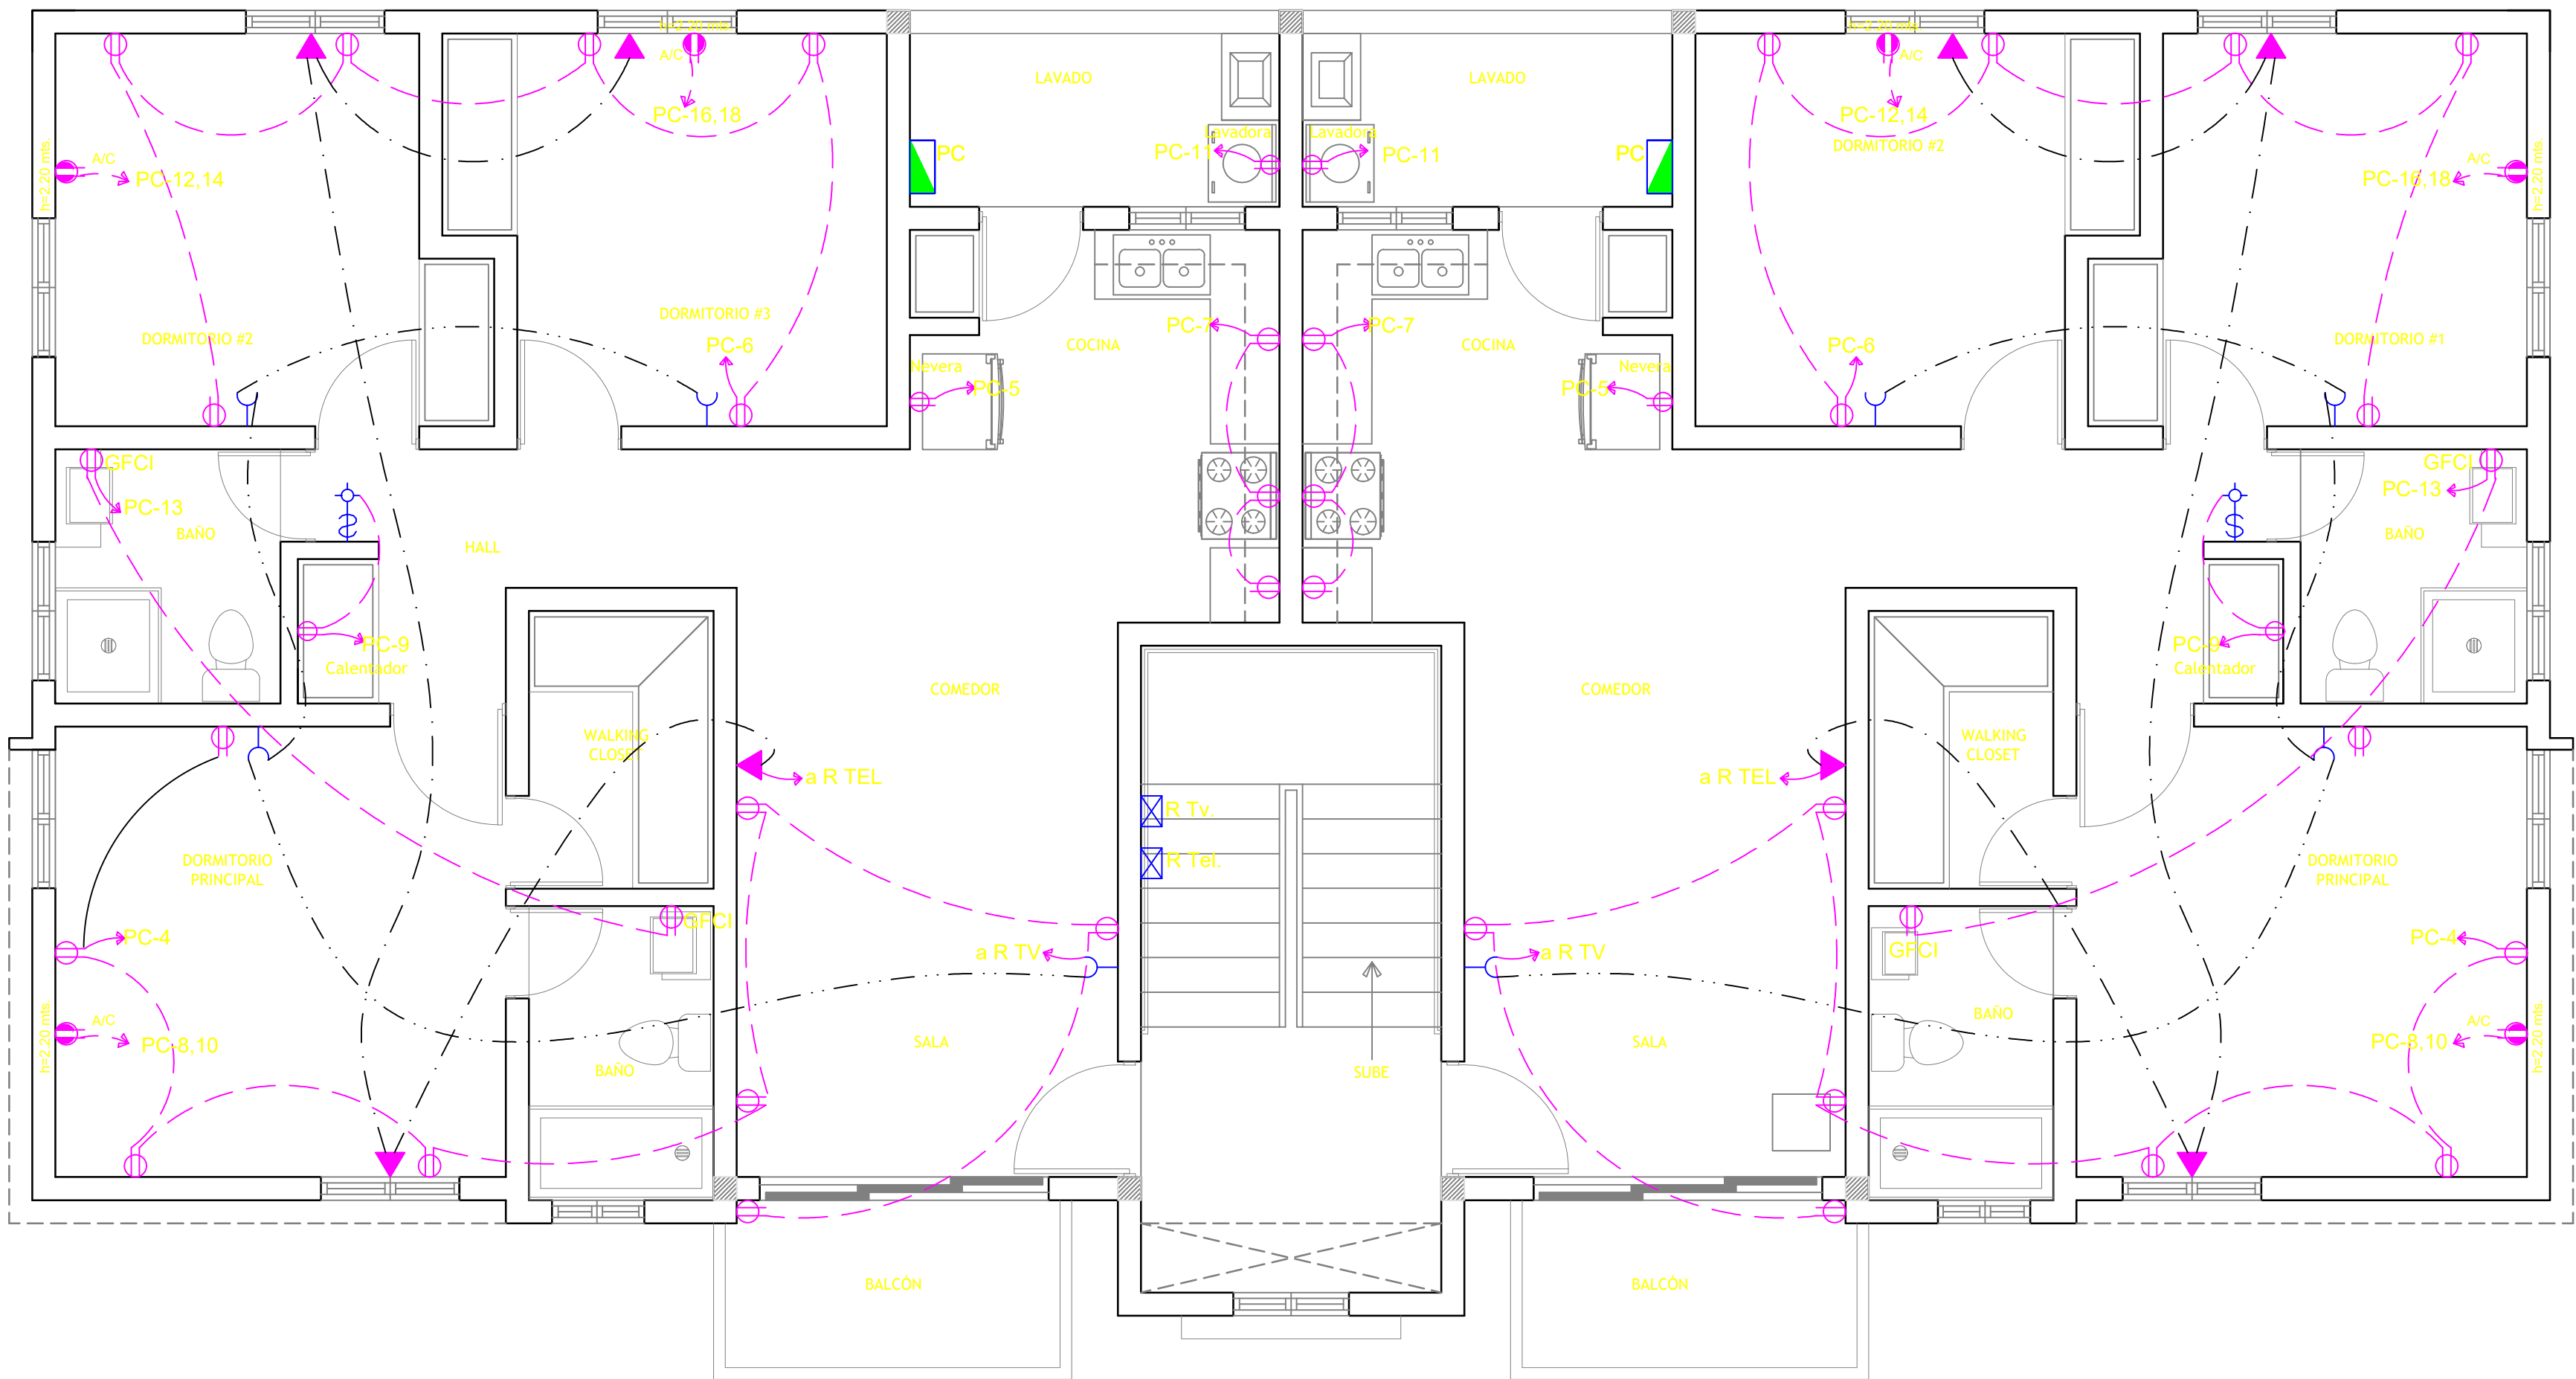

PLANTA TOMACORRIENTES 2DO. NIVEL, BLOQUE B
ESCALA: 1:50

2
EL-05

PANEL:	PC	SIMILAR A:	TLM1212C	No. DE ESPACIOS:	24
LUGAR:	LAVADO	TIPO DE BKR:	THOC270	VOLTAGE:	240 V
FORMA:	EMPOTRADO	No. DE FASES:	2	CORR. BARRA:	200A
DE INST:	ELECTRICO	No. DE CONDS:	4		
PLANO:					

KVA	DESCRIPCION	TUB	COND	Cal	Tip	Bkr	No.	A	B	No.	Bkr	Tip	Cal.	TUB	DESCRIPCION	KVA
0.60	ILUMINACION	1/2"	12	THHN	20	3	1			2	20	THHN	12	1/2"	DISPONIBLE	1.20
0.60	NEVERA	1/2"	12	THHN	20	5	6			6	20	THHN	12	1/2"	TC - USO GRAL.	0.60
1.50	TSM	3/4"	10	THHN	30	7	7			8	20	THHN	10	3/4"	TC - (240 V)	1.25
1.50	CALENTADOR	3/4"	10	THHN	30	9	9			10	20	THHN	10	3/4"	TC - (240 V)	1.25
1.20	LAVADORA	3/4"	10	THHN	20	11	11			12	30/2	THHN	10	3/4"	TC - (240 V)	1.25
0.30	BAÑO	1/2"	12	THHN	20	13	13			14	30/2	THHN	10	3/4"	TC - (240 V)	1.25
							15			16	30/2	THHN	10	3/4"	TC - (240 V)	1.25
							17			18	30/2	THHN	10	3/4"	TC - (240 V)	1.25
							19			20						1.25
							21			22						1.25
							23			24						1.25
							25			26						1.25
							27			28						1.25
							29			30						1.25
							31			32						1.25
							33			34						1.25
							35			36						1.25
							37			38						1.25
							39			40						1.25
							41			42						1.25

Carga Instalada	15.90 KVA	Desbalance Fase A	3.8%	Alimentadores		Caída de Tensión	2.58
Carga de Diseño	13.12 KVA	Desbalance Fase B	3.8%	Conds/Fases	4 THHN	Regulación	1.1%
Carga de Reserva	1.19 KVA	Corriente de Carga I _{to}	54.7 A	Neutro	8 THHN	Longitud	20 M
Demanda Máxima	11.93 KVA	Corr de Diseño I _x x1.25	68.3 A	Tierra	10THHN		
Carga Fase A	7.65 KVA	Factor de Demanda	75%	CM	41.740		
Carga Fase B	8.25 KVA			Tubería	Ø 1 1/2" SDR 26		

TODO EL LOS TC ESTÁN ATERRIZADO CON UN TW#12 DE COLOR VERDE

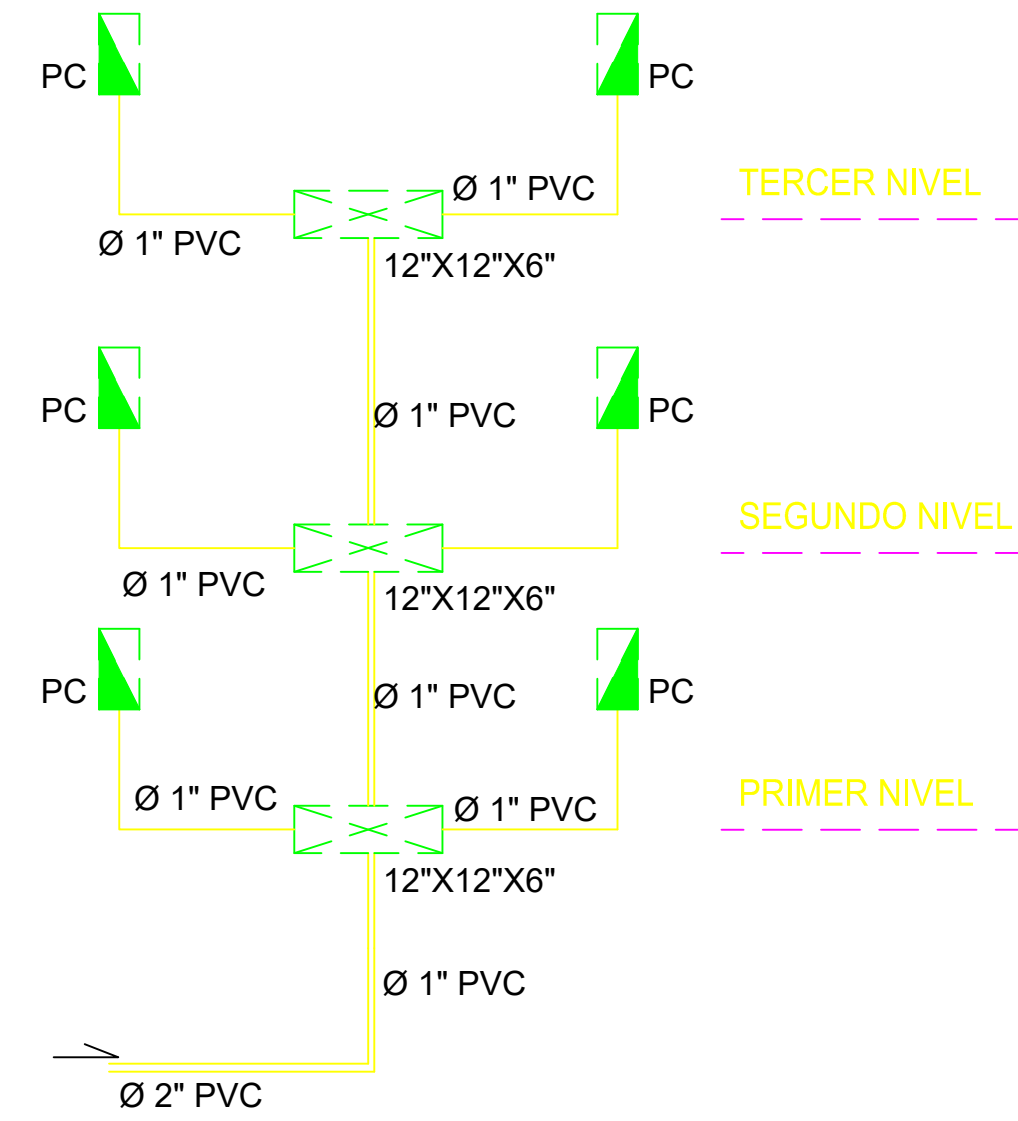


DIAGRAMA VERTICAL ELECTRICO BLOQUE B
no escala

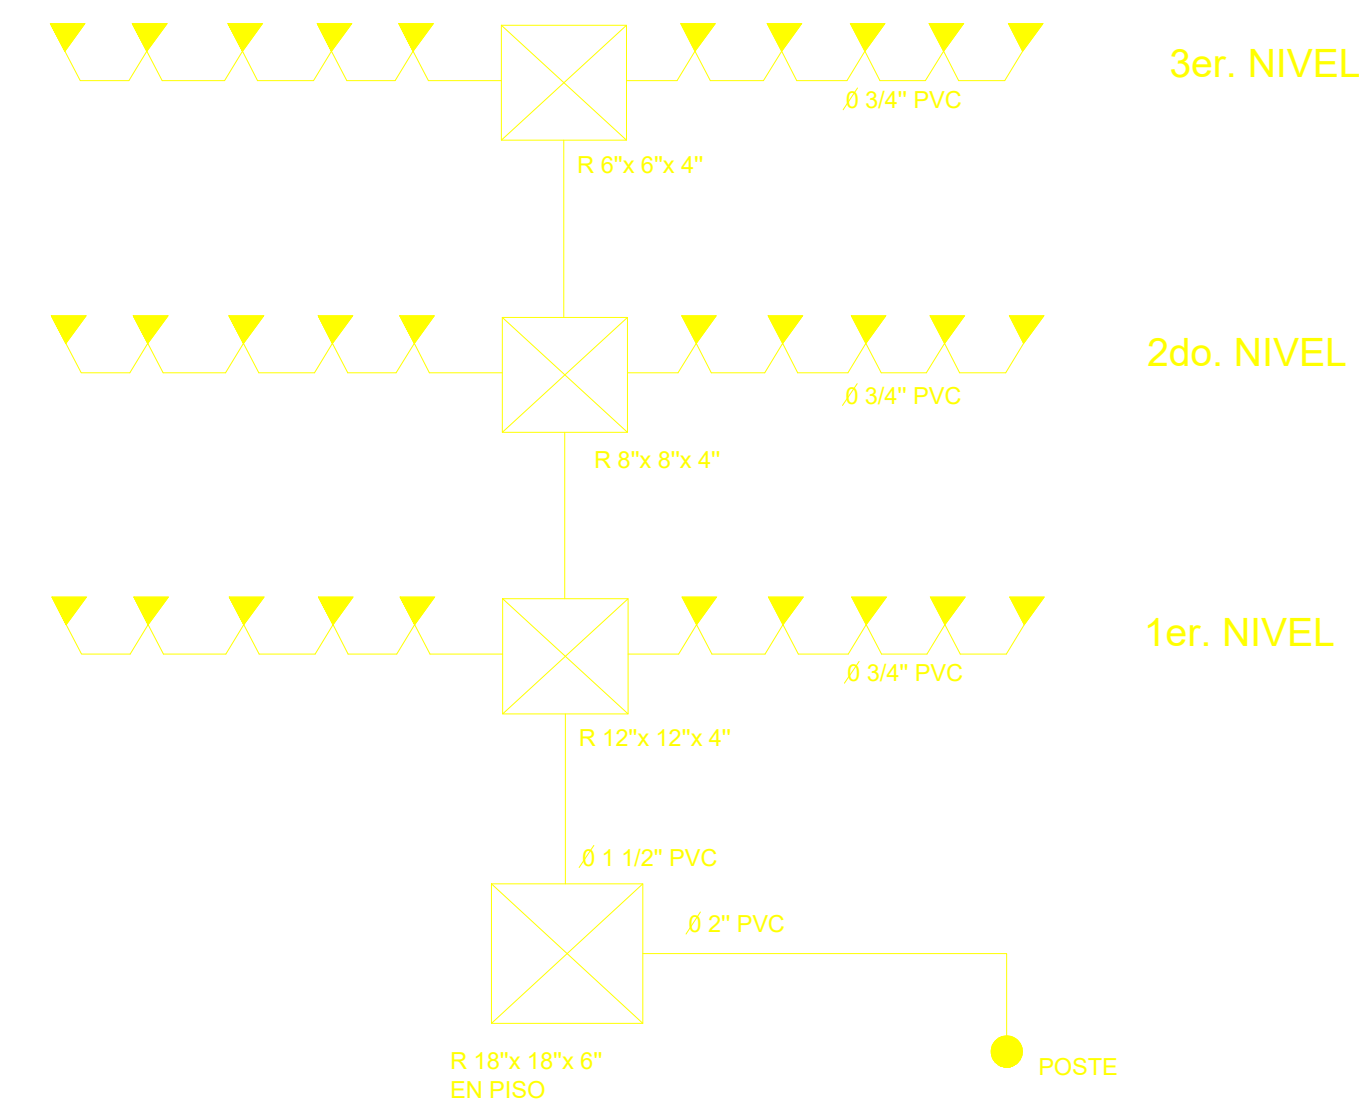


DIAGRAMA VERTICAL DE TELEFONO BLOQUE B



diaz melo & asocs.

ARQUITECTOS

Presidente Bilini # 12, Bari, R.D. 522-4989
E-mail: diazmelo@hotmail.com

COLABORACION:



ARQUITECTURA DIGITAL
DISEÑOS-CONSTRUCCION-DIGITACION
COMPROMETIDOS CON SU TIEMPO
C/JUAN SANCHEZ RAMIREZ #56,
LOCAL 5 ZONA UASD TEL:221-5400

PROPIETARIO:
GRUPO EMPRESARIAL
BANILEJO S.R.L.
GEBSA

PROYECTISTAS:

DISEÑO ARQUITECTONICO:
DIAZMELO & ASOCS.

Arq. ISMAEL DIAZ MELO

Codia: 9604

DISEÑO SANITARIO:

Arq. HAMLET TEJEDA

Codia: 18303

DISEÑO ESTRUCTURAL:

ING. ODELIN TEJEDA

Codia: 23937

DISEÑO ELECTRICO:

ING. VILLYS SANCHEZ

Codia: 19060

CONTENIDO:

PLANTAS, LUMINARIAS Y
TOMACORRIENTES
2DO. NIVEL BLOQUE B

PROYECTO:

RESIDENCIAL GEBSA IV

Fecha: MAYO/2018

UBICACION:

BANI, PROV. PERAVIA

Ref.: Acad 2000

Hoja No.

Escala: INDICADA

NOTAS:
TODAS LAS TERMINACIONES Y/O CAMBIOS EN EL SET DE DOCUMENTOS
CONSTRUCTIVOS DEBERAN SER APROBADOS POR EL SUPERVISOR
PREVIAMENTE A SU APLICACION EN LA OBRA
TODAS LAS MEDIDAS DE HUECOS Y DE SUPERFICIE A SER REVESTIDAS
SERAN REVISADAS PREVIA FABRICACION DE LOS CERRRES O LA
O LA INSTALACION DE LOS RECURRIMIENTOS
LAS TERMINACIONES Y / O DETALLES NO ESPECIFICADOS SERAN
DEFINIDOS ENTRE
EL DUEÑO Y EL AUTOR DEL PROYECTO
EL CONTRATISTA NO PODRA TOMAR DECISIONES
INCONSULTAS RESPECTO VARIACIONES EN EL CONTENIDO
DE ESTE DOCUMENTO
LOS PLANOS ARQUITECTONICOS MANDARAN RESPECTO A LOS DEMAS A
DIFERENCIA, PRIMARA LA INFORMACIONCONTENIDA EN LOS MISMOS

PLANTA LUMINARIAS 3ER. NIVEL, BLOQUE B

ESCALA: 1:75

1
EL-06

PLANTA TOMACORRIENTES 3ER. NIVEL, BLOQUE B

ESCALA: 1:75

DETALLE ILUMINACION ESCALERA BLOQUE B	3
NO ESCALA	EL-06

COLABORACION:



ARQUITECTURA DIGITAL
DISEÑOS-CONSTRUCCION-DIGITACION
COMPROMETIDOS CON SU TIEMPO
C/JUAN SANCHEZ RAMIREZ #56,
LOCAL 5 ZONA UASD TEL:221-5400

PROPIETARIO :

GRUPO EMPRESARIAL
BANILEJO S.R.L.
GEBSA

PROYECTISTAS:

DISEÑO ARQUITECTONICO:
DIAZMELO & ASOCS.

Arq. ISMAEL DIAZ MELO

Codia: 9604

DISEÑO SANITARIO:

Arq. HAMLET TEJEDA

Codia: 18303

DISEÑO ESTRUCTURAL:

ING. ODELIN TEJEDA

Codia: 23937

DISEÑO ELECTRICO:

ING. VILLYS SANCHEZ

Codia: 19060

CONTENIDO:

PLANTAS , LUMINARIAS Y
TOMACORRIENTES
3ER. NIVEL BLOQUE B

PROYECTO:

RESIDENCIAL GEBSA IV

Fecha: MAYO/2018

UBICACION:

BANI, PROV. PERAVIA

Ref.: Acad 2000

Hoja No.

Escala: INDICADA

NOTAS:

• TODAS LAS TERMINACIONES Y/O CAMBIOS EN EL SET DE DOCUMENTOS CONSTRUCTIVOS DEBERÁN SER APROBADOS POR EL SUPERVISOR PREVIAMENTE A SU APLICACIÓN EN LA OBRA.


• TODAS LAS MEDIDAS DE FUEGOS Y DE SUPERFICIE A SER REVESTIDAS SERÁN RECTIFICADAS PREVIA FIRMACIÓN DE LOS CIERRES O LA O LA INSTALACIÓN DE LOS REFORZAMIENTOS.

• LAS TERMINACIONES Y/O DETALLES NO ESPECIFICADOS SERÁN DEFINIDOS ENTRE EL DUEÑO Y EL AUTOR DEL PROYECTO.

• EL CONTRATISTA NO PODRÁ TOMAR DECISIONES INCONSULTA SIN RESPECTO A LAS VARIACIONES EN EL CONTENIDO DE ESTE DOCUMENTO.


• LOS PLANOS ARQUITECTÓNICOS MANDARÁN RESPECTO A LAS DEMAS A ANTE CUALQUIER DUDA.

• DIFERENCIA, PRIMARA LA INFORMACIONCONTENIDA EN LOS MISMOS

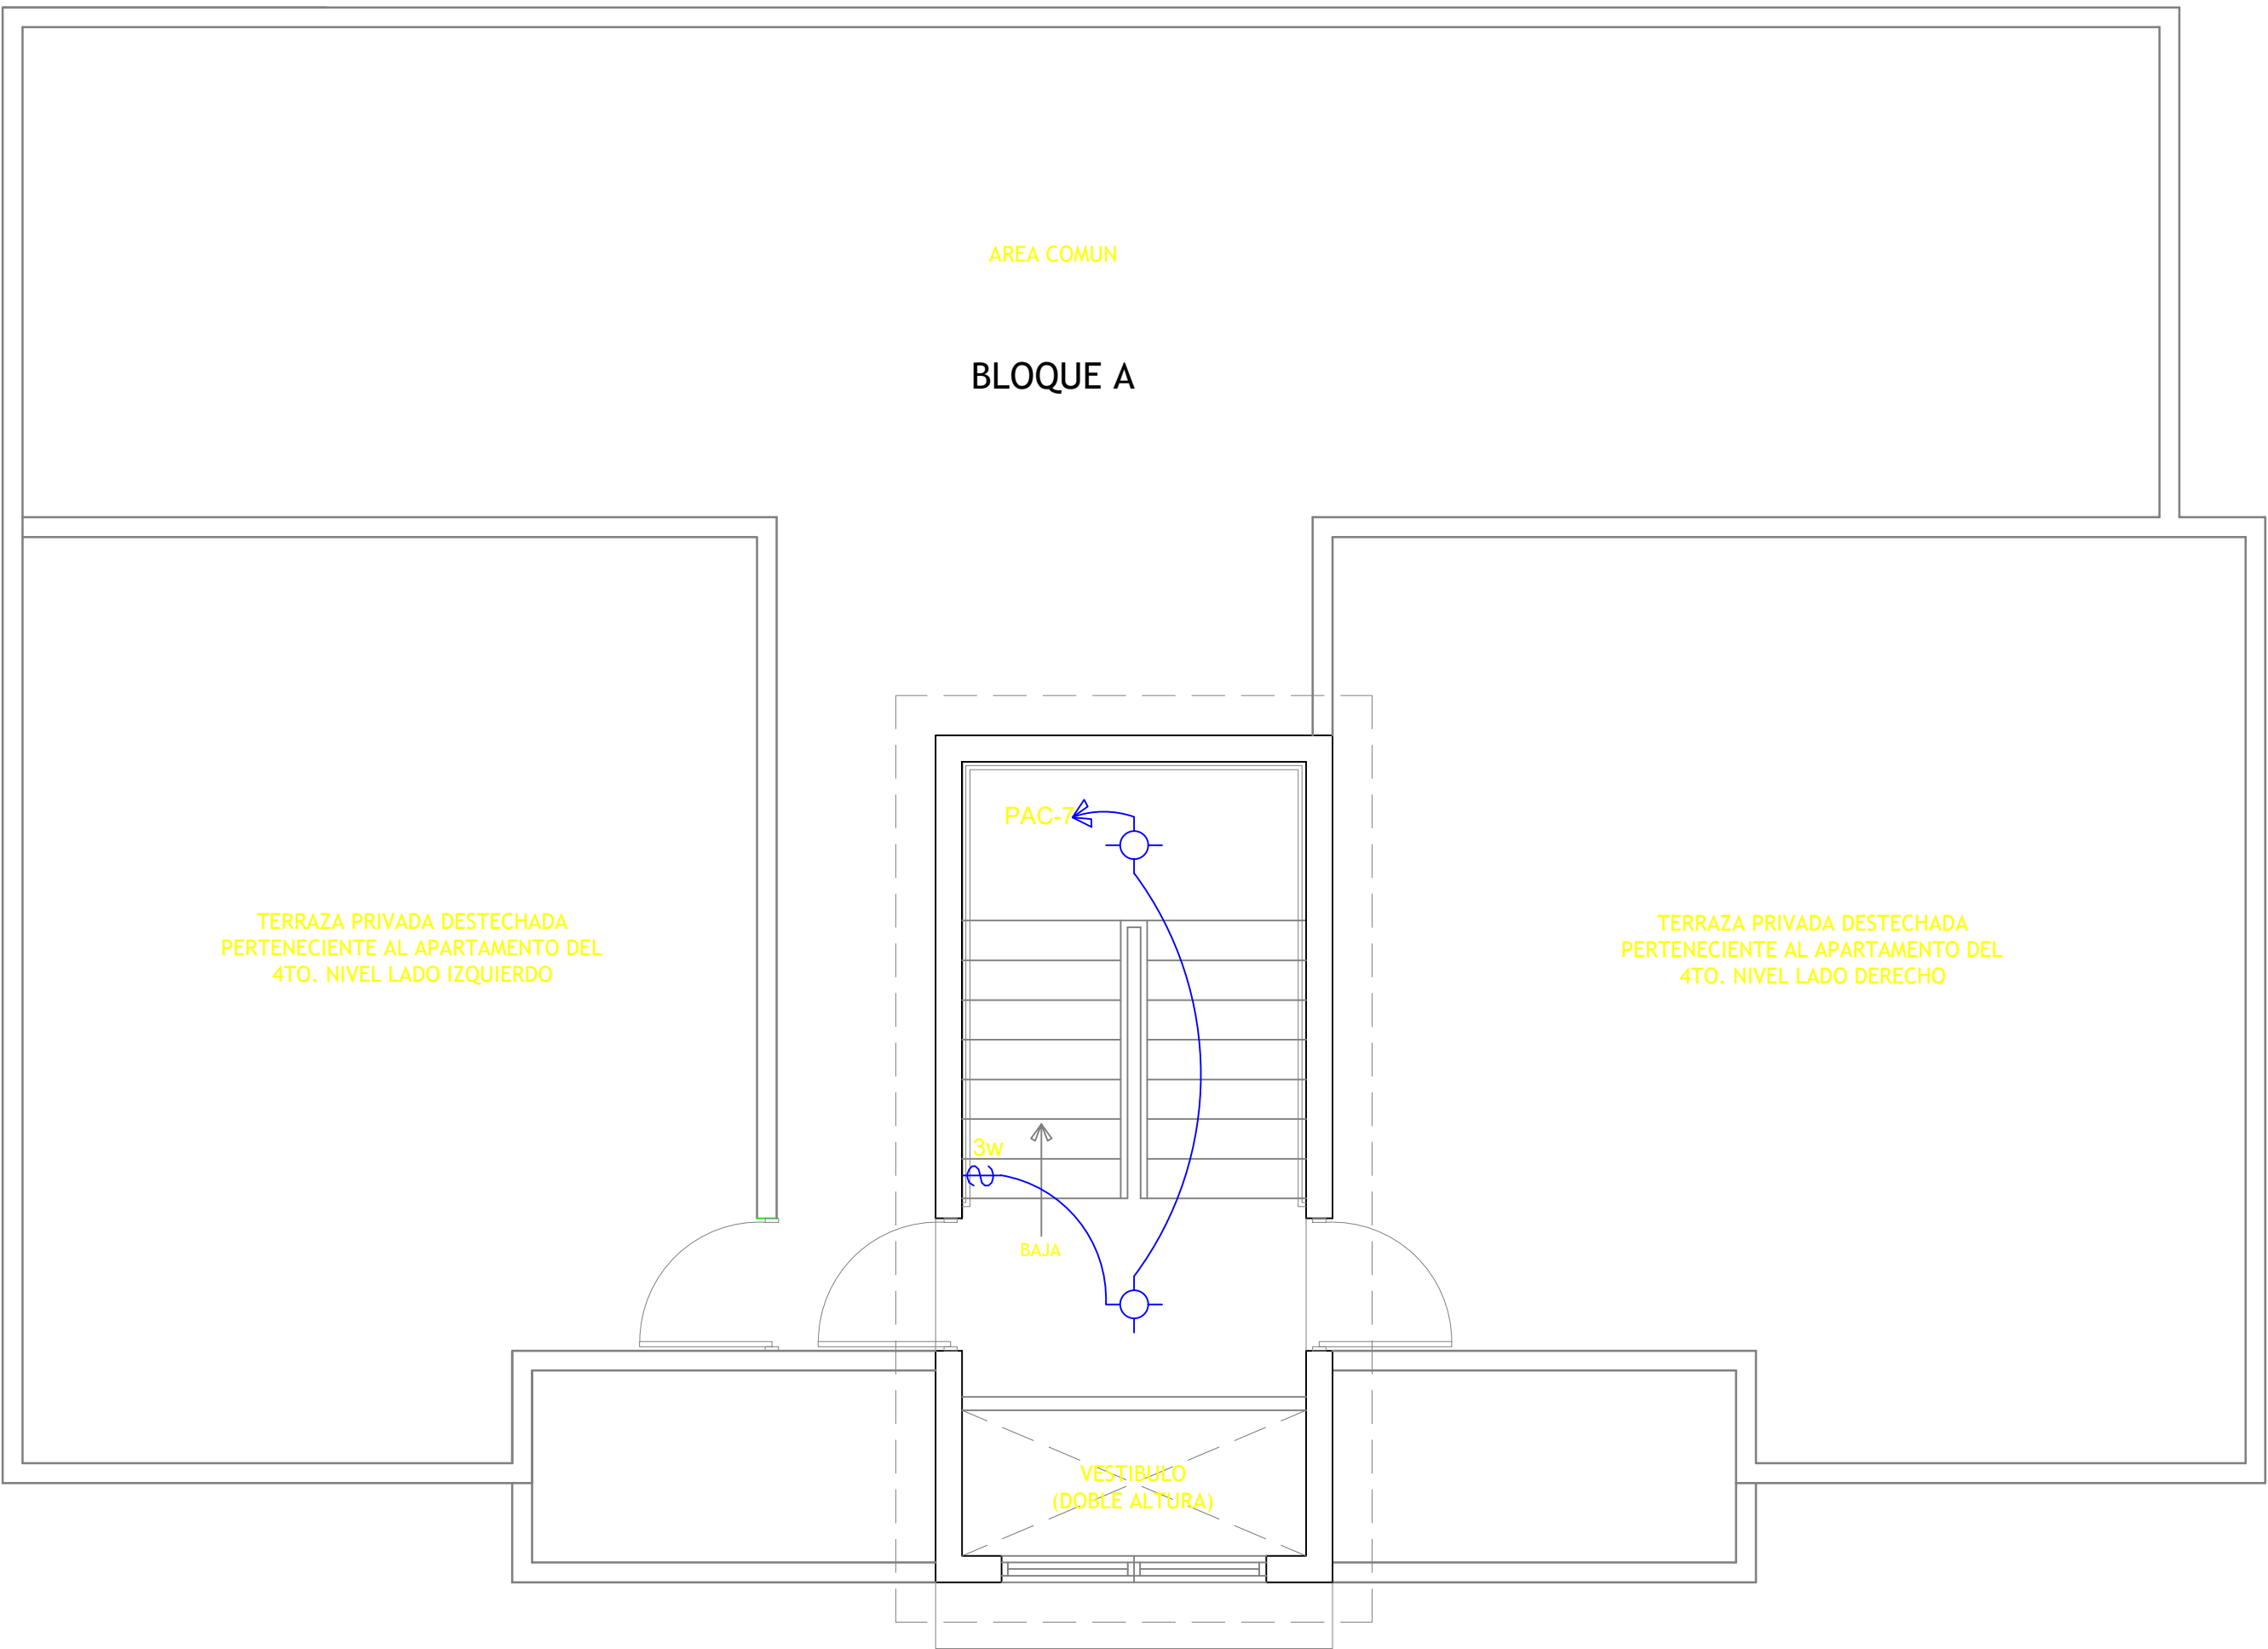


PLANTA LUMINARIAS AZOTEA, BLOQUE A
ESCALA: 1:75

1
EL-07

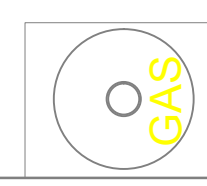


- LEYENDA ELECTRICA**
- POSTE DE CONCRETO DE 35 PIES
 - \$ SALIDA DE INTERRUPTOR SENCILLO
 - \$ab SALIDA DE INTERRUPTOR DOBLE
 - \$3w SALIDA DE INTERRUPTOR DE TRES VIAS
 - ⊖ SALIDA DE INTERRUPTOR DOBLE
 - ⊖ SALIDA DE INTERRUPTOR DE TRES VIAS
 - ▼ SALIDA DE TELEFONO
 - ⌵ SALIDA DE ANTENA
 - SALIDA DE INTERCOM
 - SALIDA DE INTERCOM
 - 📞 SALIDA DE CAMPANA DE TIMBRE
 - ⚡ PANEL DE DISTRIBUCION ELECTRICO
 - ⚡ PANEL DE DISTRIBUCION ELECTRICO
 - ⚡ PANEL DE DISTRIBUCION ELECTRICO
 - CONDUCTOR EMPOTRADO EN EL TECHO Y/O PANEL
 - CONDUCTOR EMPOTRADO EN EL TECHO Y/O PANEL
 - Ⓜ MEDIDOR ELECTRICO
 - ⚡ TRANSFORMADOR ELECTRICO
 - S CUT OUT

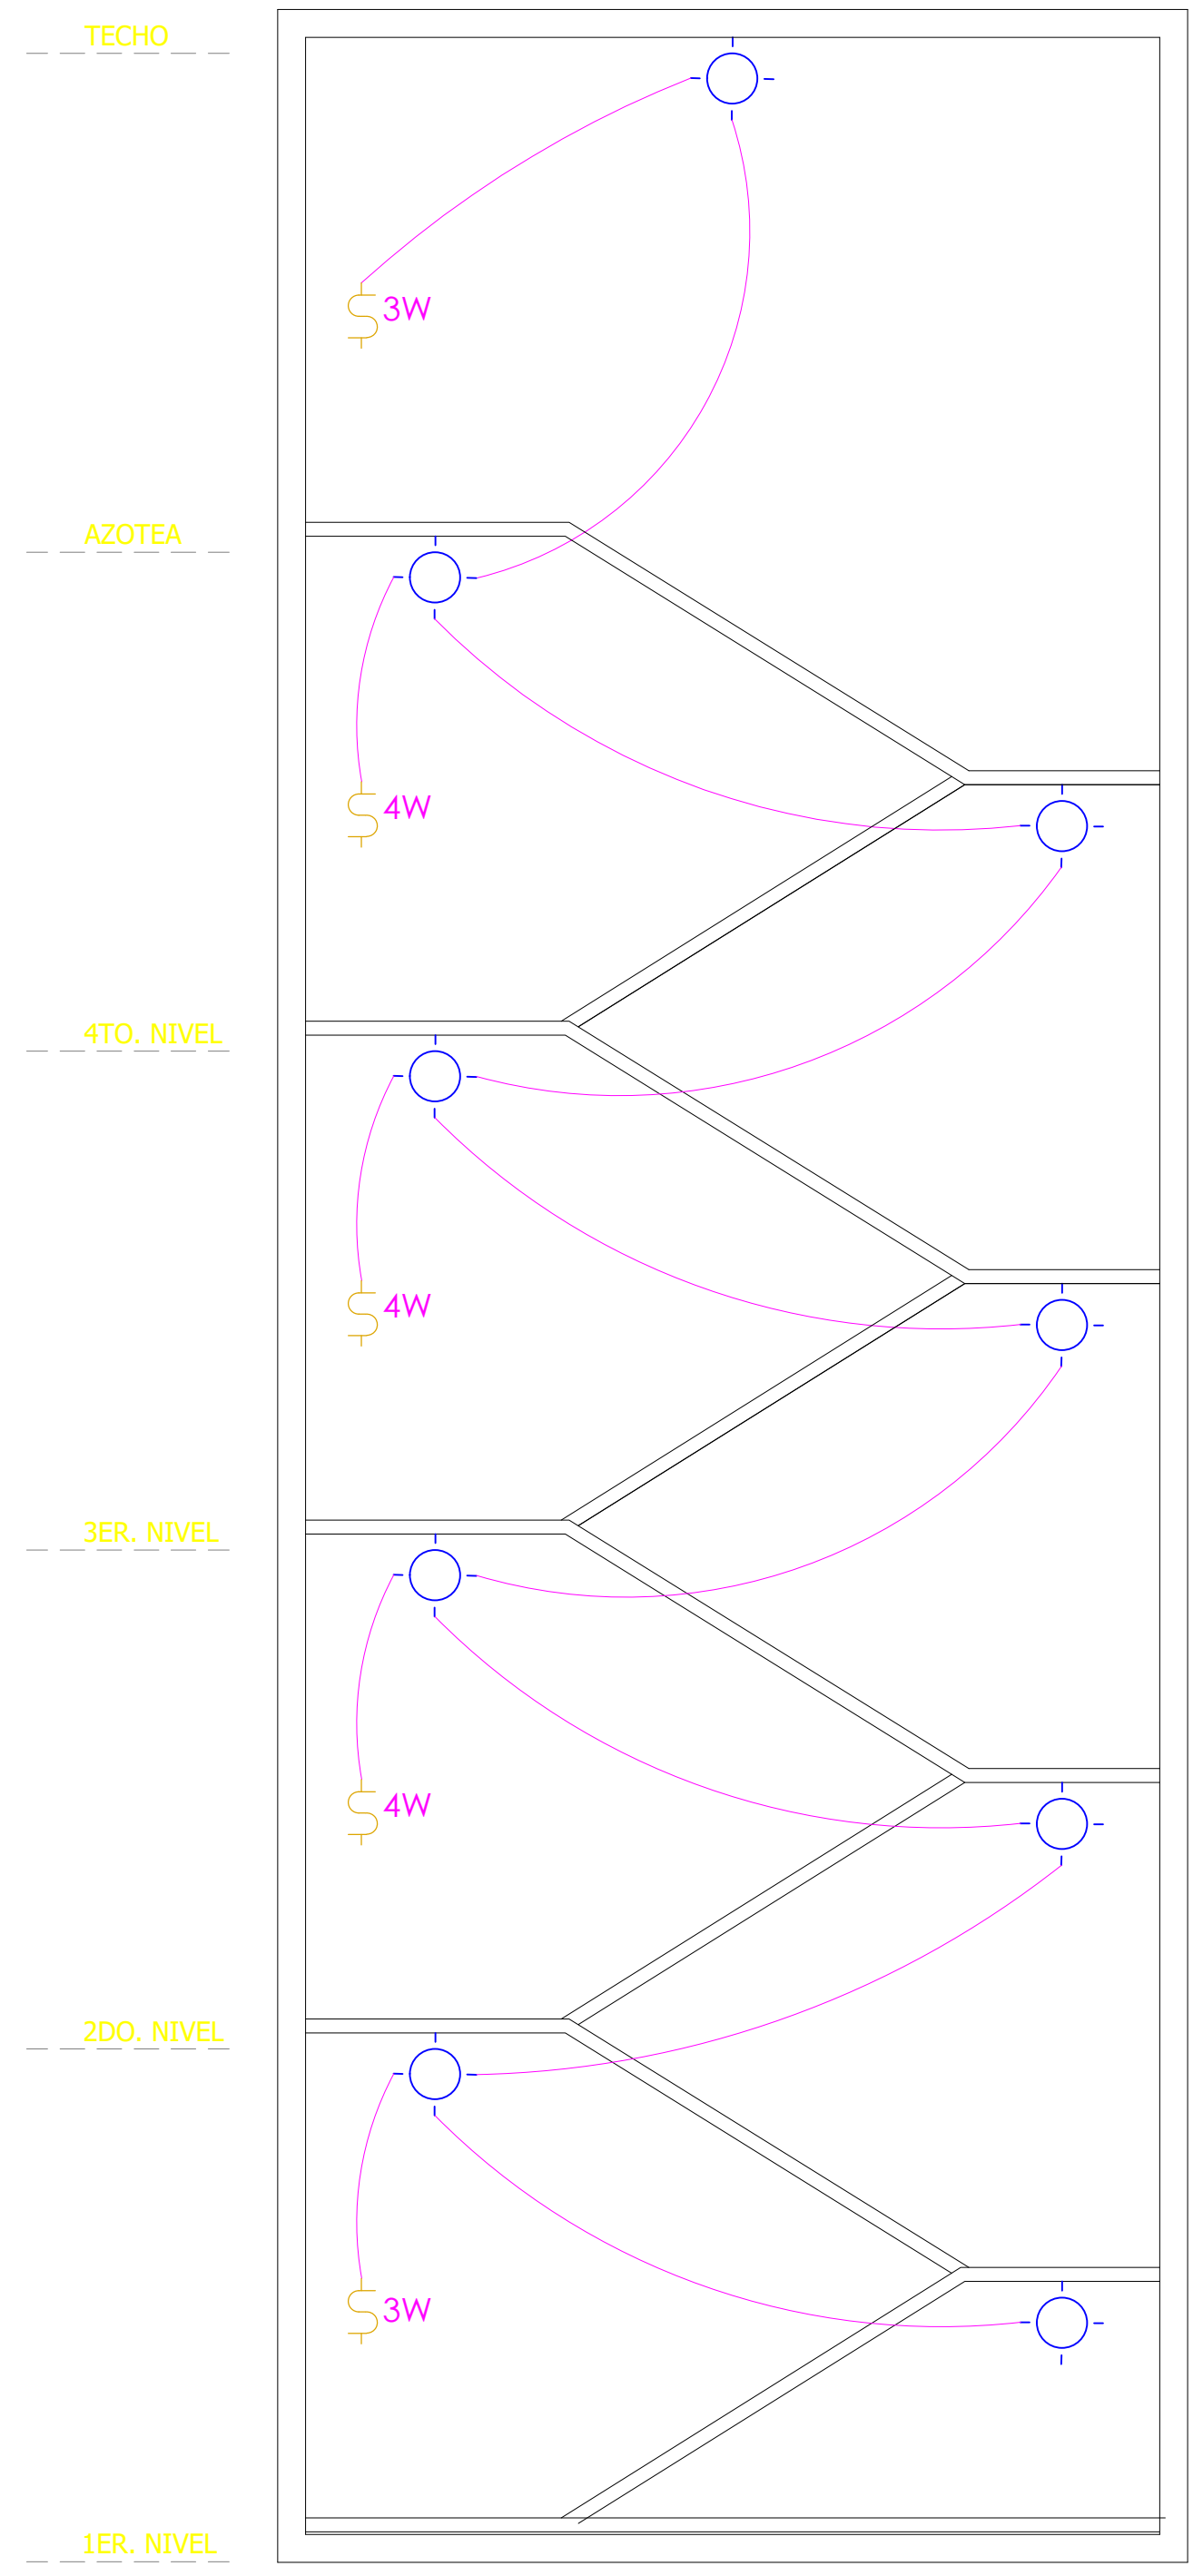

DETALLE ILUMINACION ESCALERA BLOQUE A
NO ESCALA

3
EL-07

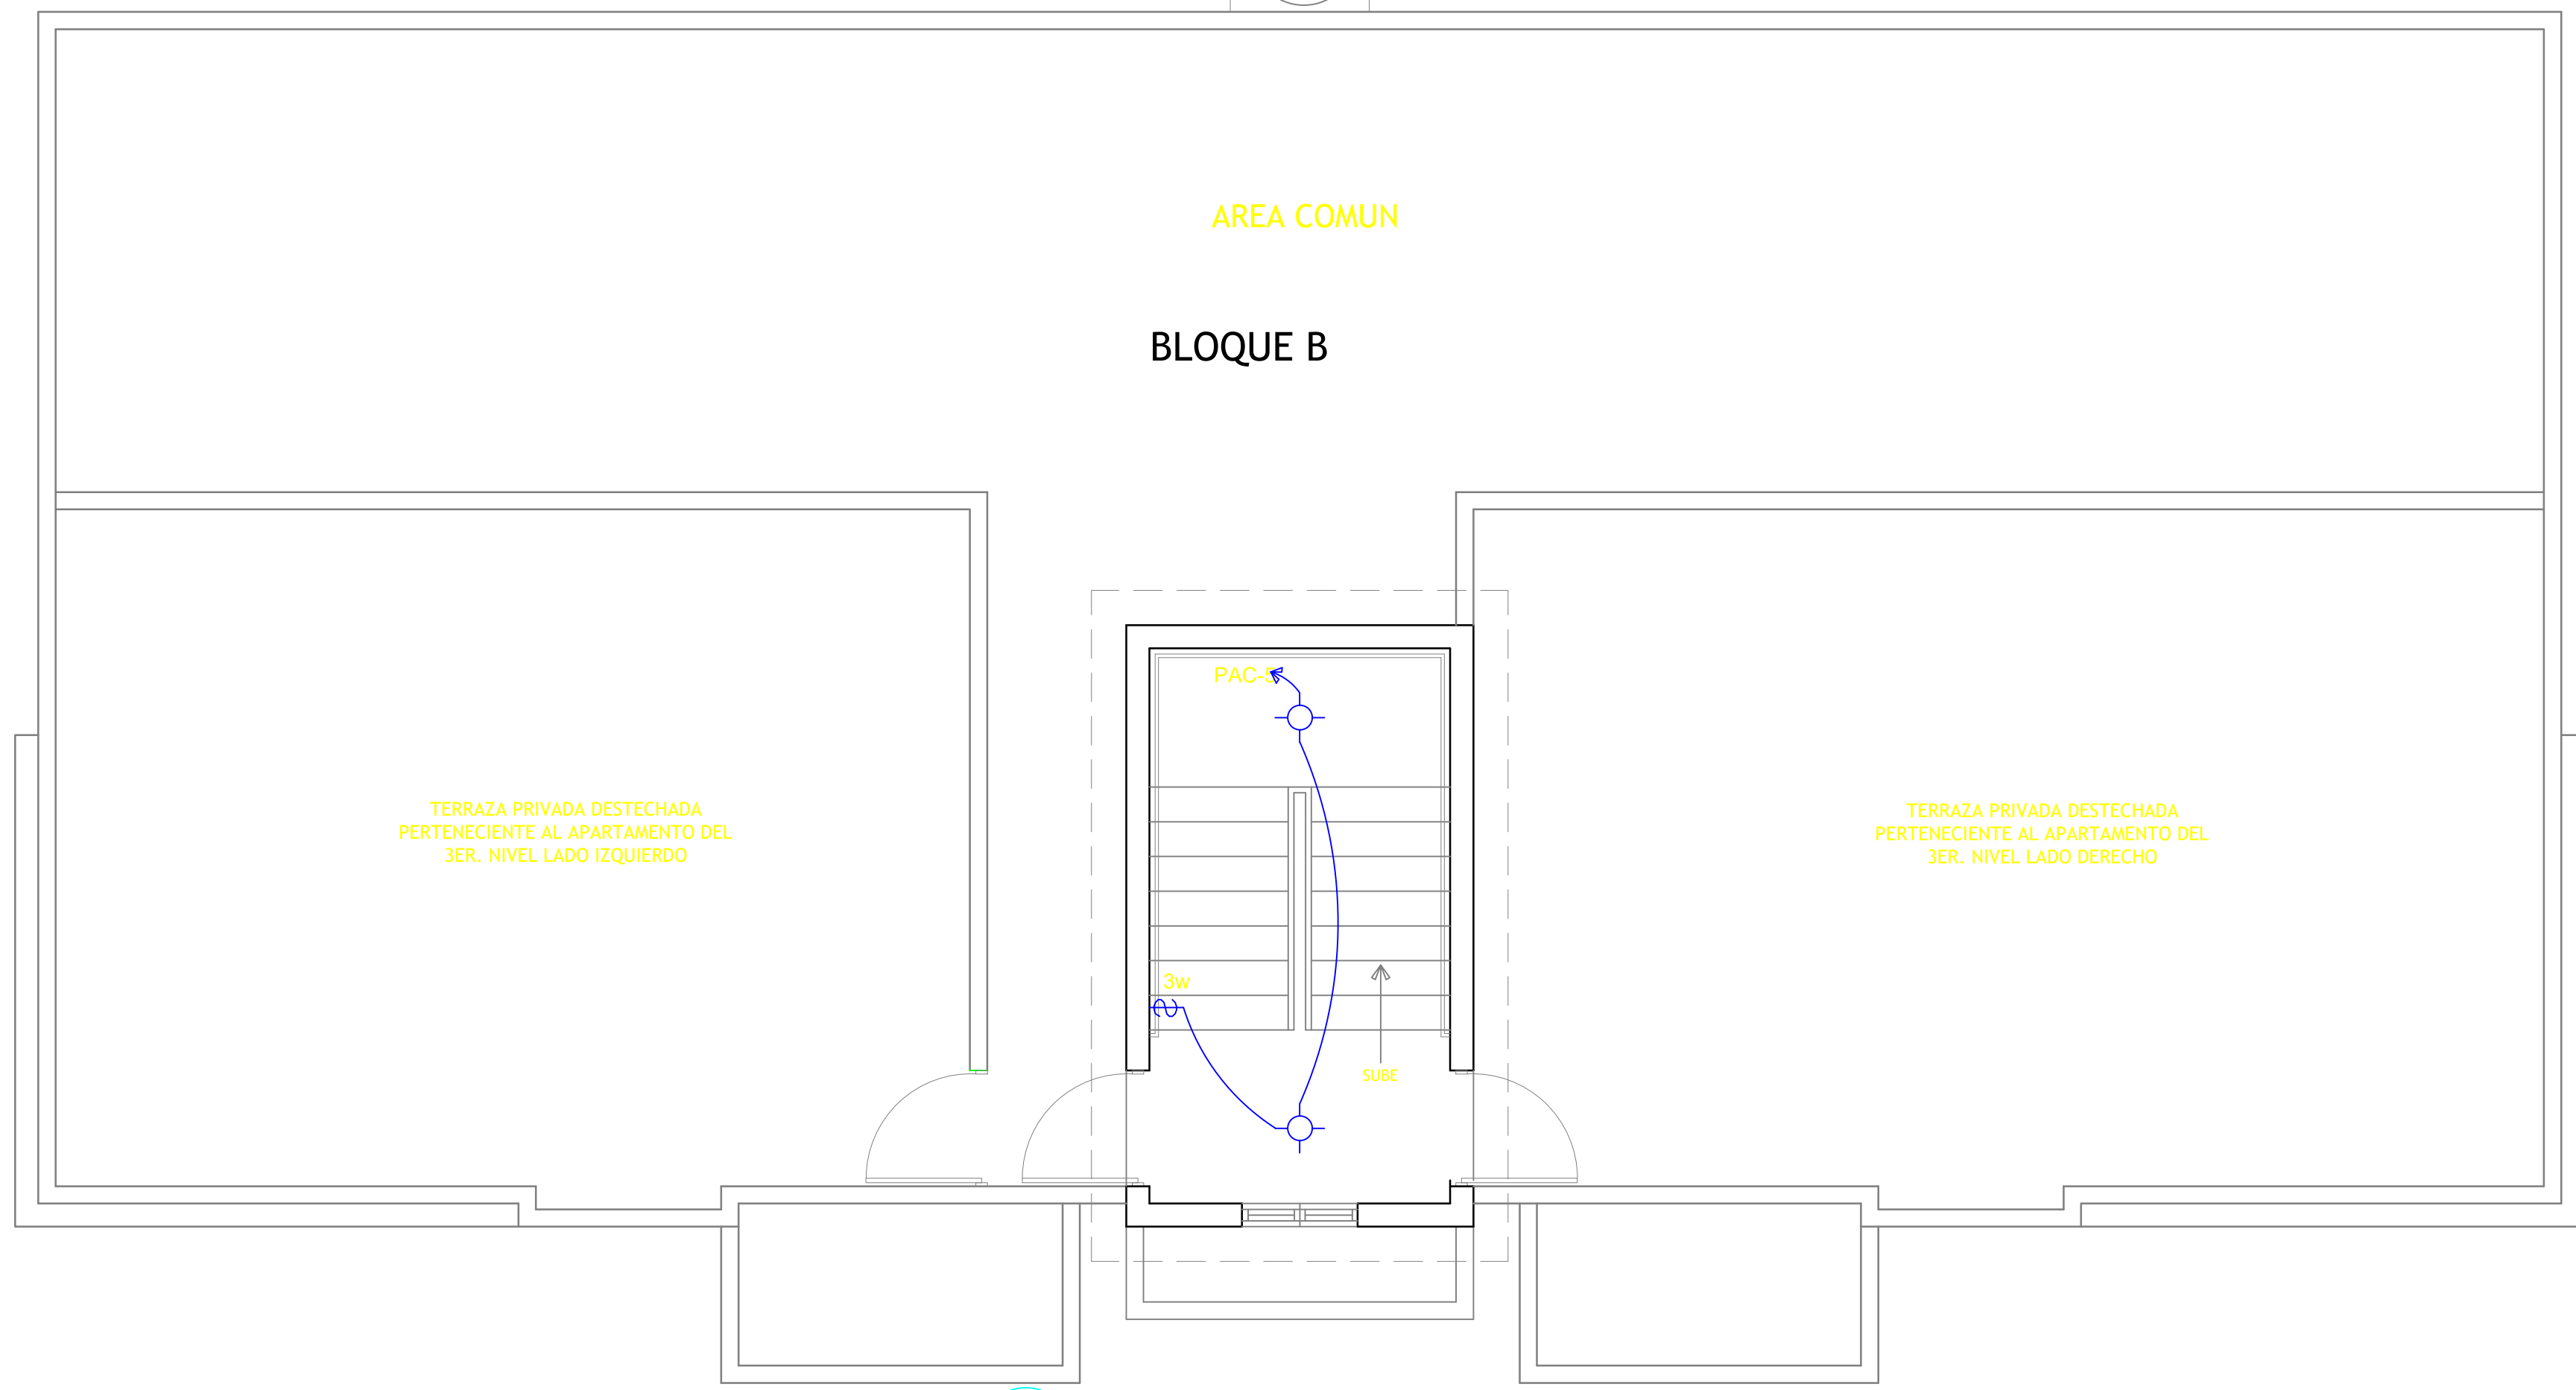

PLANTA LUMINARIAS AZOTEA, BLOQUE B
ESCALA: 1:75

2
EL-07

Presidente Billini # 12, Bani, R.D. 522-4989
E-mail: diazmelo@hotmail.com

COLABORACION:

ARQUITECTURA DIGITAL
DISEÑOS-CONSTRUCCION-DIGITACION
COMPROMETIDOS CON SU TIEMPO
C/JUAN SANCHEZ RAMIREZ #56,
LOCAL 5 ZONA UASD TEL:221-5400

PROPIETARIO:

GRUPO EMPRESARIAL
BANILEJO S.R.L.
GEBSA

PROYECTISTAS:

DISEÑO ARQUITECTONICO:
DIAZMELO & ASOCS.
Arq. ISMAEL DIAZ MELO
Codia: 9604

DISEÑO SANITARIO:
Arq. HAMLET TEJEDA
Codia: 18303

DISEÑO ESTRUCTURAL:
ING. ODELIN TEJEDA
Codia: 23937

DISEÑO ELECTRICO:
ING. VILLYS SANCHEZ
Codia: 19060

CONTENIDO:

PLANTAS , LUMINARIAS Y
TOMACORRIENTES
3ER. NIVEL BLOQUE B

PROYECTO:

RESIDENCIAL GEBSA IV

Fecha: MAYO/2018

UBICACION:

BANI, PROV. PERAVIA

Ref.: Acad 2000

Hoja No.

Escala: INDICADA

NOTAS:

TODAS LAS TERMINACIONES Y/O CAMBIOS EN EL SET DE DOCUMENTOS CONSTRUCTIVOS DEBERAN SER APROBADOS POR EL SUPERVISOR PREVIAMENTE A SU APLICACION EN LA OBRA.


TODAS LAS MEDIDAS DE HUECOS Y DE SUPERFICIE A SER REVESTIDAS SERAN RECTIFICADAS PREVIA FABRICACION DE LOS CERRES O LA O LA INSTALACION DE LOS RECUBRIMIENTOS

LAS TERMINACIONES Y / O DETALLES NO ESPECIFICADOS SERAN DEFINIDOS ENTRE EL DUEÑO Y EL AUTOR DEL PROYECTO.

EL CONTRATISTA NO PODRA TOMAR DECISIONES INCONSULTAS RESPECTO VARIACIONES EN EL CONTENIDO DE ESTE DOCUMENTO

LOS PLANOS ARQUITECTONICOS MANDARAN RESPECTO A LOS DEMAS A ANTE CUALQUIER DIFERENCIA, PRIMARA LA INFORMACIONCONTENIDA EN LOS MISMOS

LEYENDA	
	LINEA PRIMARIA AEREA 30 7.2/12.5 KV EXISTENTE
	POSTE 1/4 EXISTENTE
	LINEAS PRIMARIAS AEREA 10 7.2 KV EXISTENTE
	MODULO DE CONTADORES
	LINEAS PRIMARIAS SOTERRADA 30 7.2/12.5 KV PROPUESTA
	TRANSFORMADOR TIPO POSTE EXISTENTE
	PANEL DE DISTRIBUCION
	VIENTO SENCILLO A TIERRA EXISTENTE
	PUESTA A TIERRA
	TRANSFORMADOR PAD MOUNTED 30 112.5KVA
	7.2/12.5 KV -120/208 V ; 60 HZ, PROPUESTO
	PASADIZO DE 9 KV, 10 KA
	CUT-OUT 1/100BLK, 200 AMPS - 15 KV
	CONO ALIVIO INTERIOR, ELBOW CONECTOR-ASLADO P/15 KV
	CONO DE ALIVIO EXTERIOR AISL P/15 KV
	GENERADOR DE ENERGIA
	MAIN BREAKER
	LINEA SECUNDARIA (TRIPLEX 4/0 EXISTENTE) 120/240V

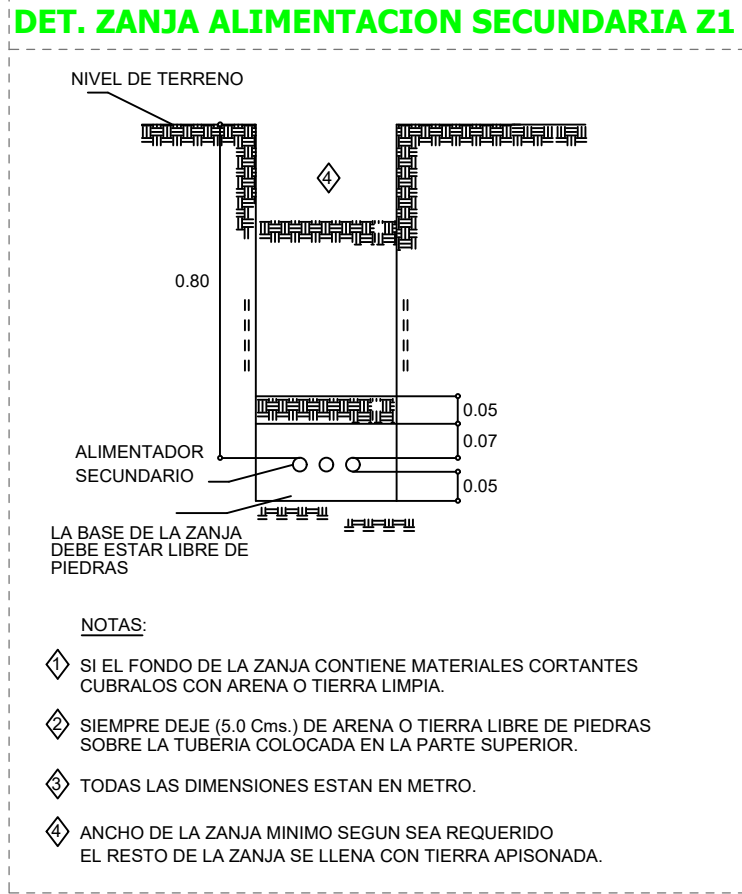

Selección de la Sub-Estación				
ITEM	Panel	Cantidad	Carga Conectada	Total de carga Conectada
1	PA	4	12.65	50.6
1.2	PB	4	15.55	62.2
1.3	PC	6	15.90	95.4
Total de KVA				208.2
2	Área Común			
2.1	PAC	1	18.6	10.4
Total de KVA AC.				10.4
3	TOTAL CARGA	FD	AREA COMUN	TOTAL KVA
	208.2	0.4	10.4	93.68
La Sub-Estación será de un transf. tipo pad mounted 112.5 KVA, 3φ, 60 Hz, 12.5 KV-240-120v				

- NOTAS GENERALES:**
- LOS INTERRUPTORES Y PULSADORES ESTARAN A 1.20 Ml. (SNT).
 - LOS TOMACORRIENTES, SALIDAS DE ANTENA Y TELEF. ESTARAN A 0.30 Ml. (SNT).
 - TODAS LAS TUBERIAS SERAN DE Ø1/2", SALVO OTRA INDICACION.
 - TODOS LOS TOMACORRIENTES SERAN ATERRIZADOS CON UN CONDUCTOR.
 - LA CAJA DE BRAKER Y PORTA CONTADOR DEBEN SER ATERRIZADAS.
 - TODAS LAS TUBERIAS DE ANTENA Y TELEF. SON DE Ø3/4".
 - PARA LOS CONDUCTORES ELECT. DEBE USARSE EL CODIGO DE COLORES:
 - POTENCIALES: ROJO, NEGRO.
 - NEUTRO: BLANCO.
 - TIERRA: VERDE.
 - LOS ALIMENTADORES PRINCIPALES SON Ø 1" PVC, DUCTO.
 - TODO EL SISTEMA ESTÁ ATERRIZADO CON UN TWH/0.
 - LA COMUNICACION DESDE EL MODULO DE PORTA CONTADOR HASTA LOS DISTINTOS PANELES DE DISTRIBUCION SERA DE FORMA SOTERRADA EN TUBOS DE UNA PULGADA.

VISTA EN PLANTA

NO ESCALA




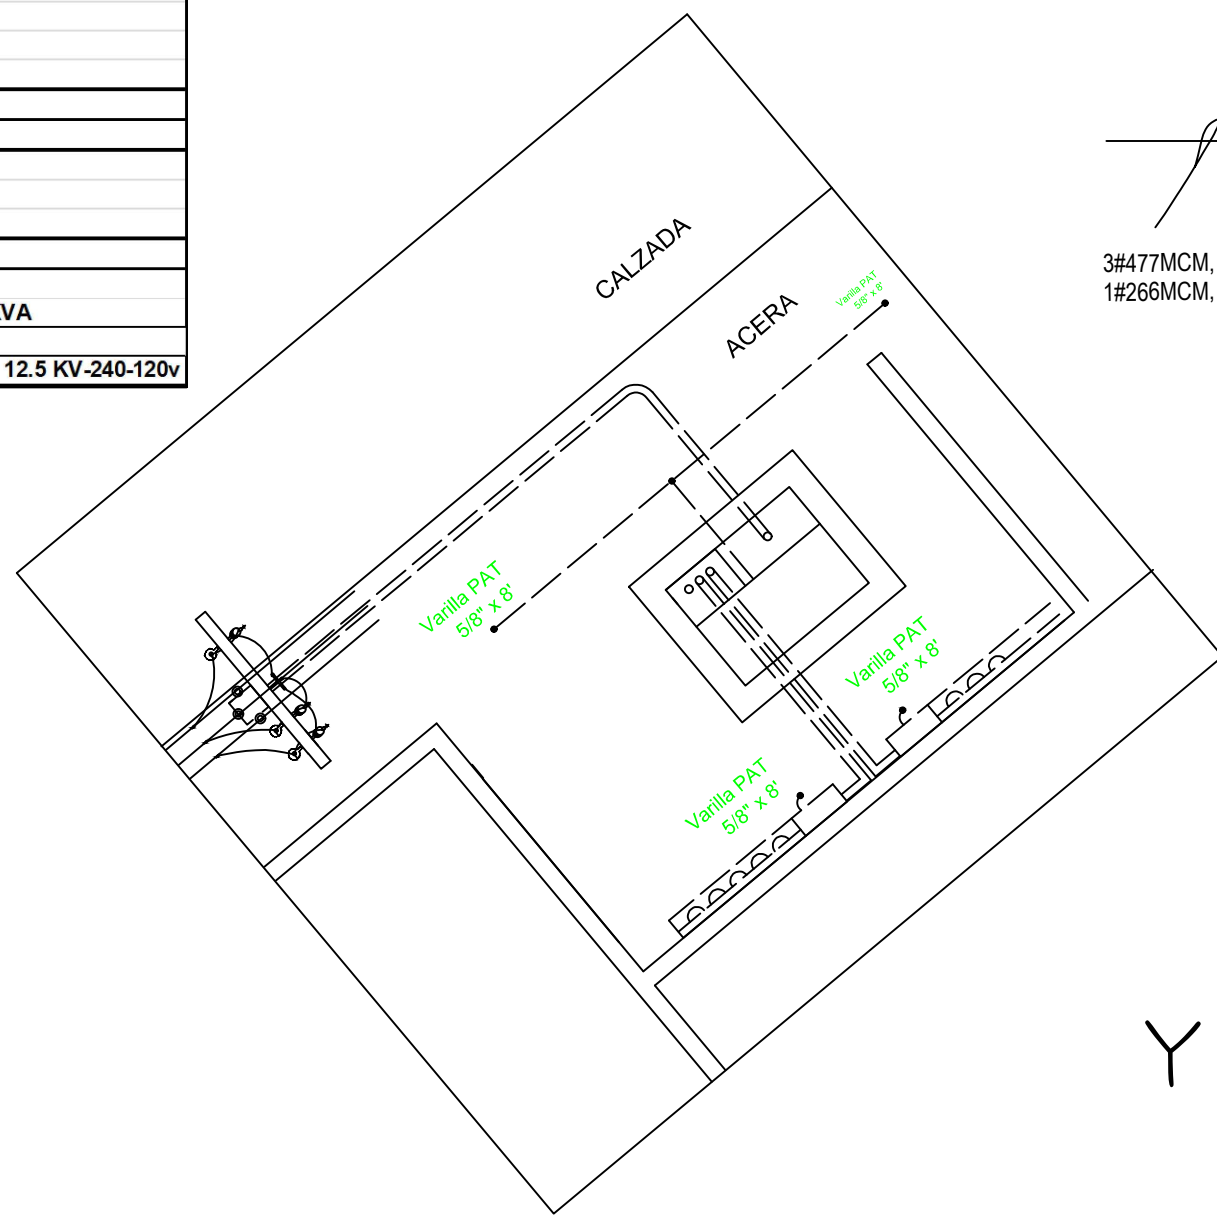


DIAGRAMA UNIFILAR

Punto. Interconexion

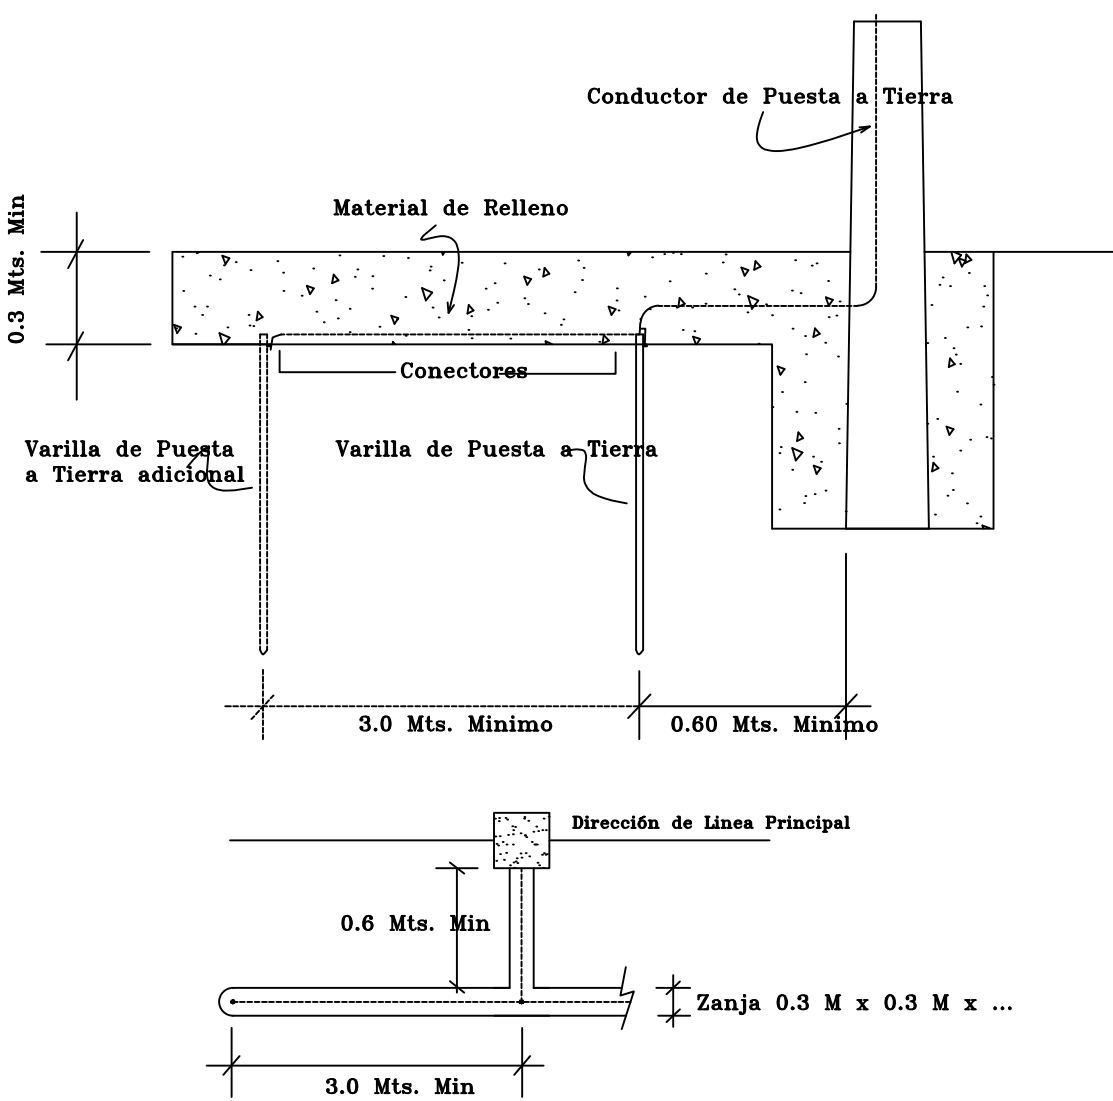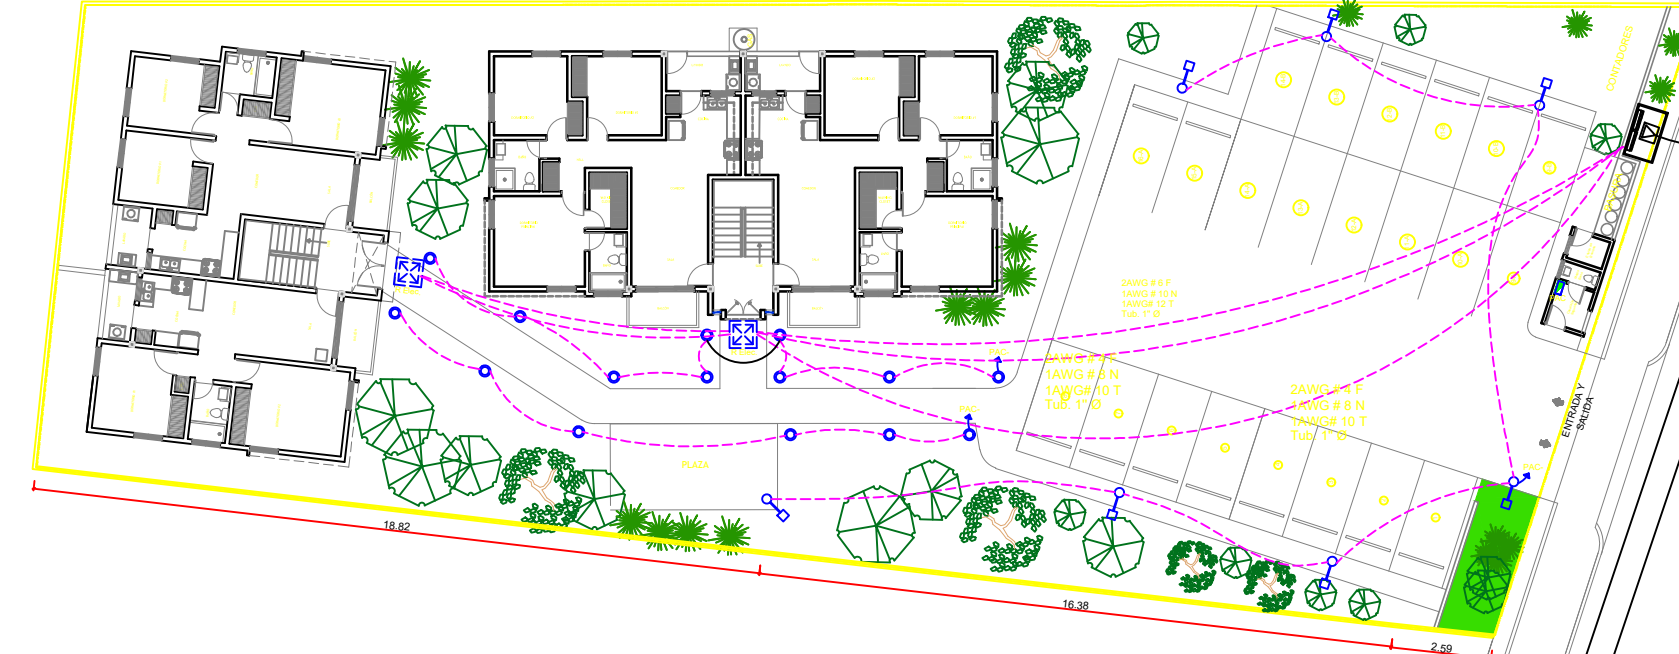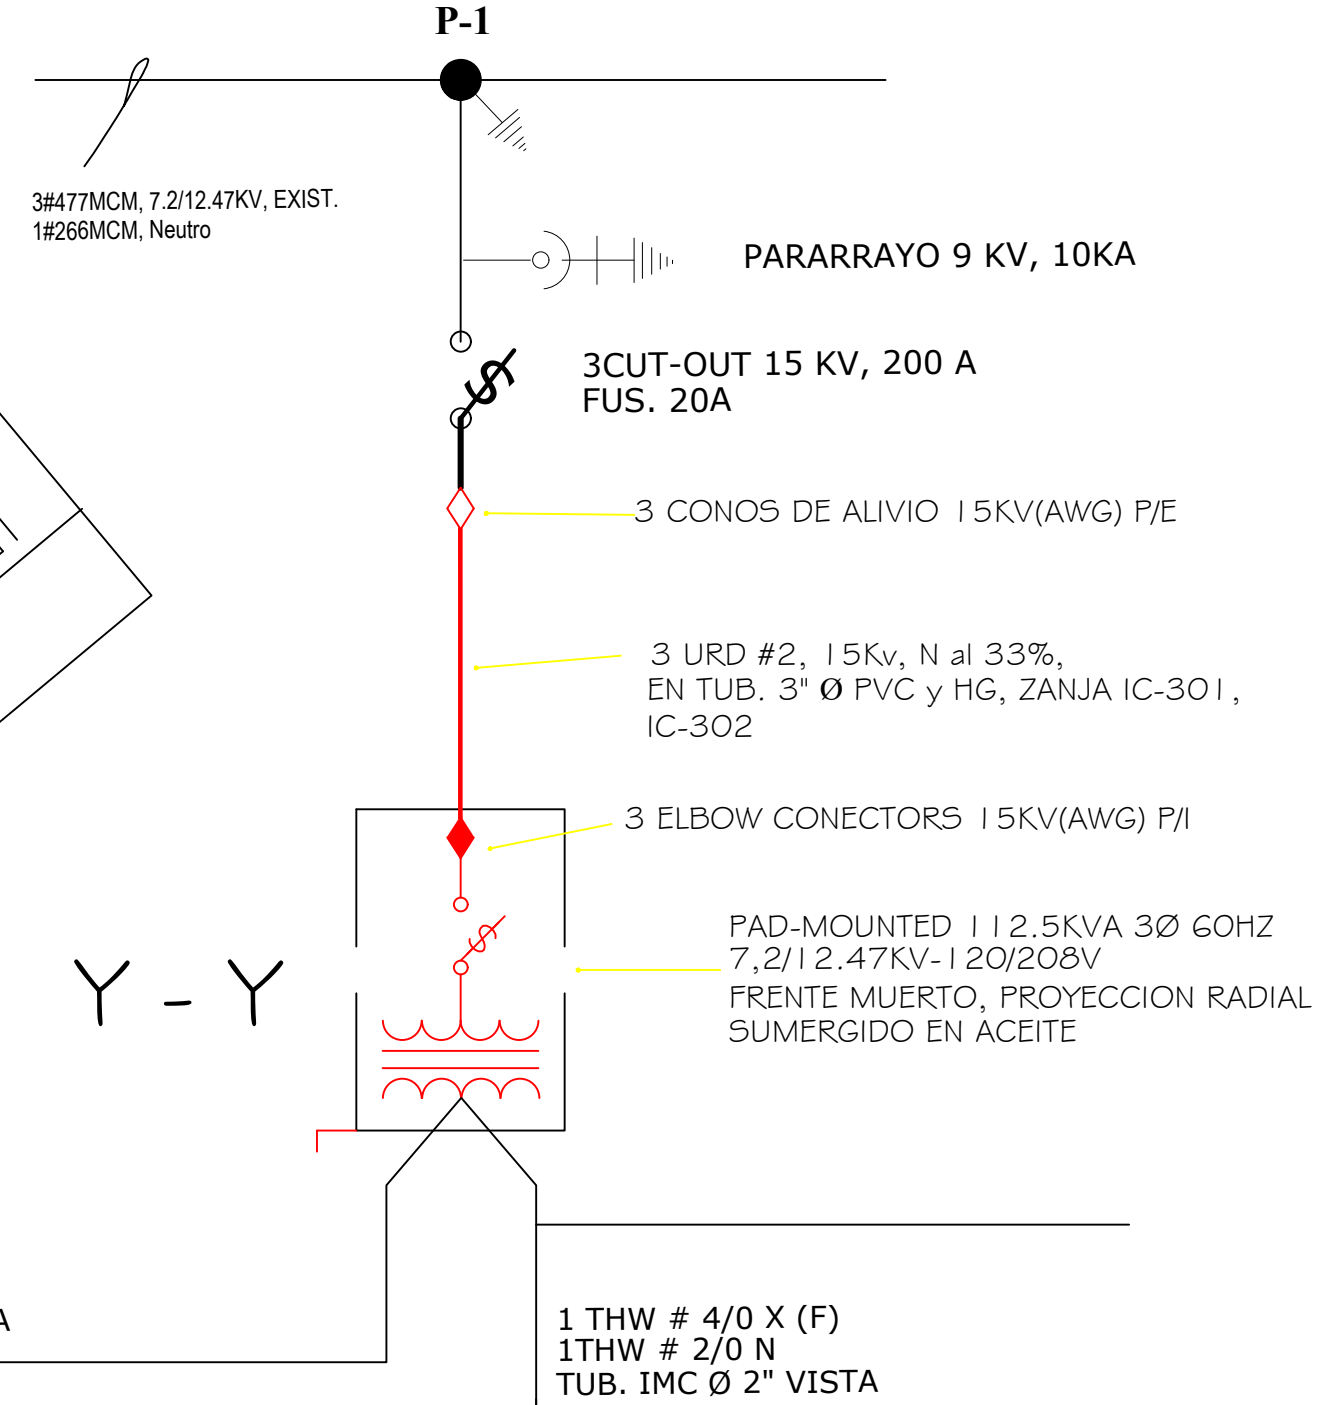


RESISTENCIA DE LA TIERRA

Postes de Media Tensión, Terminales MT y BT--Máximo 5 OHMIOS
Postes Con Transformadores y Seccionadores -- Máximo 2 OHMIOS
Cantidad Maxima de Varillas 4

NOTA:
El material de relleno de baja resistencia y Bien Compactado



Detalle de Puesta a Tierra en Poste

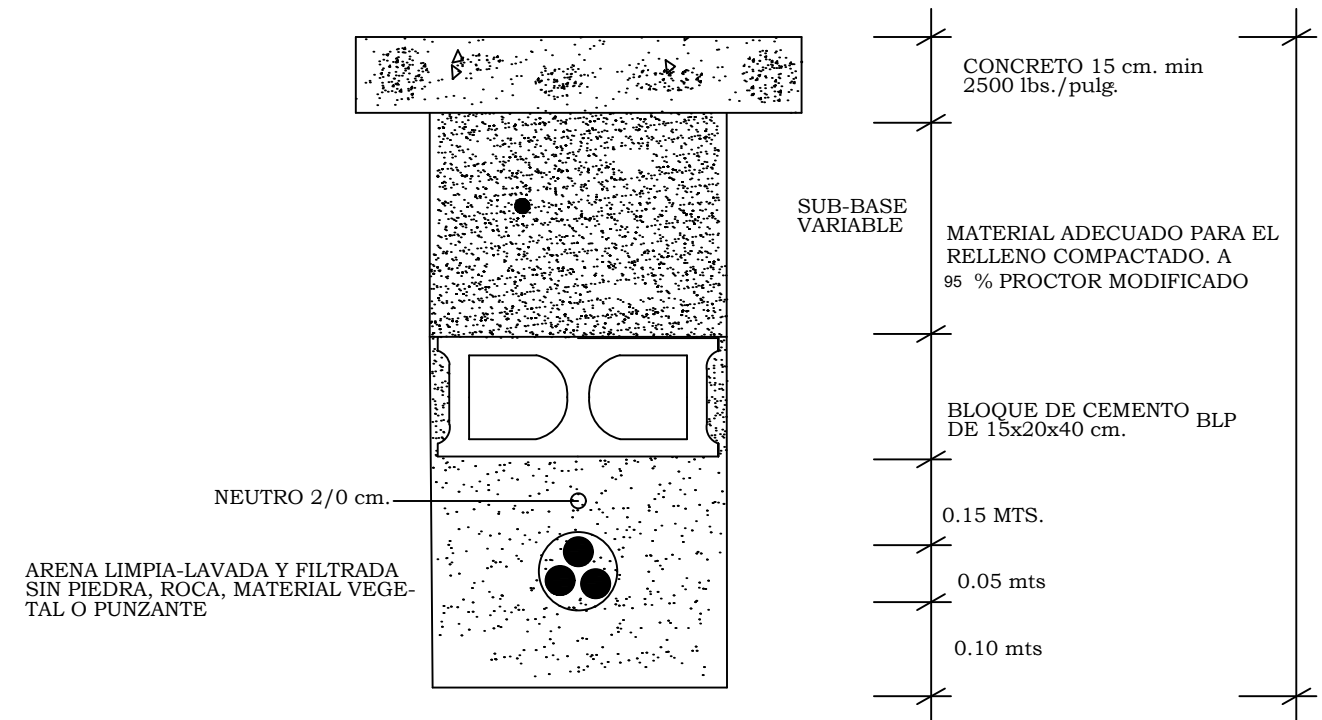

Detalle de Zanja IC-302


VISTA LATERAL

NO ESCALA

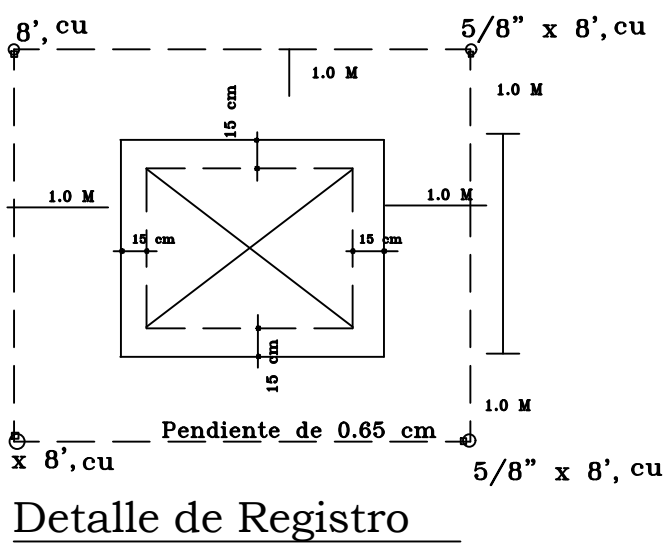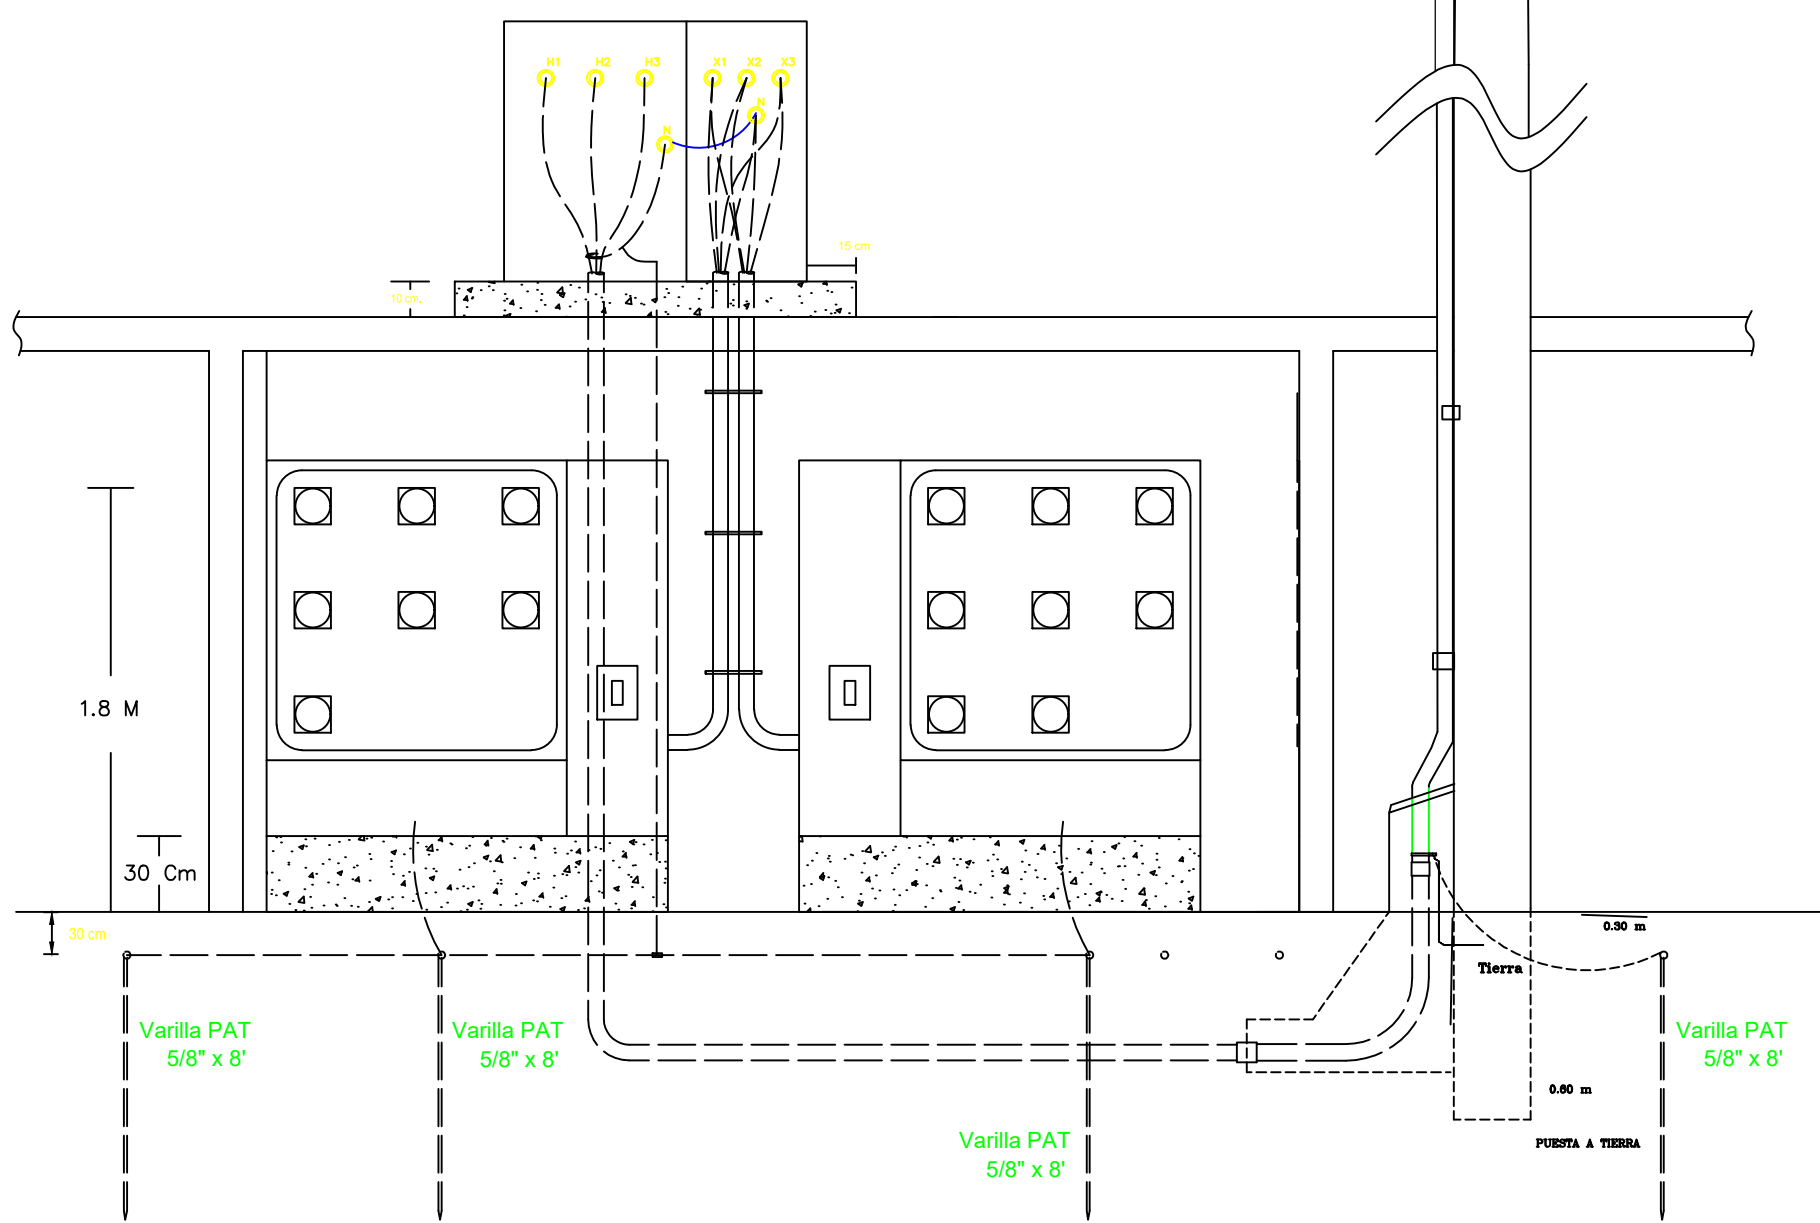


Detalle de Registro



NO ESCALA

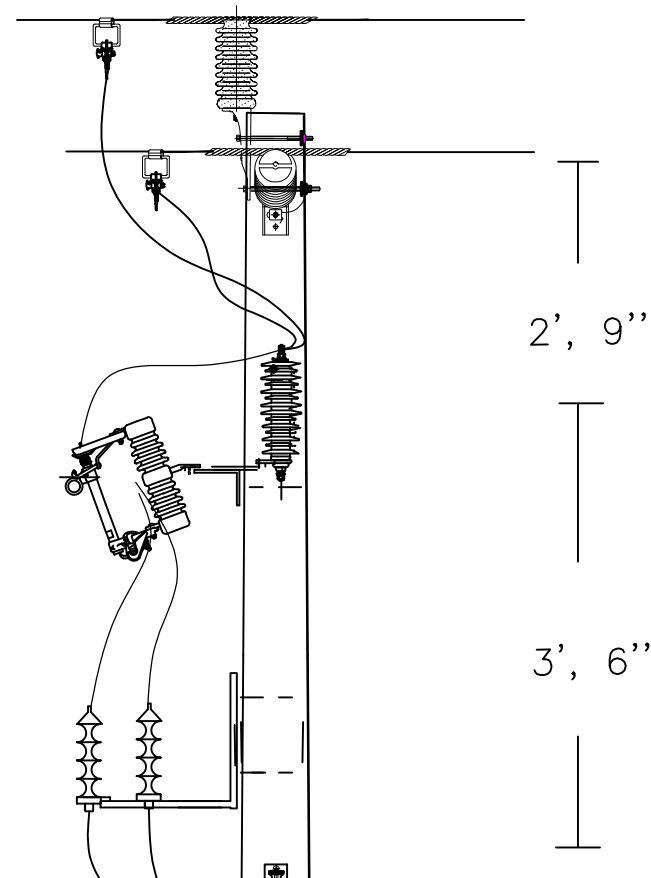

1 THW # 4/0 X (F)
1THW # 2/0 N
TUB. IMC Ø 2" VISTA

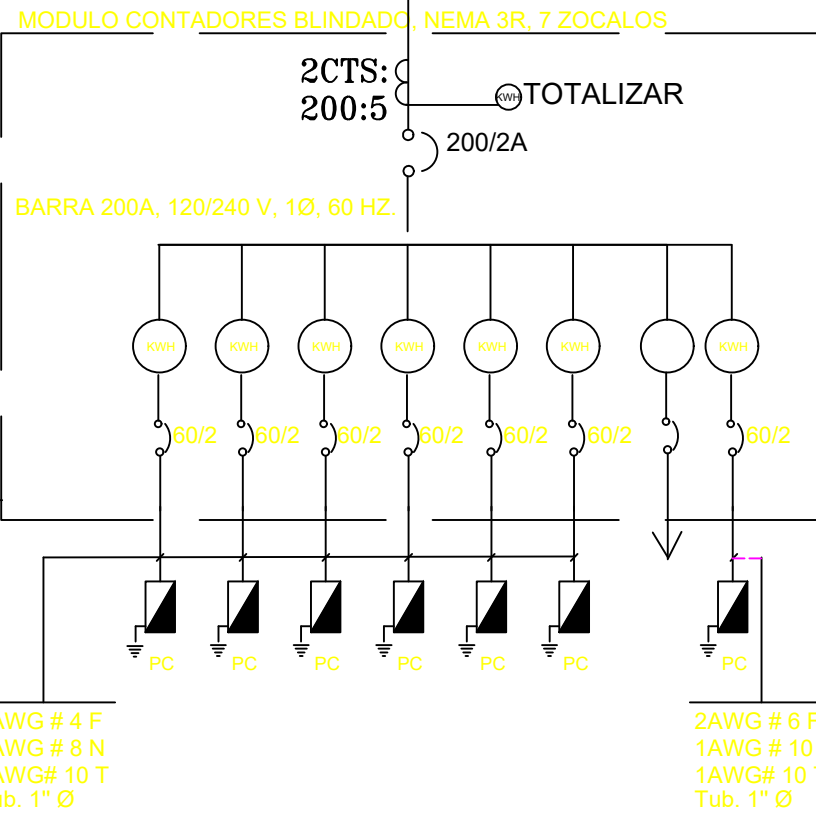

1 THW # 4/0 X (F)
1THW # 2/0 N
TUB. IMC Ø 2" VISTA

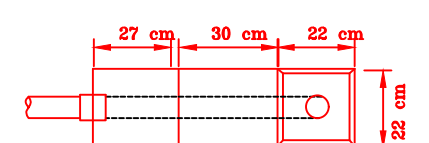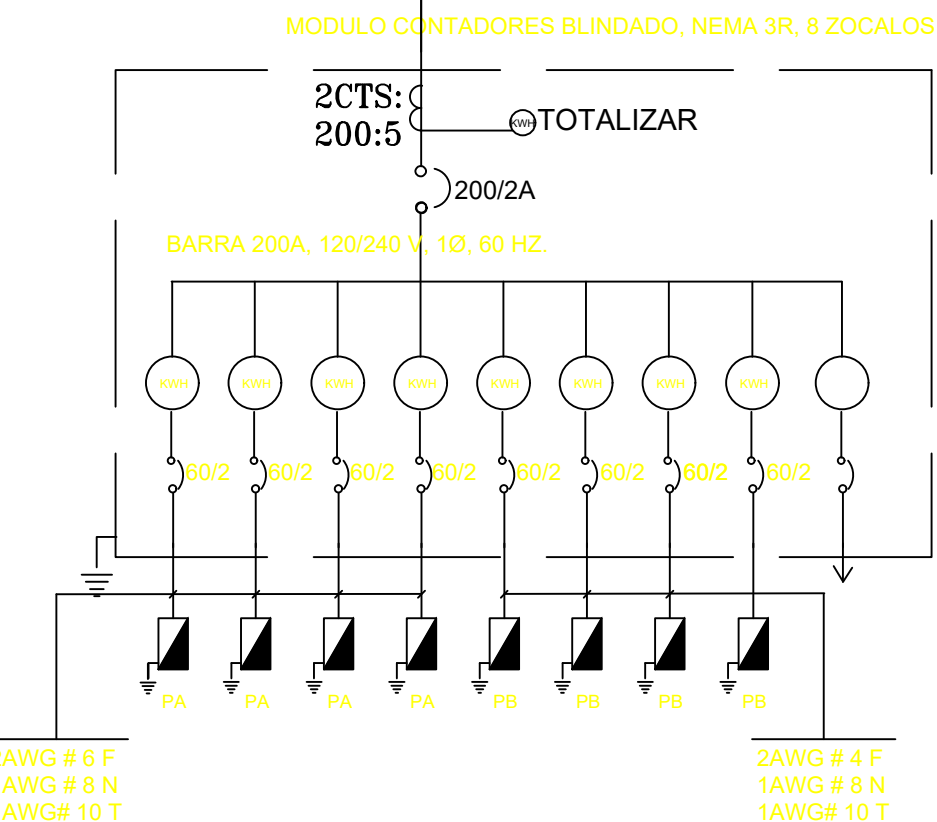

Detalle de Base SS-1

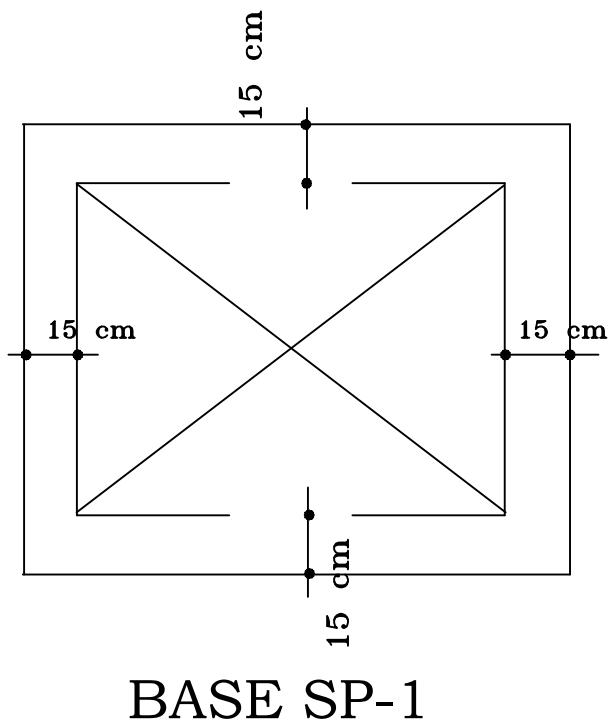


TABLA DE ESTRUCTURA

POSTE			ESTRUCTURA EXISTENTE		ESTRUCTURA PROPUESTA		ESTRUCTURA REMOCION		OBSERVACIONES
No	EXISTENTE	PROPUESTO	REMOVER	MT	BT	MT	BT	MT	
P - 1	HA-40'			ALPS	SU-BT	PR-102, PR-202, SO2-MT, SS1			Punto de interconexión
P - 2	HA-40'			ALPS, CSA-8', 3SP2-MT	SU-BT F1-BT AP-103				
P - 3	HA-40'			ALPS, DS-3, F1-MT	AL-BT F1-BT				
P - 4	HA-35'			MT-105, TR-105	AL-BT AP-103				CT: 048298
P - 5	HA-40'			AGPD	SU-BT				
P - 6	HA-40'			ALPS, AM-102	SU-BT				
P - 7	HA-40'			AGAC, HA-108	F2-BT				



diazmeo & asocs.
ARQUITECTOS
Presidente Bilini # 12, Bari, R.D. 522-4989
E-mail: diazmeo@hotmail.com

COLABORACION:



ARQUITECTURA DIGITAL
DISEÑOS-CONSTRUCCION-DIGITACION
COMPROMETIDOS CON SU TIEMPO
C/JUAN SANCHEZ RAMIREZ #56,
LOCAL 5 ZONA UASD TEL:221-5400

PROPIETARIO:
**GRUPO EMPRESARIAL
BANILEJO S.R.L.
GEBSA**

PROYECTISTAS:

DISEÑO ARQUITECTONICO:
DIAZMELO & ASOCS.

Arq. ISMAEL DIAZ MELO

Codia: 9604

DISEÑO SANITARIO:
Arq. HAMLET TEJEDA

Codia: 18303

DISEÑO ESTRUCTURAL:
ING. ODELIN TEJEDA

Codia: 23937

DISEÑO ELECTRICO:
ING. VILLYS SANCHEZ

Codia: 19060

CONTENIDO:
**DETALLES ELECTRICOS
GENERALES**

PROYECTO:
RESIDENCIAL GEBSA IV

Fecha: MAYO/2018

UBICACION:

BANI, PROV. PERAVIA

Ref.: Acad 2000

Hoja No.

Escala: INDICADA

NOTAS:
TODAS LAS TERMINACIONES Y/O CAMBIOS EN EL SET. DE DOCUMENTOS CONSTRUCTIVOS DEBERAN SER APROBADOS POR EL SUPERVISOR PREVIAMENTE A SU APLICACION EN LA OBRA.
TODAS LAS MEDIDAS DE HUECOS Y DE SUPERFICIE A SER REVESTIDAS SERAN REVISADAS PREVIA FABRICACION DE LOS CORRIERES O LA O.A. INSTALACION DE LOS RECURRIMIENTOS
LAS TERMINACIONES Y / O DETALLES NO ESPECIFICADOS SERAN DEFINIDOS ENTRE EL DUEÑO Y EL AUTOR DEL PROYECTO.
EL CONTRATISTA NO PODRA TOMAR DECISIONES INCONSULTAS RESPECTO A VARIACIONES EN EL CONTENIDO DE ESTE DOCUMENTO
LOS PLANOS ARQUITECTONICOS MANDARAN RESPECTO A LOS DEMAS A DIFERENCIA, PRIMARA LA INFORMACIONCONTENIDA EN LOS MISMOS