



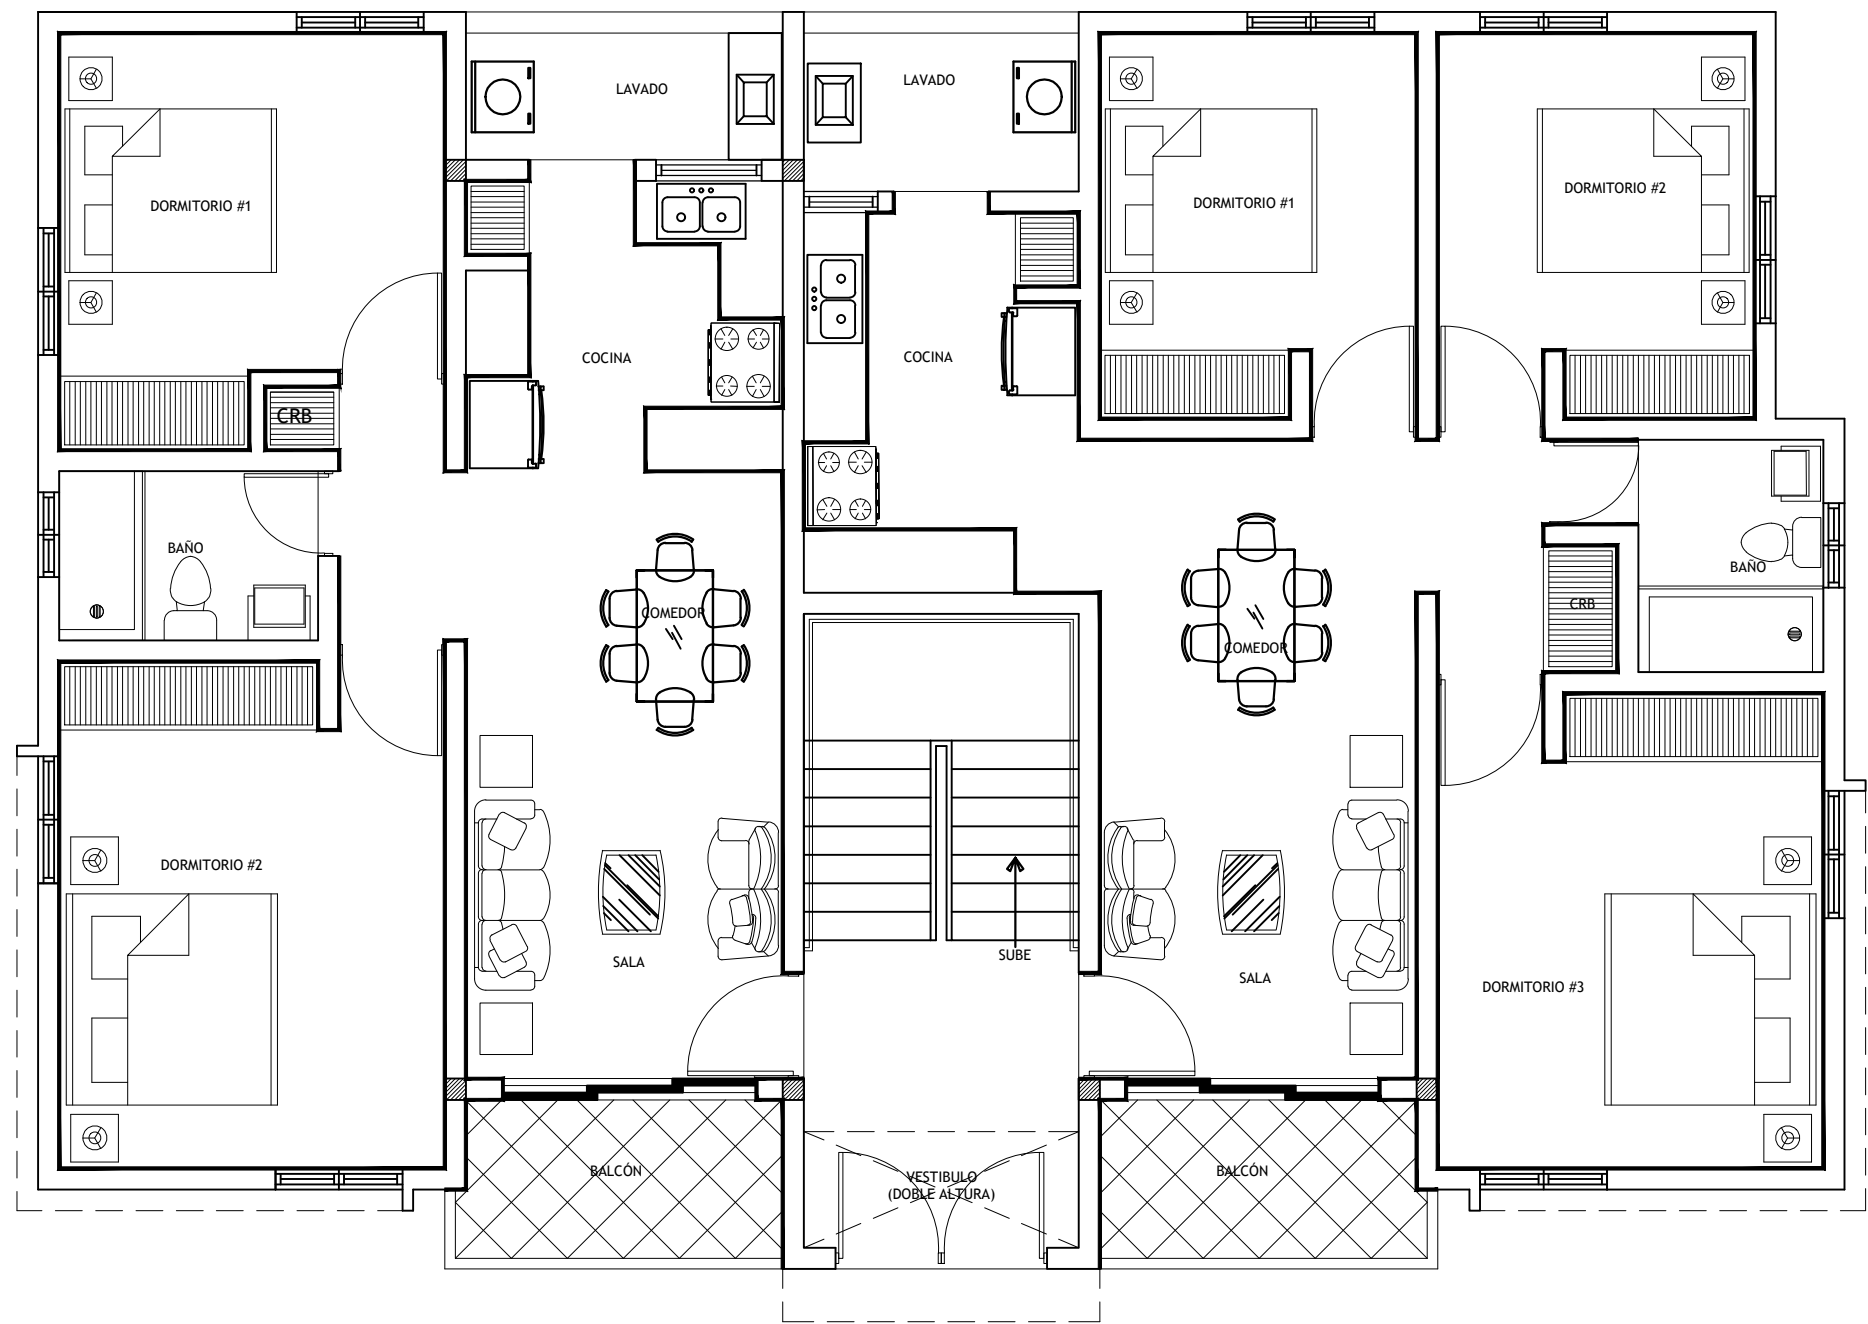


PLANTA ARQUITECTONICA 1ER. NIVEL, BLOQUE A
ESCALA: 1:75

1
A04

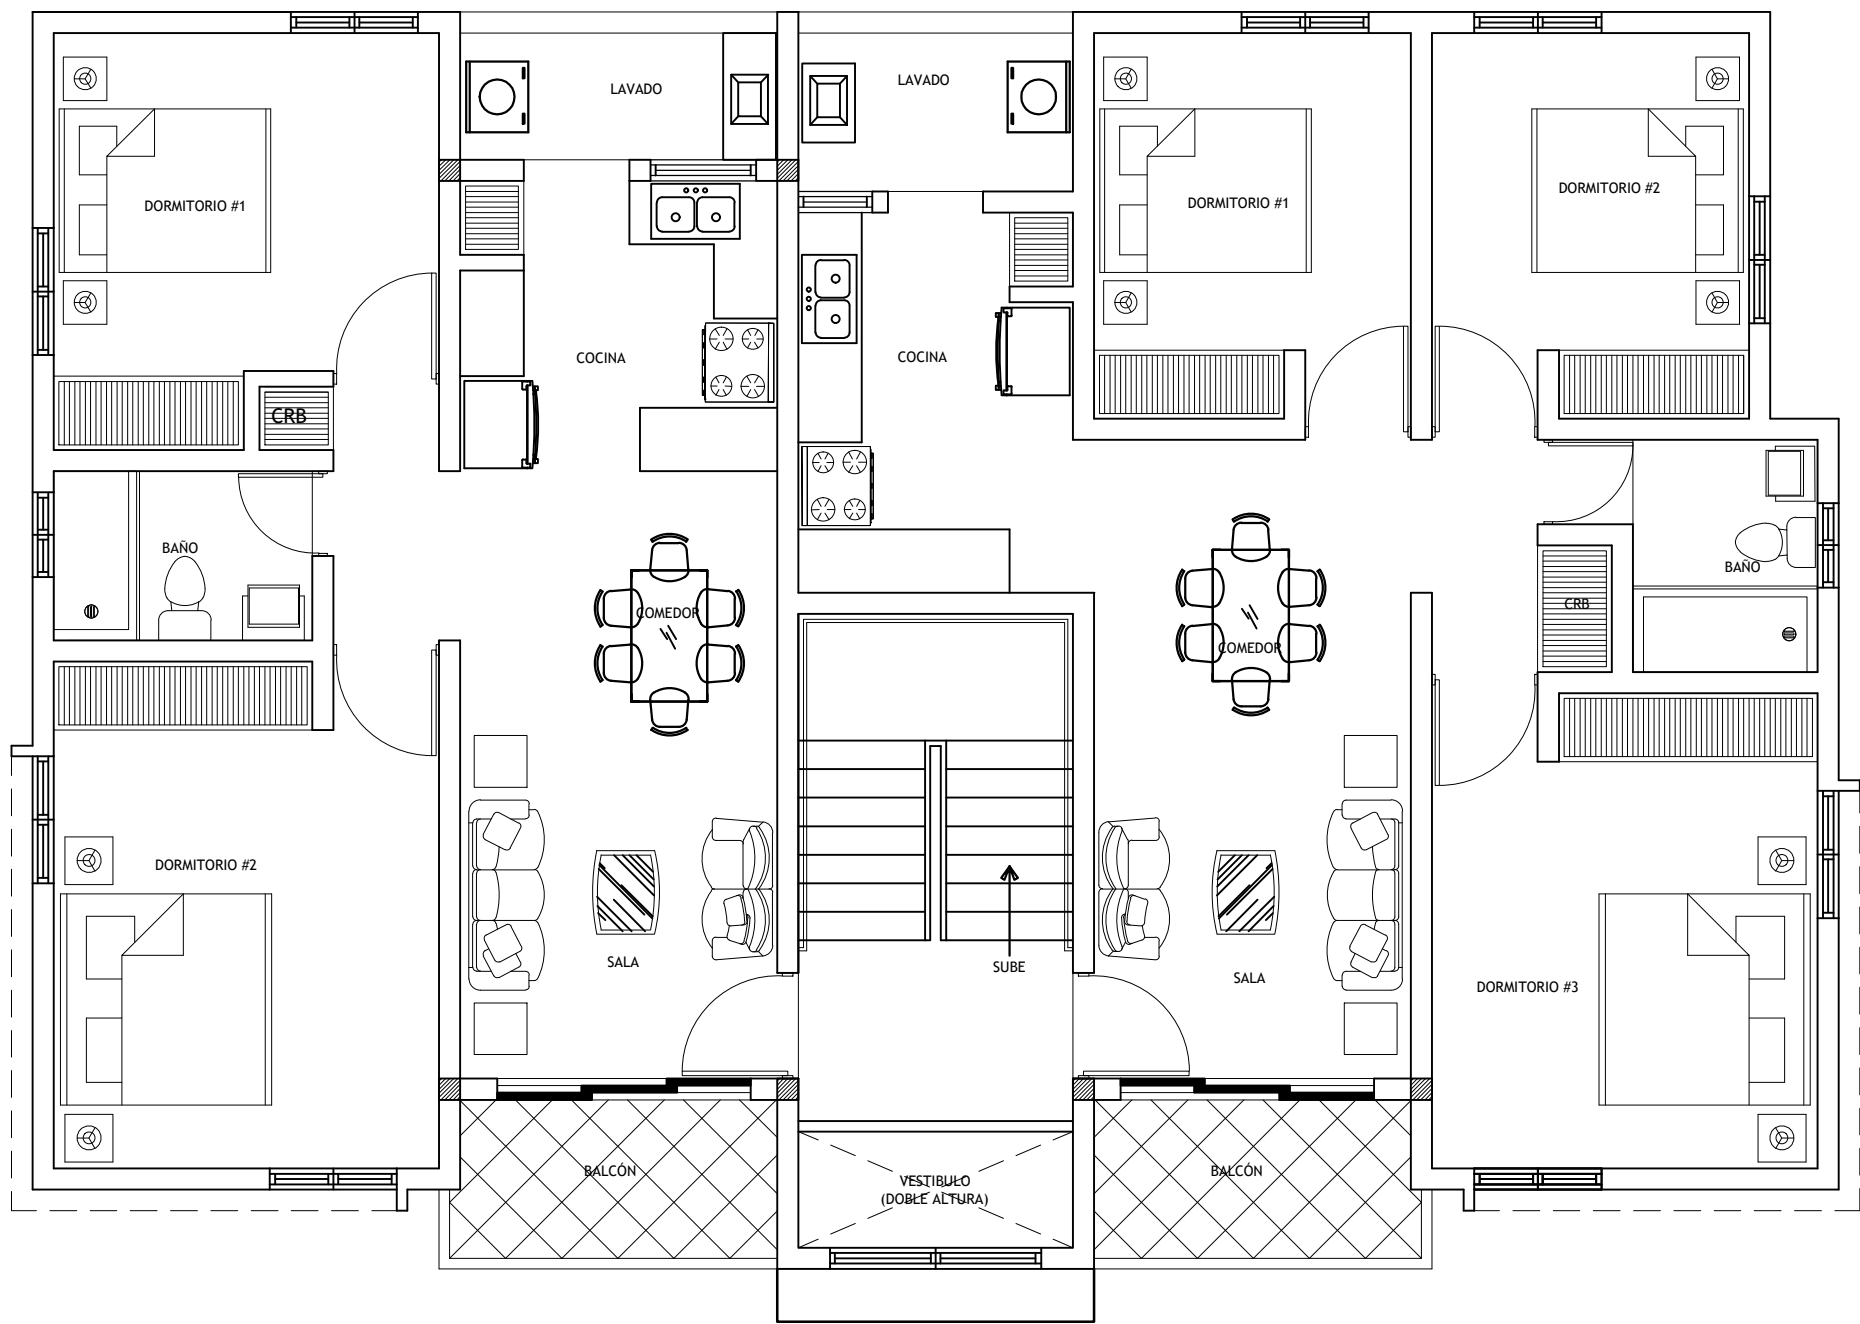


PLANTA ARQUITECTONICA 2DO. NIVEL, BLOQUE A
ESCALA: 1:75

2
A04

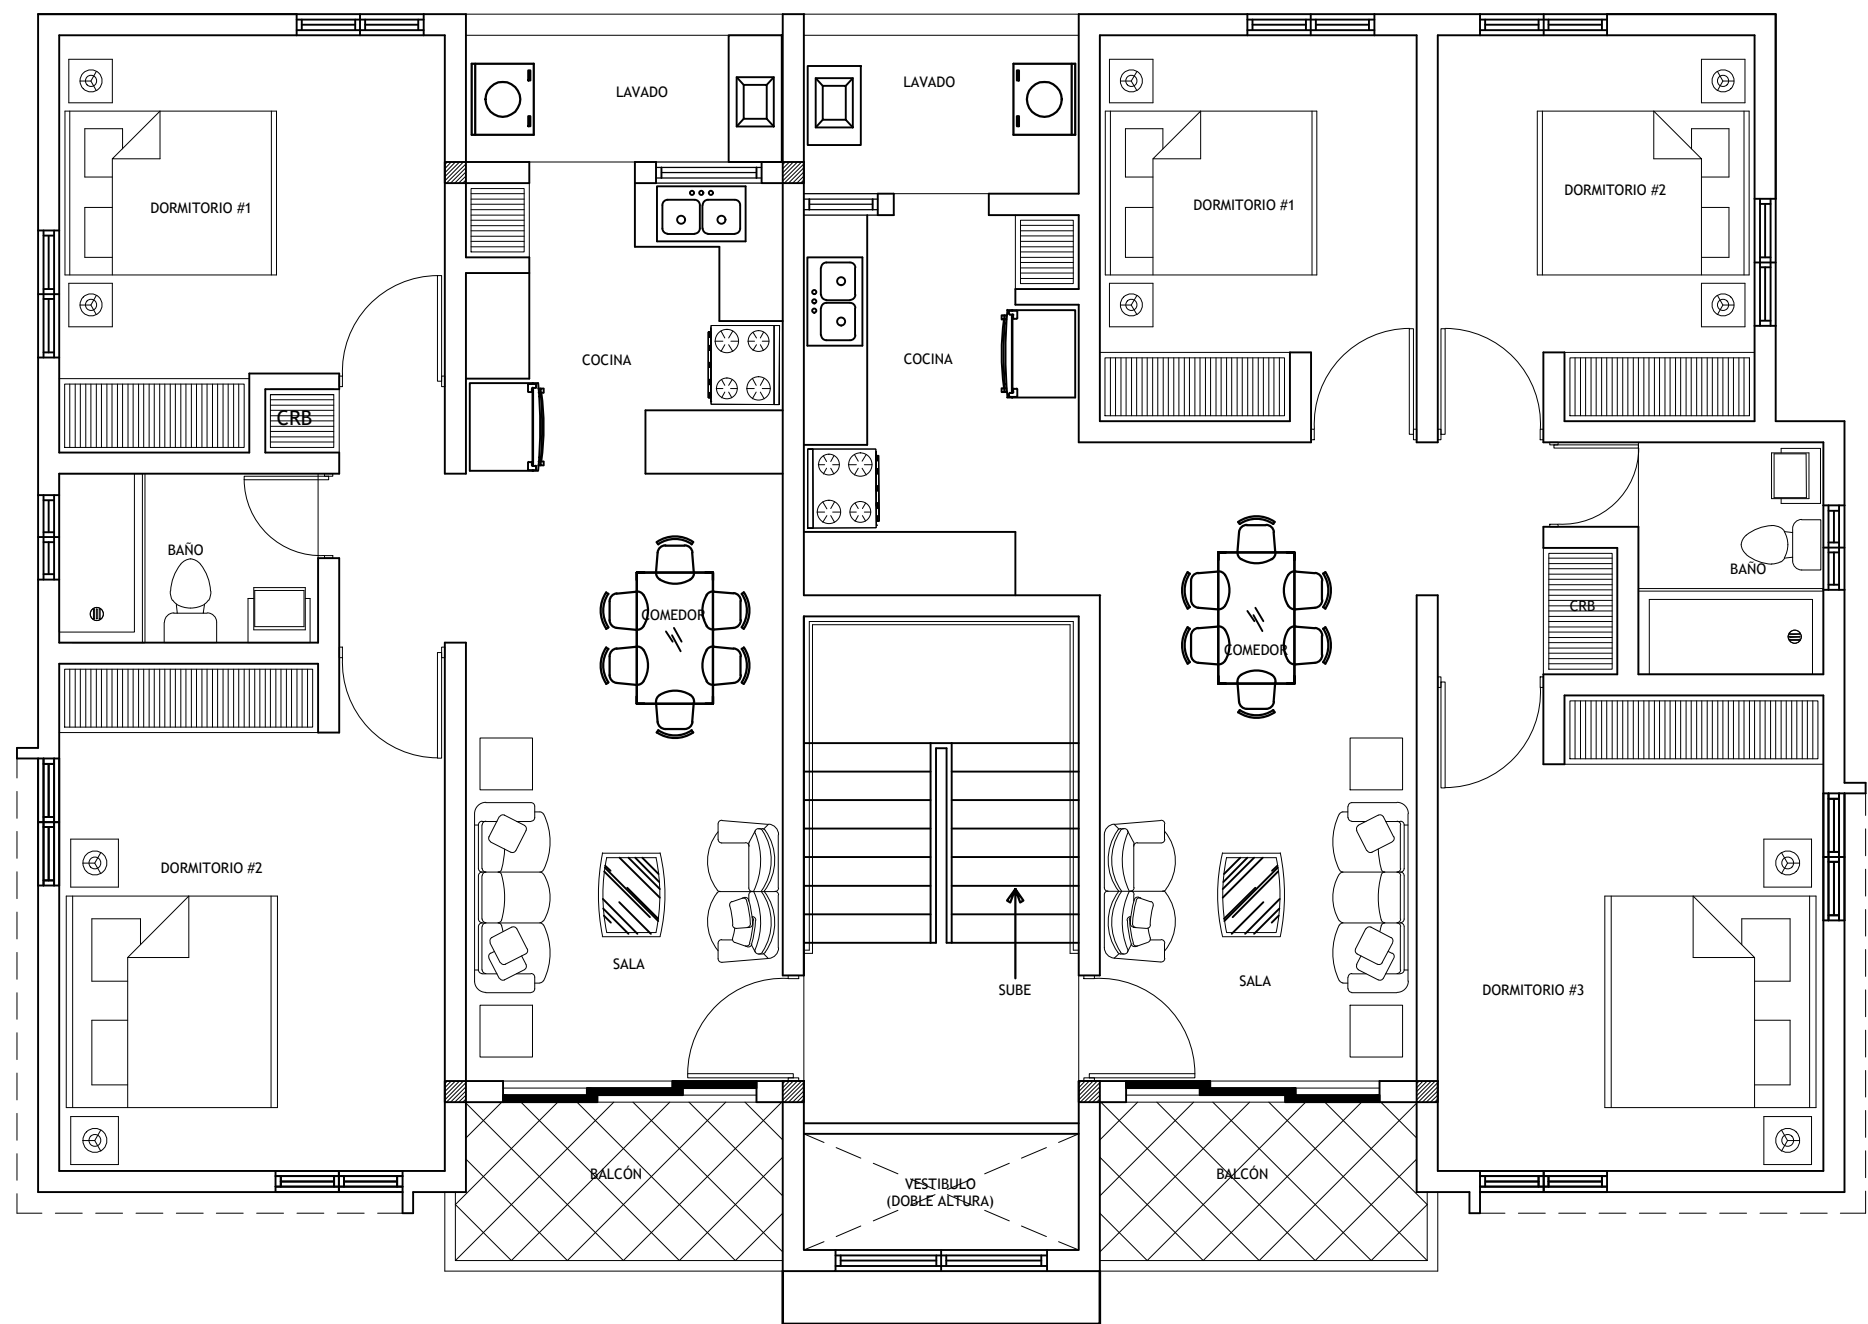

PLANTA ARQUITECTONICA 3ER. NIVEL, BLOQUE A
ESCALA: 1:75

3
A04

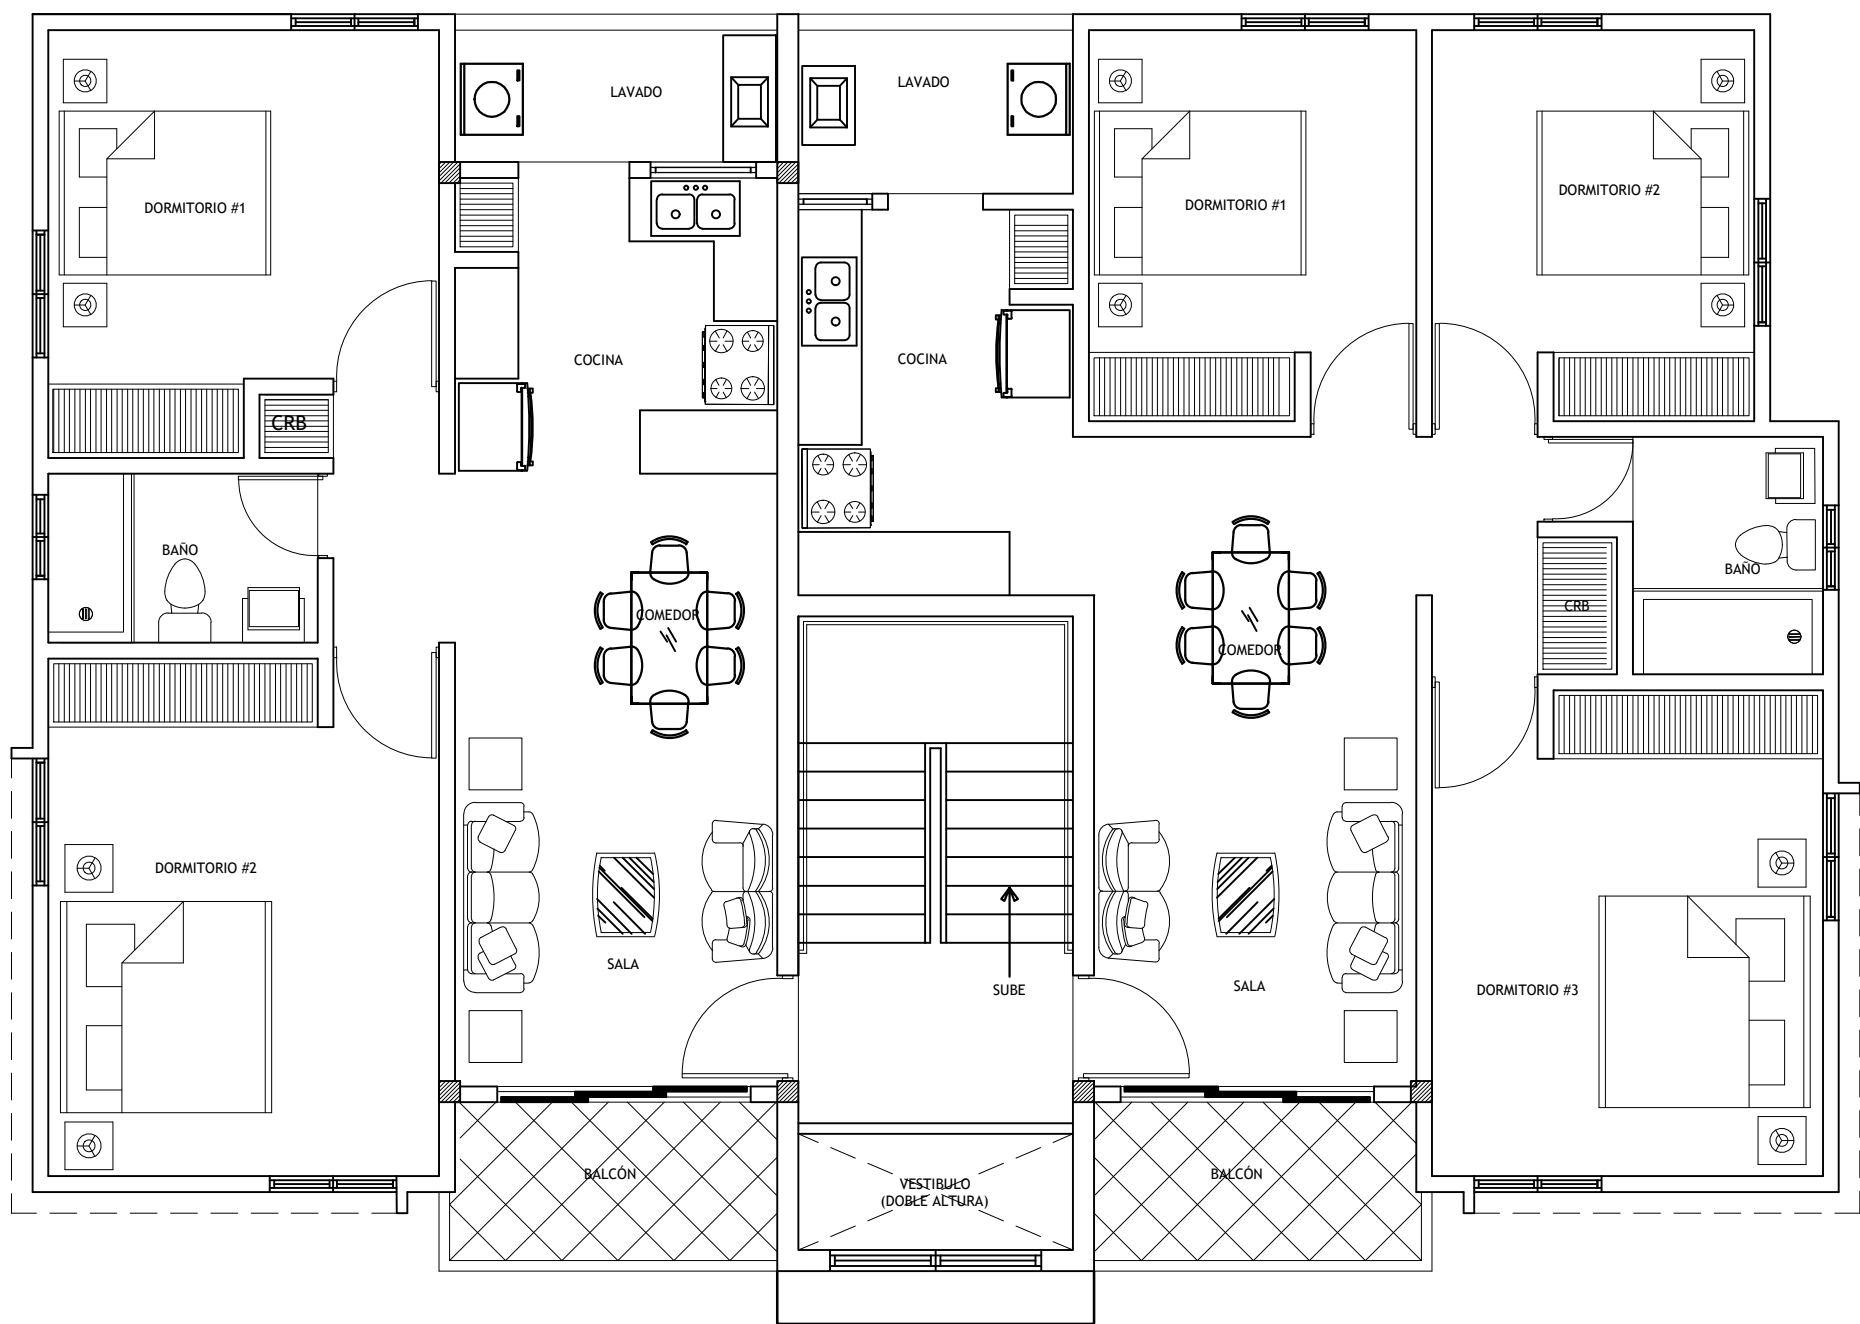

PLANTA ARQUITECTONICA 4TO. NIVEL, BLOQUE A
ESCALA: 1:75

4
A04



diazmelo & asocs.
ARQUITECTOS
Presidente Billini # 12, Bani, R.D. 522-4989
E-mail: diazmelo@hotmail.com

COLABORACION:



ARQUITECTURA DIGITAL
DISEÑOS-CONSTRUCCION-DIGITACION
COMPROMETIDOS CON SU TIEMPO
C/JUAN SANCHEZ RAMIREZ #56,
LOCAL 5 ZONA UASD TEL:221-5400

PROPIETARIO :
**GRUPO EMPRESARIAL
BANILEJO S.R.L.
GEBSA**

PROYECTISTAS:

DISEÑO ARQUITECTONICO:
DIAZMELO & ASOCS.
Arq. ISMAEL DIAZ MELO
Codia: 9604

DISEÑO SANITARIO:
Arq. HAMLET TEJEDA
Codia: 18303

DISEÑO ESTRUCTURAL:
ING. ODELIN TEJEDA
Codia: 23937

DISEÑO ELECTRICO:
ING. VILLYS SANCHEZ
Codia: 19060

CONTENIDO:
**PLANTAS ARQUITECTONICAS
BLOQUE A**

PROYECTO:
RESIDENCIAL GEBSA IV

Fecha: MAYO/2018

UBICACION:
BANI, PROV. PERAVIA

Ref.: Acad 2000
Escala: INDICADA

NOTAS:
TODAS LAS TERMINACIONES Y/O CAMBIOS EN EL SET. DE DOCUMENTOS CONSTRUCTIVOS DEBERAN SER APROBADOS POR EL SUPERVISOR PREVIAMENTE A SU APLICACION EN LA OBRA.
TODAS LAS MEDIDAS DE MUEBLES Y DE SUPERFICIE A SER REVESTIDAS SERAN RECTIFICADAS PREVIA FABRICACION DE LOS CIERRES O LA O LA INSTALACION DE LOS RECURRIMIENTOS
LAS TERMINACIONES Y/O DETALLES NO ESPECIFICADOS SERAN DEFINIDOS ENTRE:
EL DUEÑO Y EL AUTOR DEL PROYECTO.
EL CONTRATISTA NO PODRA TOMAR DECISIONES INCONSULTAS RESPECTO A LAS VARIACIONES EN EL CONTENIDO DE ESTE DOCUMENTO

LOS PLANOS ARQUITECTONICOS MANDARAN RESPECTO A LOS DEMAS A DIFERENCIA PRIMARA LA INFORMACIONCONTENIDA EN LOS MISMOS



diazmelo & asocs.
ARQUITECTOS

Presidente Bilini # 12, Bani, R.D. 522-4989
E-mail: diazmelo@hotmail.com

COLABORACION:



ARQUITECTURA DIGITAL
DISEÑOS-CONSTRUCCION-DIGITACION
COMPROMETIDOS CON SU TIEMPO
CIJUAN SANCHEZ RAMIREZ #56,
LOCAL 5 ZONA UASD TEL:221-5400

PROPIETARIO :
**GRUPO EMPRESARIAL
BANILEJO S.R.L.
GEBSA**

PROYECTISTAS:

DISEÑO ARQUITECTONICO:
DIAZMELO & ASOCS.
Arq. ISMAEL DIAZ MELO
Codia: 9604

DISEÑO SANITARIO:
Arq. HAMLET TEJEDA
Codia: 18303

DISEÑO ESTRUCTURAL:
ING. ODELIN TEJEDA
Codia: 23937

DISEÑO ELECTRICO:
ING. VILLYS SANCHEZ
Codia: 19060

CONTENIDO:
**PLANTAS DIMENSIONADAS
BLOQUE A**

PROYECTO:
RESIDENCIAL GEBSA IV

Fecha: MAYO/2018

UBICACION:

BANI, PROV. PERAVIA

Ref.: Acad 2000

Escala: INDICADA

Hoja No.


NOTAS:
TODAS LAS TERMINACIONES Y/O CAMBIOS EN EL SET. DE DOCUMENTOS CONSTRUCTIVOS DEBERAN SER APROBADOS POR EL SUPERVISOR PREVIAMENTE.
A SU APLICACION EN LA OBRA.

TODAS LAS MEDIDAS DE MUROS Y DE SUPERFICIE A SER REVESTIDAS SERAN RECTIFICADAS PREVIA FABRICACION DE LOS CIERRES O LA O LA INSTALACION DE LOS RECURRIMIENTOS

LAS TERMINACIONES Y/O DETALLES NO ESPECIFICADOS SERAN DETERMINADOS ENTRE:


EL DUEÑO Y EL AUTOR DEL PROYECTO.
EL CONTRATISTA NO PODRA TOMAR DECISIONES INCONSULTAS RESPECTO A VARIACIONES EN EL CONTENIDO DE ESTE DOCUMENTO

LOS PLANOS ARQUITECTONICOS MANDARAN RESPECTO A LOS DEMAS A ANTE CUALQUIER
DIFERENCIA PRIMARA LA INFORMACIONCONTENIDA EN LOS MISOS

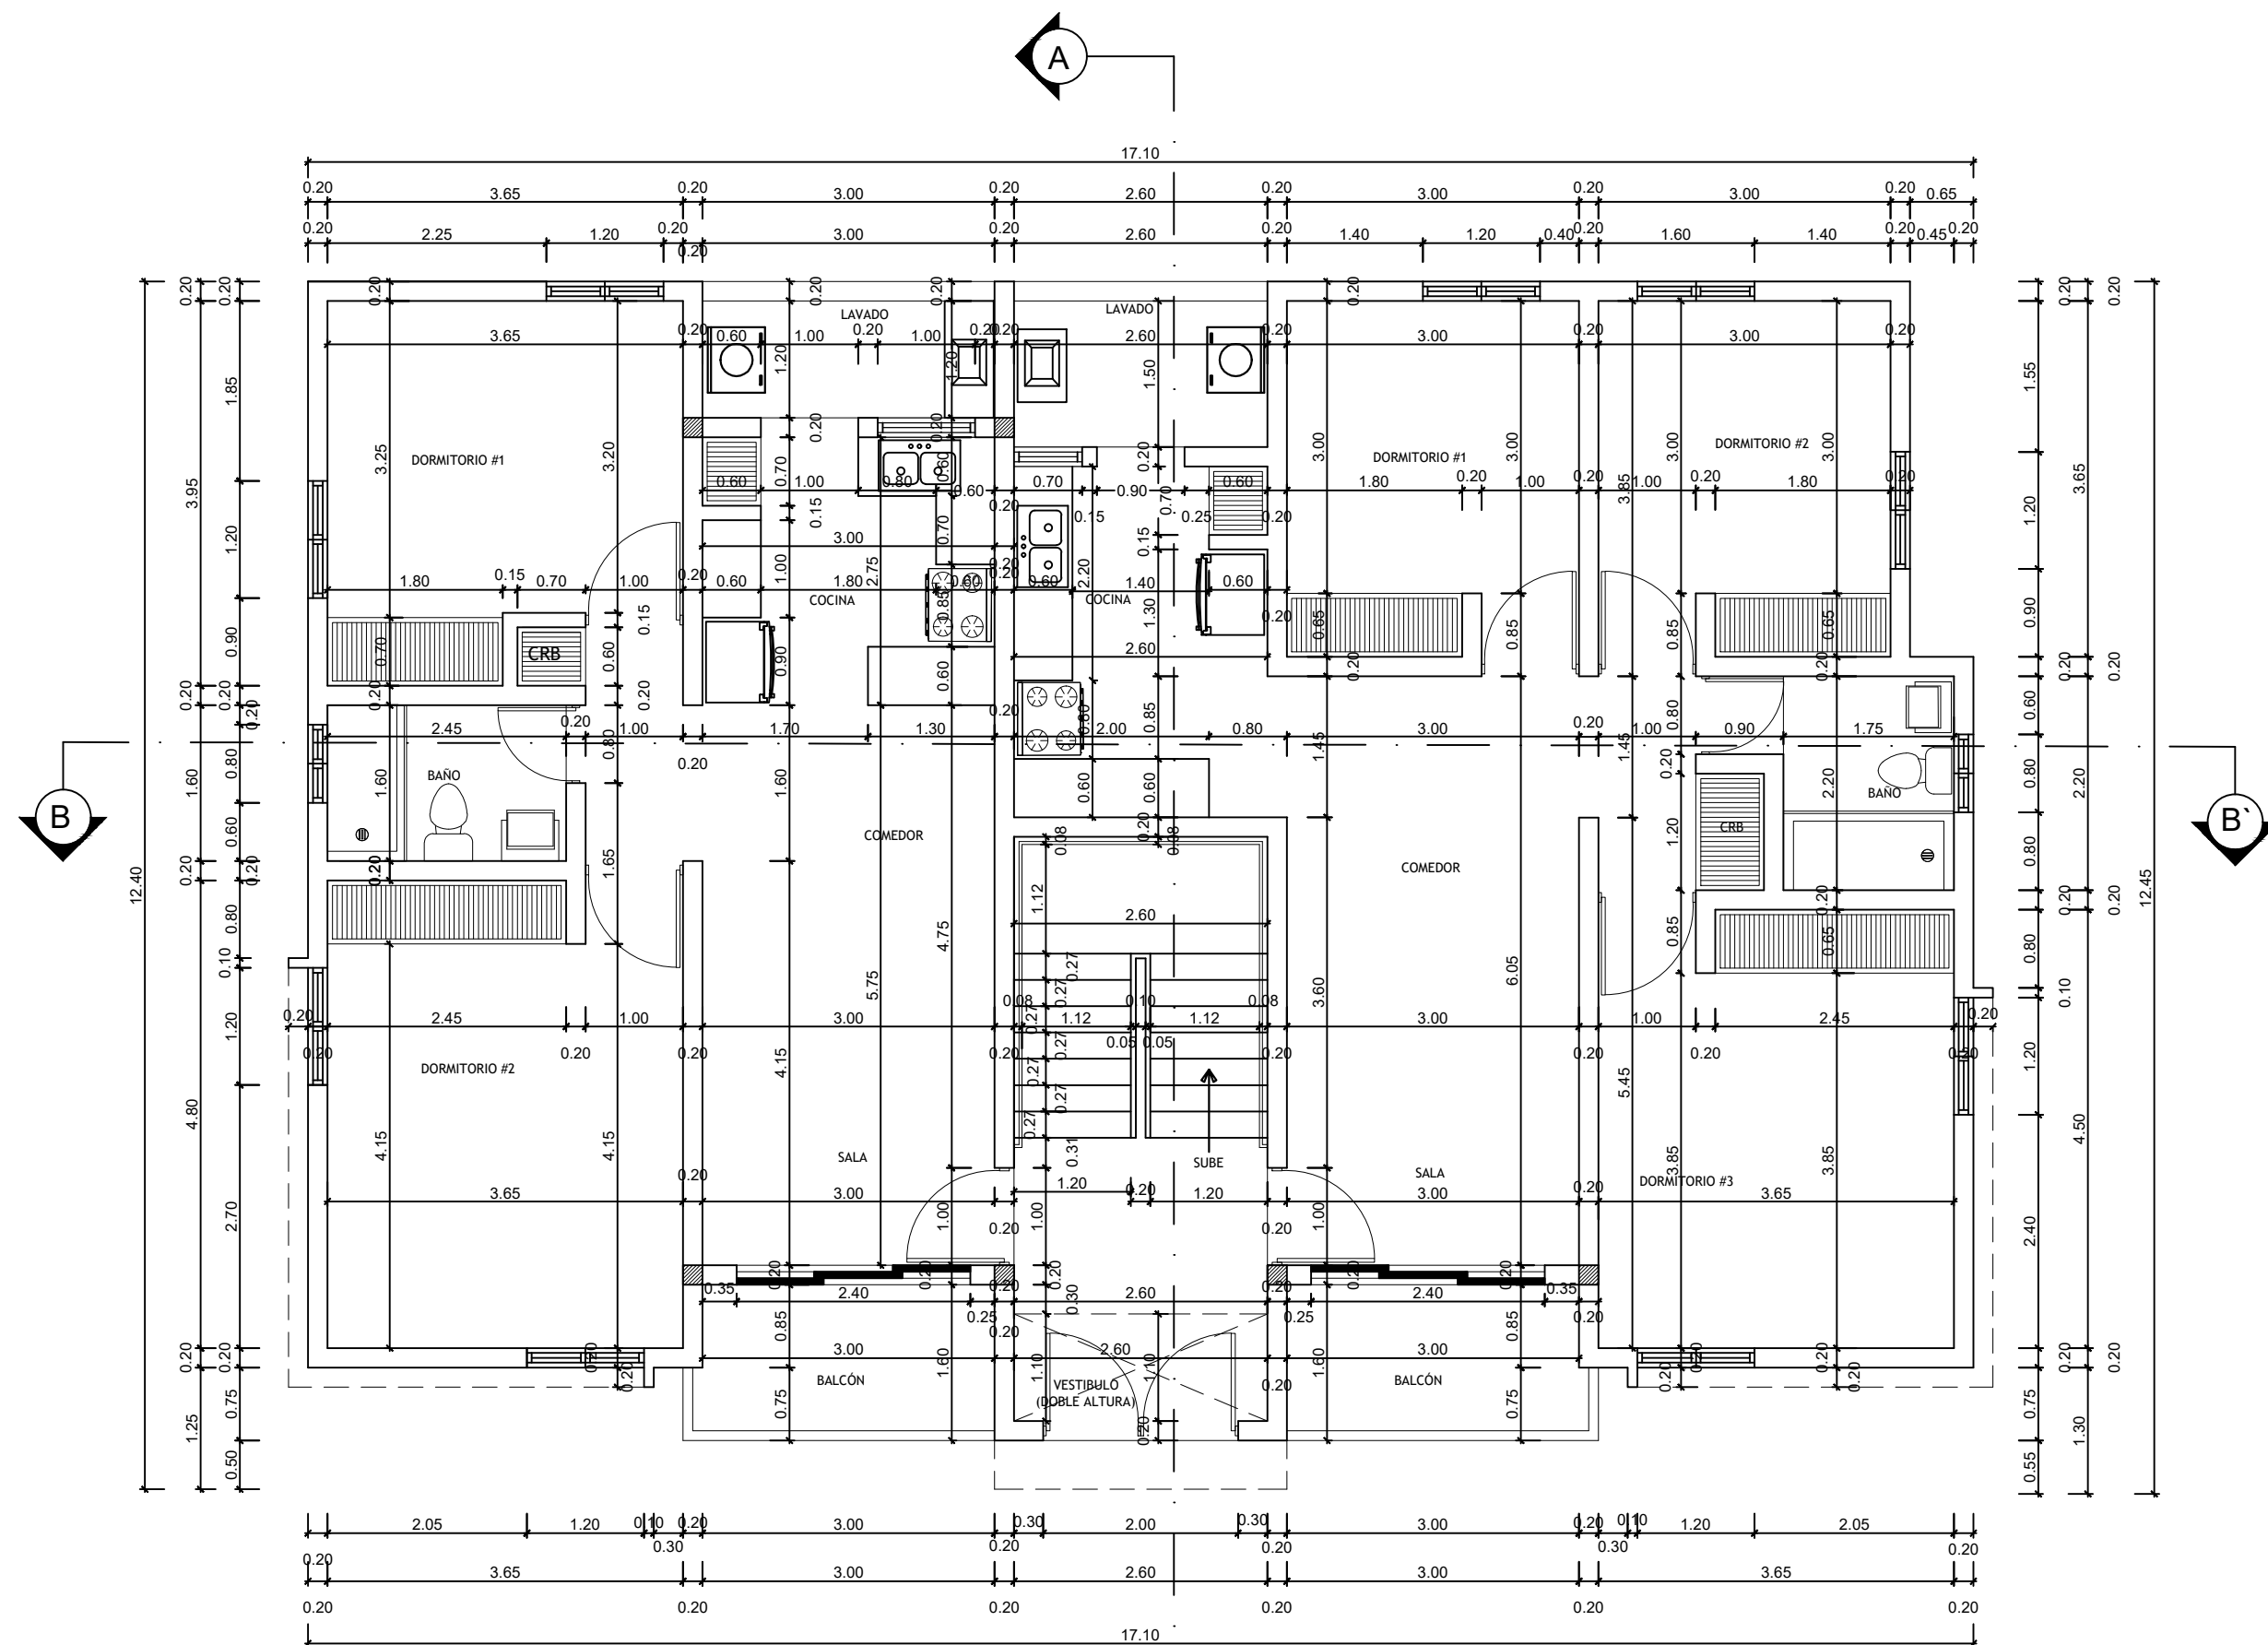


PLANTA DIMENSIONADA 1ER. NIVEL, BLOQUE A
ESCALA: 1:75

1
A05

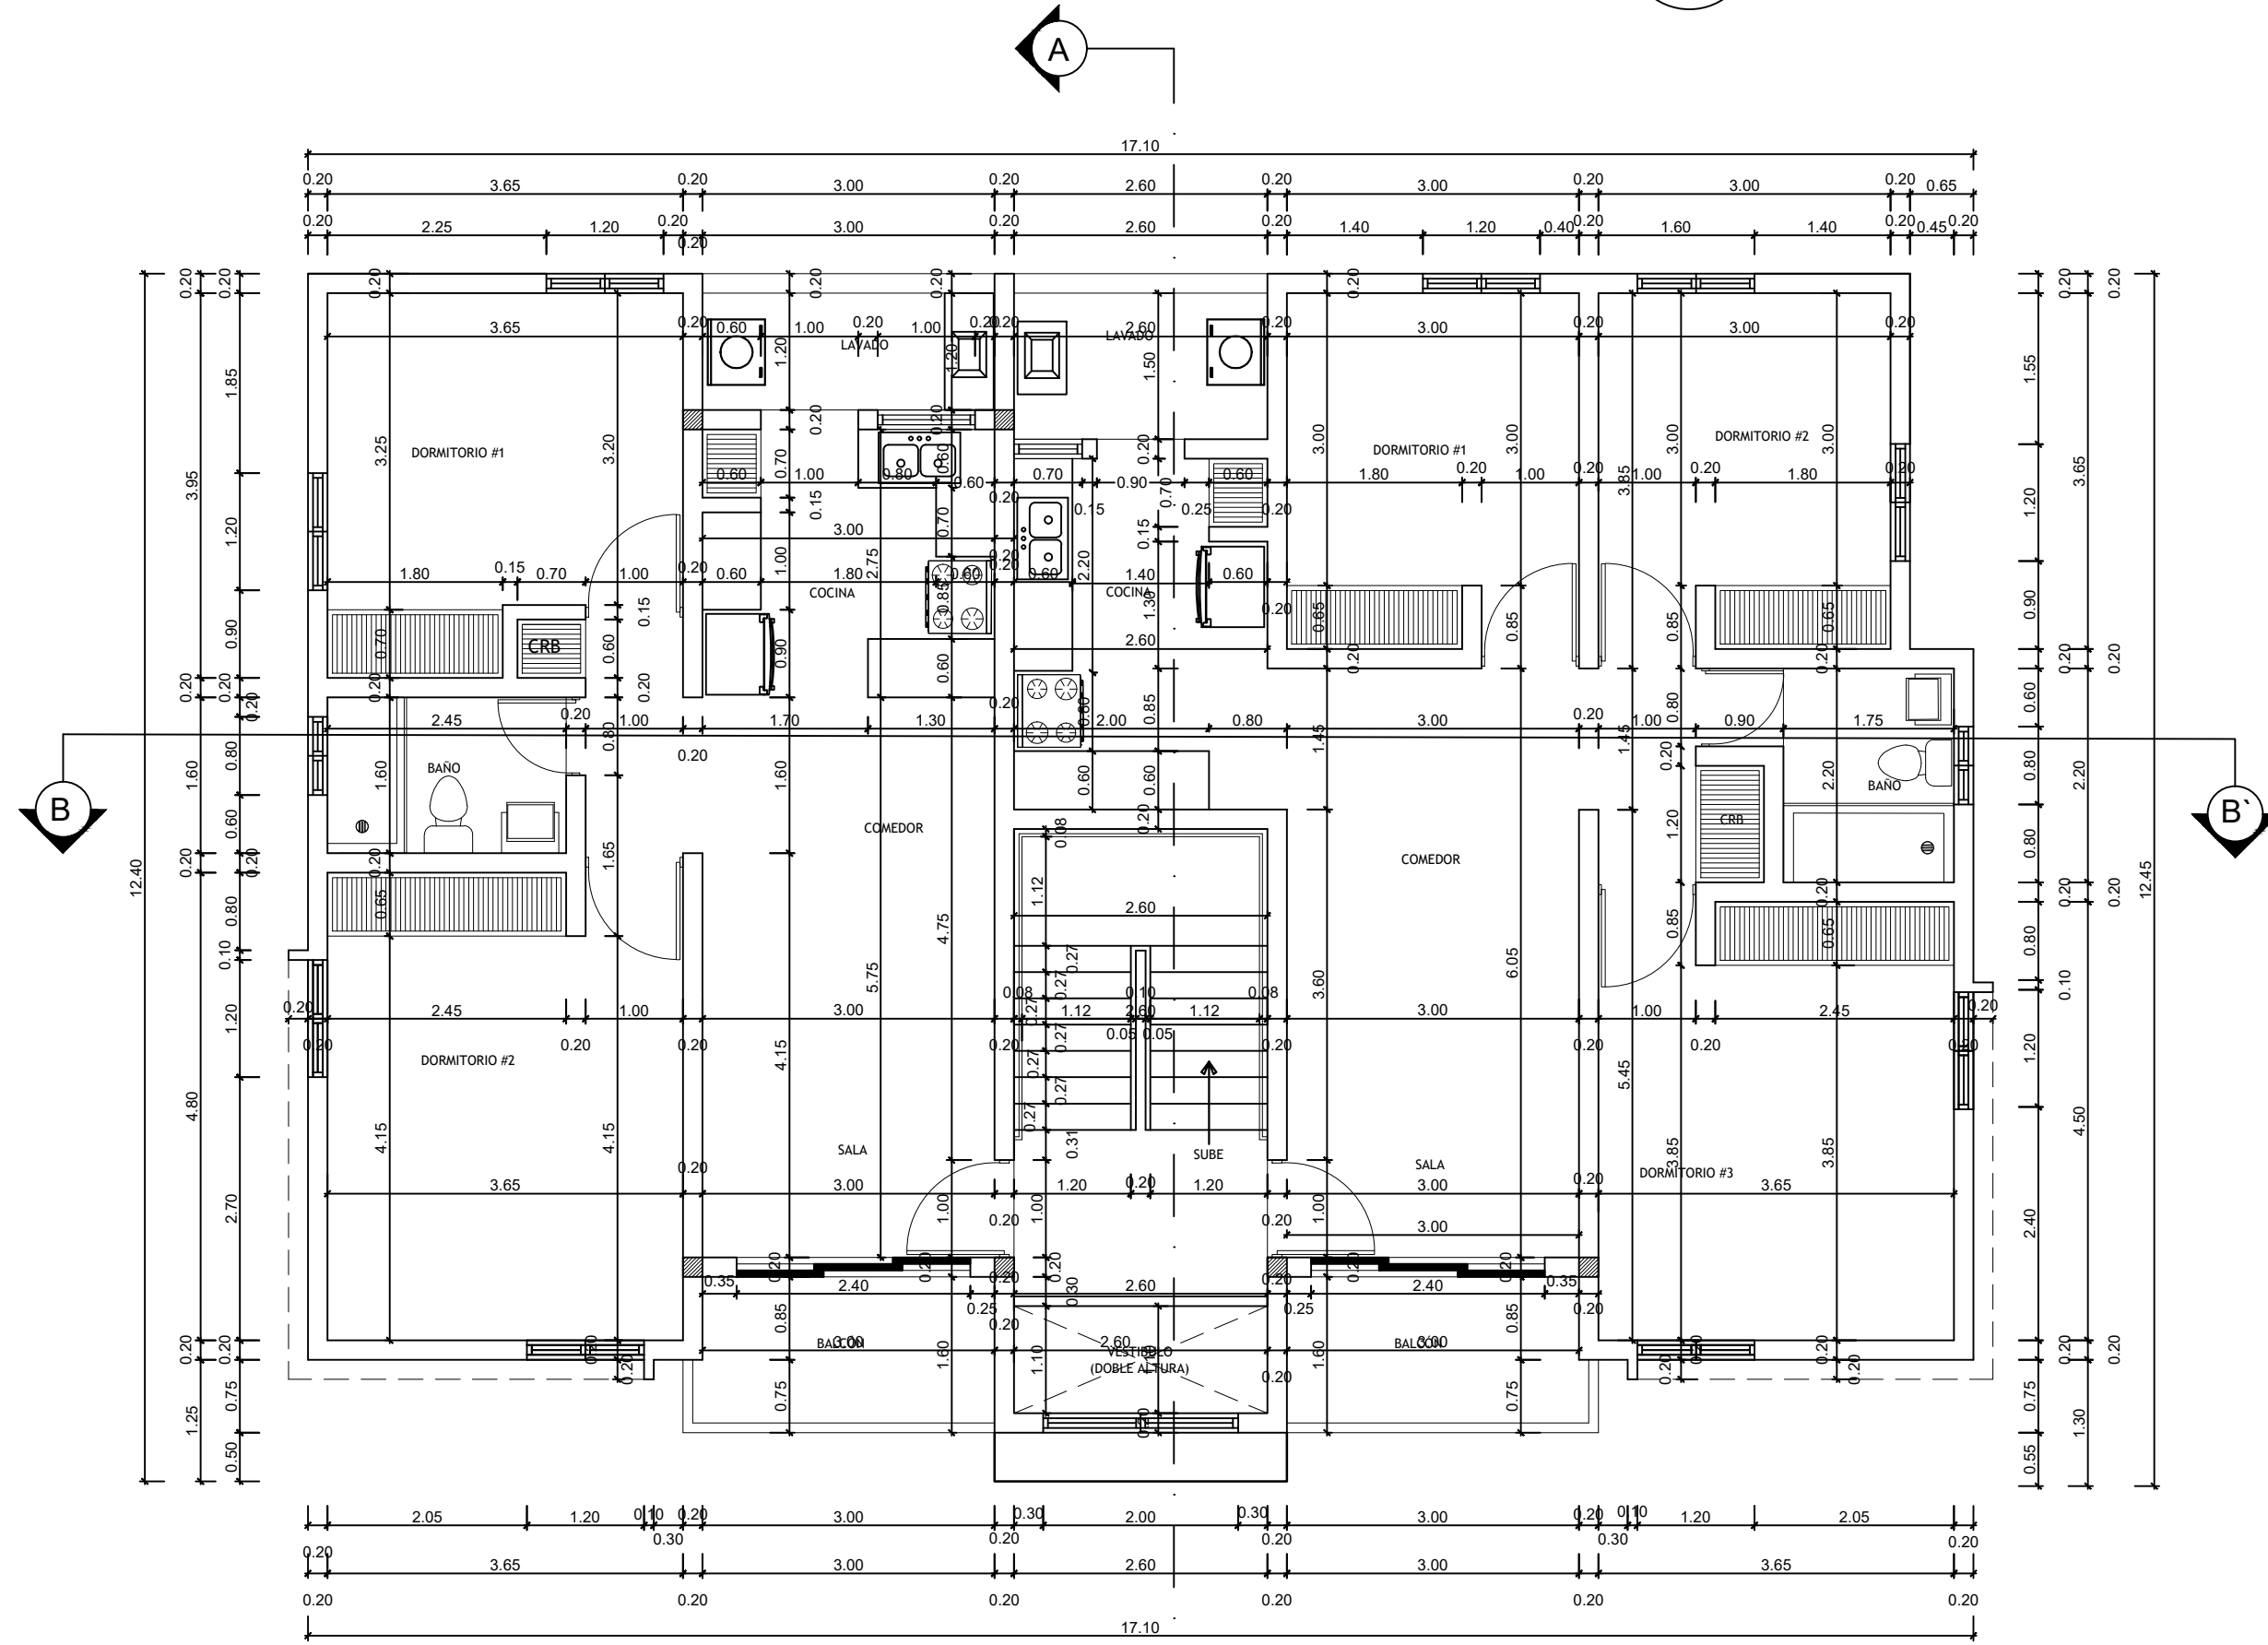


PLANTA DIMENSIONADA 3ER. NIVEL, BLOQUE A
ESCALA: 1:75

3
A05

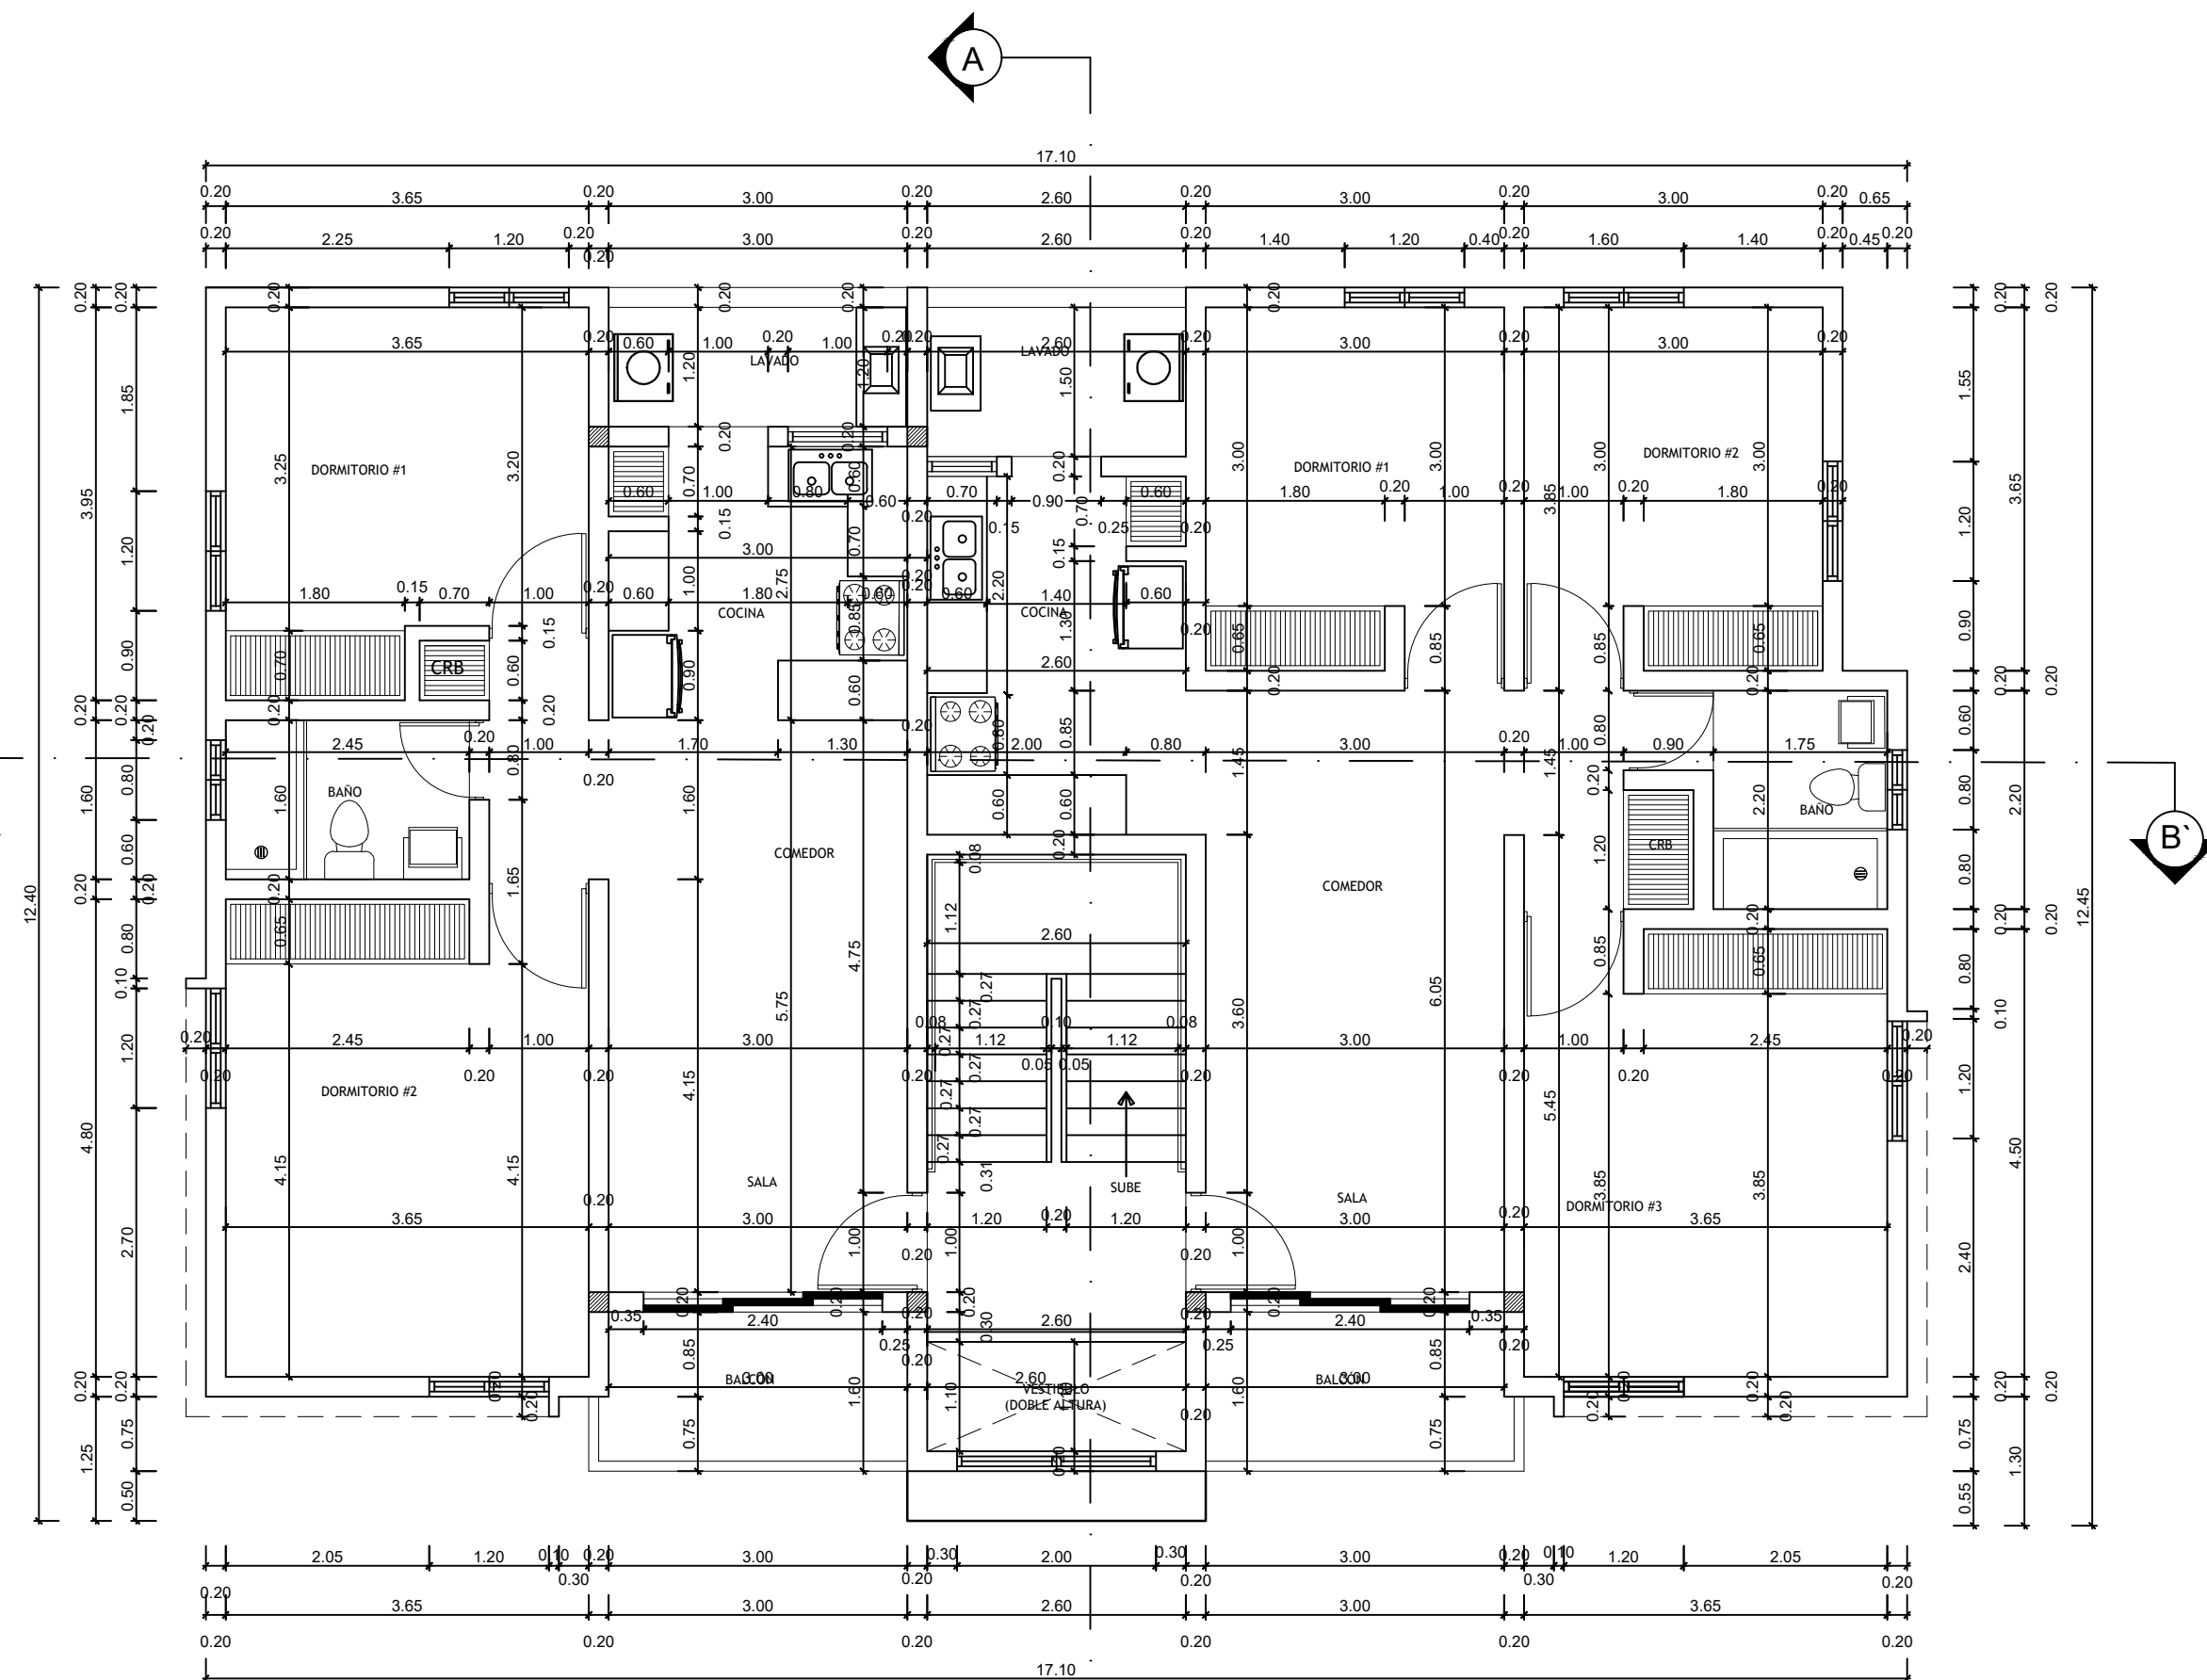

PLANTA DIMENSIONADA 2DO. NIVEL, BLOQUE A
ESCALA: 1:75

2
A05

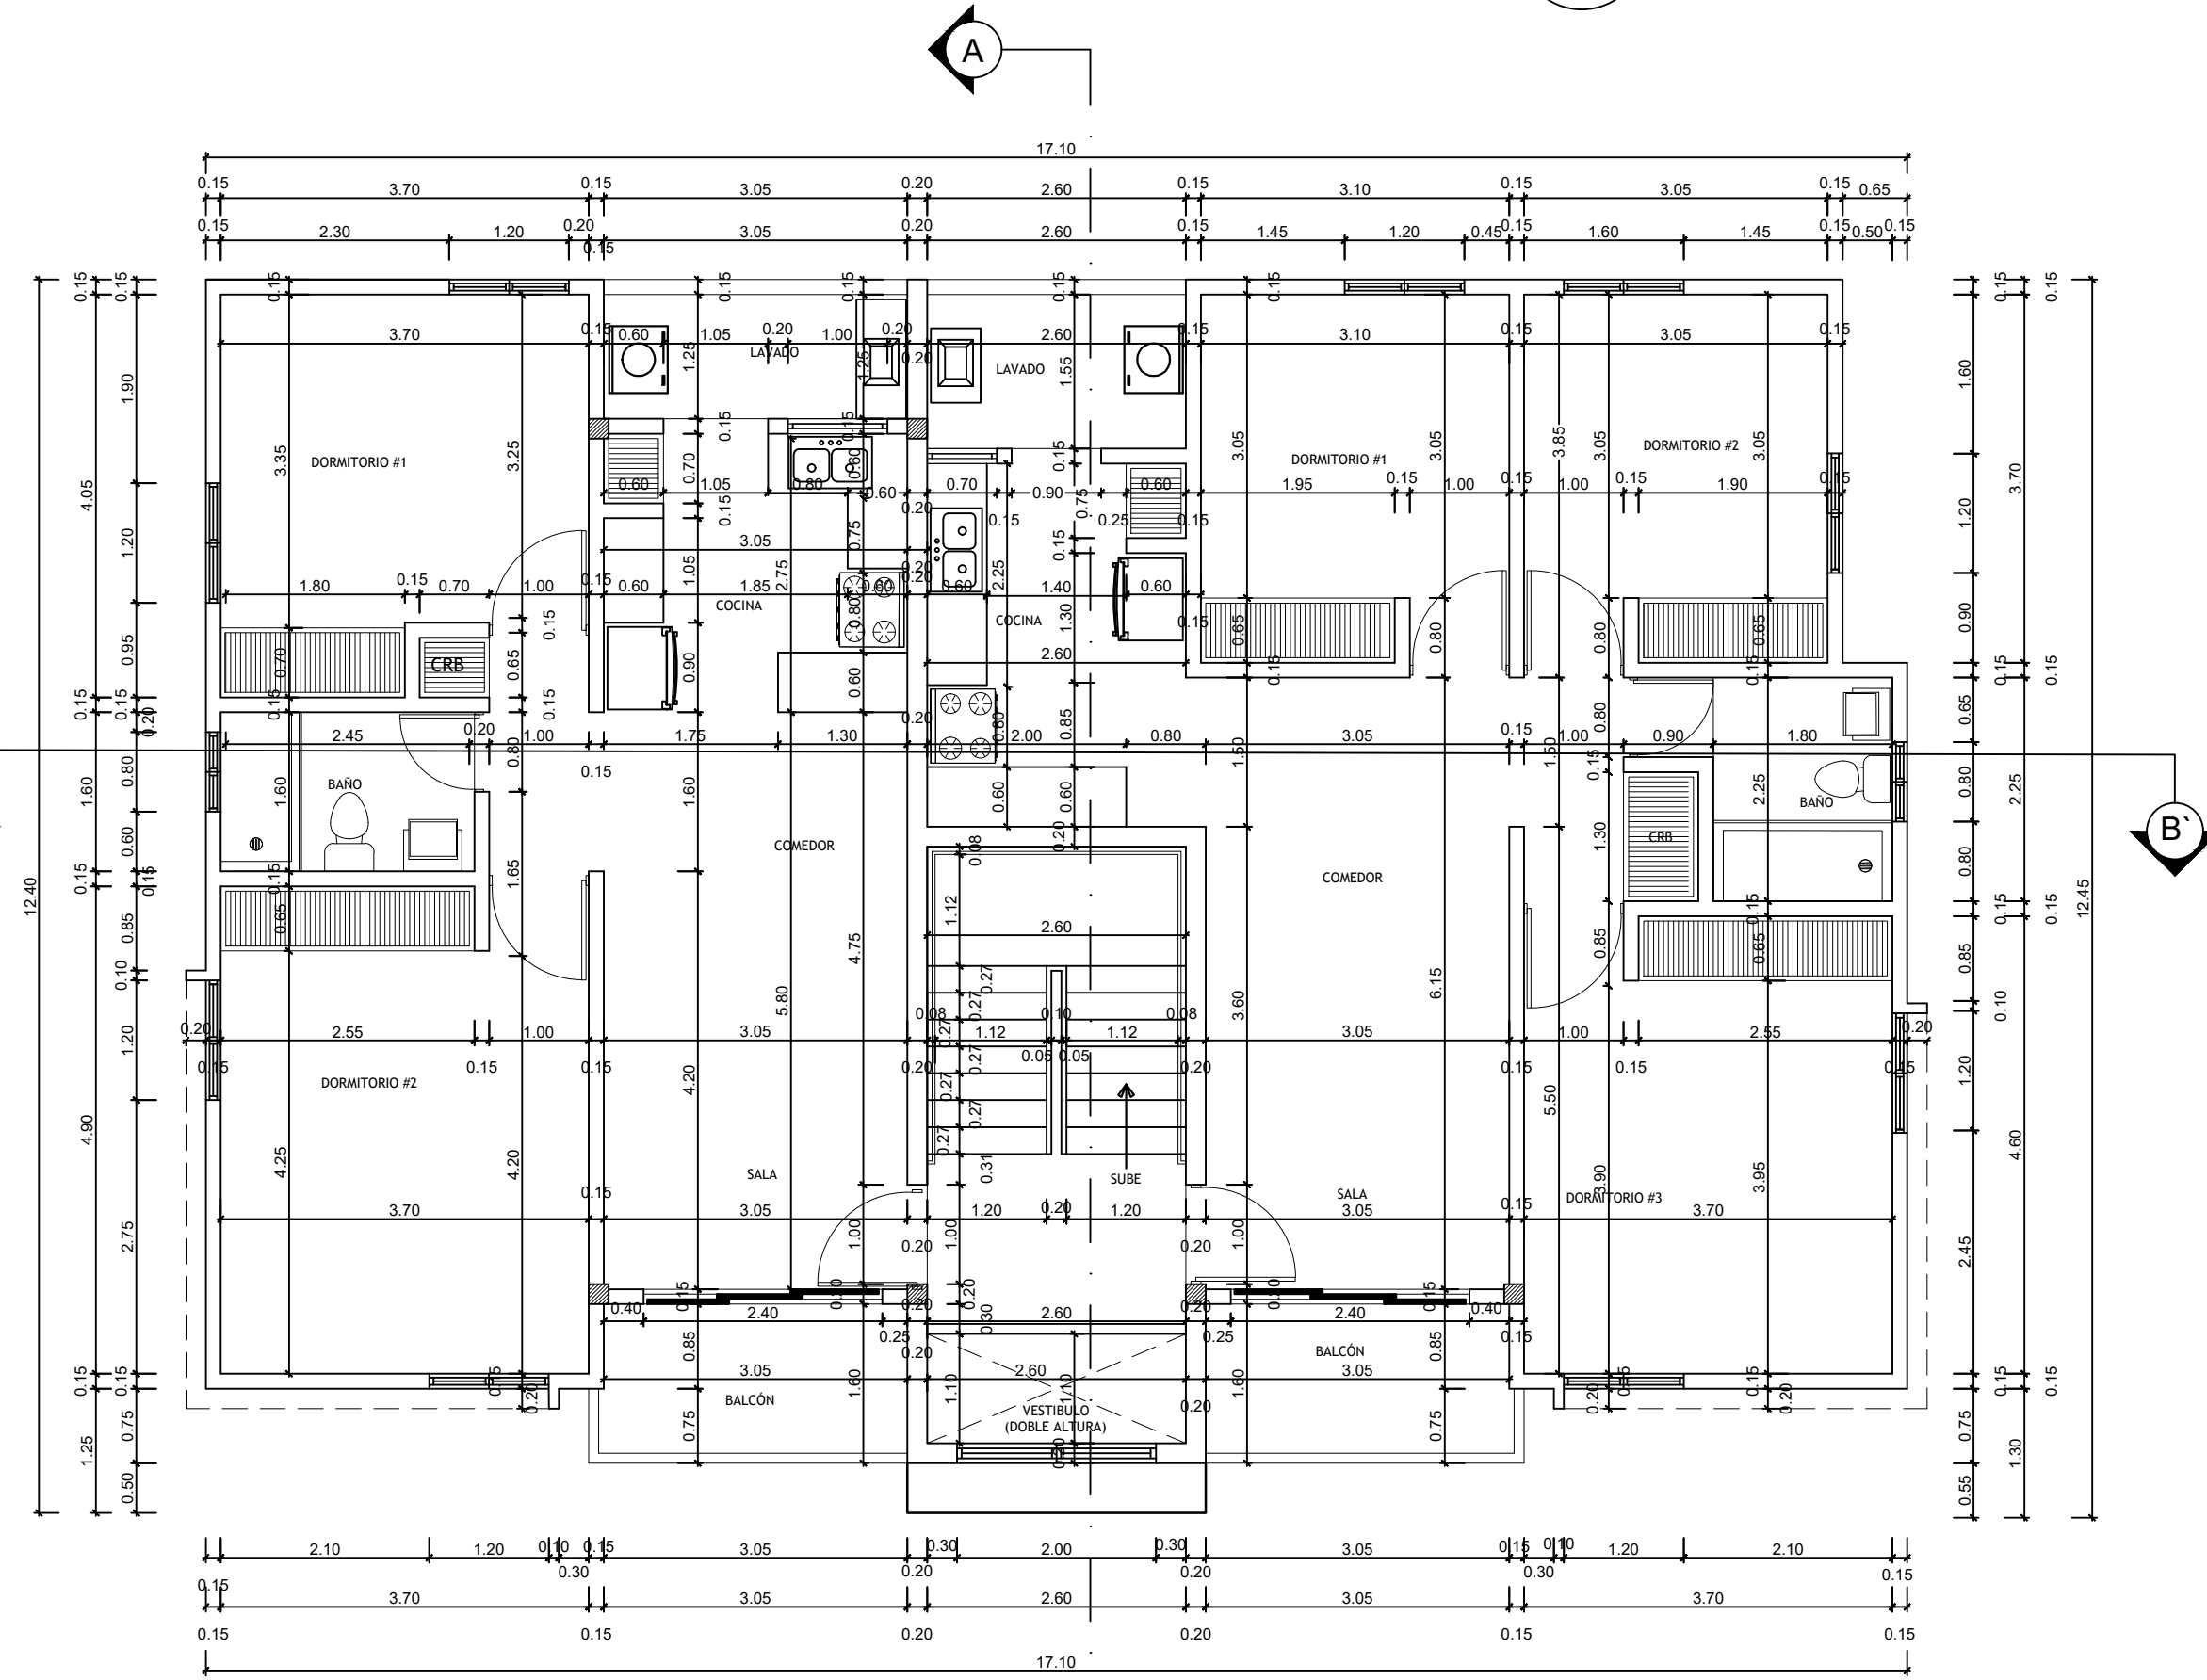


PLANTA DIMENSIONADA 4TO. NIVEL, BLOQUE A
ESCALA: 1:75

4
A05




ELEVACION FRONTAL, BLOQUE A
ESCALA: 1:75

1
A06

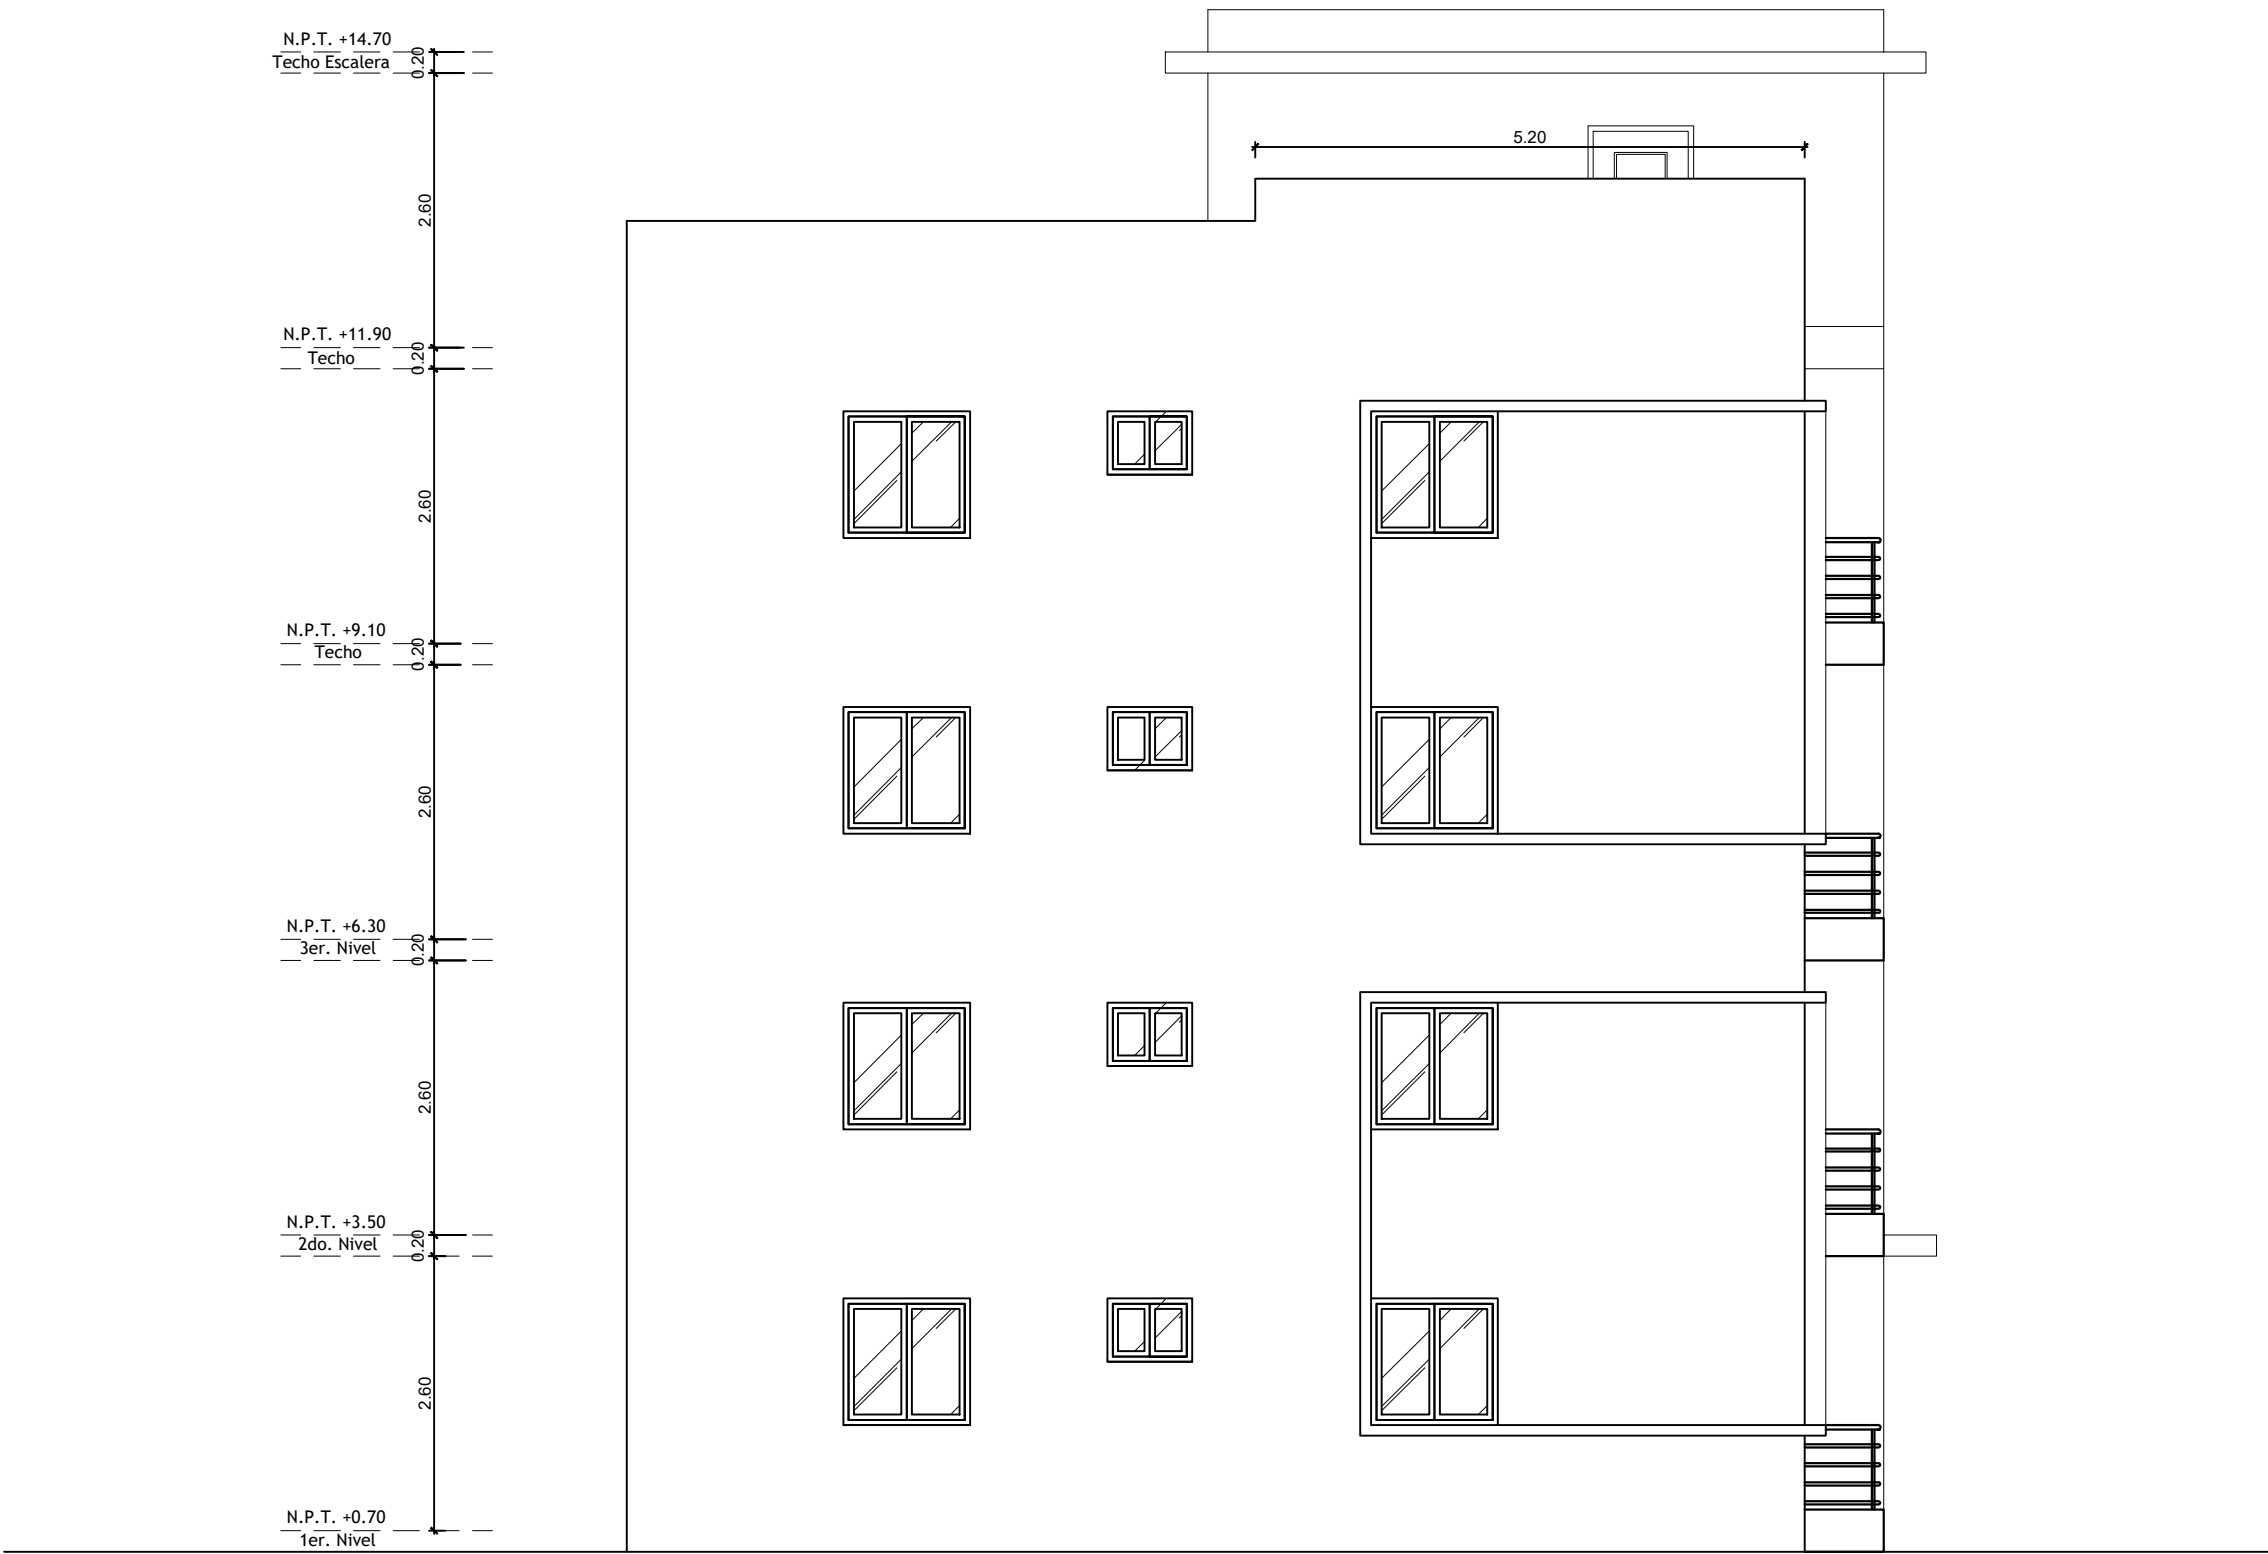


ELEVACION LATERAL IZQUIERDO, BLOQUE A
ESCALA: 1:75

2
A06

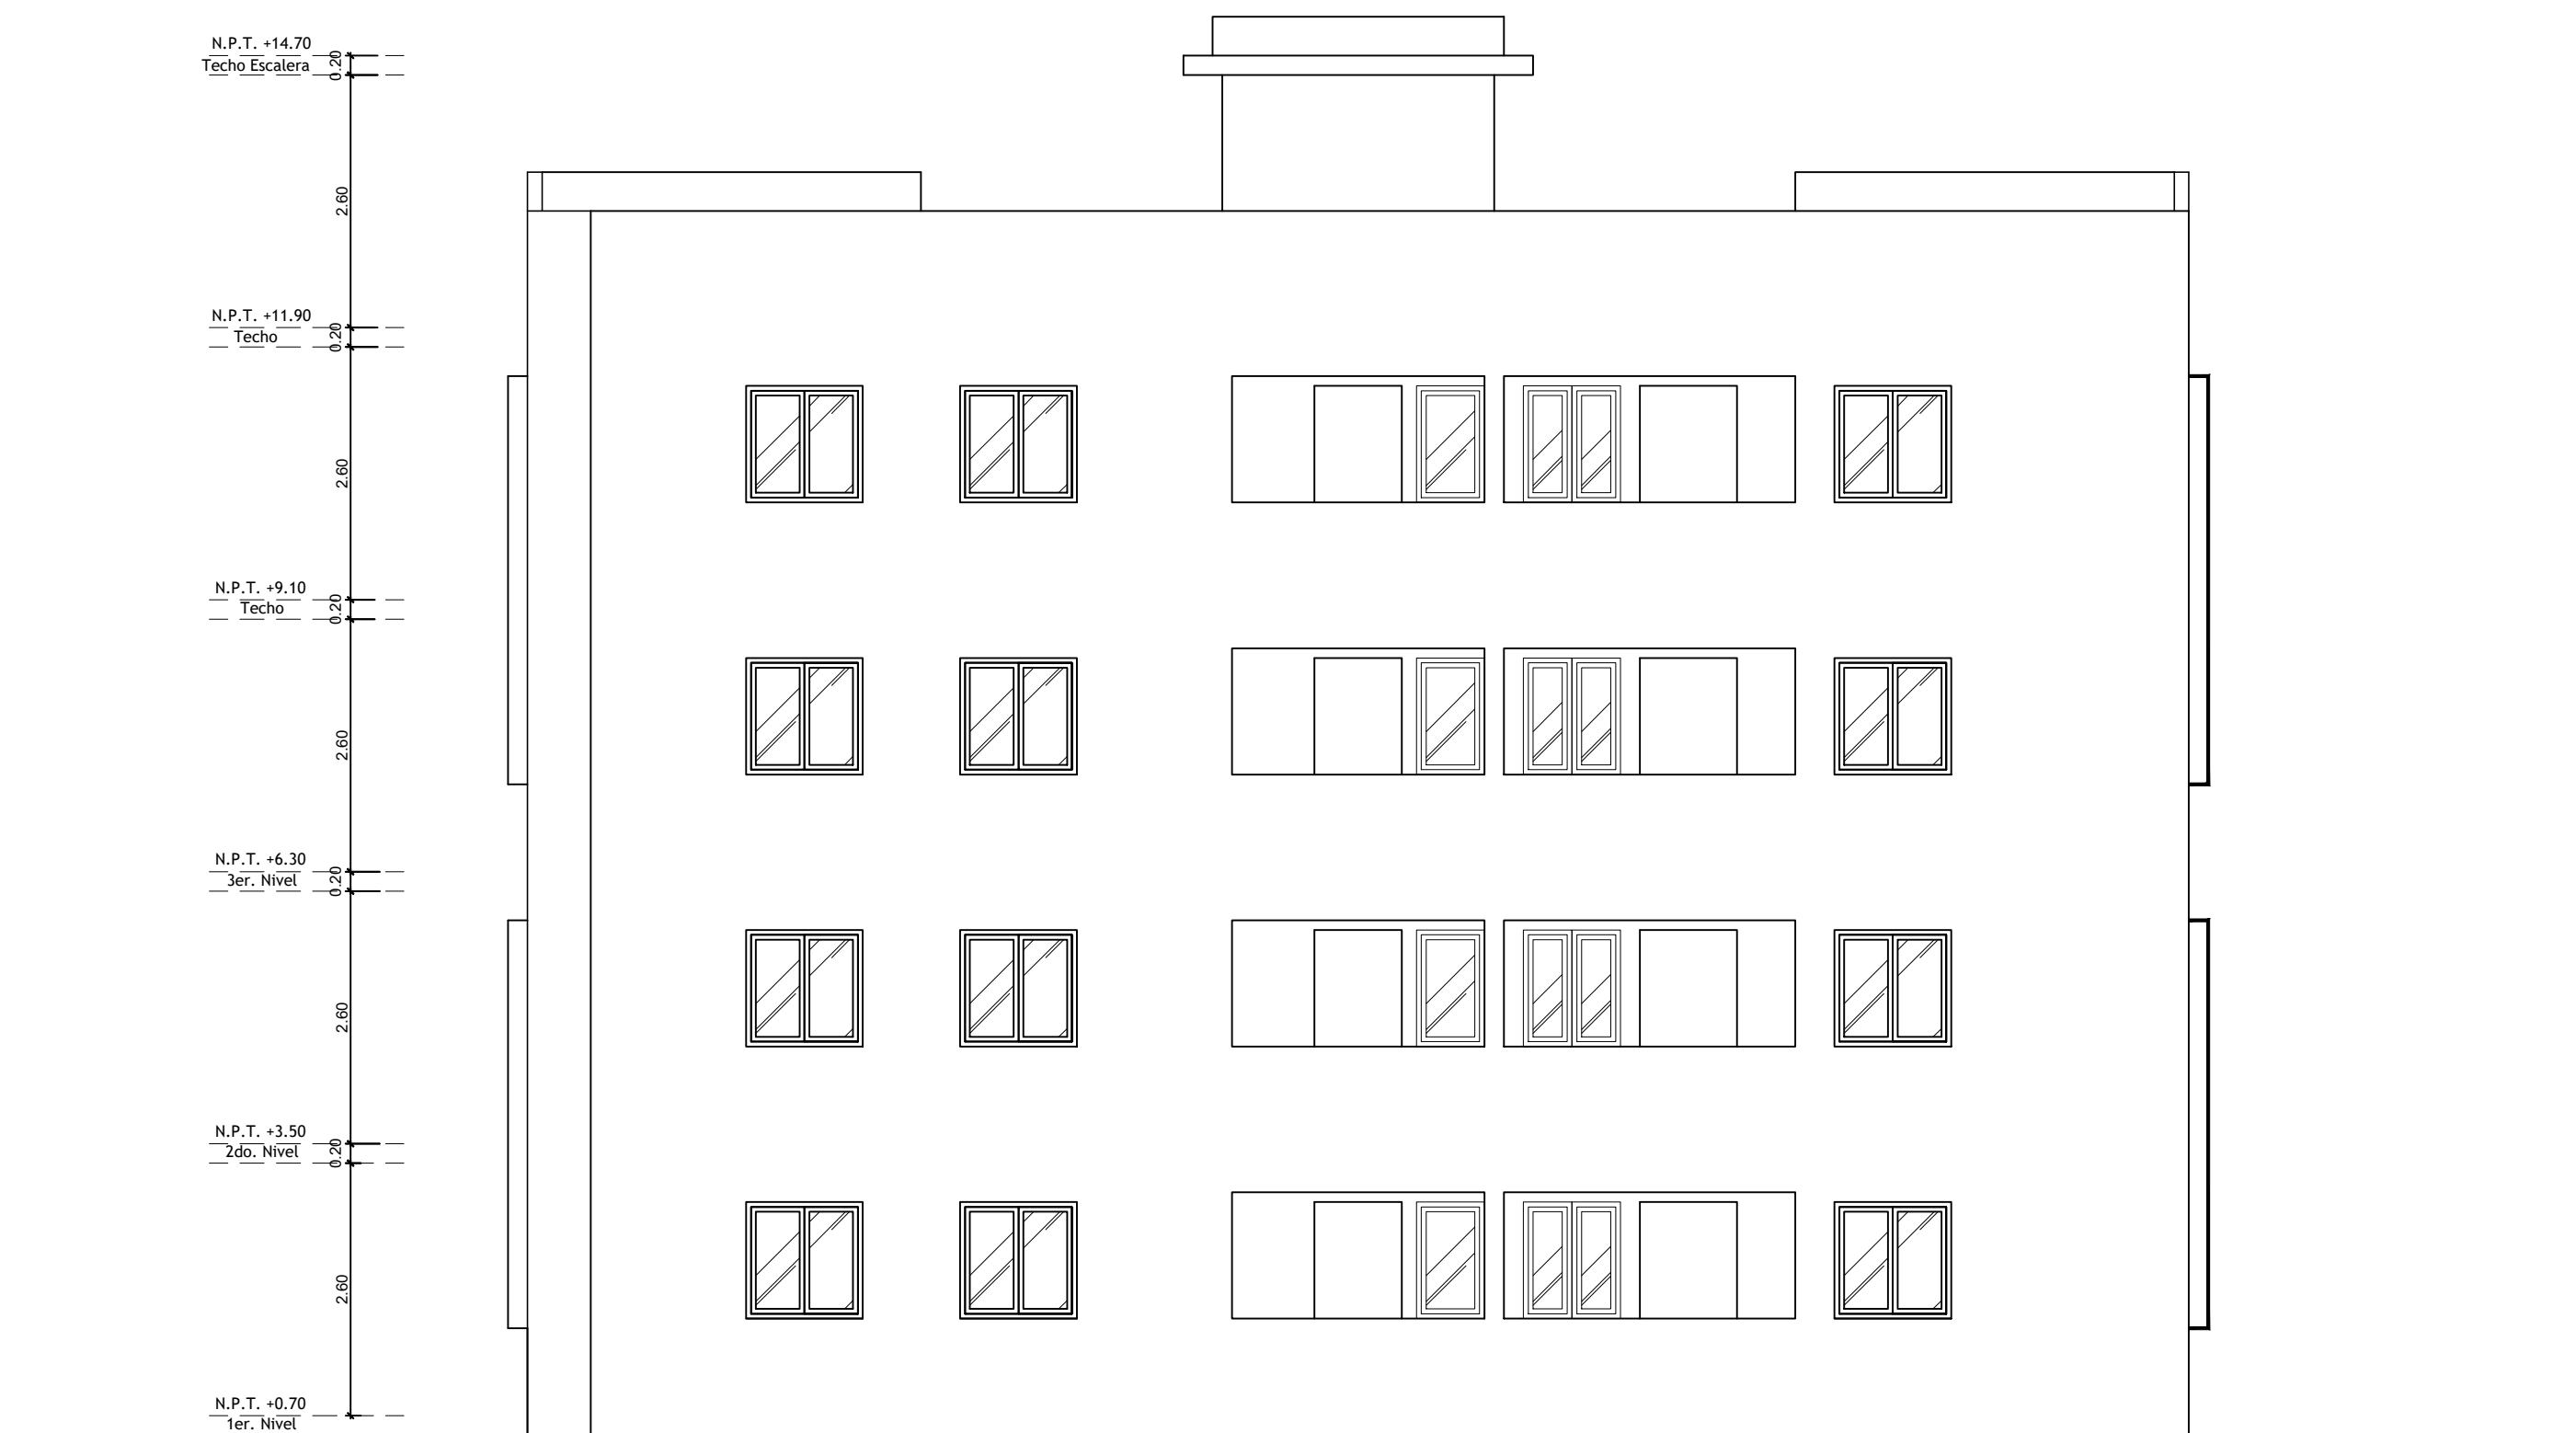

ELEVACION POSTERIOR, BLOQUE A
ESCALA: 1:75

3
A06

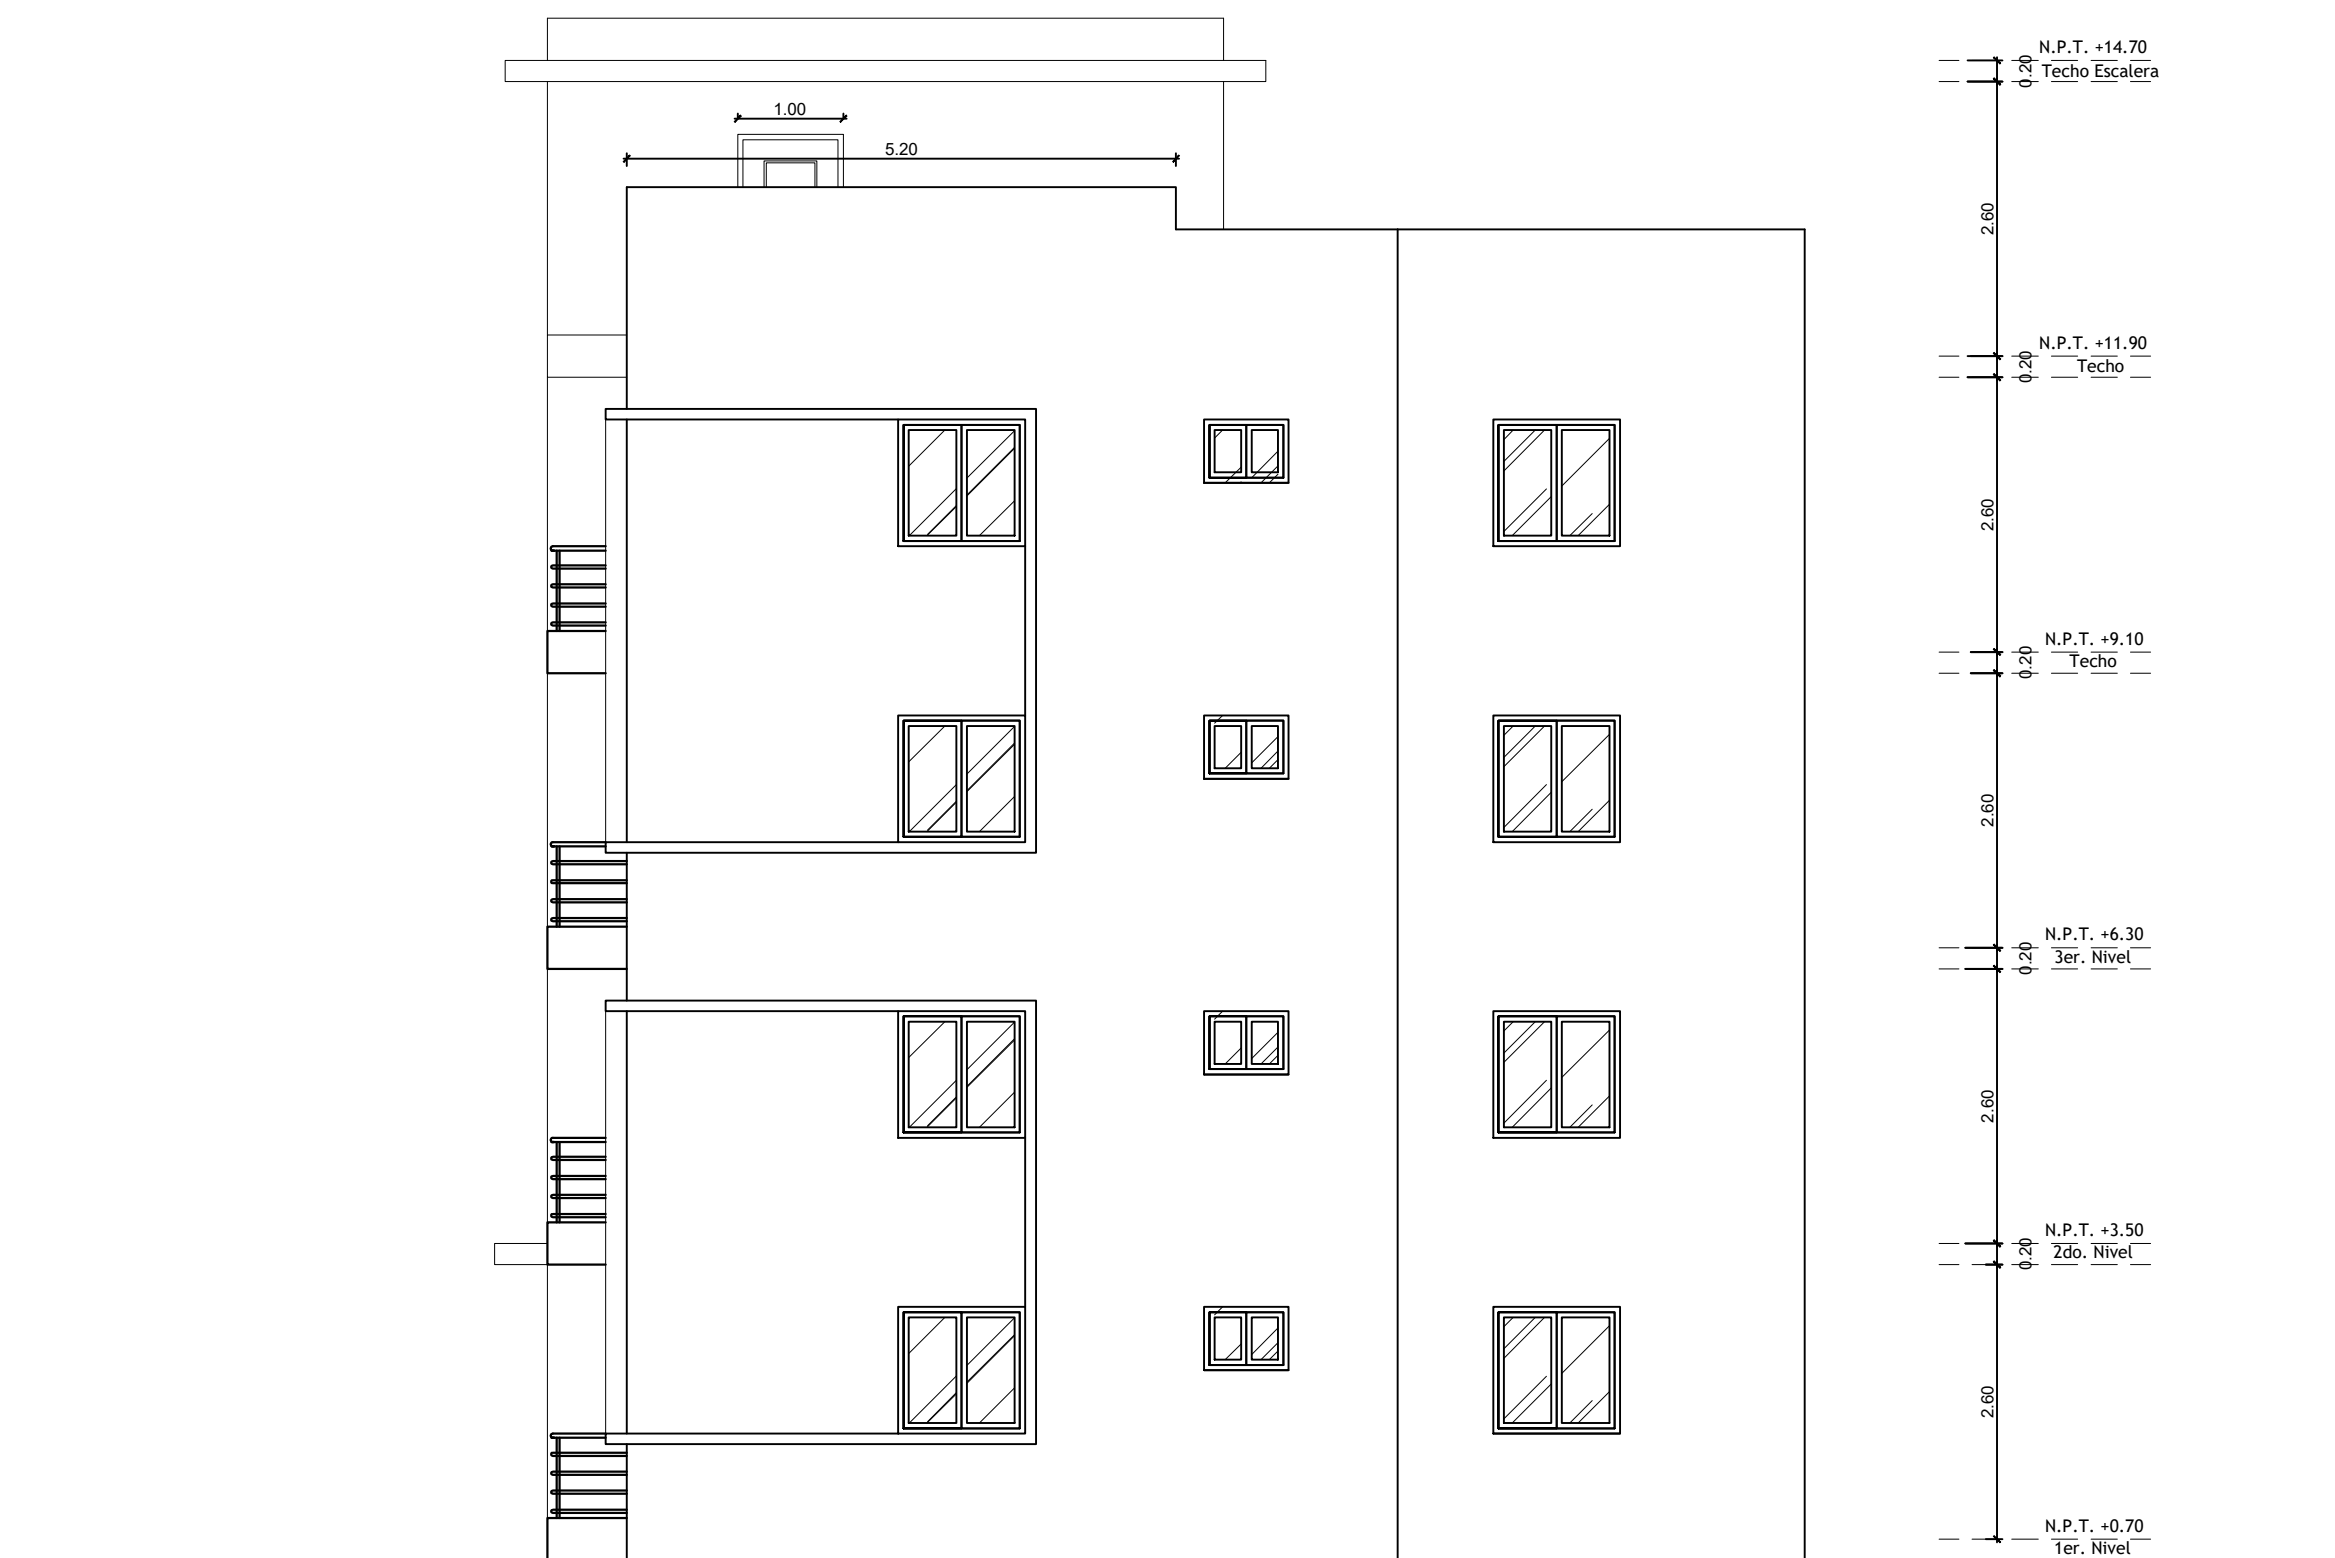

ELEVACION LATERAL DERECHO, BLOQUE A
ESCALA: 1:75

4
A06



diazmeo & asocs.
ARQUITECTOS
Presidente Billini # 12, Bani, R.D. 522-4989
E-mail: diazmeo@hotmail.com

COLABORACION:



ARQUITECTURA DIGITAL
DISEÑOS-CONSTRUCCION-DIGITACION
COMPROMETIDOS CON SU TIEMPO
C/JUAN SANCHEZ RAMIREZ #56,
LOCAL 5 ZONA UASD TEL:221-5400

PROPIETARIO :
**GRUPO EMPRESARIAL
BANILEJO S.R.L.
GEBSA**

PROYECTISTAS:

DISEÑO ARQUITECTONICO:
DIAZMELO & ASOCS.
Arq. ISMAEL DIAZ MELO
Codia: 9604

DISEÑO SANITARIO:
Arq. HAMLET TEJEDA
Codia: 18303

DISEÑO ESTRUCTURAL:
ING. ODELIN TEJEDA
Codia: 23937

DISEÑO ELECTRICO:
ING. VILLYS SANCHEZ
Codia: 19060

CONTENIDO:
**ELEVACIONES
BLOQUE A**

PROYECTO:
RESIDENCIAL GEBSA IV

Fecha: MAYO/2018

UBICACION:
BANI, PROV. PERAVIA

Ref.: Acad 2000 Hoja No.
Escala: INDICADA

NOTAS:
TODAS LAS TERMINACIONES Y/O CAMBIOS EN EL SET. DE DOCUMENTOS CONSTRUCTIVOS DEBERAN SER APROBADOS POR EL SUPERVISOR RELEVANTE A SU APLICACION EN LA OBRA.
TODAS LAS MEDIDAS DE MUROS Y DE SUPERFICIE A SER REVESTIDAS SERAN RECTIFICADAS PREVIA FABRICACION DE LOS CIERRES O LA O LA INSTALACION DE LOS RECRUBRIMIENTOS
LAS TERMINACIONES Y/O DETALLES NO ESPECIFICADOS SERAN DETERMINADOS ENTRE:
EL DUEÑO Y EL AUTOR DEL PROYECTO.
EL CONTRATISTA NO PODRA TOMAR DECISIONES INCONSULTAS RESPECTO VARIACIONES EN EL CONTENIDO DE ESTE DOCUMENTO
LOS PLANOS ARQUITECTONICOS MANDARAN RESPECTO A LOS DEMAS A ANTE CUALQUIER DIFERENCIA PRIMARA LA INFORMACIONCONTENIDA EN LOS MISMOS



diaz melo & asocs.

ARQUITECTOS

Presidente Billini # 12, Bani, R.D. 522-4989

E-mail: diazmelohotmail.com

COLABORACION:



ARQUITECTURA DIGITAL
DISEÑOS-CONSTRUCCION-DIGITACION
COMPROMETIDOS CON SU TIEMPO
C./JUAN SANCHEZ RAMIREZ #56,
LOCAL 5 ZONA UASD TEL:221-5400

PROPIETARIO :
**GRUPO EMPRESARIAL
BANILEJO S.R.L.
GEBSA**

PROYECTISTAS:

DISEÑO ARQUITECTONICO:
DIAZMELO & ASOCS.
Arq. ISMAEL DIAZ MELO
Codia: 9604

DISEÑO SANITARIO:
Arq. HAMLET TEJEDA
Codia: 18303

DISEÑO ESTRUCTURAL:
ING. ODELIN TEJEDA
Codia: 23937

DISEÑO ELECTRICO:
ING. VILLYS SANCHEZ
Codia: 19060

CONTENIDO:
SECCIONES BLOQUE A

PROYECTO:
RESIDENCIAL GEBSA IV

Fecha: MAYO/2018

UBICACION:

BANI, PROV. PERAVIA

Ref.: Acad 2000
Escala: INDICADA

Hoja No.


NOTAS:
TODAS LAS TERMINACIONES Y/O CAMBIOS EN EL SET. DE DOCUMENTOS CONSTRUCTIVOS DEBERAN SER APROBADOS POR EL SUPERVISOR RELEVANTE A SU APLICACION EN LA OBRA.

TODAS LAS MEDIDAS DE MUROS Y DE SUPERFICIE A SER REVESTIDAS SERAN RECTIFICADAS PREVIA FABRICACION DE LOS CIERRES O LA O LA INSTALACION DE LOS RECURRIMIENTOS

LAS TERMINACIONES Y/O DETALLES NO ESPECIFICADOS SERAN DEFINIDOS ENTRE:

EL DUEÑO Y EL AUTOR DEL PROYECTO.
EL CONTRATISTA NO PODRA TOMAR DECISIONES INCONSULTAS RESPECTO A LAS VARIACIONES EN EL CONTENIDO DE ESTE DOCUMENTO


LOS PLANOS ARQUITECTONICOS MANDARAN RESPECTO A LOS DEMAS A DIFERENCIA. PRIMARA LA INFORMACIONCONTENIDA EN LOS MISMOS

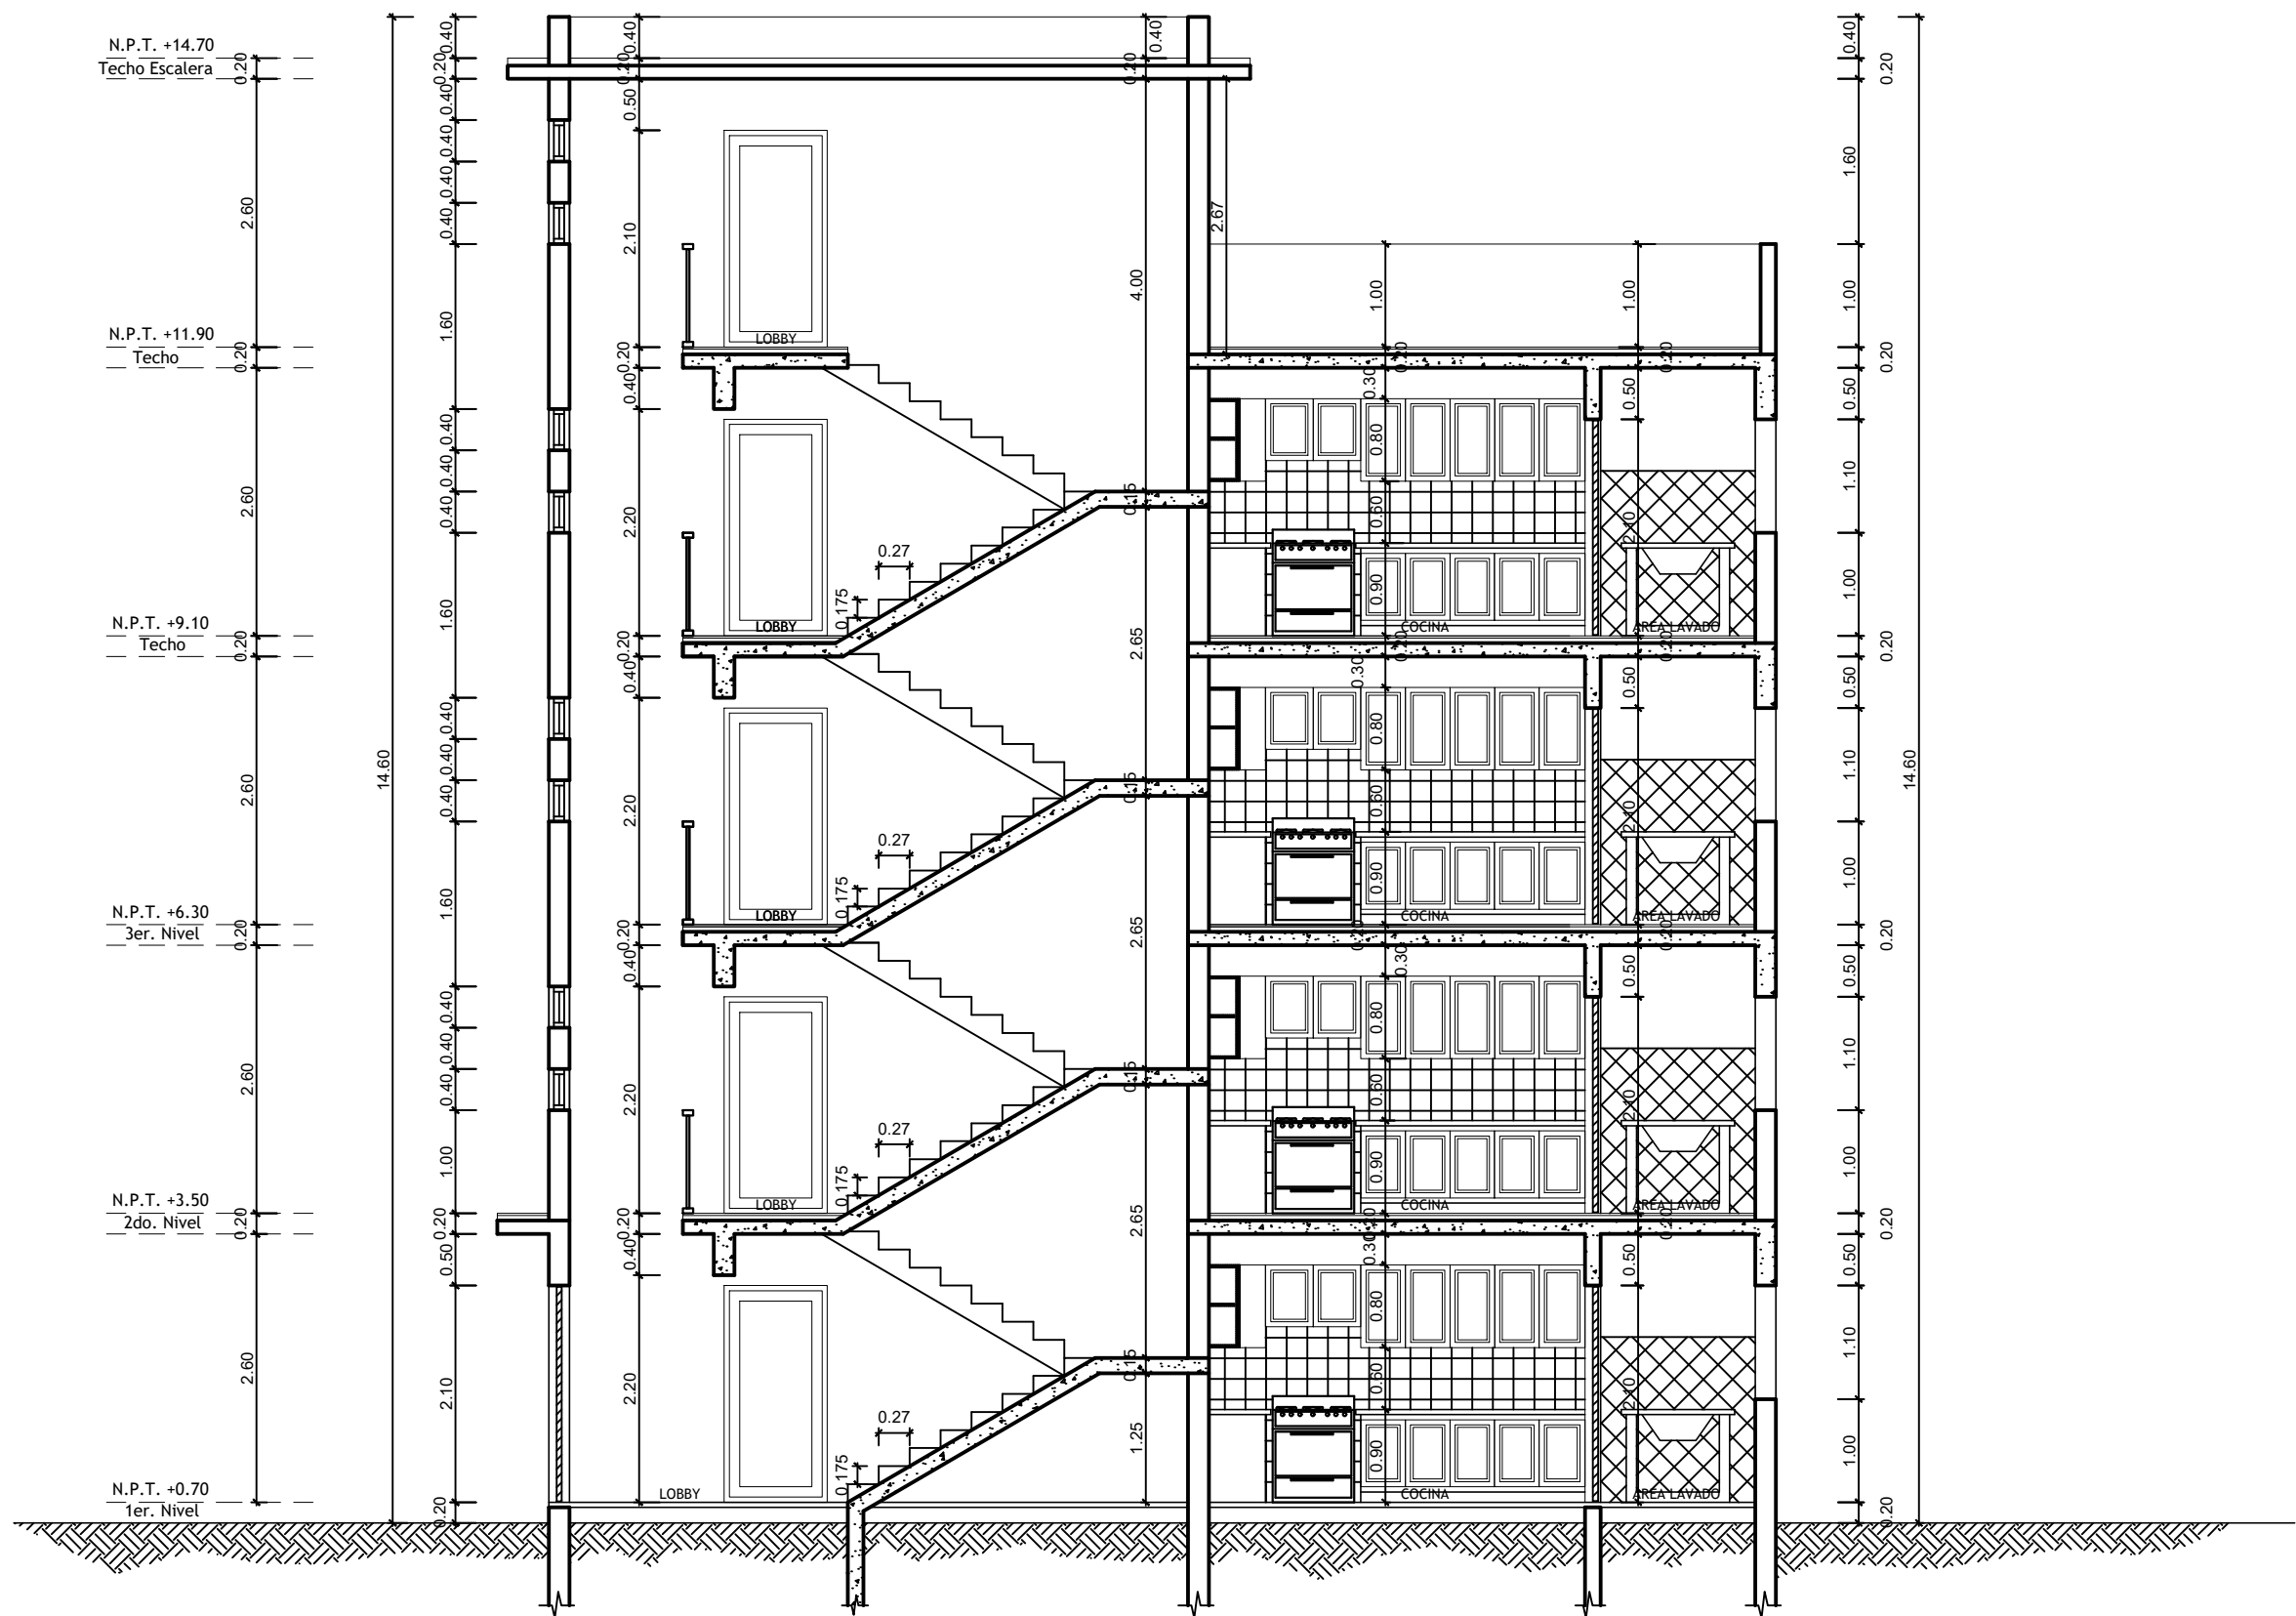

SECCION A-A', BLOQUE A

ESCALA: 1:75


1
A07

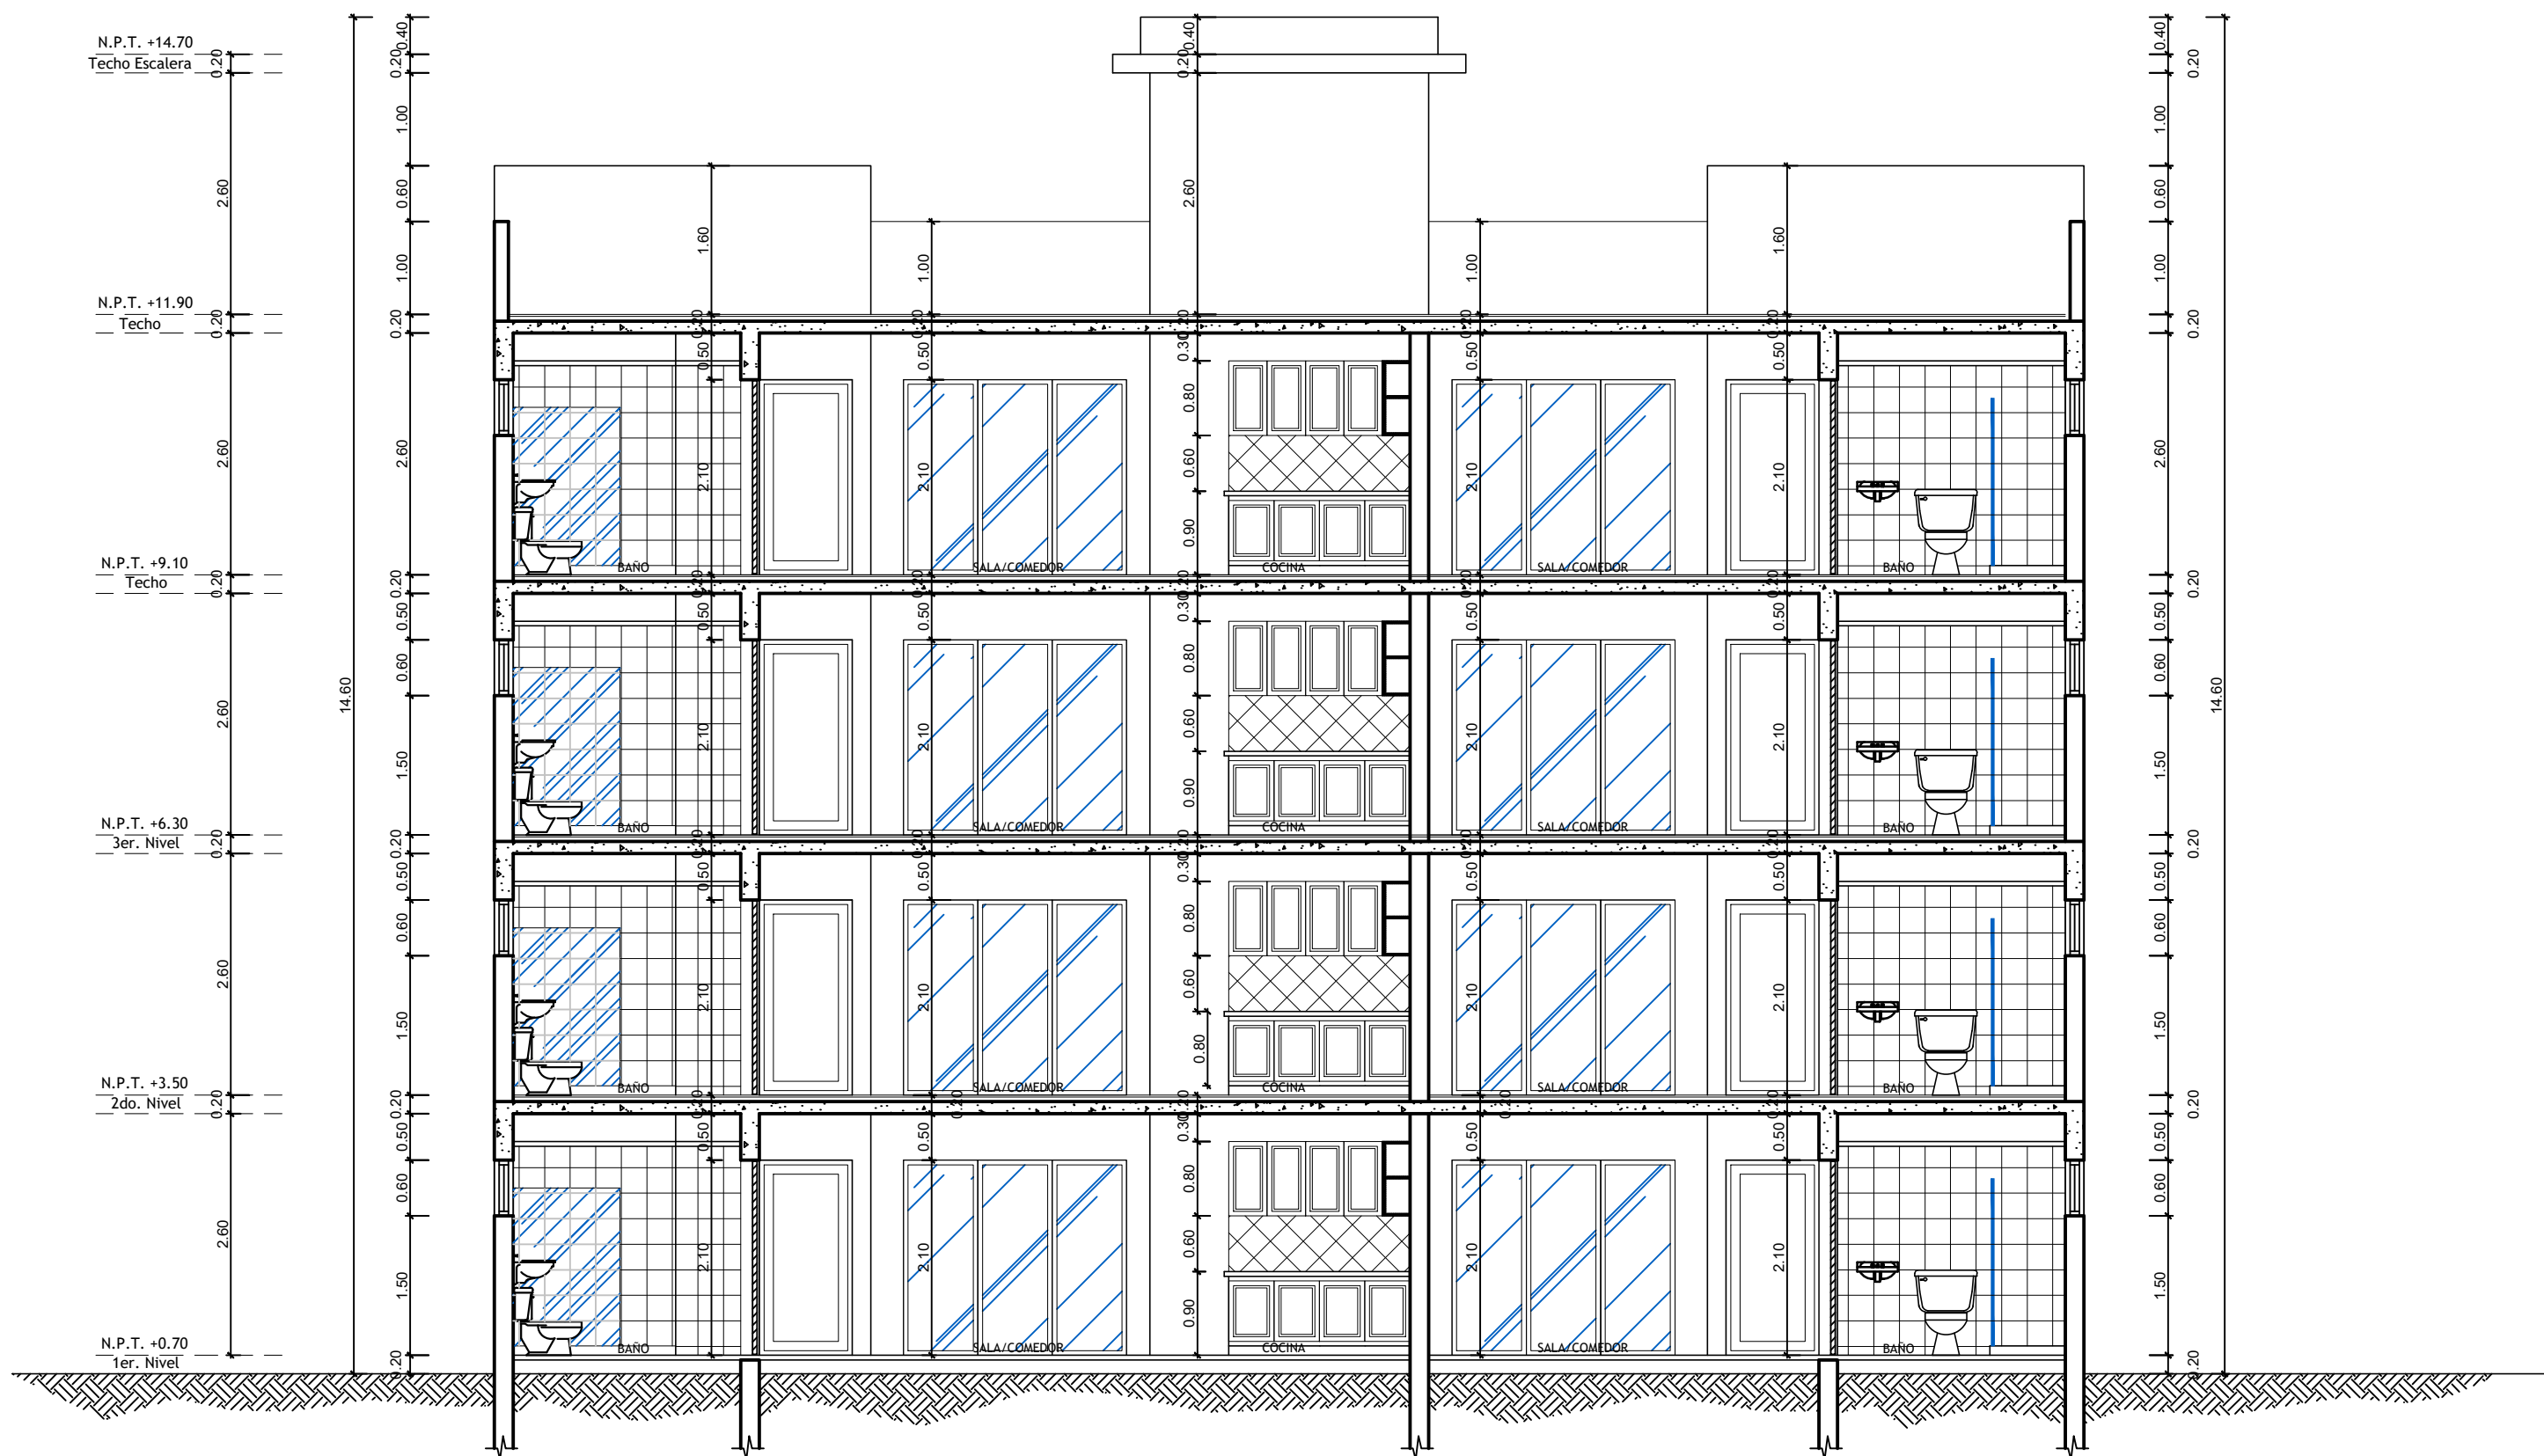


SECCION B-B', BLOQUE A

ESCALA: 1:75


2
A07

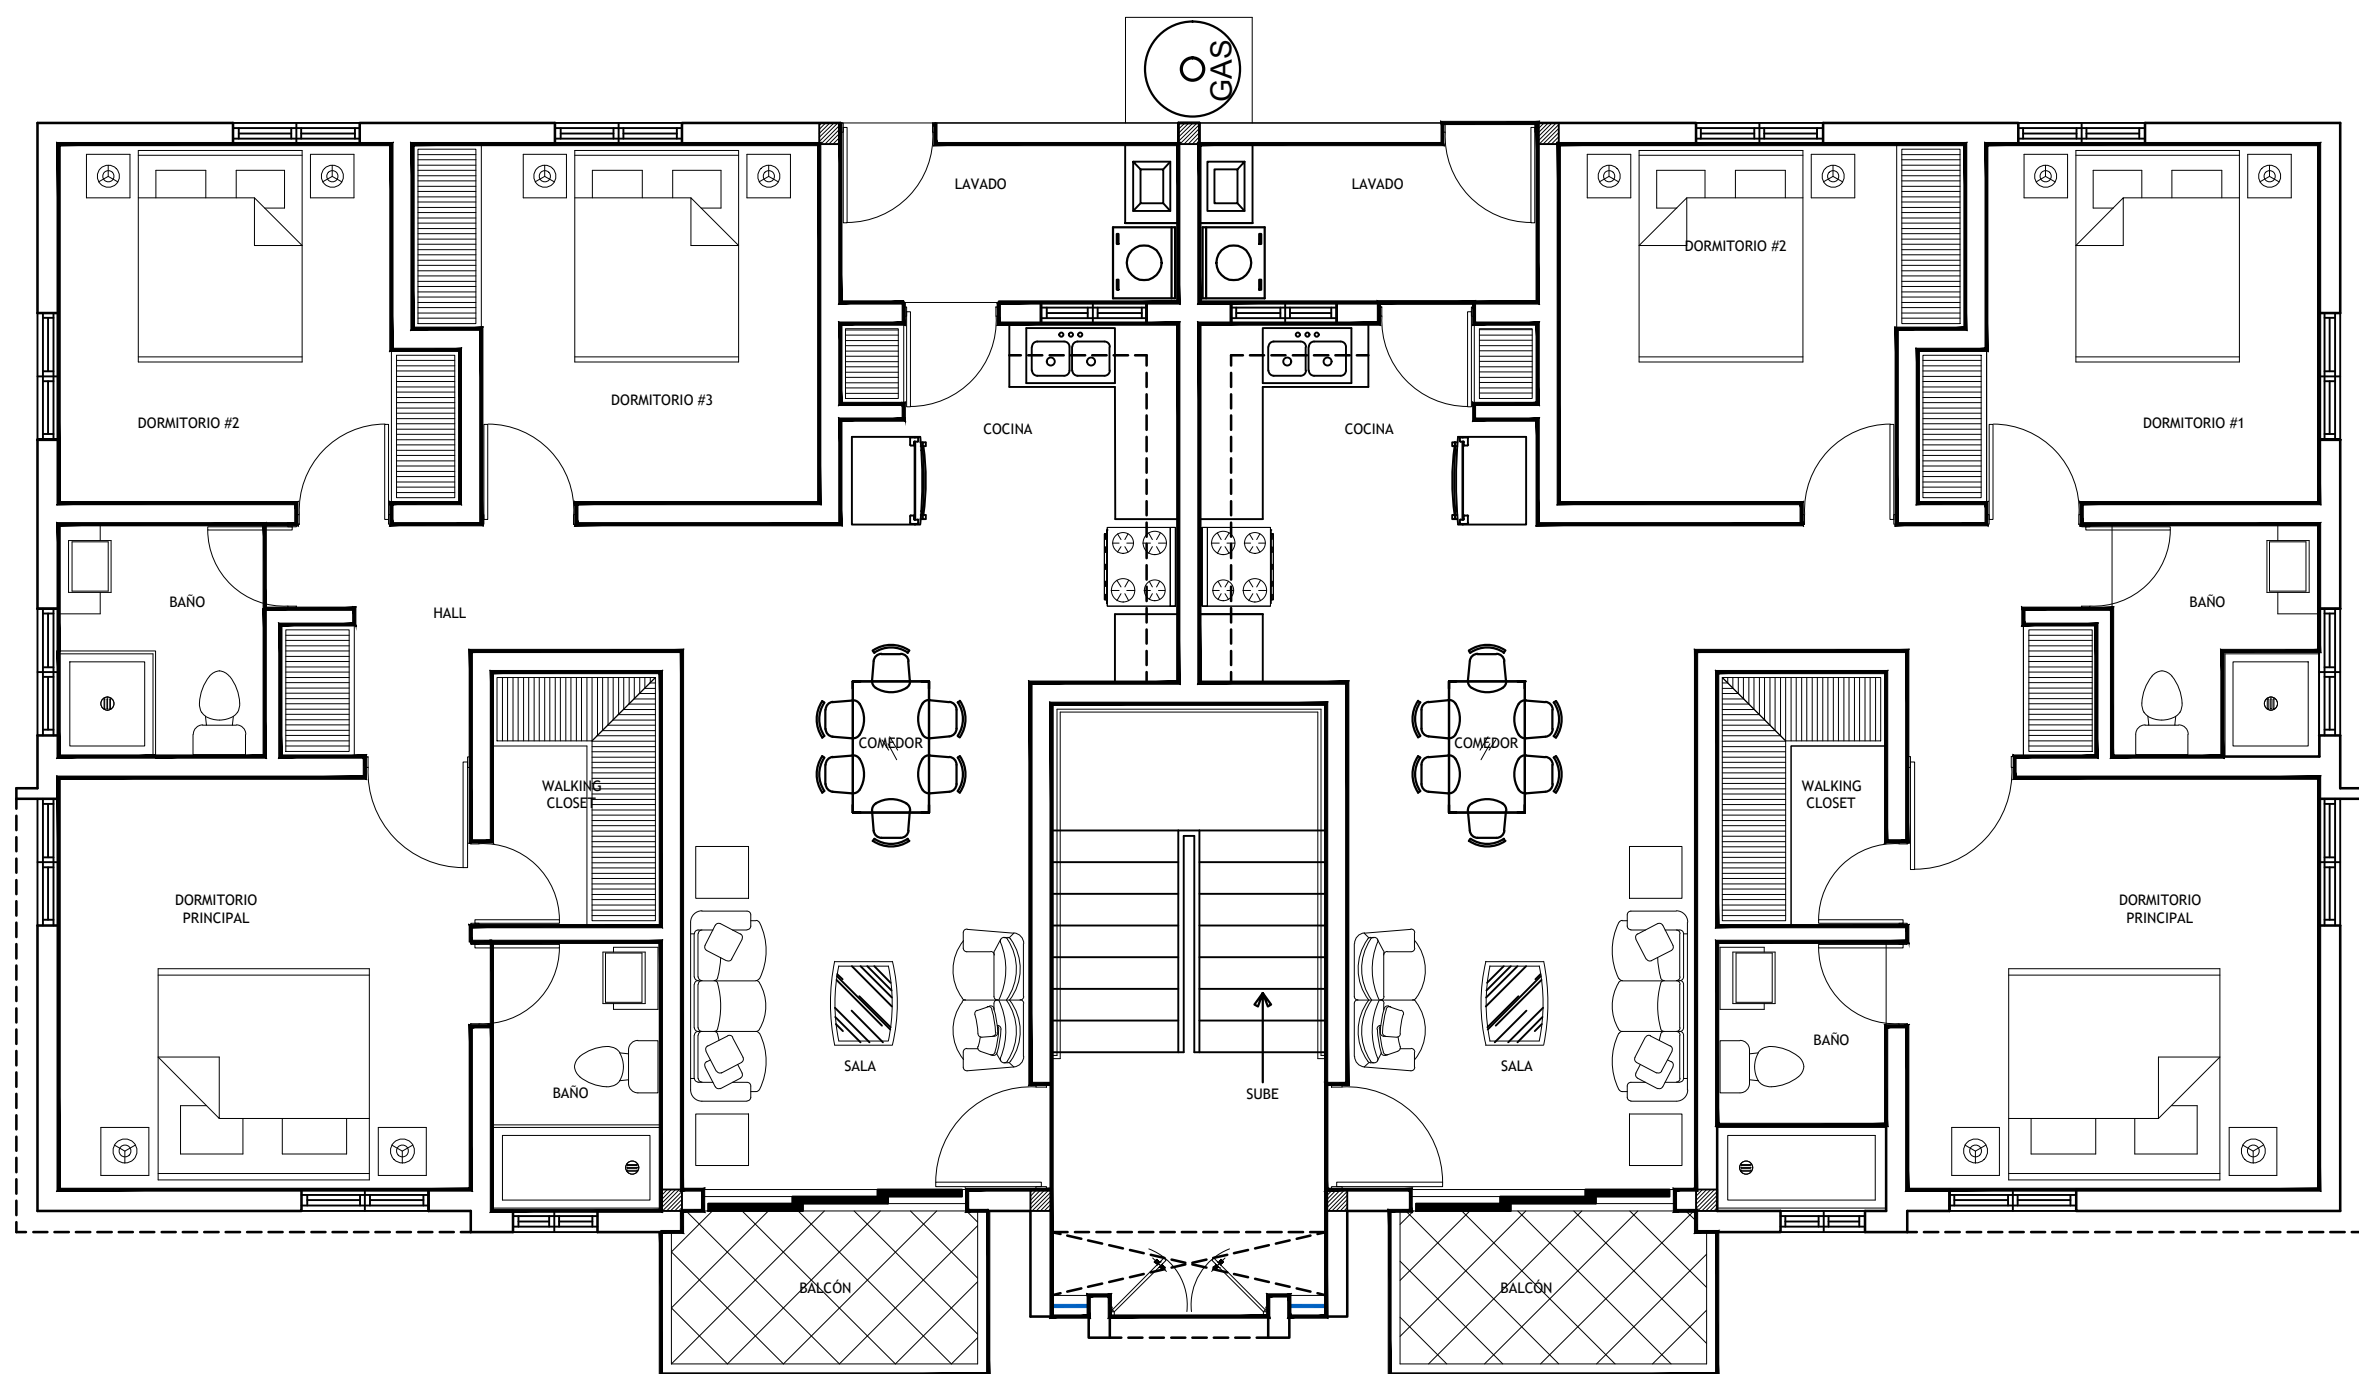

PLANTA ARQUITECTONICA 1ER. NIVEL, BLOQUE B
ESCALA: 1:75

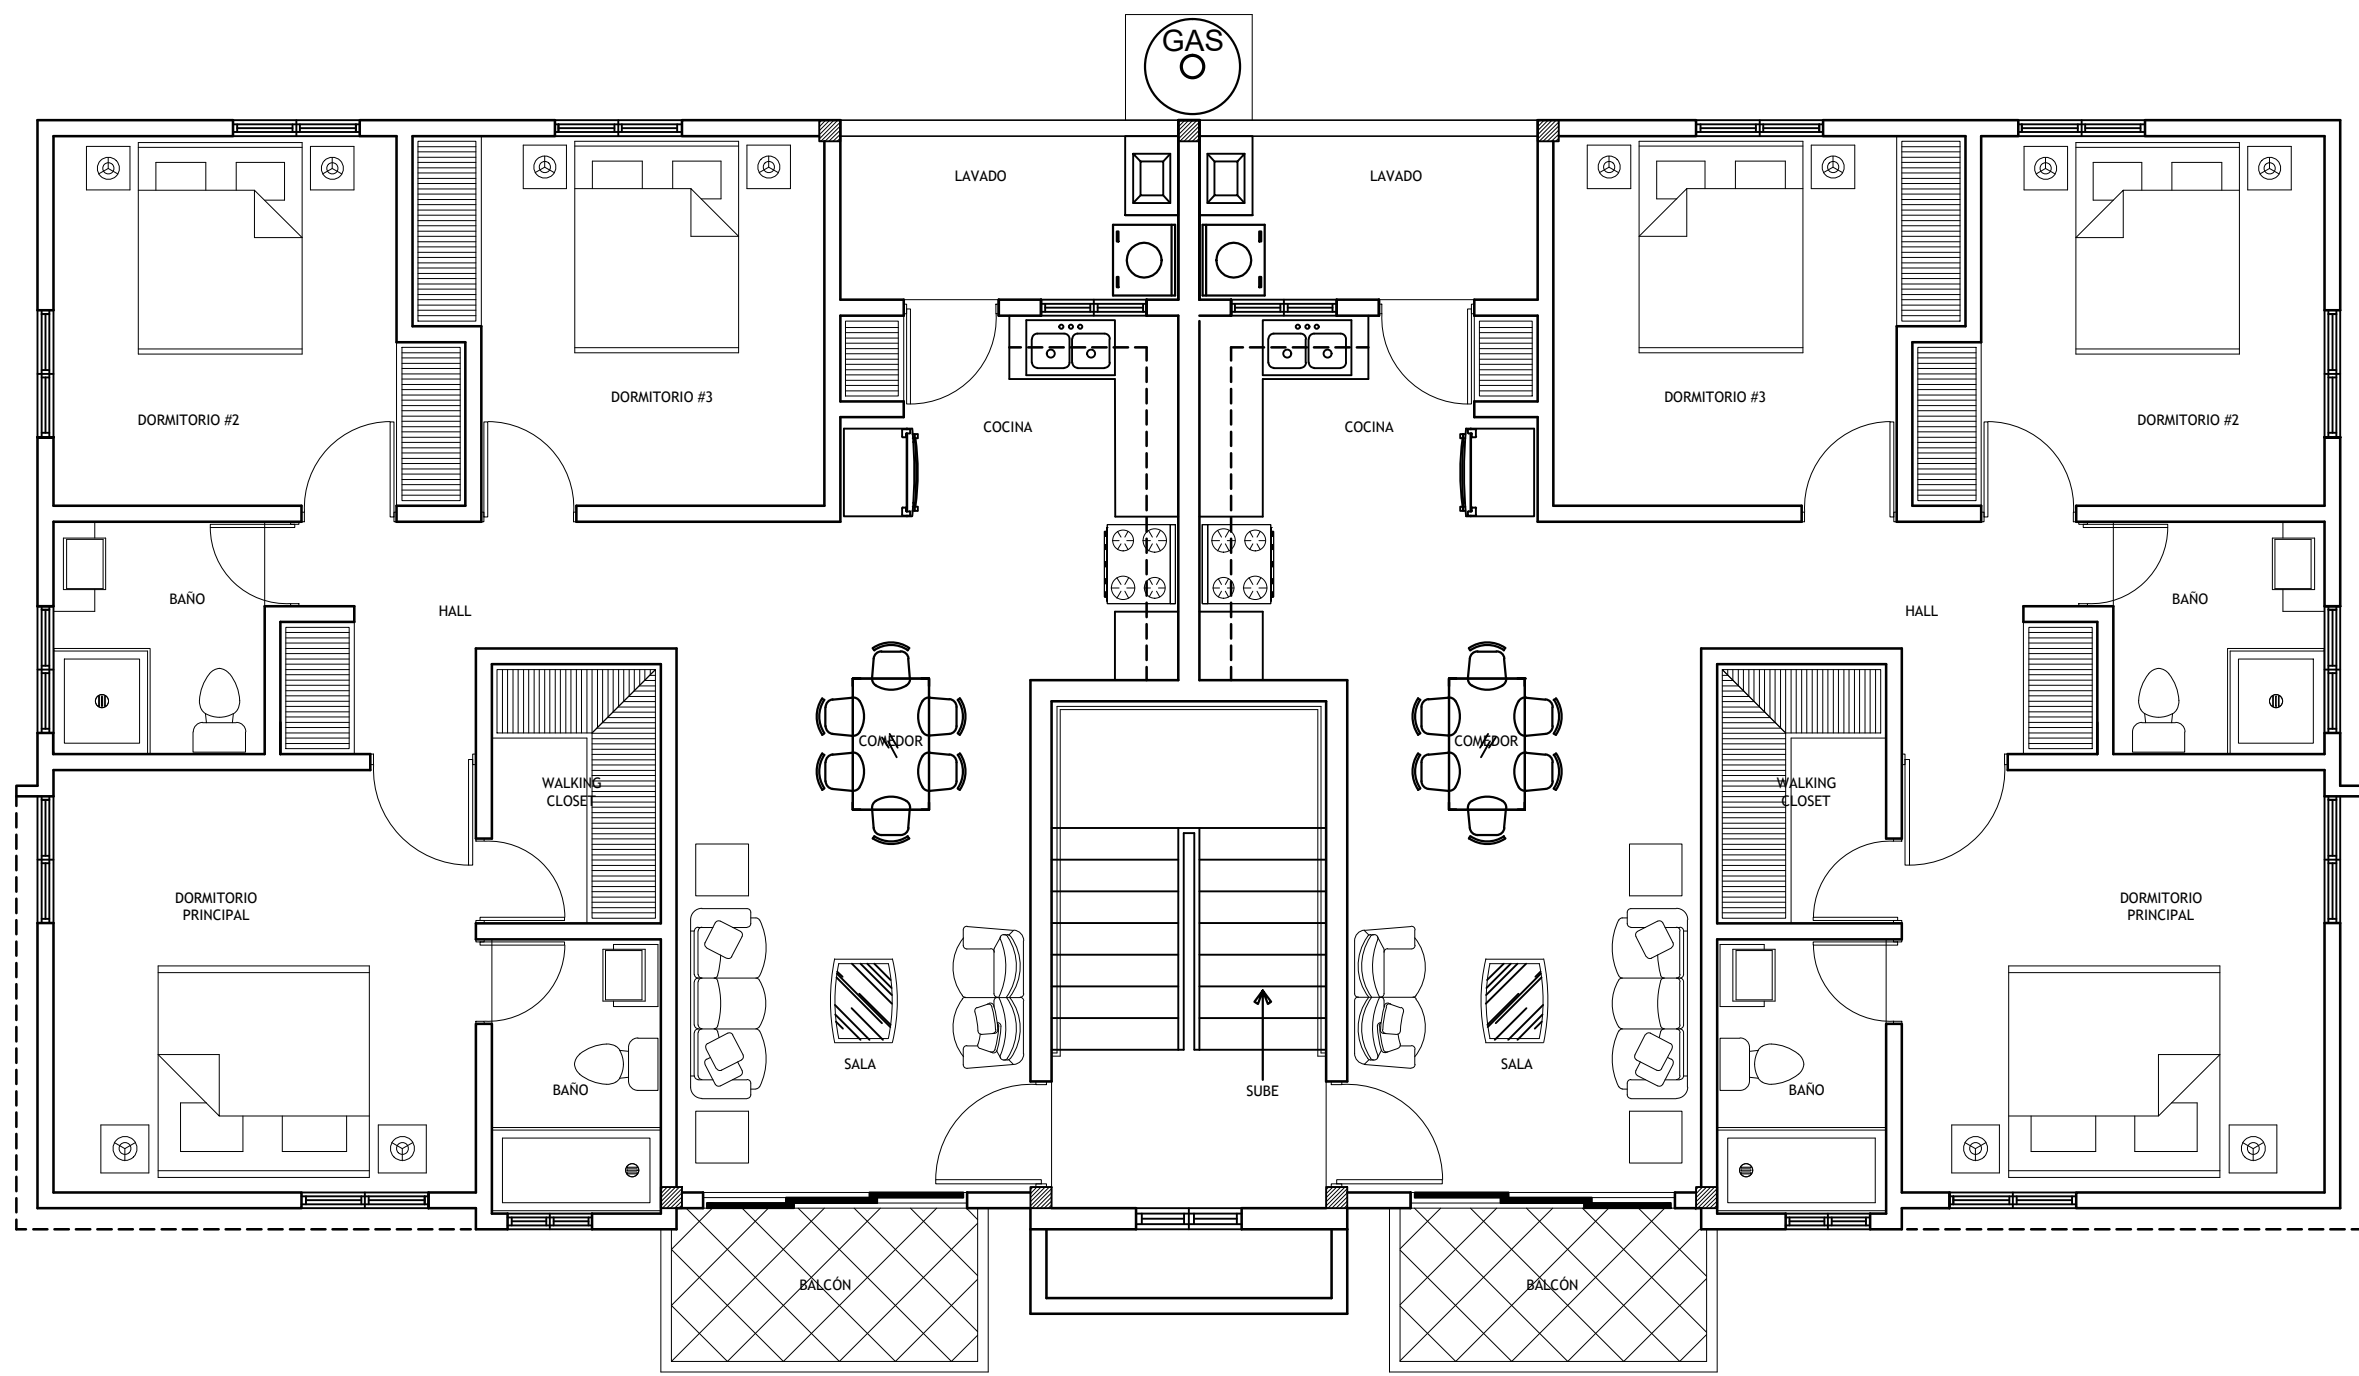

PLANTA ARQUITECTONICA 3ER. NIVEL, BLOQUE B
ESCALA: 1:75

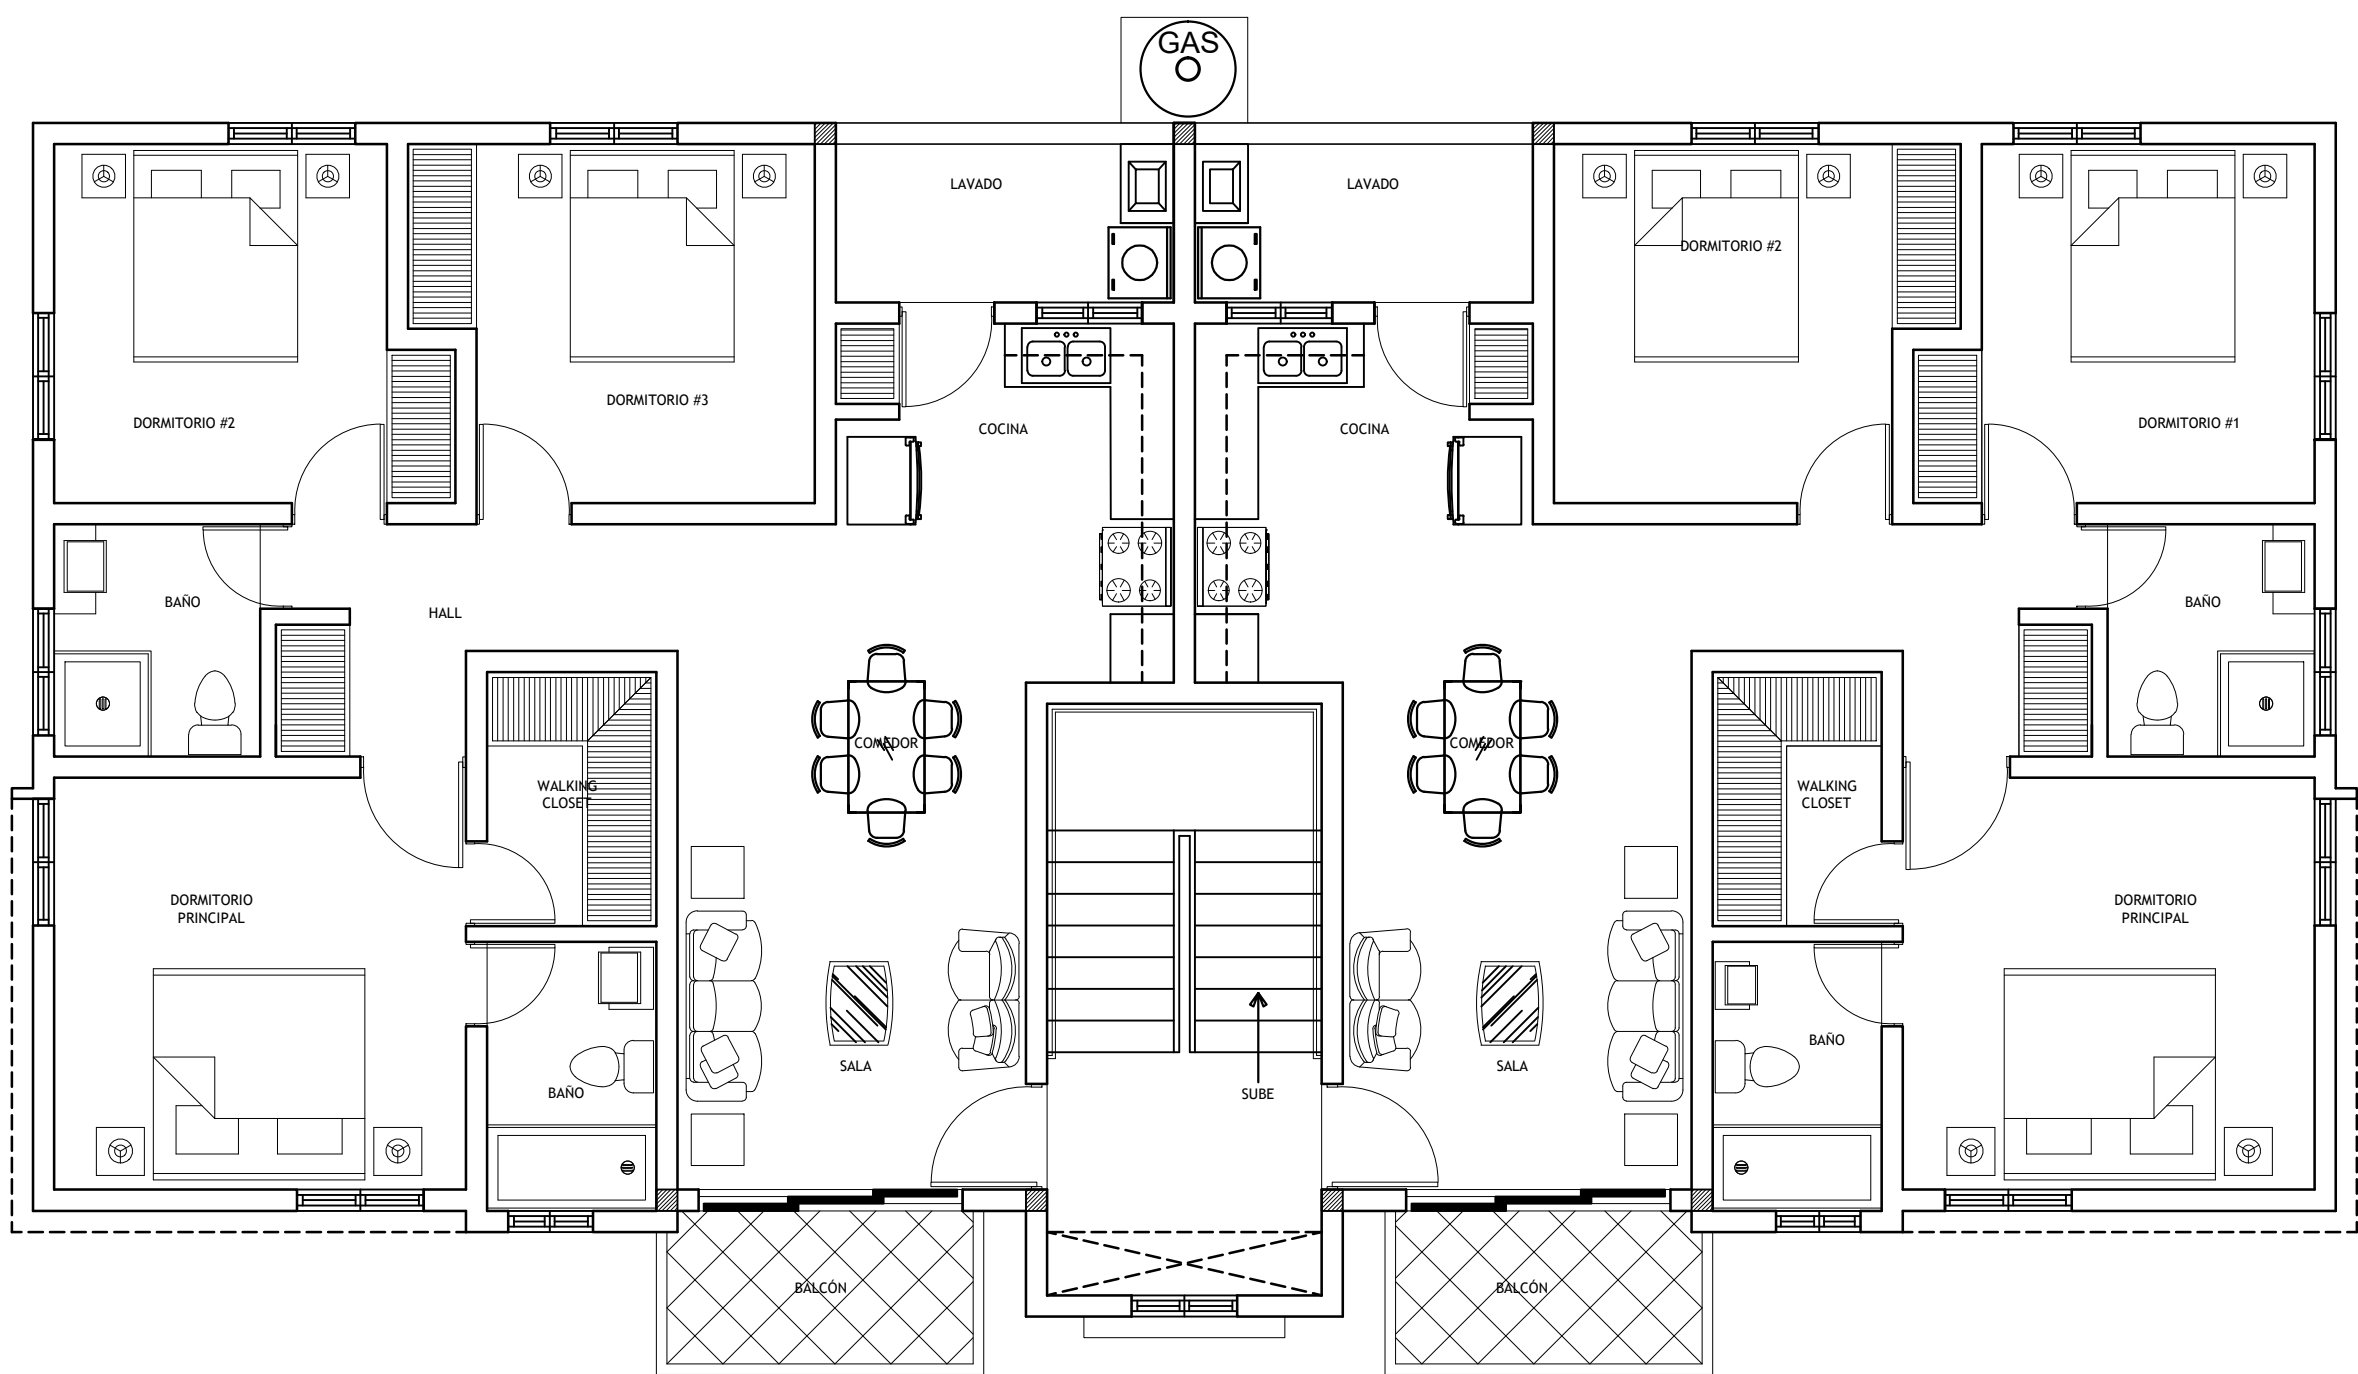

PLANTA ARQUITECTONICA 2DO. NIVEL, BLOQUE B
ESCALA: 1:75



diaz melo & asocs.
ARQUITECTOS
Presidente Billini # 12, Bani, R.D. 522-4989
E-mail: diazmelos@hotmail.com

COLABORACION:



ARQUITECTURA DIGITAL
DISEÑOS-CONSTRUCCION-DIGITACION
COMPROMETIDOS CON SU TIEMPO
C/JUAN SANCHEZ RAMIREZ #56,
LOCAL 5 ZONA UASD TEL:221-5400

PROPIETARIO :
**GRUPO EMPRESARIAL
BANILEJO S.R.L.
GEBSA**

PROYECTISTAS:

DISEÑO ARQUITECTONICO:
DIAZMELO & ASOCS.
Arq. ISMAEL DIAZ MELO
Codia: 9604

DISEÑO SANITARIO:
Arq. HAMLET TEJEDA
Codia: 18303

DISEÑO ESTRUCTURAL:
ING. ODELIN TEJEDA
Codia: 23937

DISEÑO ELECTRICO:
ING. VILLYS SANCHEZ
Codia: 19060

CONTENIDO:
**PLANTAS ARQUITECTONICAS
BLOQUE B**

PROYECTO:
RESIDENCIAL GEBSA IV

Fecha: MAYO/2018

UBICACION:
BANI, PROV. PERAVIA

Ref.: Acad 2000
Escala: INDICADA

Hoja No.

NOTAS:
TODAS LAS TERMINACIONES Y/O CAMBIOS EN EL SET. DE DOCUMENTOS CONSTRUCTIVOS DEBERAN SER APROBADOS POR EL SUPERVISOR PREVIAMENTE A SU APLICACION EN LA OBRA.
TODAS LAS MEDIDAS DE MUROS Y DE SUPERFICIE A SER REVESTIDAS SERAN RECTIFICADAS PREVIA FABRICACION DE LOS CIERRES O LA O LA INSTALACION DE LOS RECURRIMIENTOS
LAS TERMINACIONES Y/O DETALLES NO ESPECIFICADOS SERAN DEFINIDOS ENTRE:
EL DUEÑO Y EL AUTOR DEL PROYECTO.
EL CONTRATISTA NO PODRA TOMAR DECISIONES INCONSULTAS RESPECTO VARIACIONES EN EL CONTENIDO DE ESTE DOCUMENTO

LOS PLANOS ARQUITECTONICOS MANDARAN RESPECTO A LOS DEMAS A DIFERENCIA PRIMARA LA INFORMACIONCONTENIDA EN LOS MISMOS



diazme & asocs.

ARQUITECTOS

Presidente Bilini # 12, Bani, R.D. 522-4989

E-mail: diazme@hotmail.com

COLABORACION:



ARQUITECTURA DIGITAL
DISEÑO-CONSTRUCCION-DIGITACION
COMPROMETIDOS CON SU TIEMPO
C/ JUAN SANCHEZ RAMIREZ #56,
LOCAL 5 ZONA UASD TEL:221-5400

PROPIETARIO :
GRUPO EMPRESARIAL
BANILEJO S.R.L.
GEBSA

PROYECTISTAS:

DISEÑO ARQUITECTONICO:
DIAZMELO & ASOCS.
Arq. ISMAEL DIAZ MELO
Codia: 9604

DISEÑO SANITARIO:
Arq. HAMLET TEJEDA
Codia: 18303

DISEÑO ESTRUCTURAL:
ING. ODELIN TEJEDA
Codia: 23937

DISEÑO ELECTRICO:
ING. VILLYS SANCHEZ
Codia: 19060

CONTENIDO:
PLANTAS DIMENSIONADAS
BLOQUE B

PROYECTO:
RESIDENCIAL GEBSA IV


Fecha: MAYO/2018

UBICACION:
BANI, PROV. PERAVIA

Ref.: Acad 2000
Escala: INDICADA

NOTAS:
TODAS LAS TERMINACIONES Y/O CAMBIOS EN EL SET. DE DOCUMENTOS CONSTRUCTIVOS DEBERAN SER APROBADOS POR EL SUPERVISOR PREVIAMENTE.
A SU APLICACION EN LA OBRA.
TODAS LAS MEDIDAS DE MUROS Y DE SUPERFICIE A SER REVESTIDAS SERAN RECTIFICADAS PREVIA FABRICACION DE LOS CIERRES O LA O LA INSTALACION DE LOS RECRUBRIMIENTOS.
LAS TERMINACIONES Y/O DETALLES NO ESPECIFICADOS SERAN DEFINIDOS ENTRE:
EL DUEÑO Y EL AUTOR DEL PROYECTO.
EL CONTRATISTA NO PODRA TOMAR DECISIONES INCONSULTAS RESPECTO A LAS VARIACIONES EN EL CONTENIDO DE ESTE DOCUMENTO.


LOS PLANOS ARQUITECTONICOS MANDARAN RESPECTO A LOS DEMAS A ANTE CUALQUIER DIFERENCIA PRIMARA LA INFORMACIONCONTENIDA EN LOS MISOS

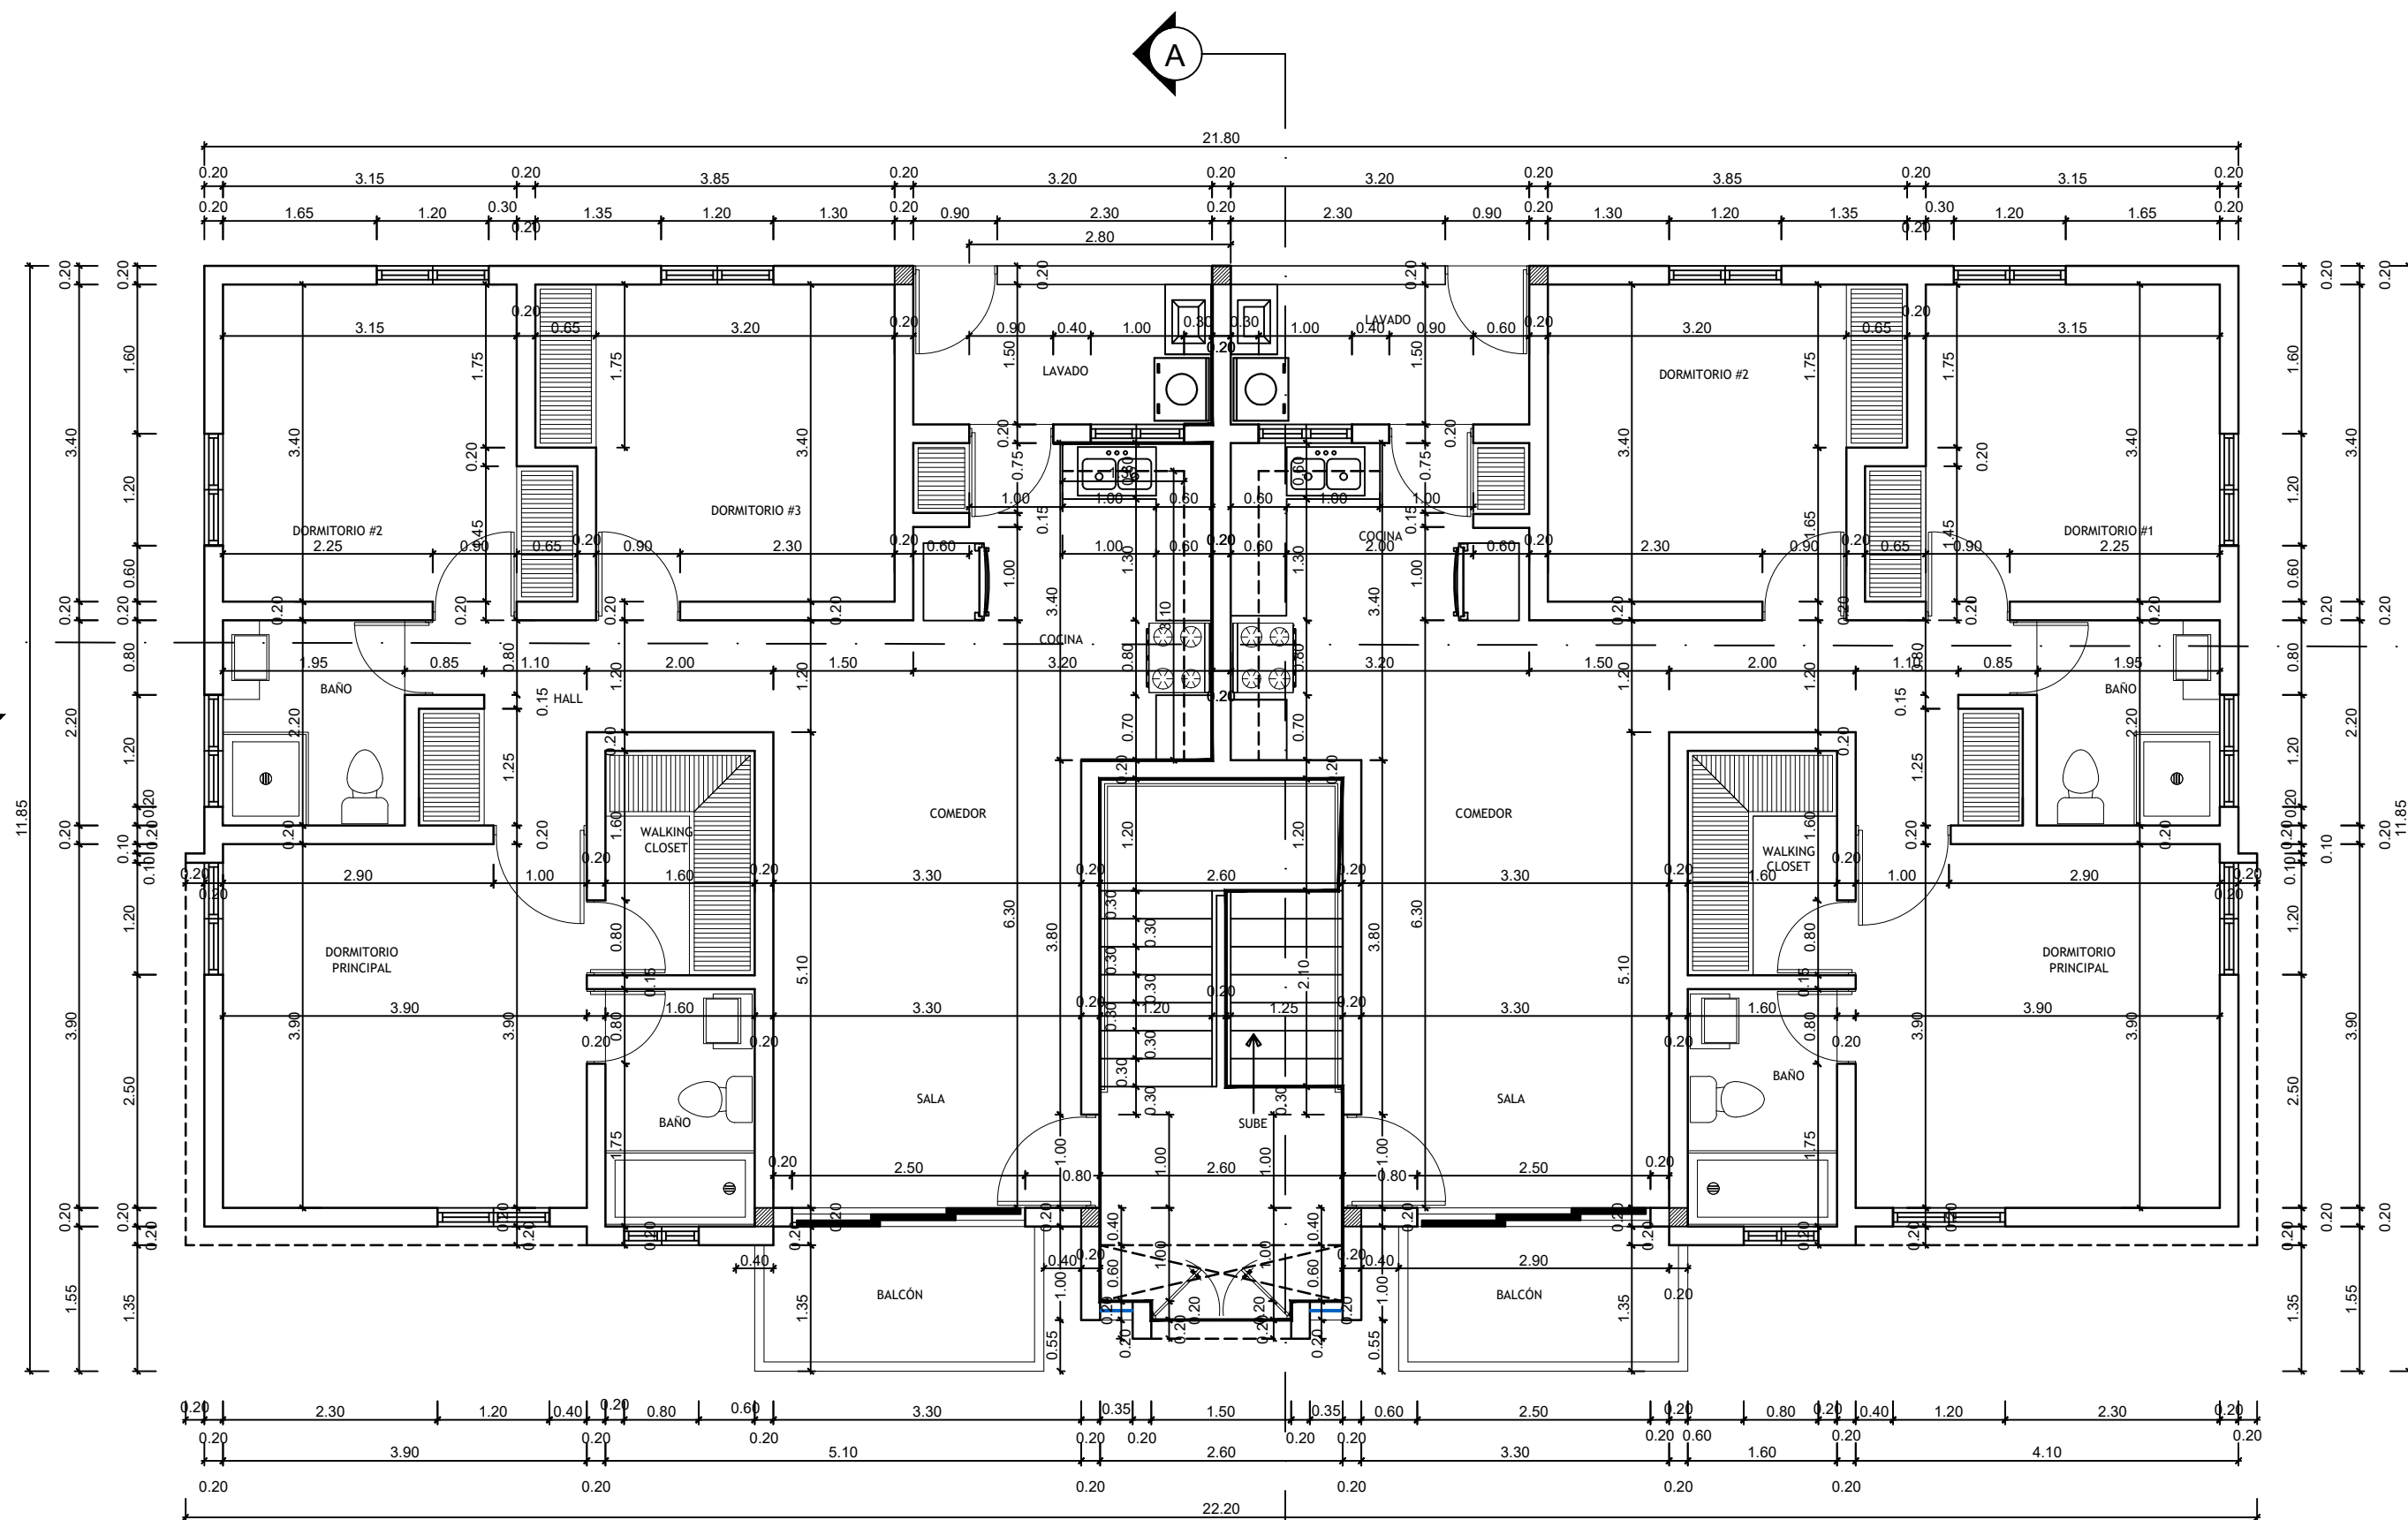

PLANTA DIMENSIONADA 1ER. NIVEL, BLOQUE B
ESCALA: 1:75

1


A09

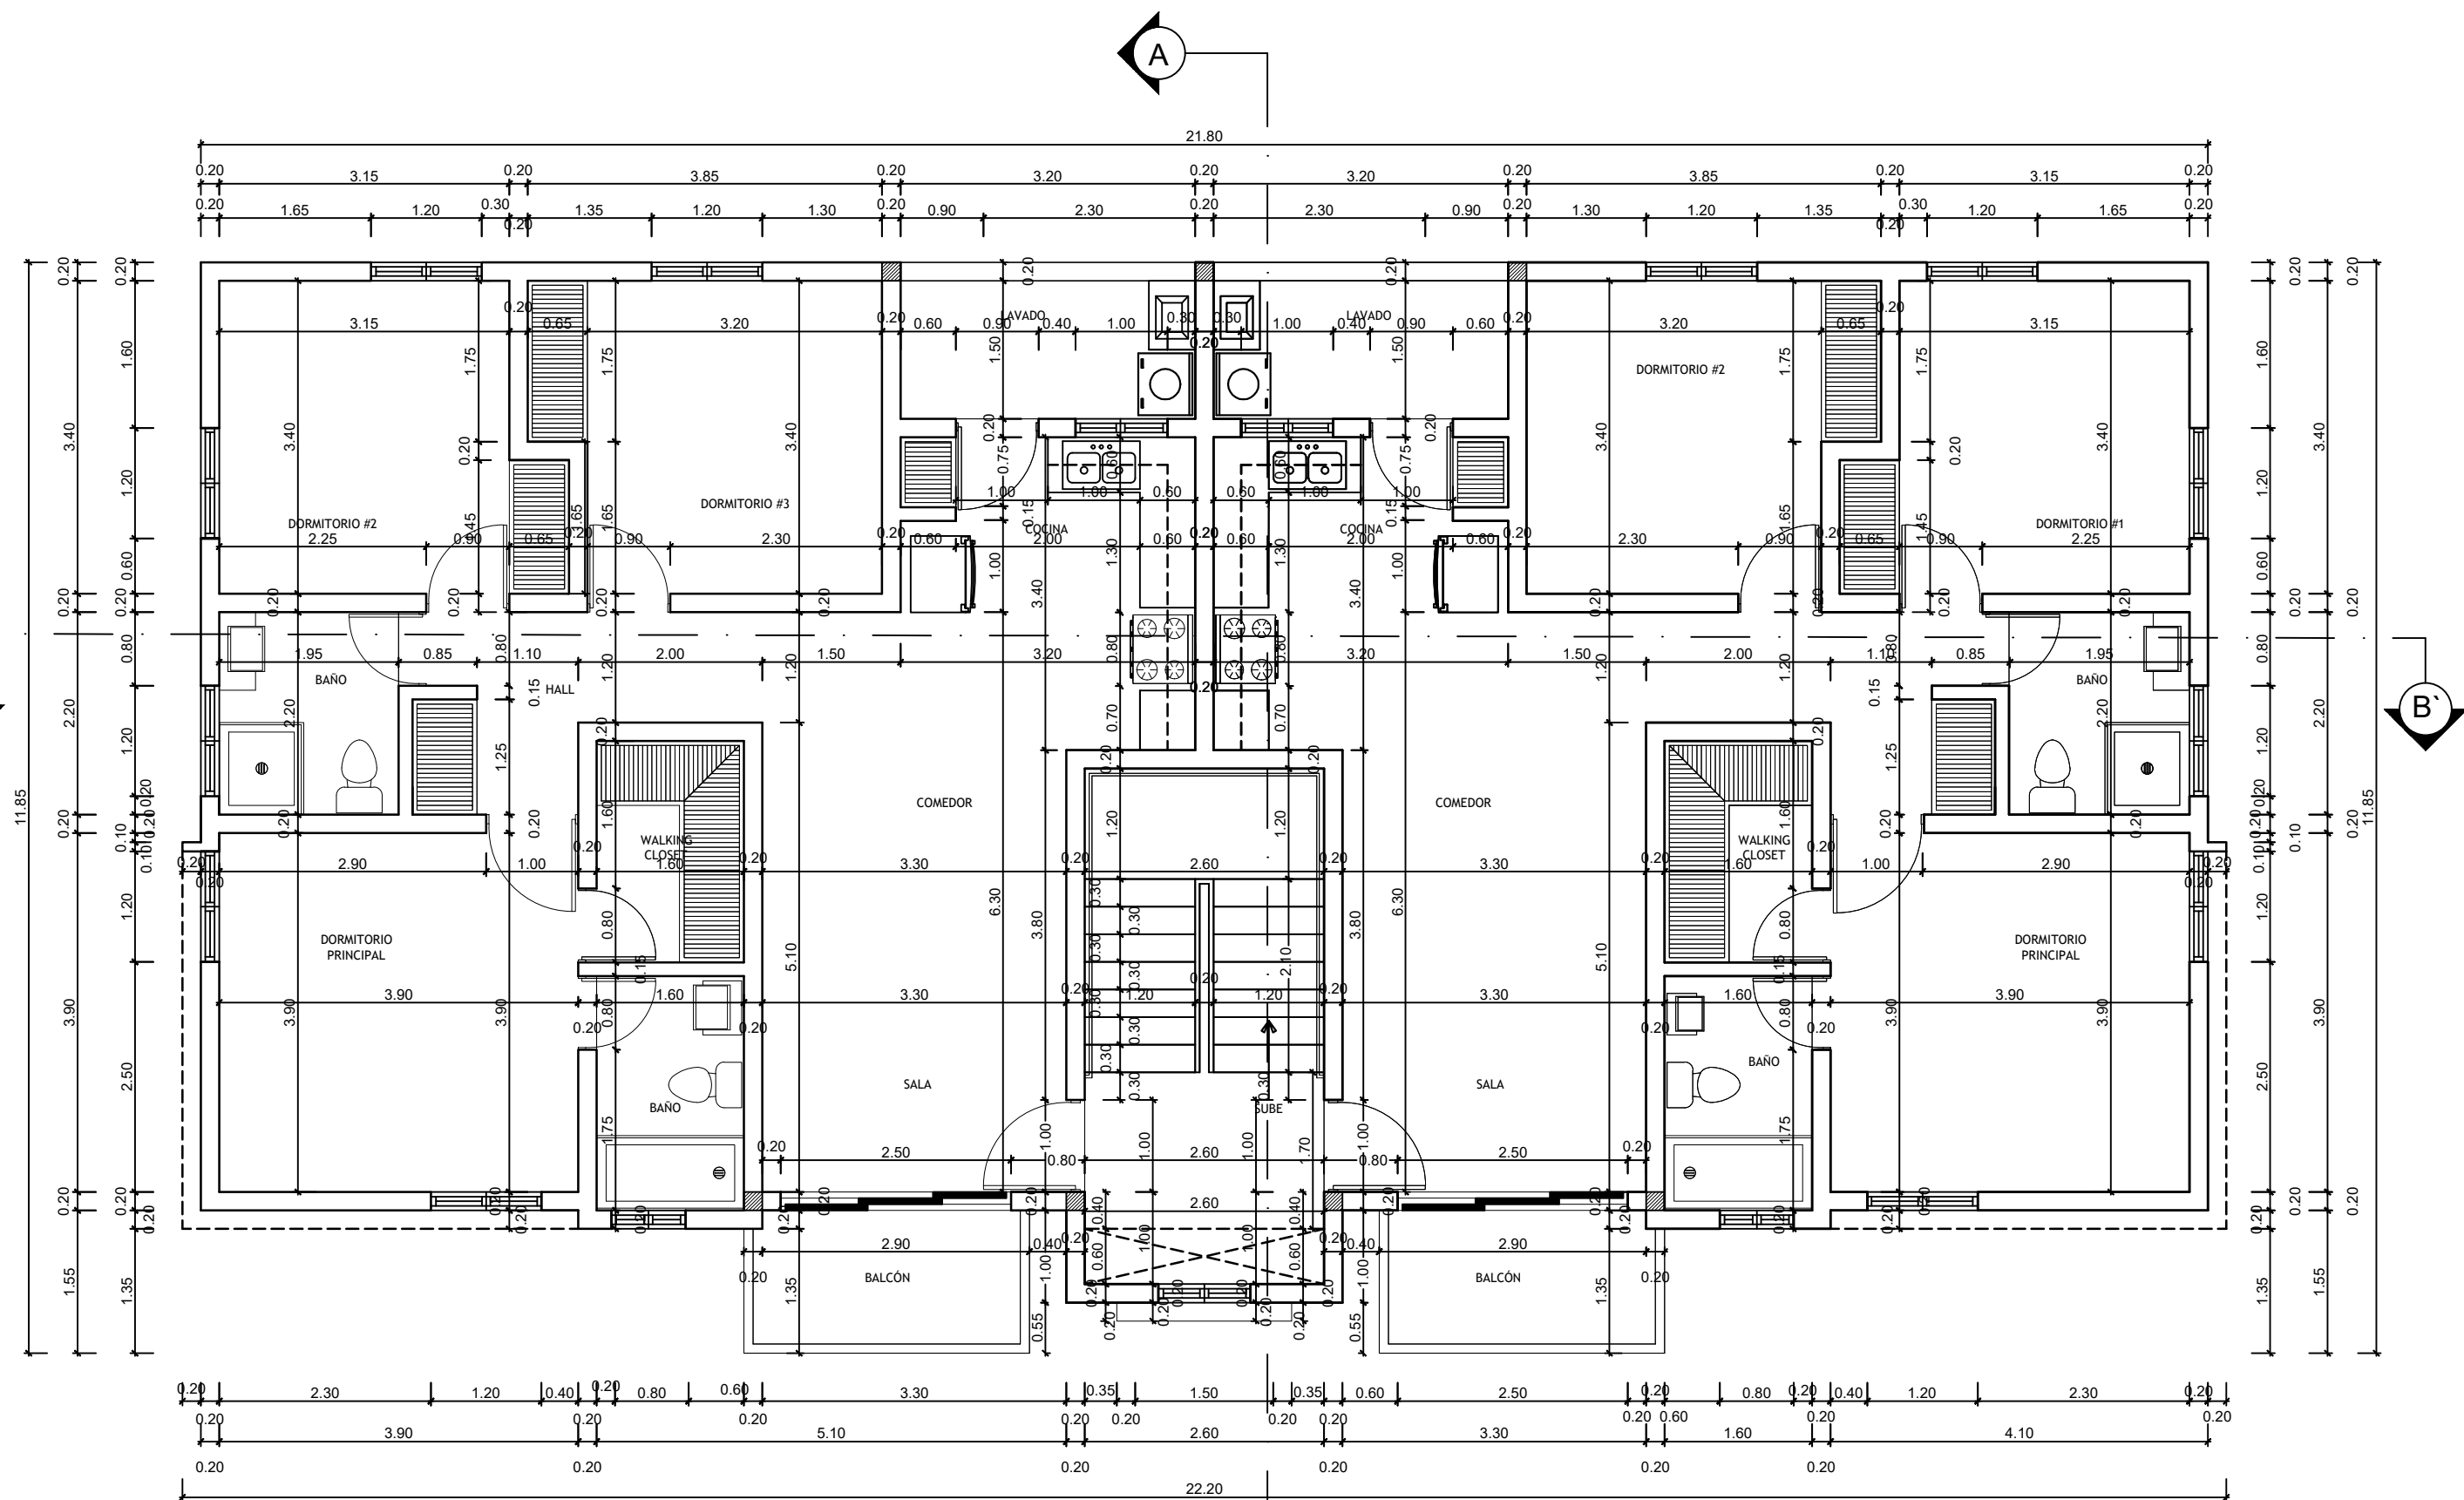

PLANTA DIMENSIONADA 2DO. NIVEL, BLOQUE B
ESCALA: 1:75

2


A09

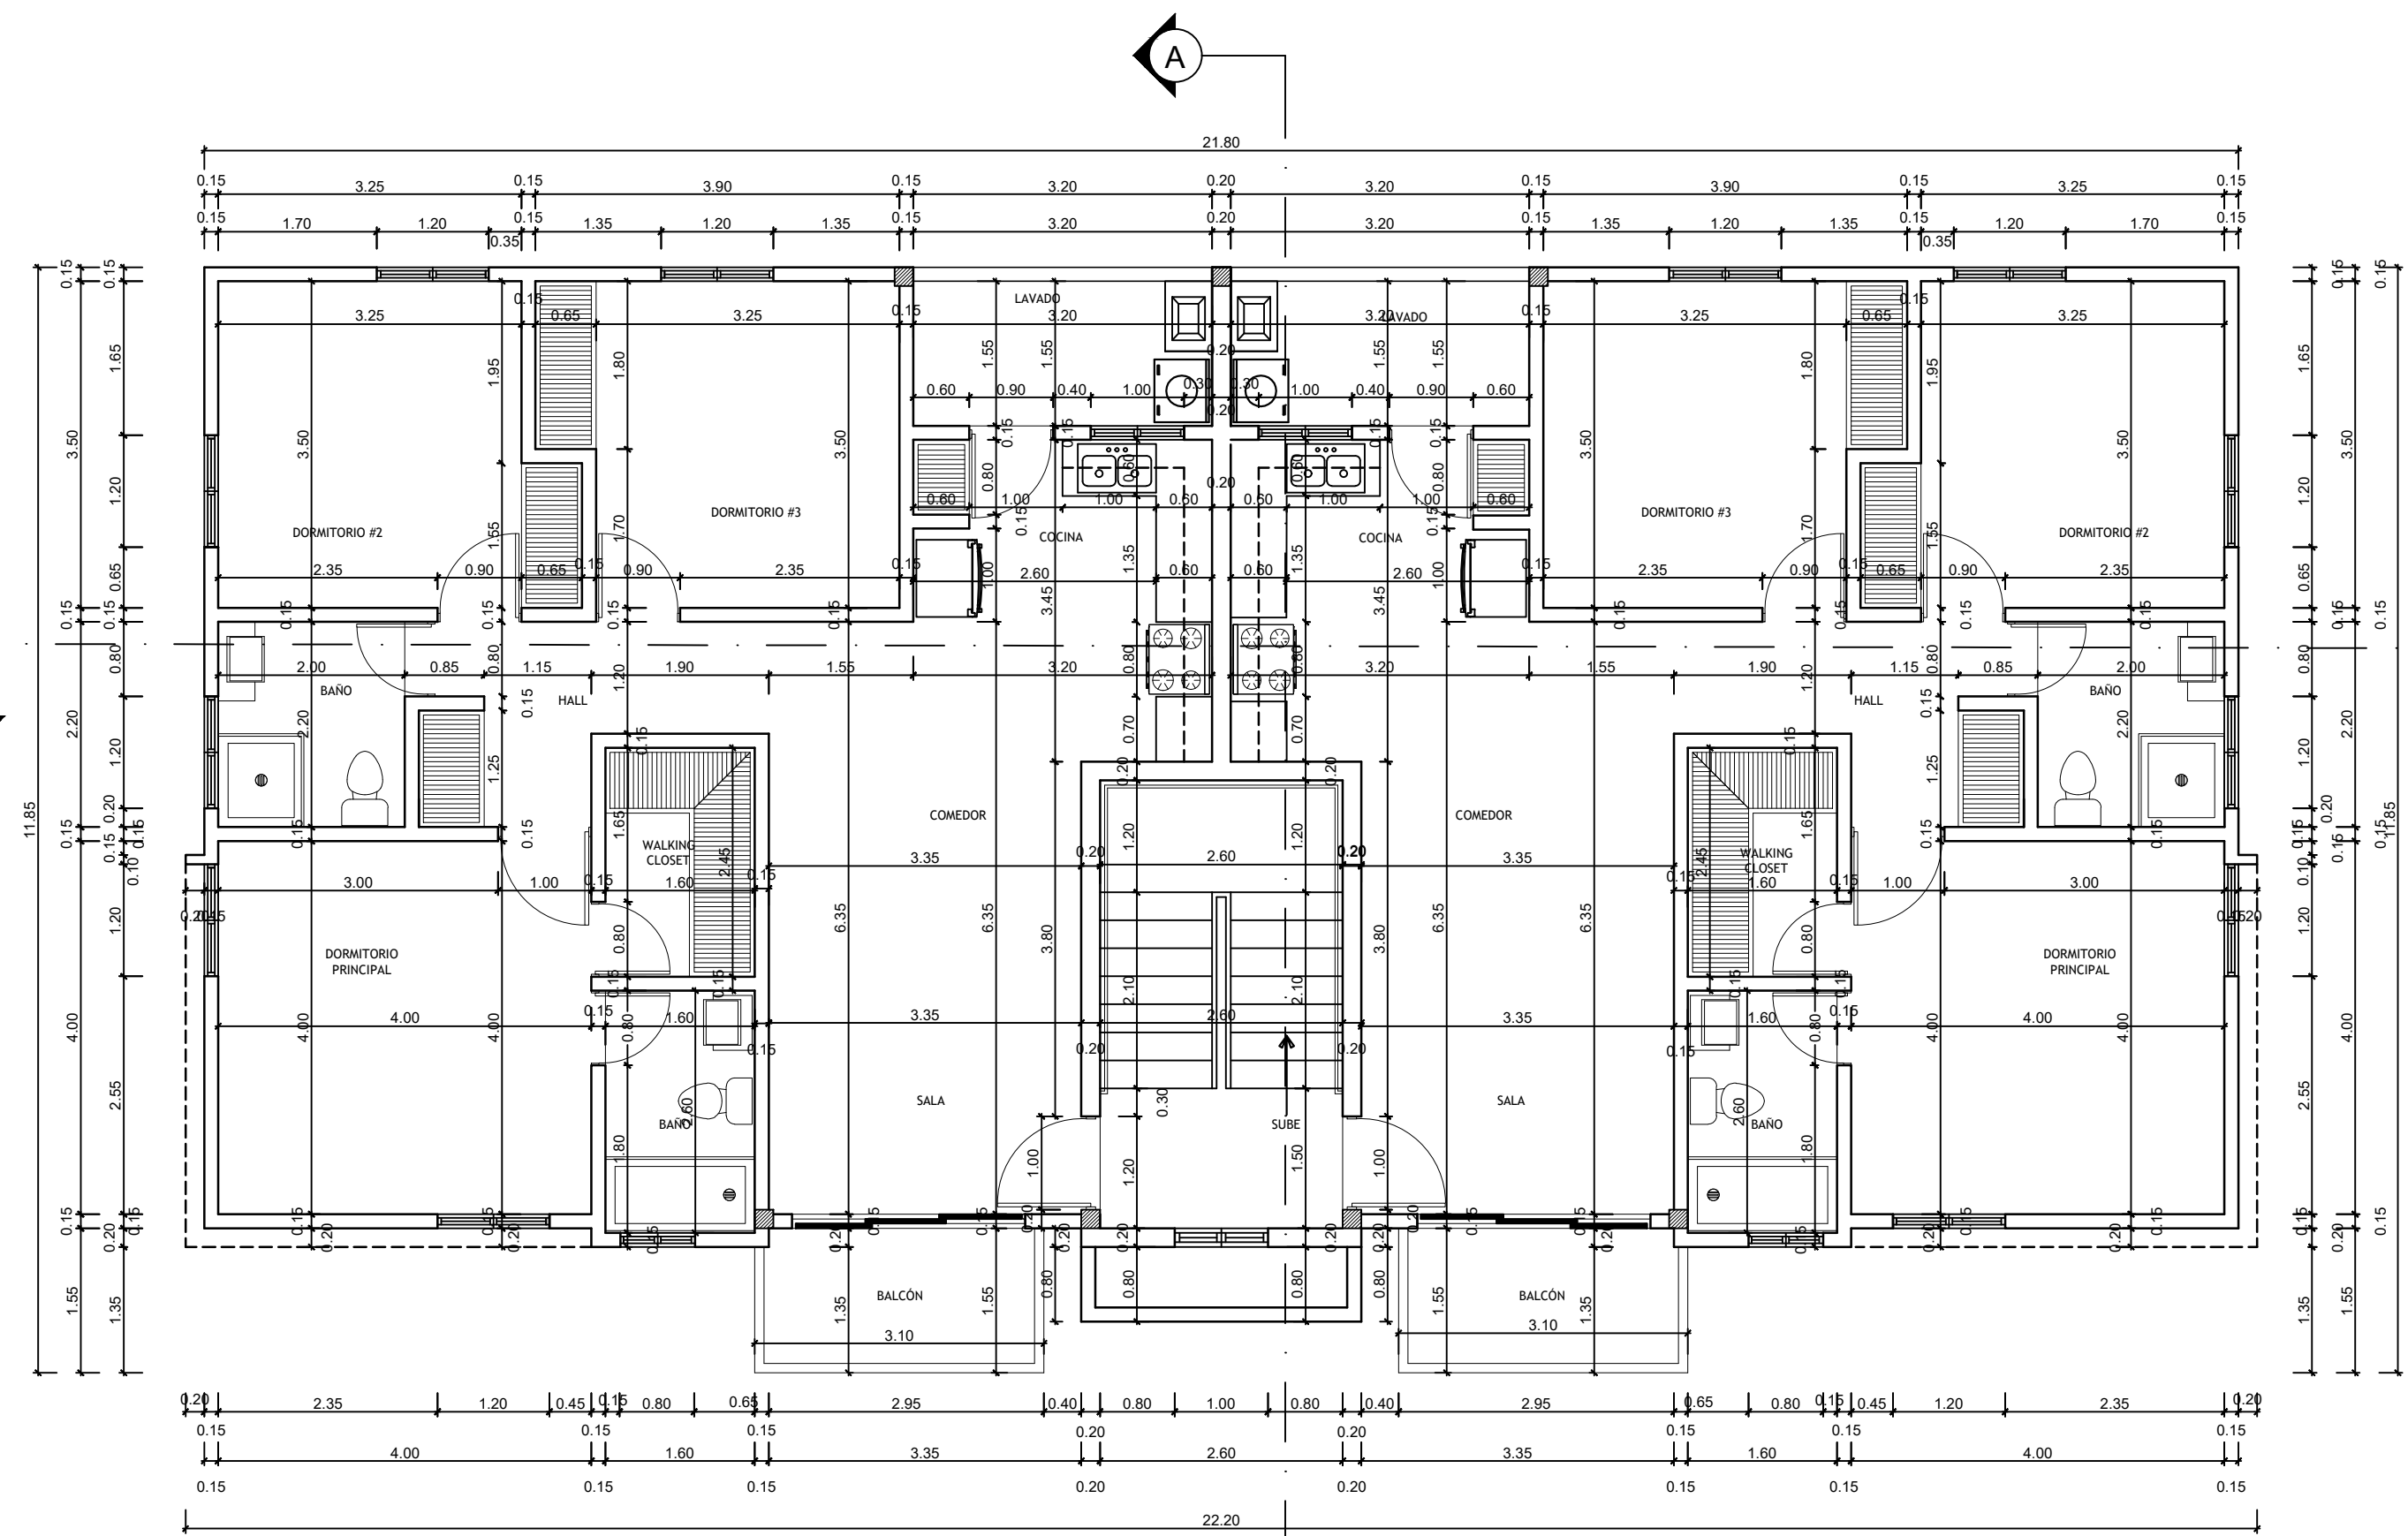

PLANTA DIMENSIONADA 3ER. NIVEL, BLOQUE B
ESCALA: 1:75


3

A09

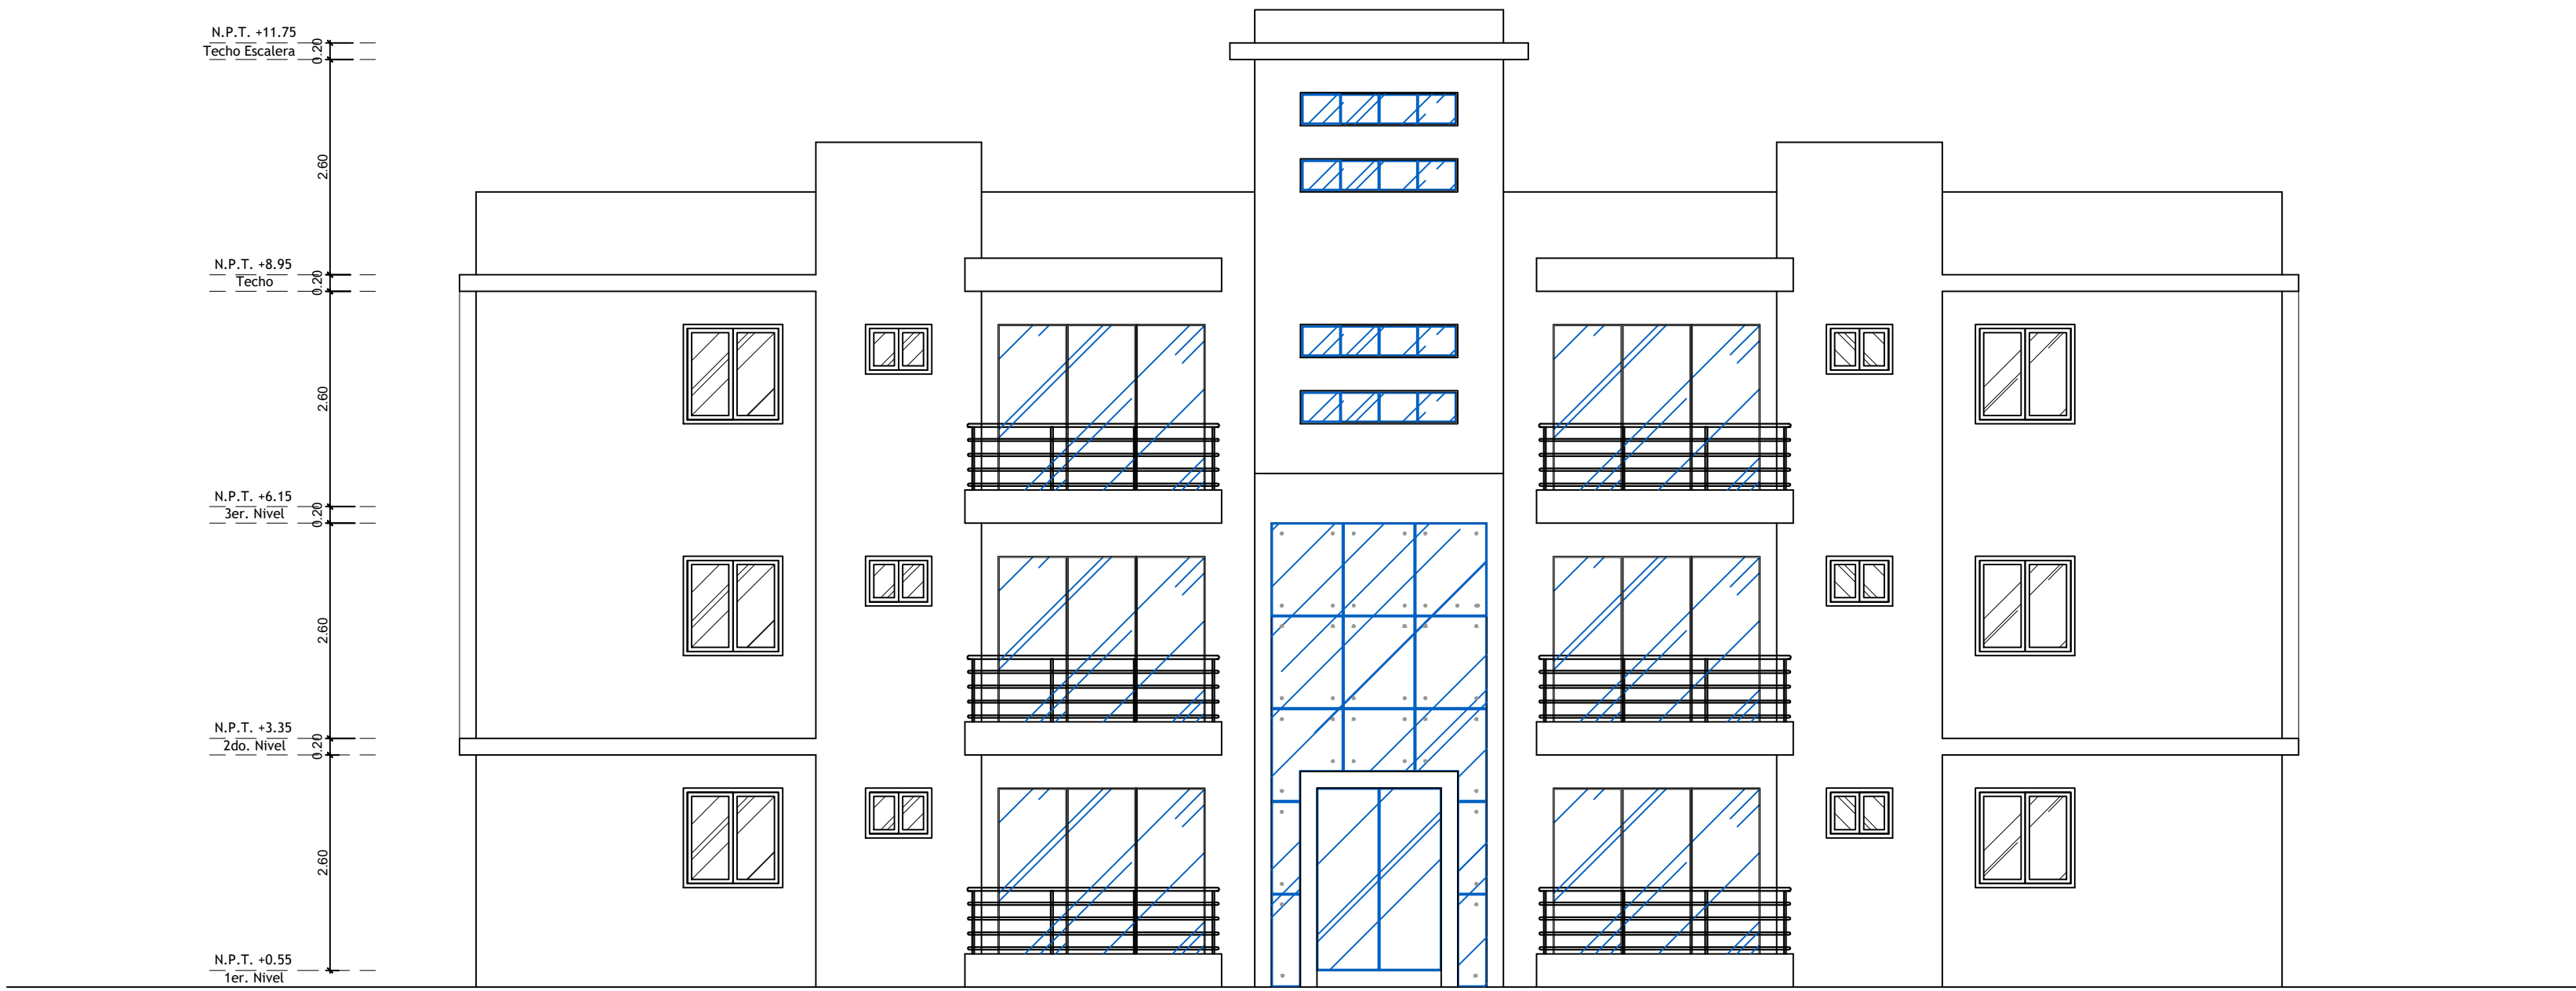


ELEVACION FRONTAL, BLOQUE B
ESCALA: 1:75

1
A10

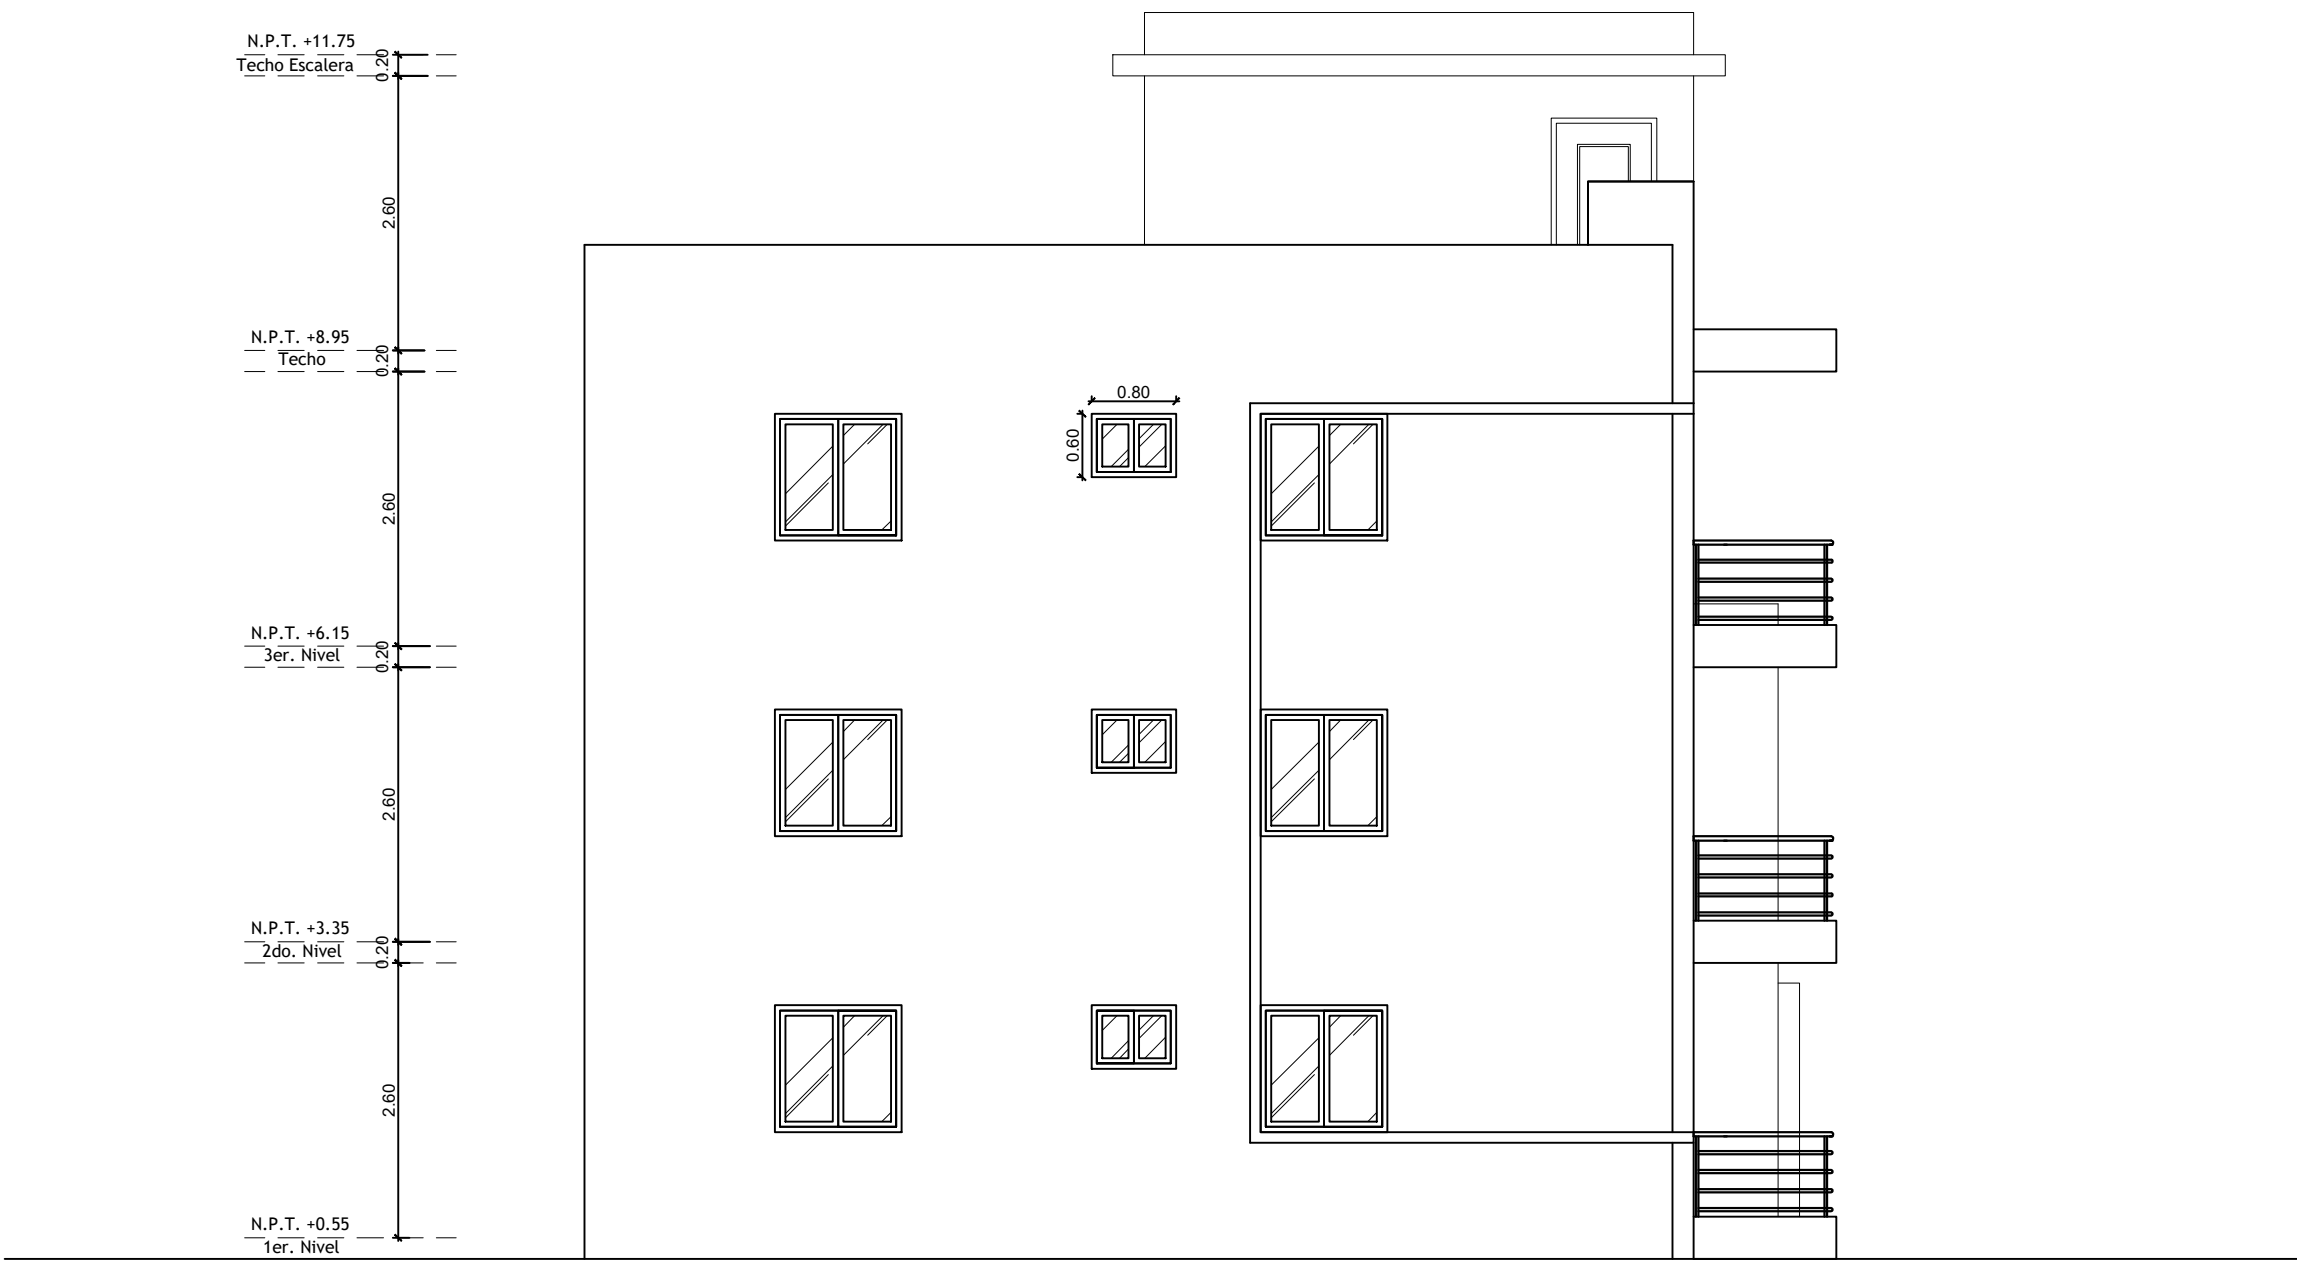

ELEVACION LATERAL IZQUIERDO, BLOQUE B
ESCALA: 1:75

2
A10

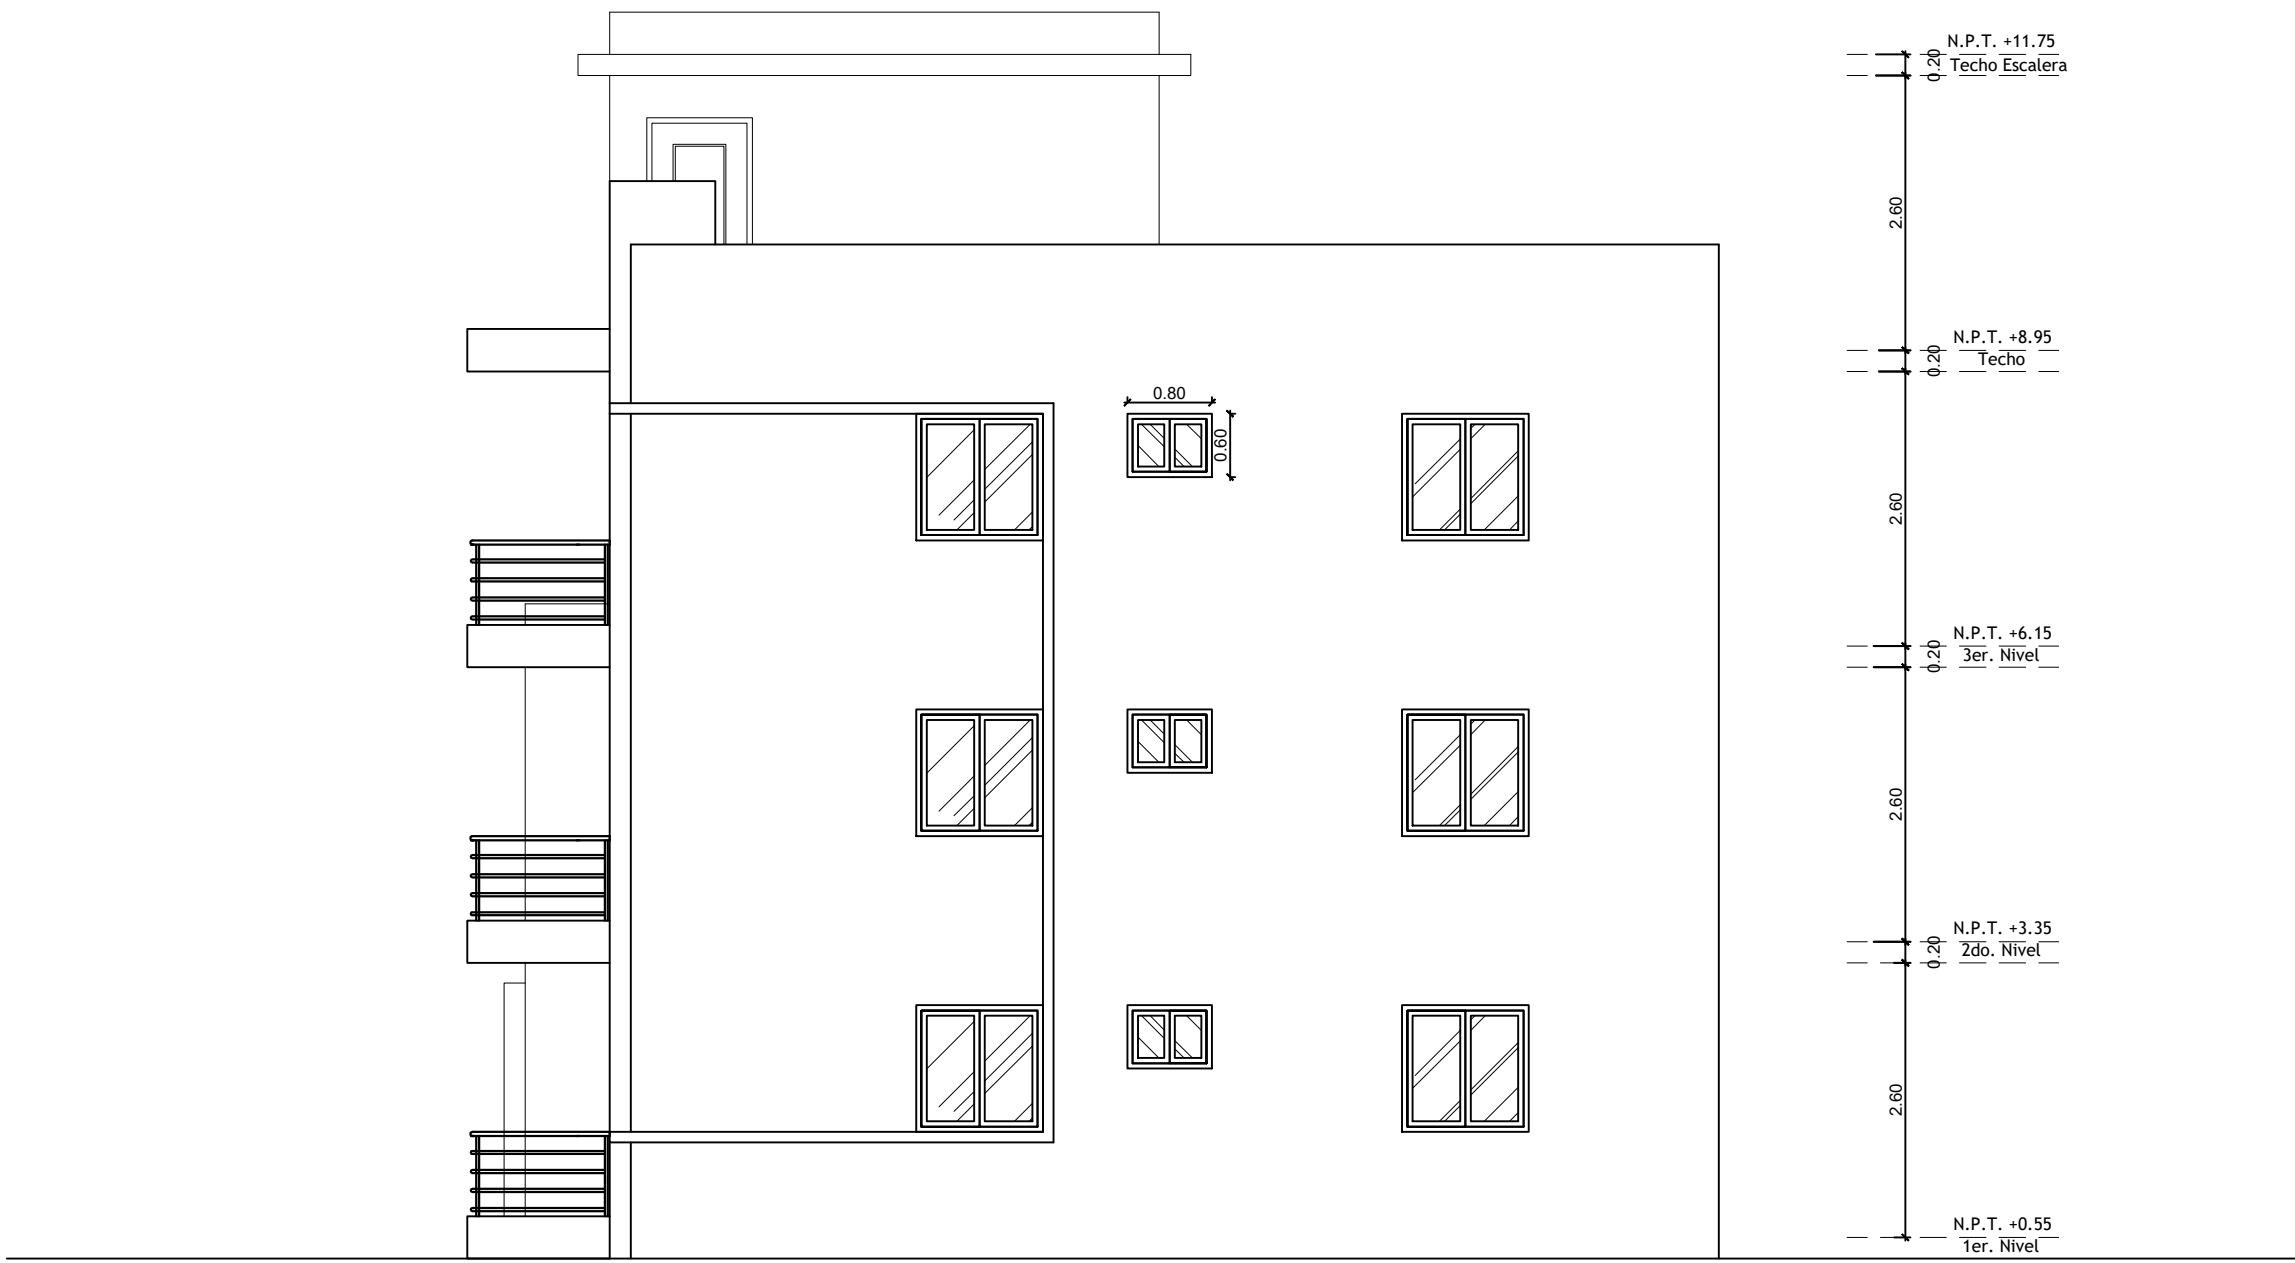

ELEVACION LATERAL DERECHO, BLOQUE B
ESCALA: 1:75

3
A10



ELEVACION POSTERIOR, BLOQUE B
ESCALA: 1:75

4
A10



diazmelo & asocs.
ARQUITECTOS
Presidente Billini # 12, Bani, R.D. 522-4989
E-mail: diazmelo@hotmail.com

COLABORACION:



ARQUITECTURA DIGITAL
DISEÑOS-CONSTRUCCION-DIGITACION
COMPROMETIDOS CON SU TIEMPO
C/JUAN SANCHEZ RAMIREZ #56,
LOCAL 5 ZONA UASD TEL:221-5400

PROPIETARIO :
GRUPO EMPRESARIAL
BANILEJO S.R.L.
GEBSA

PROYECTISTAS:

DISEÑO ARQUITECTONICO:
DIAZMELO & ASOCS.
Arq. ISMAEL DIAZ MELO
Codia: 9604

DISEÑO SANITARIO:
Arq. HAMLET TEJEDA
Codia: 18303

DISEÑO ESTRUCTURAL:
ING. ODELIN TEJEDA
Codia: 23937

DISEÑO ELECTRICO:
ING. VILLYS SANCHEZ
Codia: 19060

CONTENIDO:
ELEVACIONES
BLOQUE B

PROYECTO:
RESIDENCIAL GEBSA IV


Fecha: MAYO/2018

UBICACION:
BANI, PROV. PERAVIA

Ref.: Acad 2000
Escala: INDICADA


Hoja No.

NOTAS:
TODAS LAS TERMINACIONES Y/O CAMBIOS EN EL SET. DE DOCUMENTOS CONSTRUCTIVOS DEBERAN SER APROBADOS POR EL SUPERVISOR PREVIAMENTE A SU APLICACION EN LA OBRA.
TODAS LAS MEDIDAS DE huecos Y DE SUPERFICIE A SER REVESTIDAS SERAN RECTIFICADAS PREVIA FABRICACION DE LOS CIERRES O LA O LA INSTALACION DE LOS RECURRIMIENTOS
LAS TERMINACIONES Y/O DETALLES NO ESPECIFICADOS SERAN DEFINIDOS ENTRE:
EL DUEÑO Y EL AUTOR DEL PROYECTO.
EL CONTRATISTA NO PODRA TOMAR DECISIONES INCONSULTAS RESPECTO VARIACIONES EN EL CONTENIDO DE ESTE DOCUMENTO
LOS PLANOS ARQUITECTONICOS MANDARAN RESPECTO A LOS DEMAS A DIFERENCIA PRIMARA LA INFORMACIONCONTENIDA EN LOS MISMOS

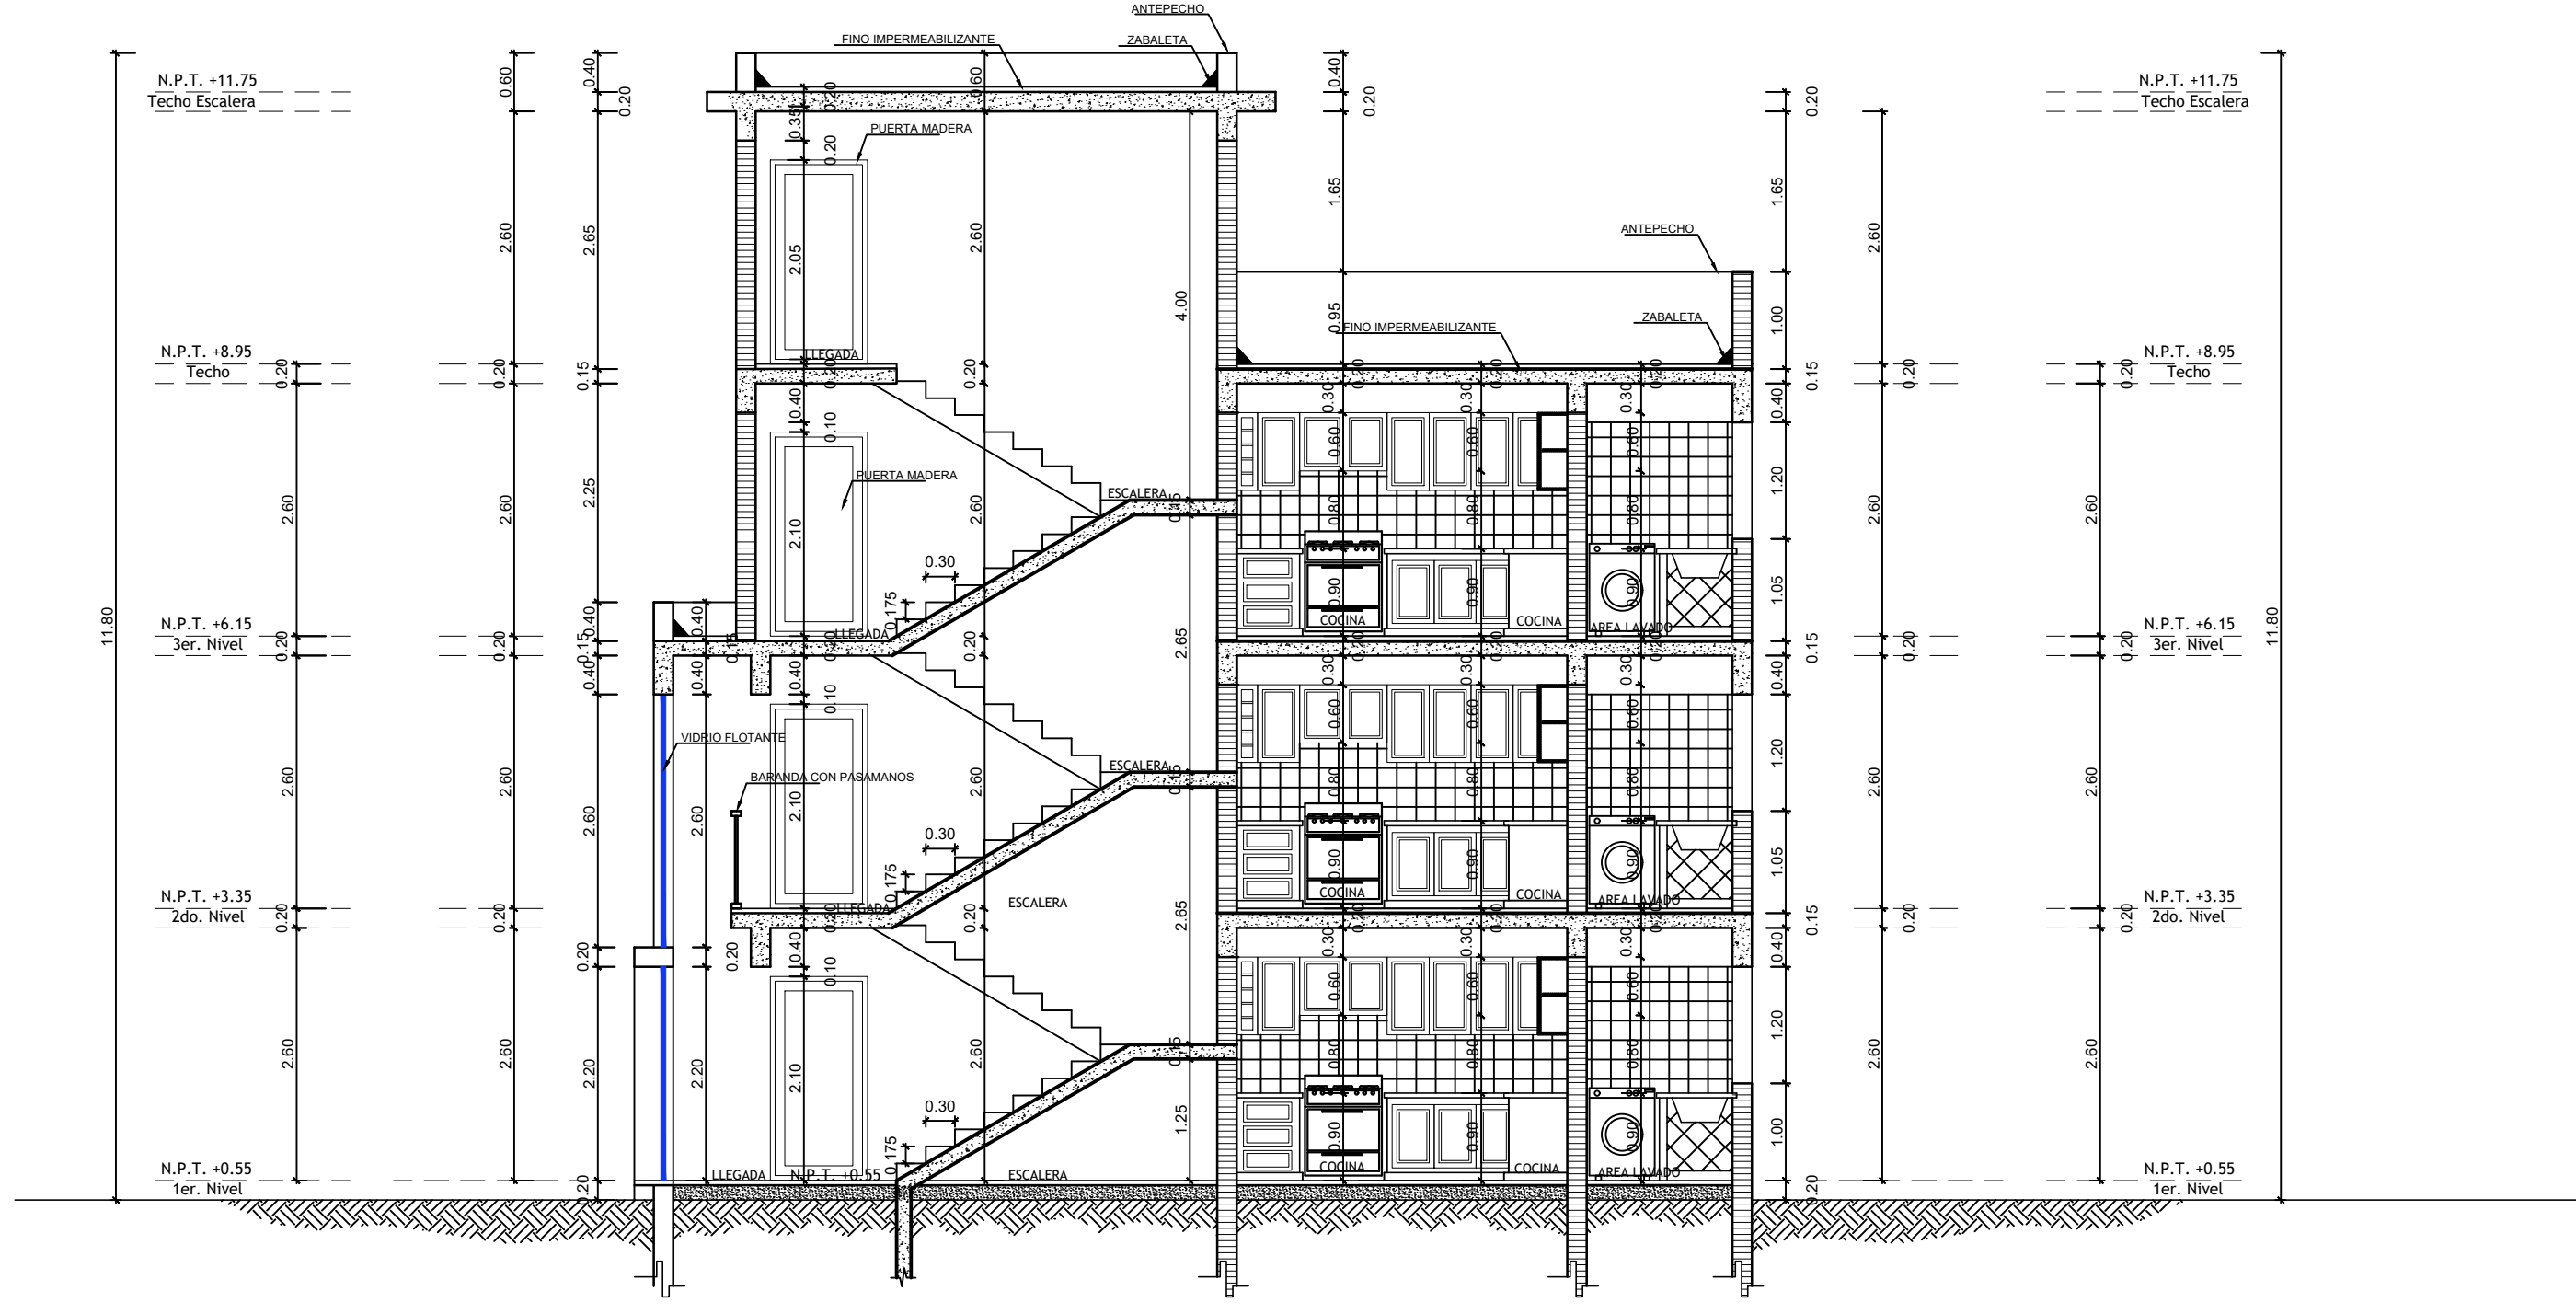

SECCION A-A', BLOQUE B
ESCALA: 1:75

1
A11

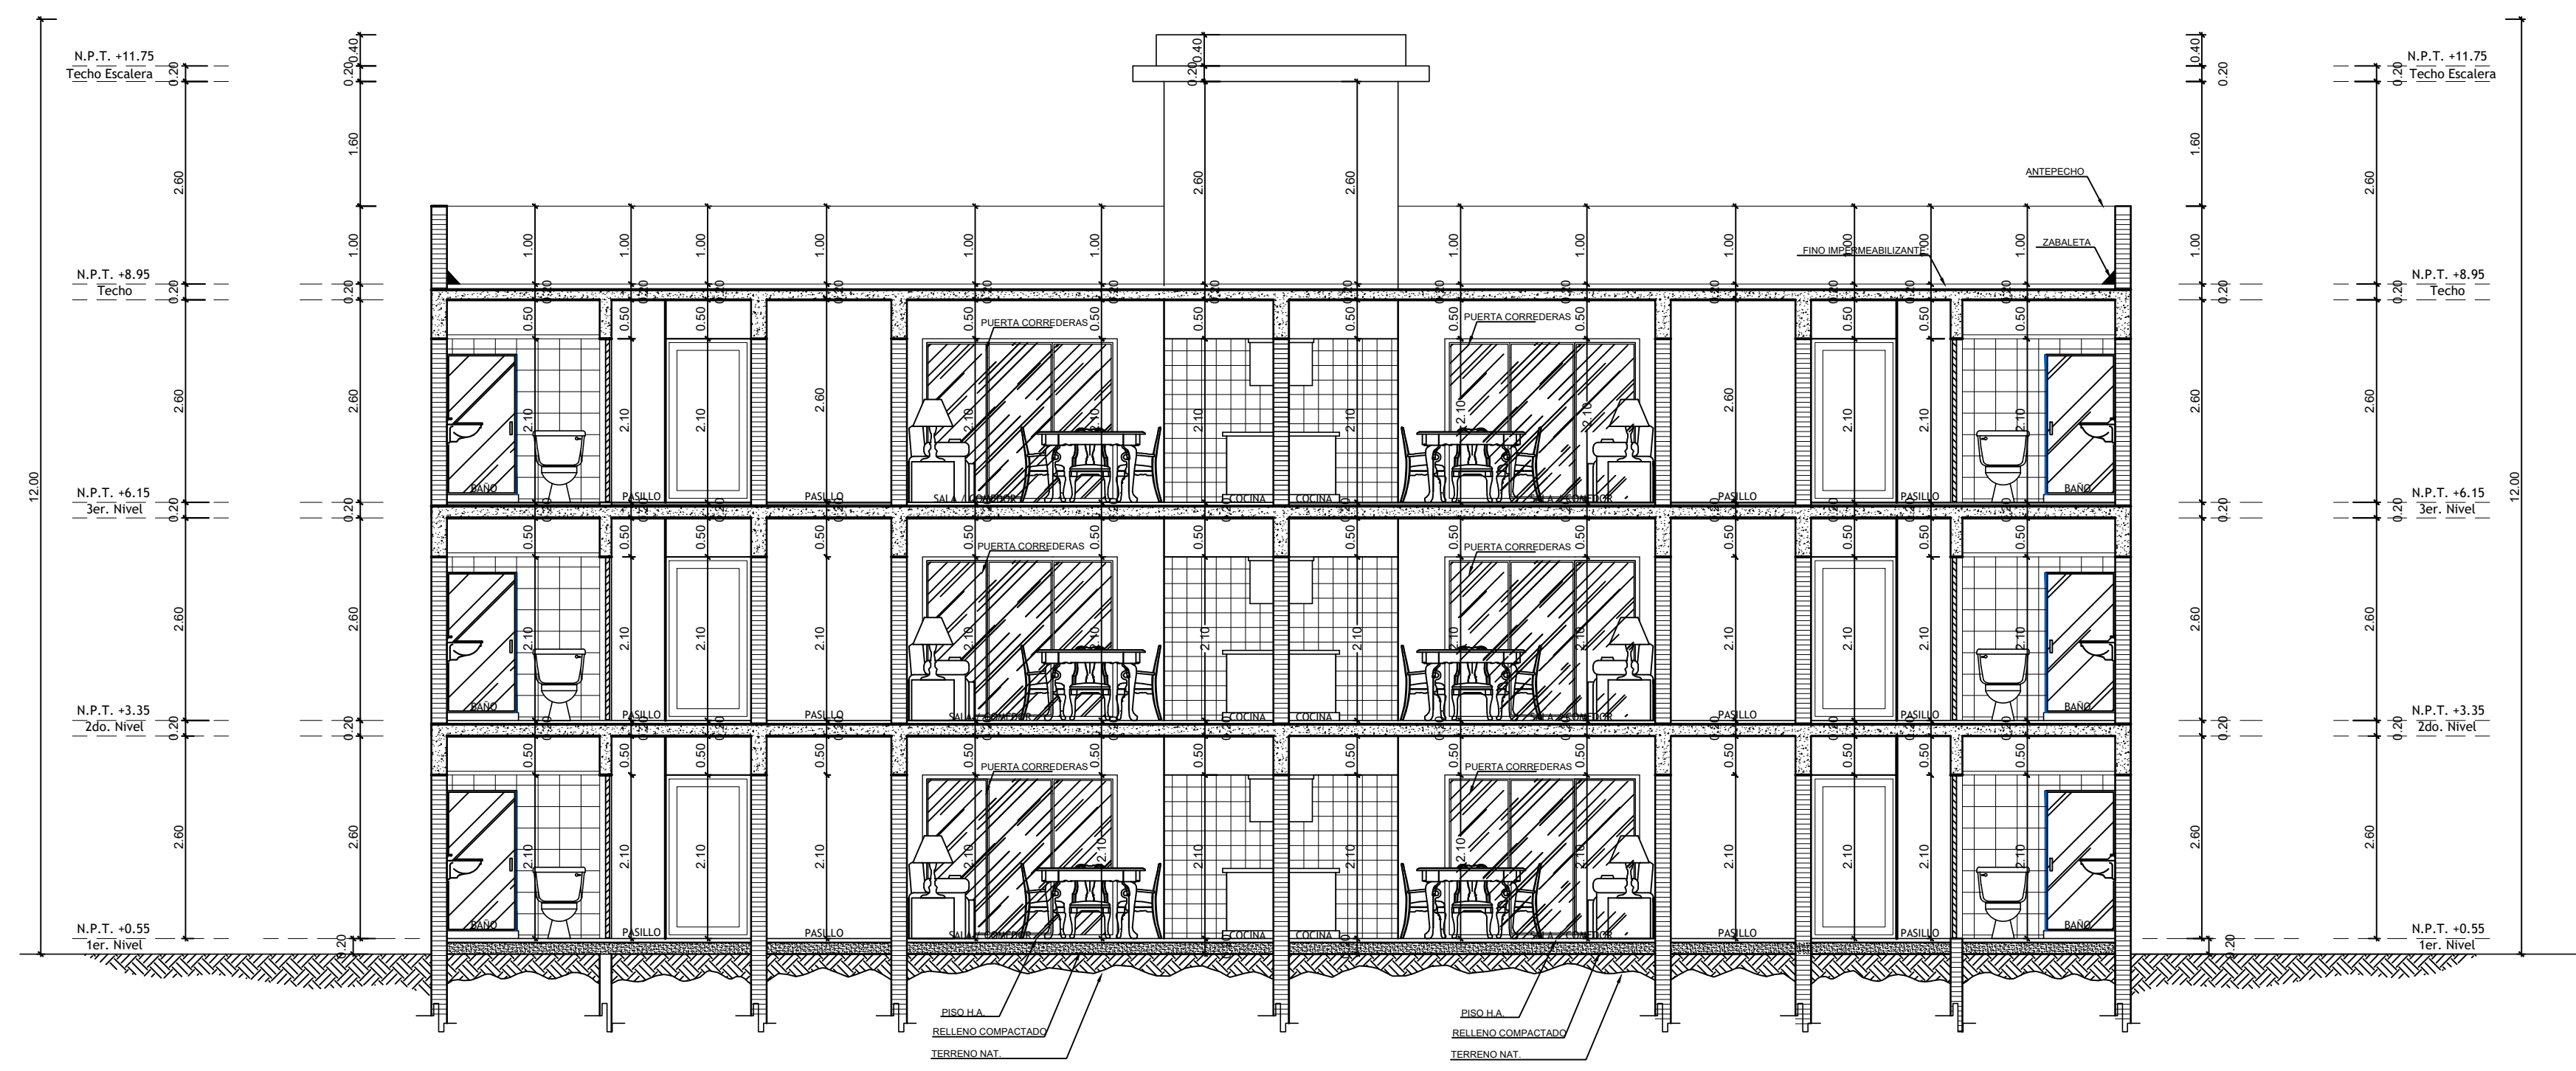

SECCION B-B', BLOQUE B
ESCALA: 1:75

2
A11



diazmelo & asocs.
ARQUITECTOS
Presidente Billini # 12, Bani, R.D. 522-4989
E-mail: diazmelo@hotmail.com

COLABORACION:



ARQUITECTURA DIGITAL
DISEÑOS-CONSTRUCCION-DIGITACION
COMPROMETIDOS CON SU TIEMPO
C/JUAN SANCHEZ RAMIREZ #56,
LOCAL 5 ZONA UASD TEL:221-5400

PROPIETARIO :
**GRUPO EMPRESARIAL
BANILEJO S.R.L.
GEBSA**

PROYECTISTAS:

DISEÑO ARQUITECTONICO:
DIAZMELO & ASOCS.
Arq. ISMAEL DIAZ MELO
Codia: 9604

DISEÑO SANITARIO:
Arq. HAMLET TEJEDA
Codia: 18303

DISEÑO ESTRUCTURAL:
ING. ODELIN TEJEDA
Codia: 23937

DISEÑO ELECTRICO:
ING. VILLYS SANCHEZ
Codia: 19060

CONTENIDO:
**SECCIONES
BLOQUE B**

PROYECTO:
RESIDENCIAL GEBSA IV


Fecha: MAYO/2018

UBICACION:
BANI, PROV. PERAVIA

Ref.: Acad 2000 Hoja No.
Escala: INDICADA

NOTAS:
TODAS LAS TERMINACIONES Y/O CAMBIOS EN EL SET. DE DOCUMENTOS CONSTRUCTIVOS DEBERAN SER APROBADOS POR EL SUPERVISOR PREVIAMENTE. A SU APLICACION EN LA OBRA.
TODAS LAS MEDIDAS DE MUROS Y DE SUPERFICIE A SER REVESTIDAS SERAN RECTIFICADAS PREVIA FABRICACION DE LOS CIERRES O LA O LA INSTALACION DE LOS RECURRIMIENTOS
LAS TERMINACIONES Y/O DETALLES NO ESPECIFICADOS SERAN DEFINIDOS ENTRE:
EL DUENO Y EL AUTOR DEL PROYECTO.
EL CONTRATISTA NO PODRA TOMAR DECISIONES INCONSULTAS RESPECTO VARIACIONES EN EL CONTENIDO DE ESTE DOCUMENTO

LOS PLANOS ARQUITECTONICOS MANDARAN RESPECTO A LOS DEMAS A DIFERENCIA PRIMARA LA INFORMACION/CONTENIDO EN LOS MISMOS

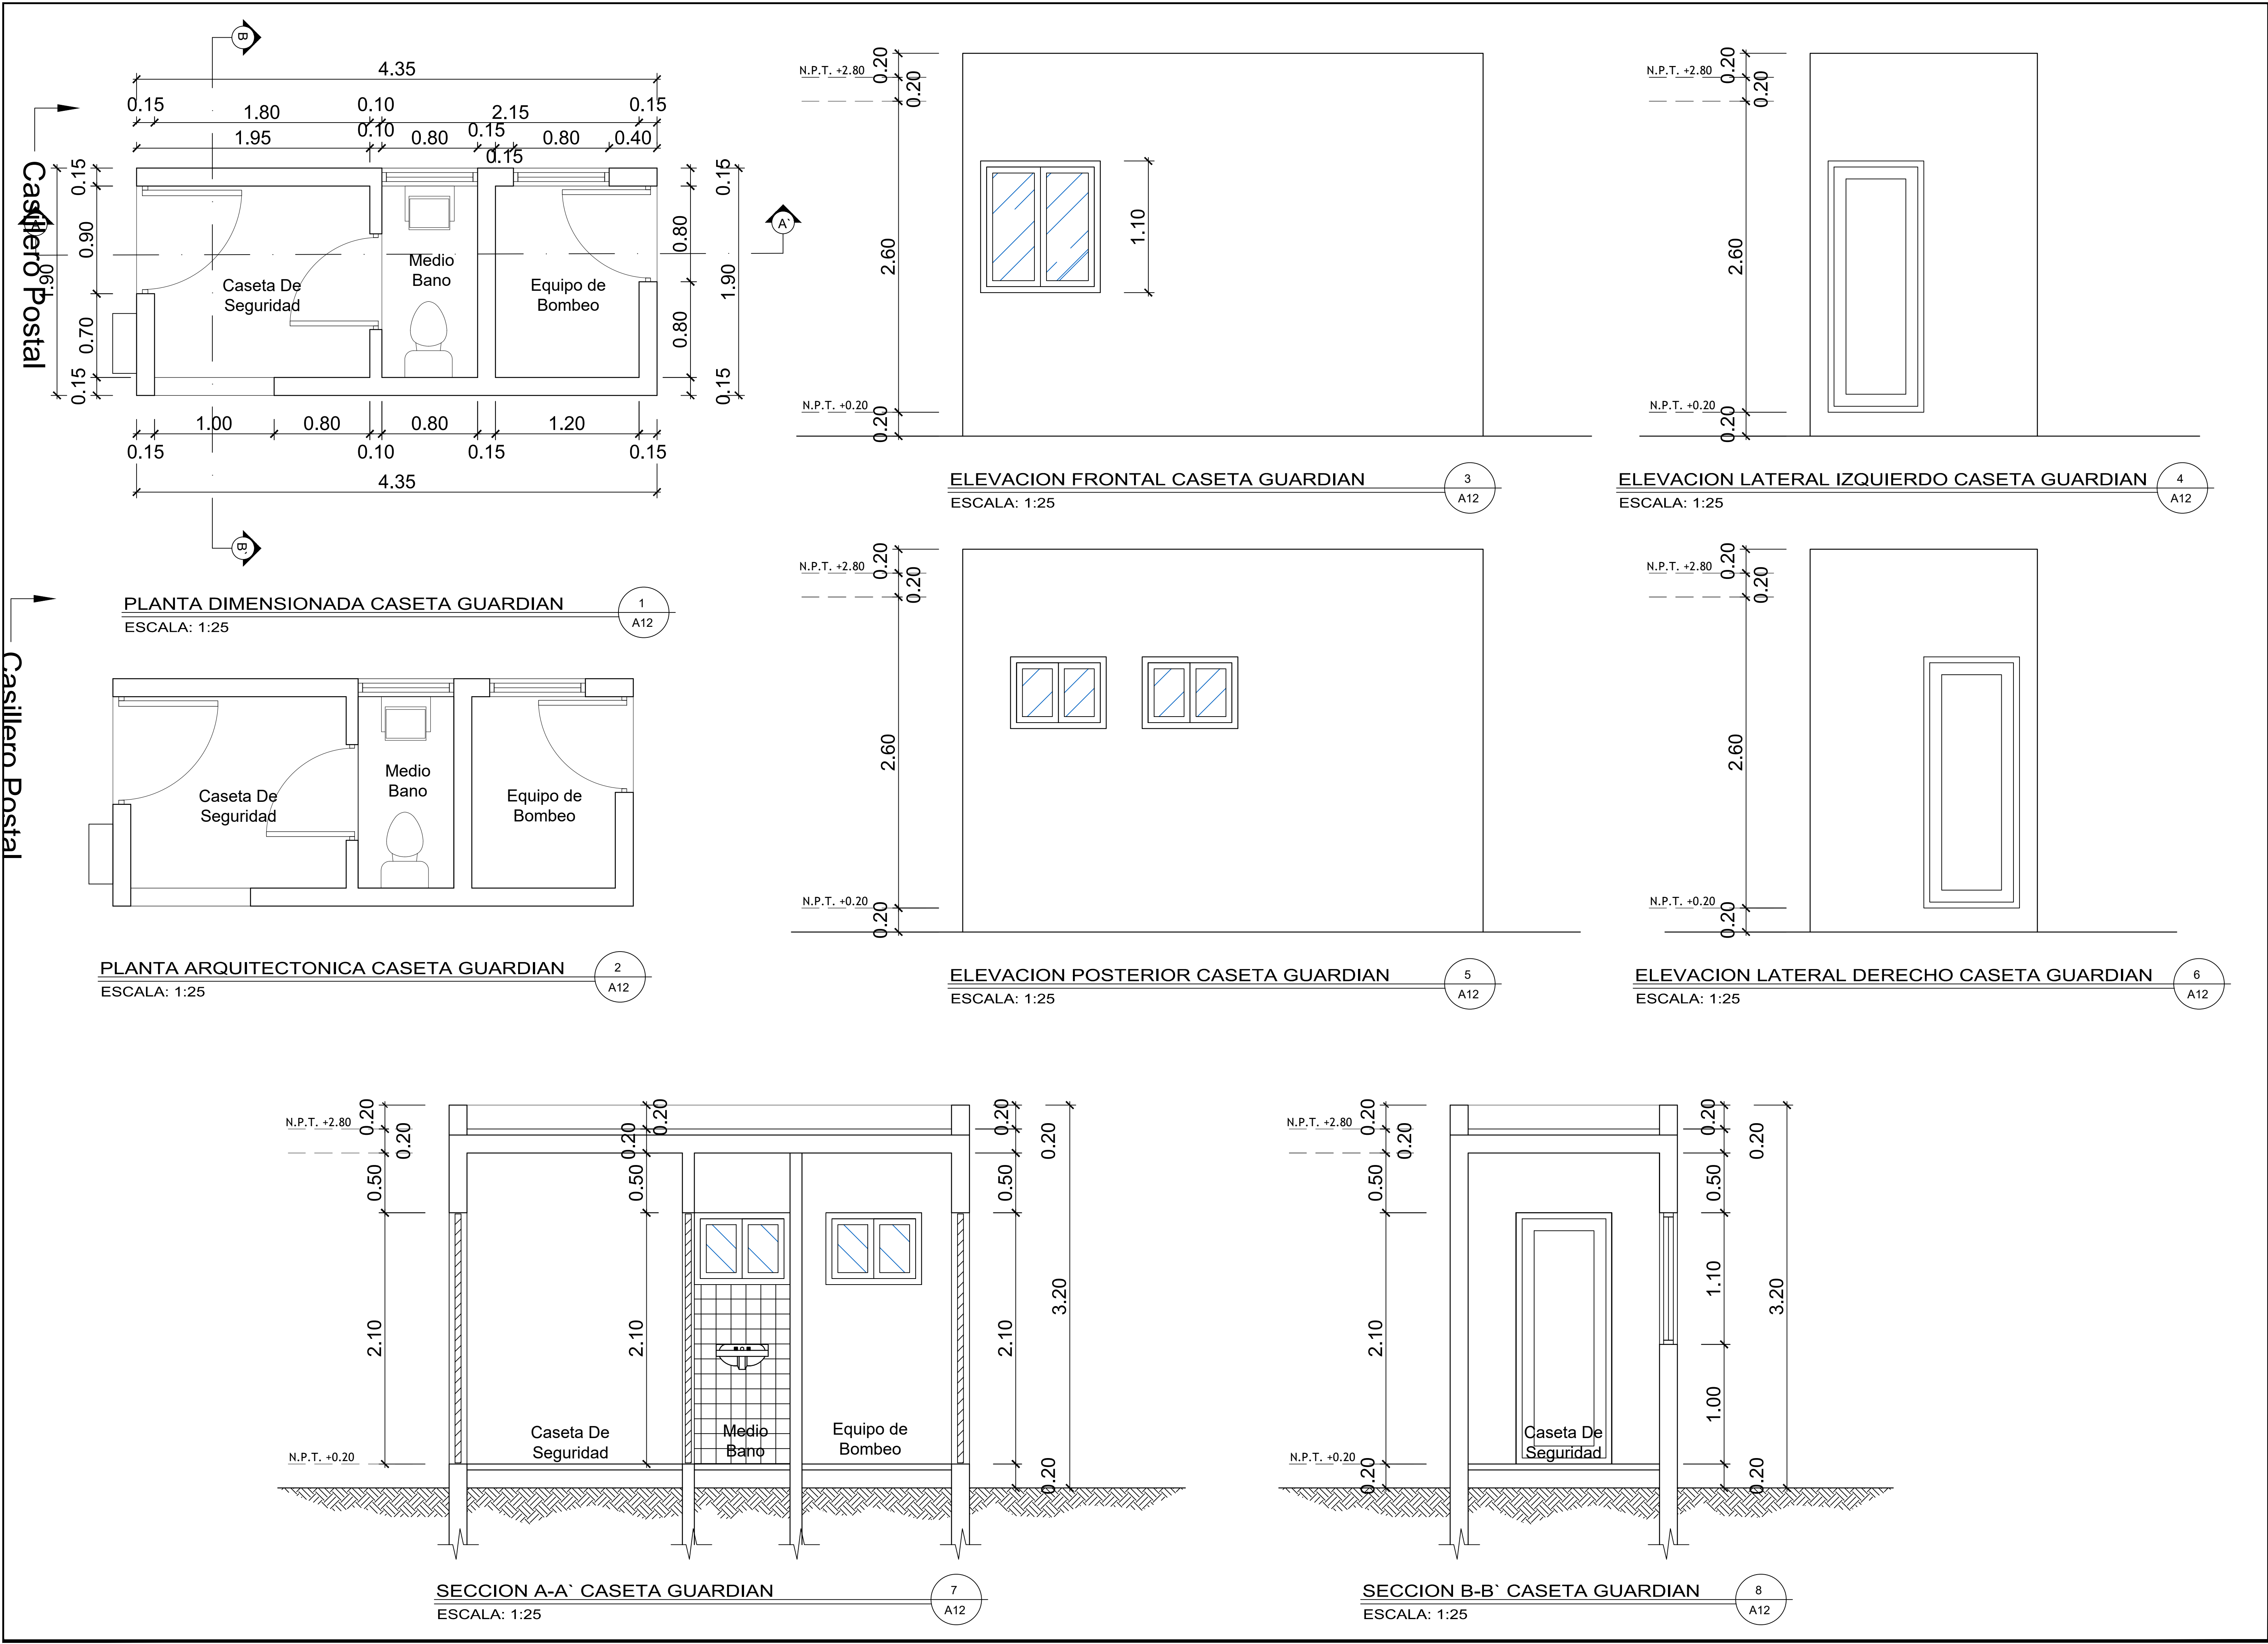

diazmelo & asocs.

ARQUITECTOS

Presidente Billini # 12, Bani, R.D. 522-4989

E-mail: diazmelo@hotmail.com

COLABORACION:



ARQUITECTURA DIGITAL
DISEÑOS-CONSTRUCCION-DIGITACION
COMPROMETIDOS CON SU TIEMPO
C/ JUAN SANCHEZ RAMIREZ #56,
LOCAL 5 ZONA UASD TEL:221-5400

PROPIETARIO :

GRUPO EMPRESARIAL

BANILEJO S.R.L.

GEBSA

PROYECTISTAS:

DISEÑO ARQUITECTONICO:

DIAZMELO & ASOCS.

Arq. ISMAEL DIAZ MELO

Codia: 9604

DISEÑO SANITARIO:

Arq. HAMLET TEJEDA

Codia: 18303

DISEÑO ESTRUCTURAL:

ING. ODELIN TEJEDA

Codia: 23937

DISEÑO ELECTRICO:

ING. VILLYS SANCHEZ

Codia: 19060

CONTENIDO:

DETALLE CASETA DE PLANTA
Y EQUIPO DE BOMBEO

PROYECTO:

RESIDENCIAL GEBSA IV

Fecha: MAYO/2018

UBICACION:

BANI, PROV. PERAVIA

Ref.: Acad 2000

Escala: INDICADA

Hoja No.

NOTAS:
TODAS LAS TERMINACIONES Y/O CAMBIOS EN EL SET. DE DOCUMENTOS
CONSTRUCTIVOS DEBERAN SER APROBADOS POR EL SUPERVISOR
PREVIAMENTE A SU APLICACION EN LA OBRA

TODAS LAS MEDIDAS DE MUROS Y DE SUPERFICIE A SER REVESTIDAS
SERAN RECTIFICADAS PREVIA FABRICACION DE LOS CIERRES O LA
O LA INSTALACION DE LOS RECURRIMIENTOS

LAS TERMINACIONES Y/O DETALLES NO ESPECIFICADOS SERAN
DEFINIDOS ENTRE:

EL DUEÑO Y EL AUTOR DEL PROYECTO

EL CONTRATISTA NO PODRA TOMAR DECISIONES
INCONSULTAS RESPECTO A VARIACIONES EN EL CONTENIDO
DE ESTE DOCUMENTO

LOS PLANOS ARQUITECTONICOS MANDARAN RESPECTO A LOS DEMAS A

ANTE CUALQUIER DIFERENCIA PRIMARA LA INFORMACION/CONTENIDO EN LOS MISMOS