



diaz melo & asocs.
ARQUITECTOS

Presidente Billini # 12, Bani, R.D. 522-4989
E-mail: diazmelo@hotmail.com

COLABORACION:



ARQUITECTURA DIGITAL
DISEÑOS-CONSTRUCCION-DIGITACION
COMPROMETIDOS CON SU TIEMPO
C/JUAN SANCHEZ RAMIREZ #56,
LOCAL 5 ZONA UASD TEL:221-5400

PROPIETARIO:
**GRUPO EMPRESARIAL
BANILEJO S.R.L.
GEBSA**

PROYECTISTAS:

DISEÑO ARQUITECTONICO:
DIAZMELO & ASOCS.
Arq. ISMAEL DIAZ MELO
Codia: 9604

DISEÑO SANITARIO:
Arq. HAMLET TEJEDA
Codia: 18303

DISEÑO ESTRUCTURAL:
ING. ODELIN TEJEDA
Codia: 23937

DISEÑO ELECTRICO:
ING. VILLYS SANCHEZ
Codia: 19060

CONTENIDO:
**PLANTA SANITARIA DE
1ER. DEL CONJUNTO**

PROYECTO:
RESIDENCIAL GEBSA IV

Fecha: MARZO/2020

UBICACION:

SOMBRERO, BANI, PROV. PERAVIA



Ref.: Acad 2000

Hoja No.

Escala: INDICADA

4

NOTAS:
TODAS LAS TERMINACIONES Y/O CAMBIOS EN EL SET DE DOCUMENTOS CONSTRUCTIVOS DEBERAN SER APROBADOS POR EL SUPERVISOR PREVIAMENTE A SU APLICACION EN LA OBRA.
TODAS LAS MEDIDAS DE HUECOS Y DE SUPERFICIE A SER REVESTIDAS SERAN RECTIFICADAS PREVIA FABRICACION DE LOS CERRRES O LA O LA INSTALACION DE LOS RECURBIMIENTOS
LAS TERMINACIONES Y / O DETALLES NO ESPECIFICADOS SERAN DEFINIDOS ENTRE EL DUEÑO Y EL AUTOR DEL PROYECTO.
EL CONTRATISTA NO PODRA TOMAR DECISIONES INCONSULTAS RESPECTO VARIACIONES EN EL CONTENIDO DE ESTE DOCUMENTO
LOS PLANOS ARQUITECTONICOS MANDARAN RESPECTO A LOS DEMAS A ANTE CUALQUIER DIFERENCIA, PRIMARA LA INFORMACIONCONTENIDA EN LOS MISMOS

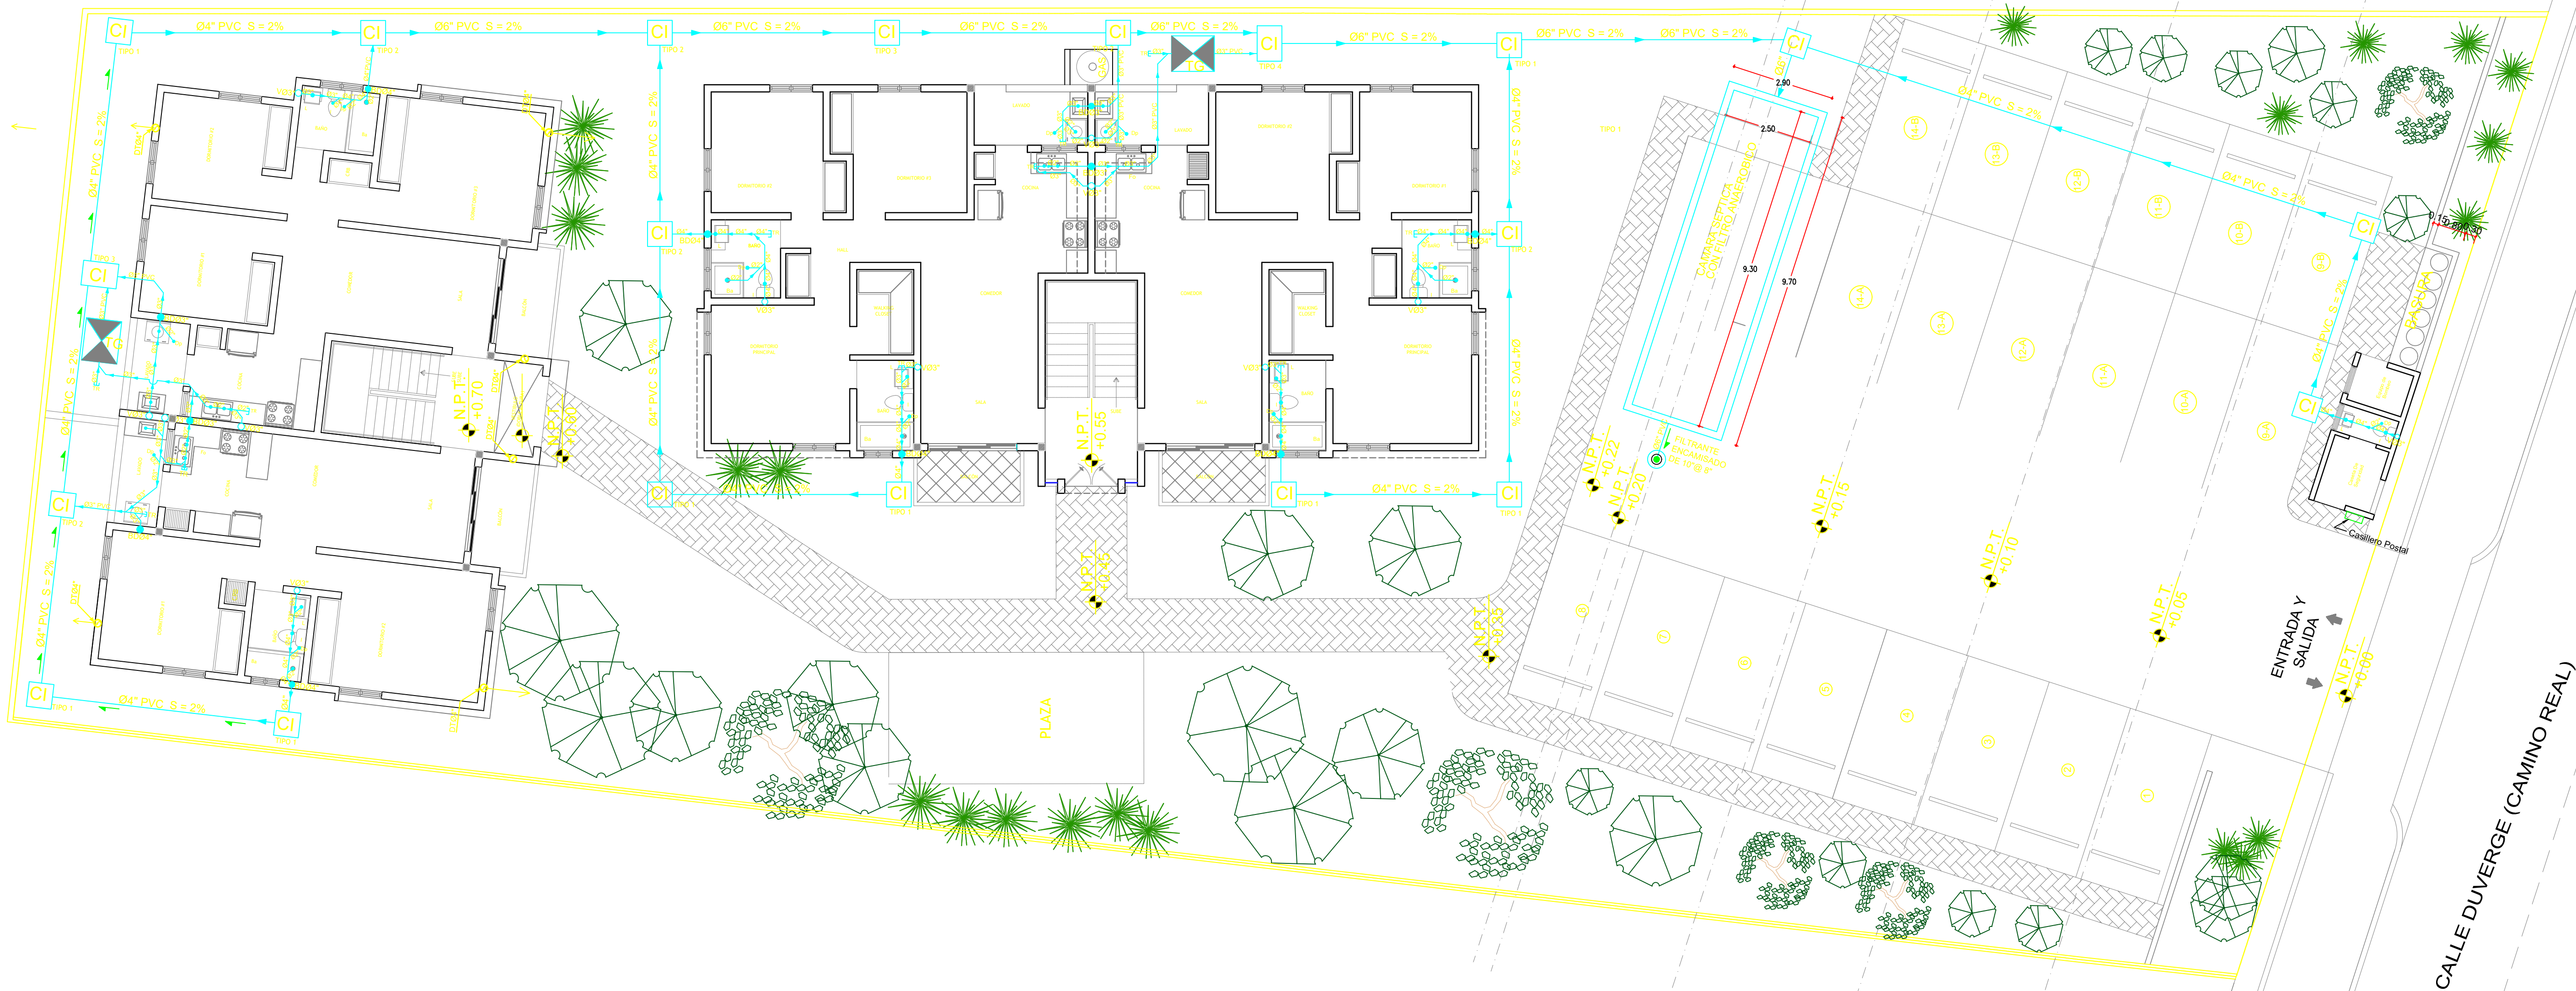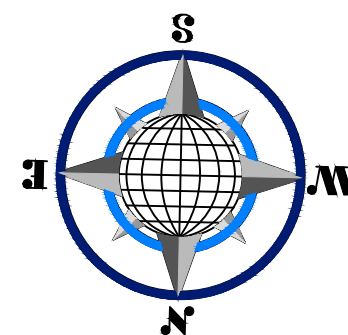

PLANTA RECOLECCION AGUAS RESIDUALES DE 1ER. NIVEL Y DE CONJUNTO
ESCALA: 1:100

1

S01



diazmeo & asocs.
ARQUITECTOS

Presidente Billini # 12, Bani, R.D. 522-4989
E-mail: diazmeo@hotmail.com

COLABORACION:



ARQUITECTURA DIGITAL
DISEÑOS-CONSTRUCCION-DIGITACION
COMPROMETIDOS CON SU TIEMPO
C/JUAN SANCHEZ RAMIREZ #56,
LOCAL 5 ZONA UASD TEL:221-5400

PROPIETARIO:
**GRUPO EMPRESARIAL
BANILEJO S.R.L.
GEBSA**

PROYECTISTAS:

DISEÑO ARQUITECTONICO:
DIAZMELO & ASOCS.
Arq. ISMAEL DIAZ MELO
Codia: 9604

DISEÑO SANITARIO:
Arq. HAMLET TEJEDA
Codia: 18303

DISEÑO ESTRUCTURAL:
ING. ODELIN TEJEDA
Codia: 23937

DISEÑO ELECTRICO:
ING. VILLYS SANCHEZ
Codia: 19060

CONTENIDO:
PLANTAS SANITARIAS

PROYECTO:
RESIDENCIAL GEBSA IV

Fecha: **MARZO/2020**

UBICACION:

BANI, PROV. PERAVIA


Ref.: **Acad 2000**

Hoja No.

Escala: **INDICADA**


5

NOTAS:
TODAS LAS TERMINACIONES Y/O CAMBIOS EN EL SET DE DOCUMENTOS CONSTRUCTIVOS DEBERAN SER APROBADOS POR EL SUPERVISOR PREVIAMENTE A SU APLICACION EN LA OBRA.
TODAS LAS MEDIDAS DE HUECOS Y DE SUPERFICIE A SER REVESTIDAS SERAN RECTIFICADAS PREVIA FABRICACION DE LOS CERRES O LA O LA INSTALACION DE LOS RECURBIMIENTOS
LAS TERMINACIONES Y / O DETALLES NO ESPECIFICADOS SERAN DEFINIDOS ENTRE EL DUEÑO Y EL AUTOR DEL PROYECTO.
EL CONTRATISTA NO PODRA TOMAR DECISIONES INCONSULTAS RESPECTO VARIACIONES EN EL CONTENIDO DE ESTE DOCUMENTO
LOS PLANOS ARQUITECTONICOS MANDARAN RESPECTO A LOS DEMAS A ANTE CUALQUIER DIFERENCIA, PRIMARA LA INFORMACIONCONTENIDA EN LOS MISMOS

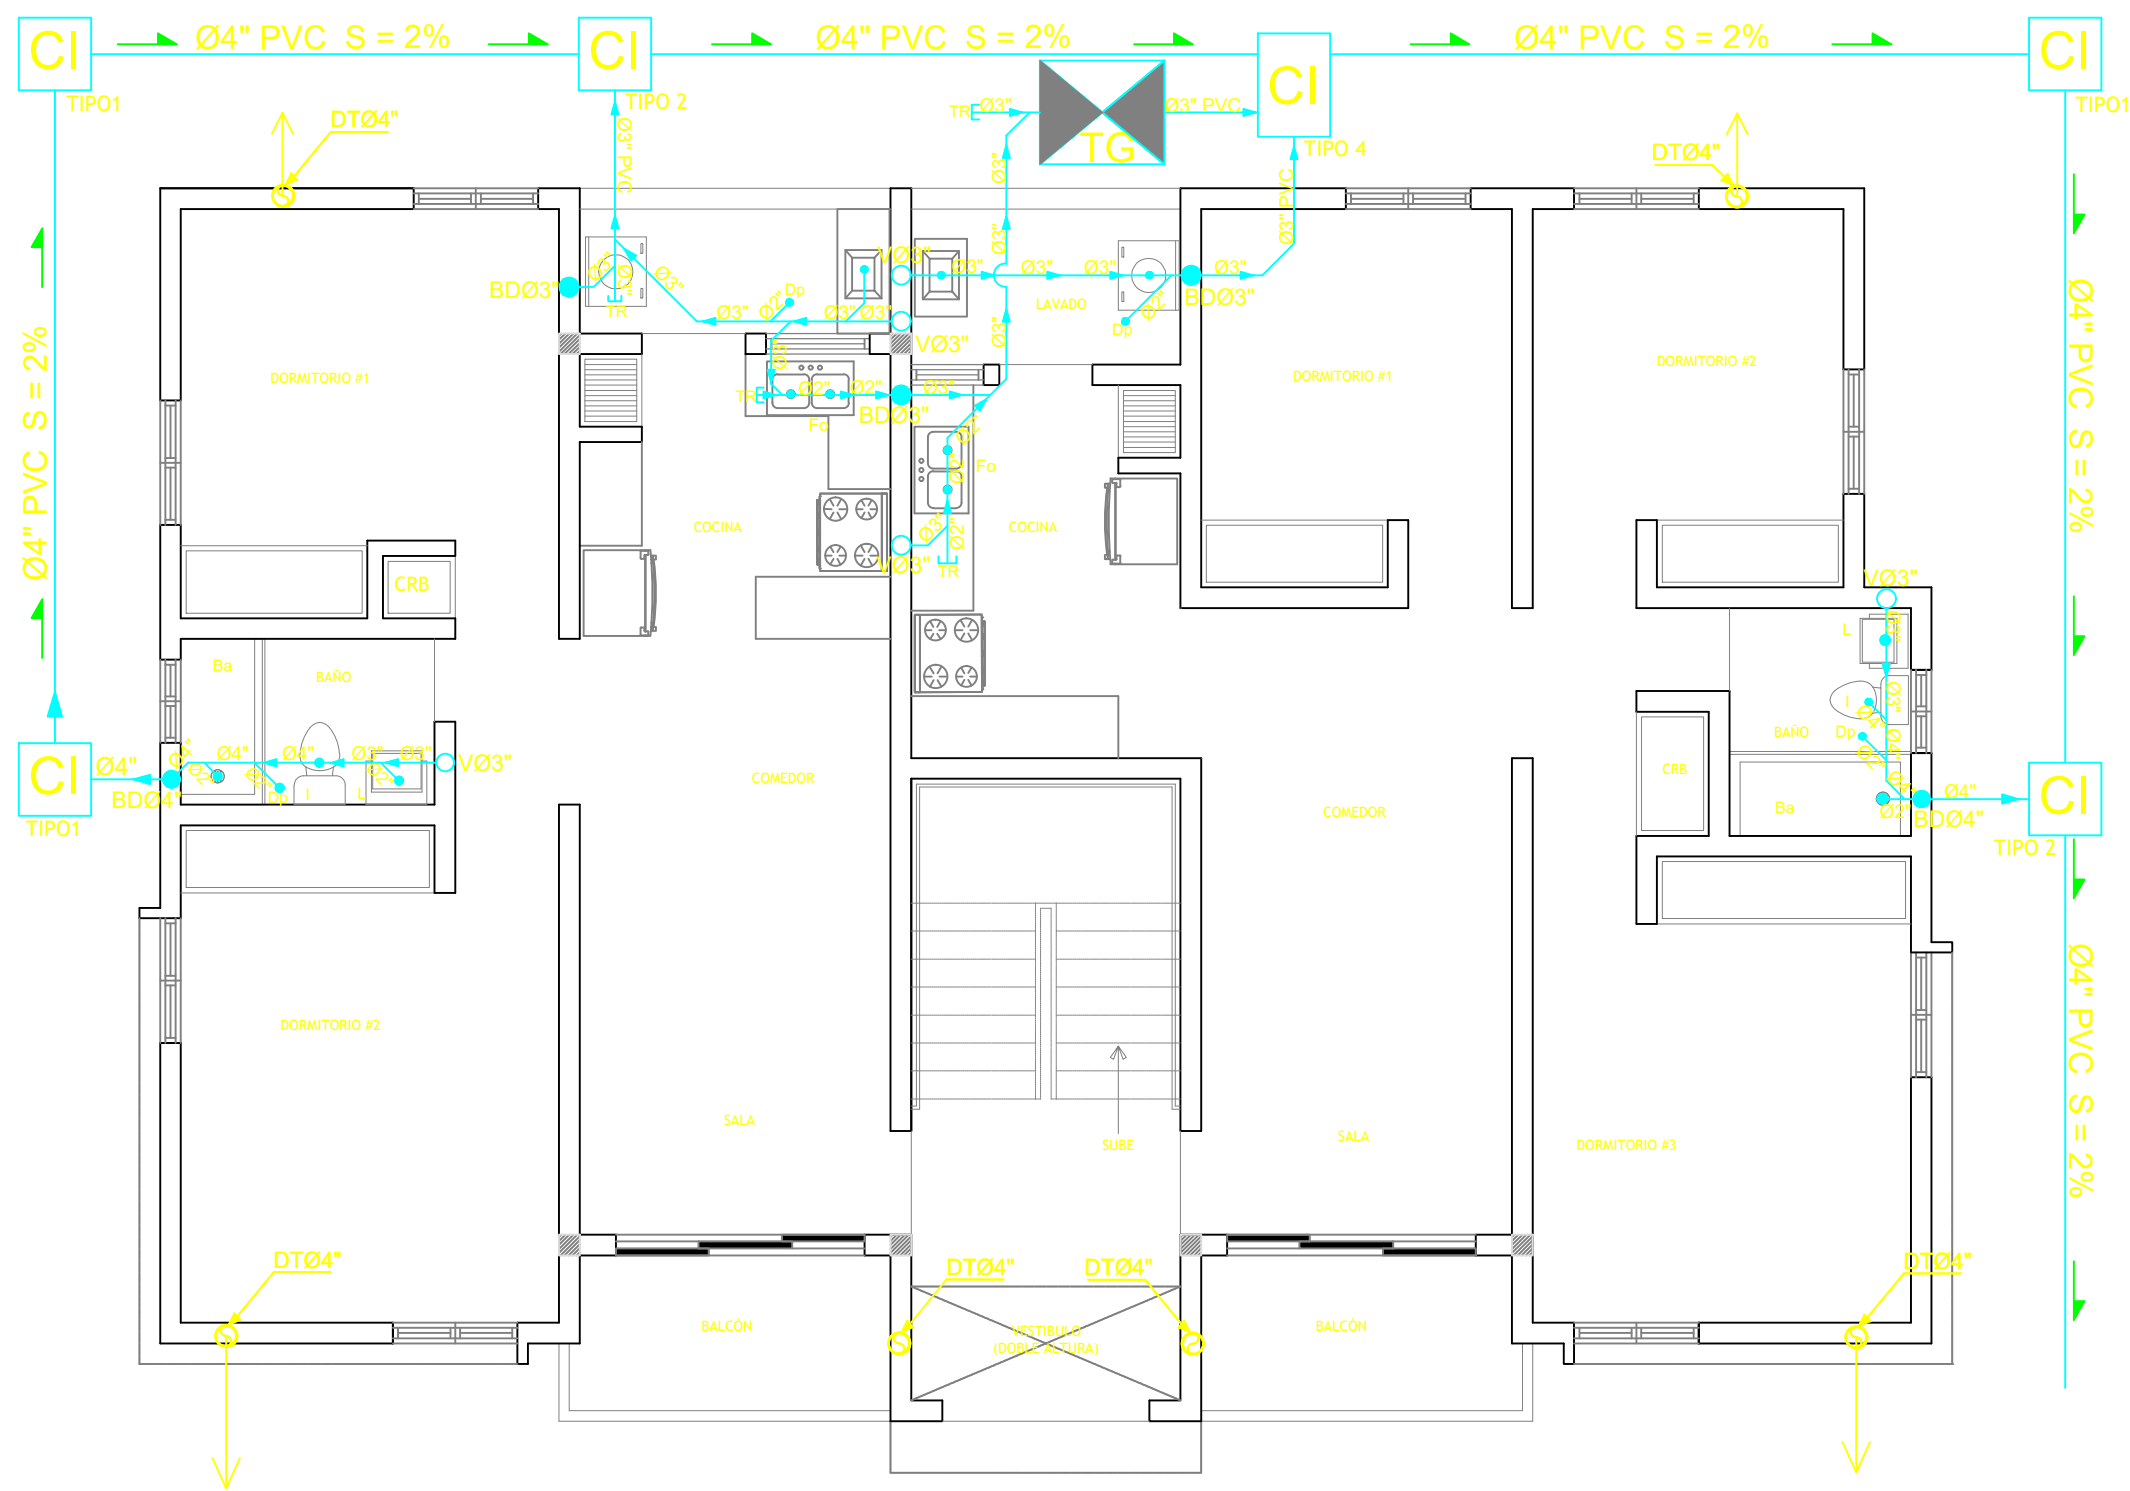


PLANTA RECOLECCION AGUAS RESIDUALES DE 1ER. NIVEL, BLOQUE A
ESCALA: 1:75

1
S02

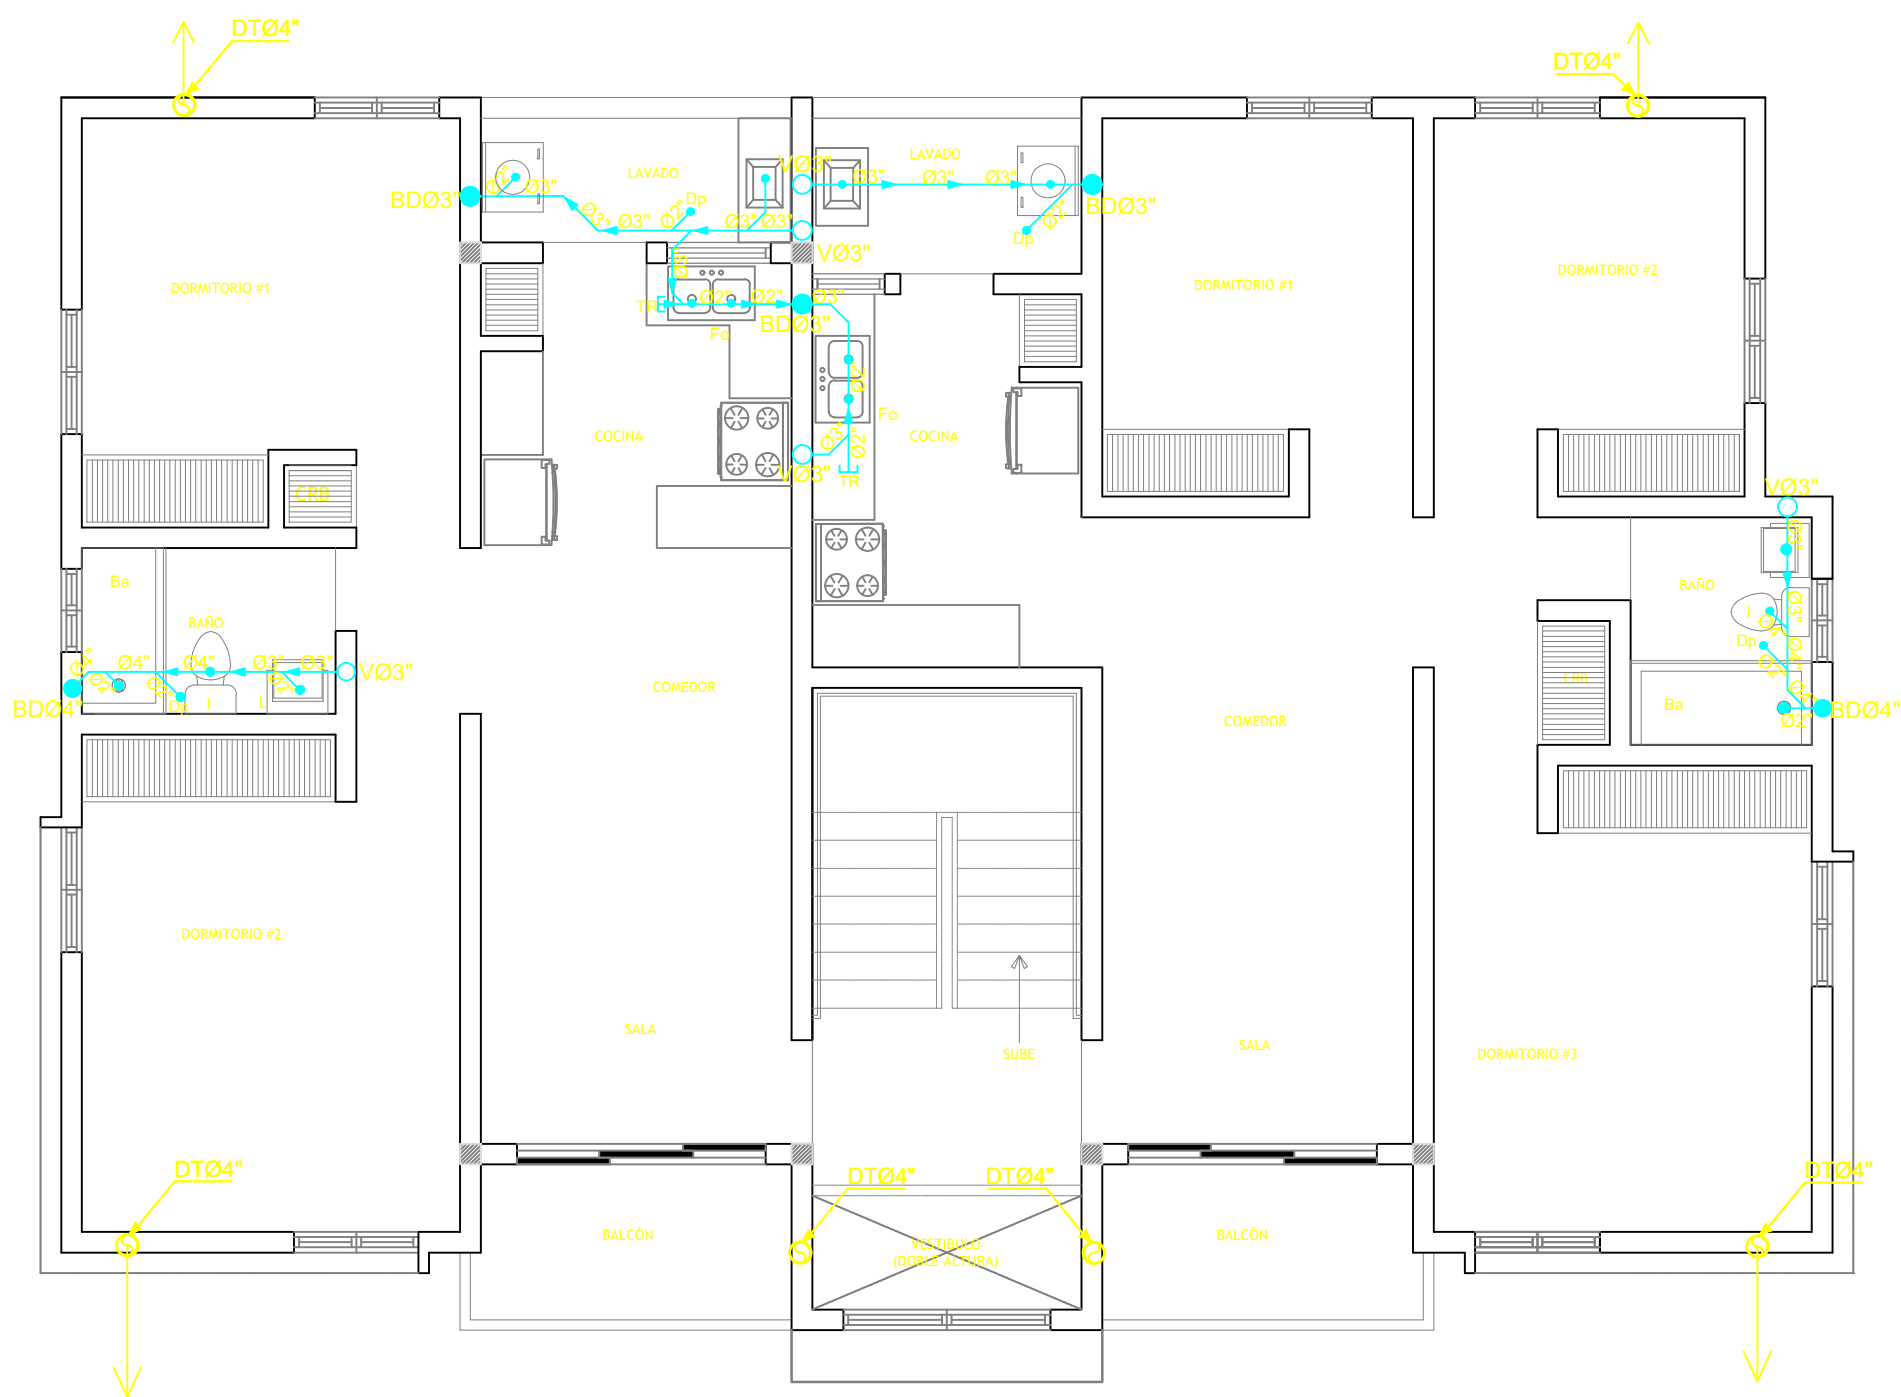


PLANTA RECOLECCION AGUAS RESIDUALES DE 2DO. NIVEL, BLOQUE A
ESCALA: 1:75

2
S02

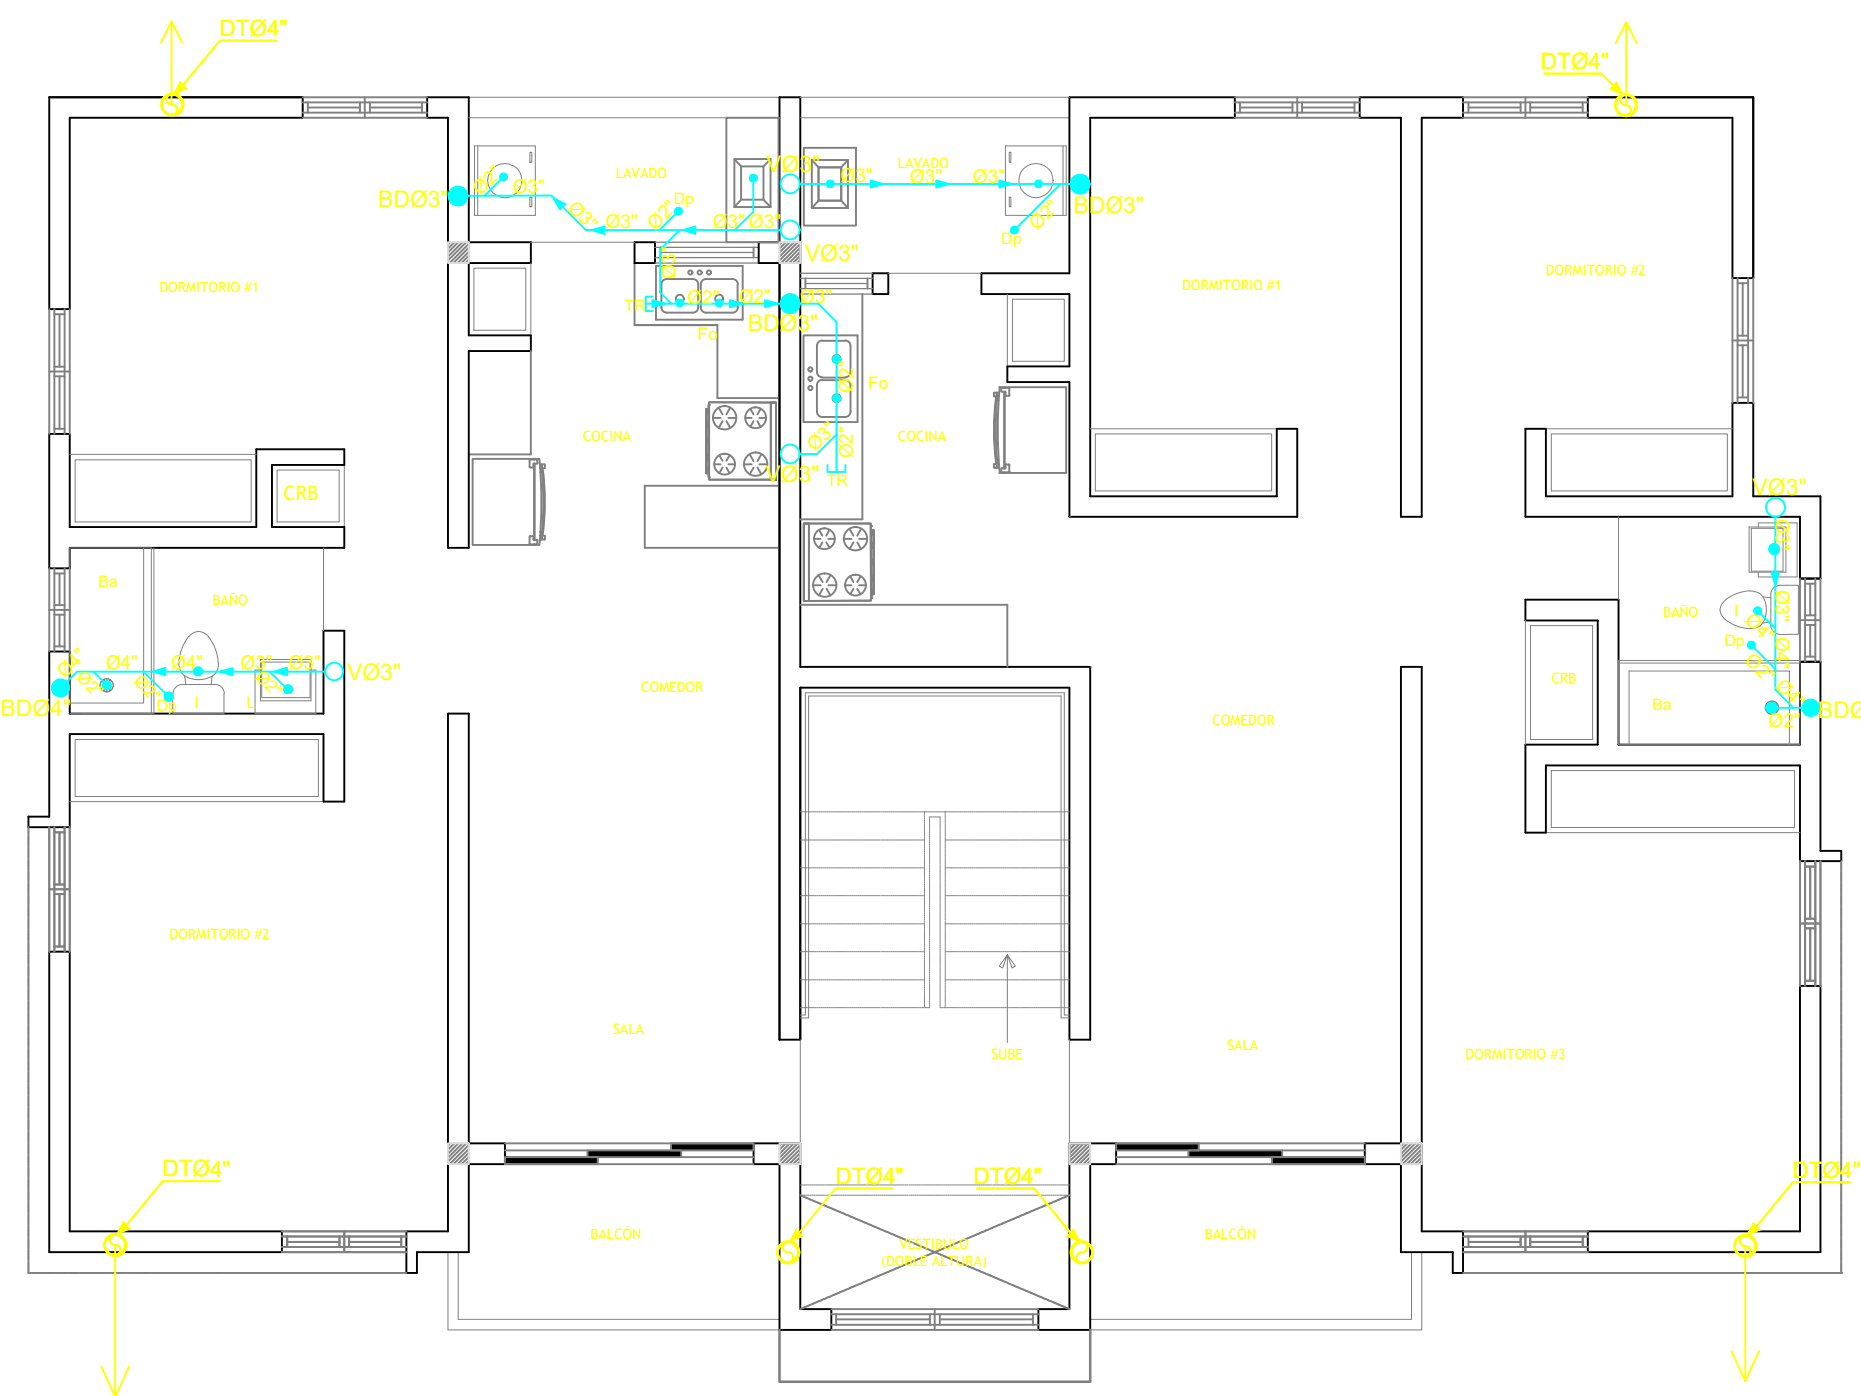

PLANTA RECOLECCION AGUAS RESIDUALES DE 3ER. NIVEL, BLOQUE A
ESCALA: 1:75

3
S02

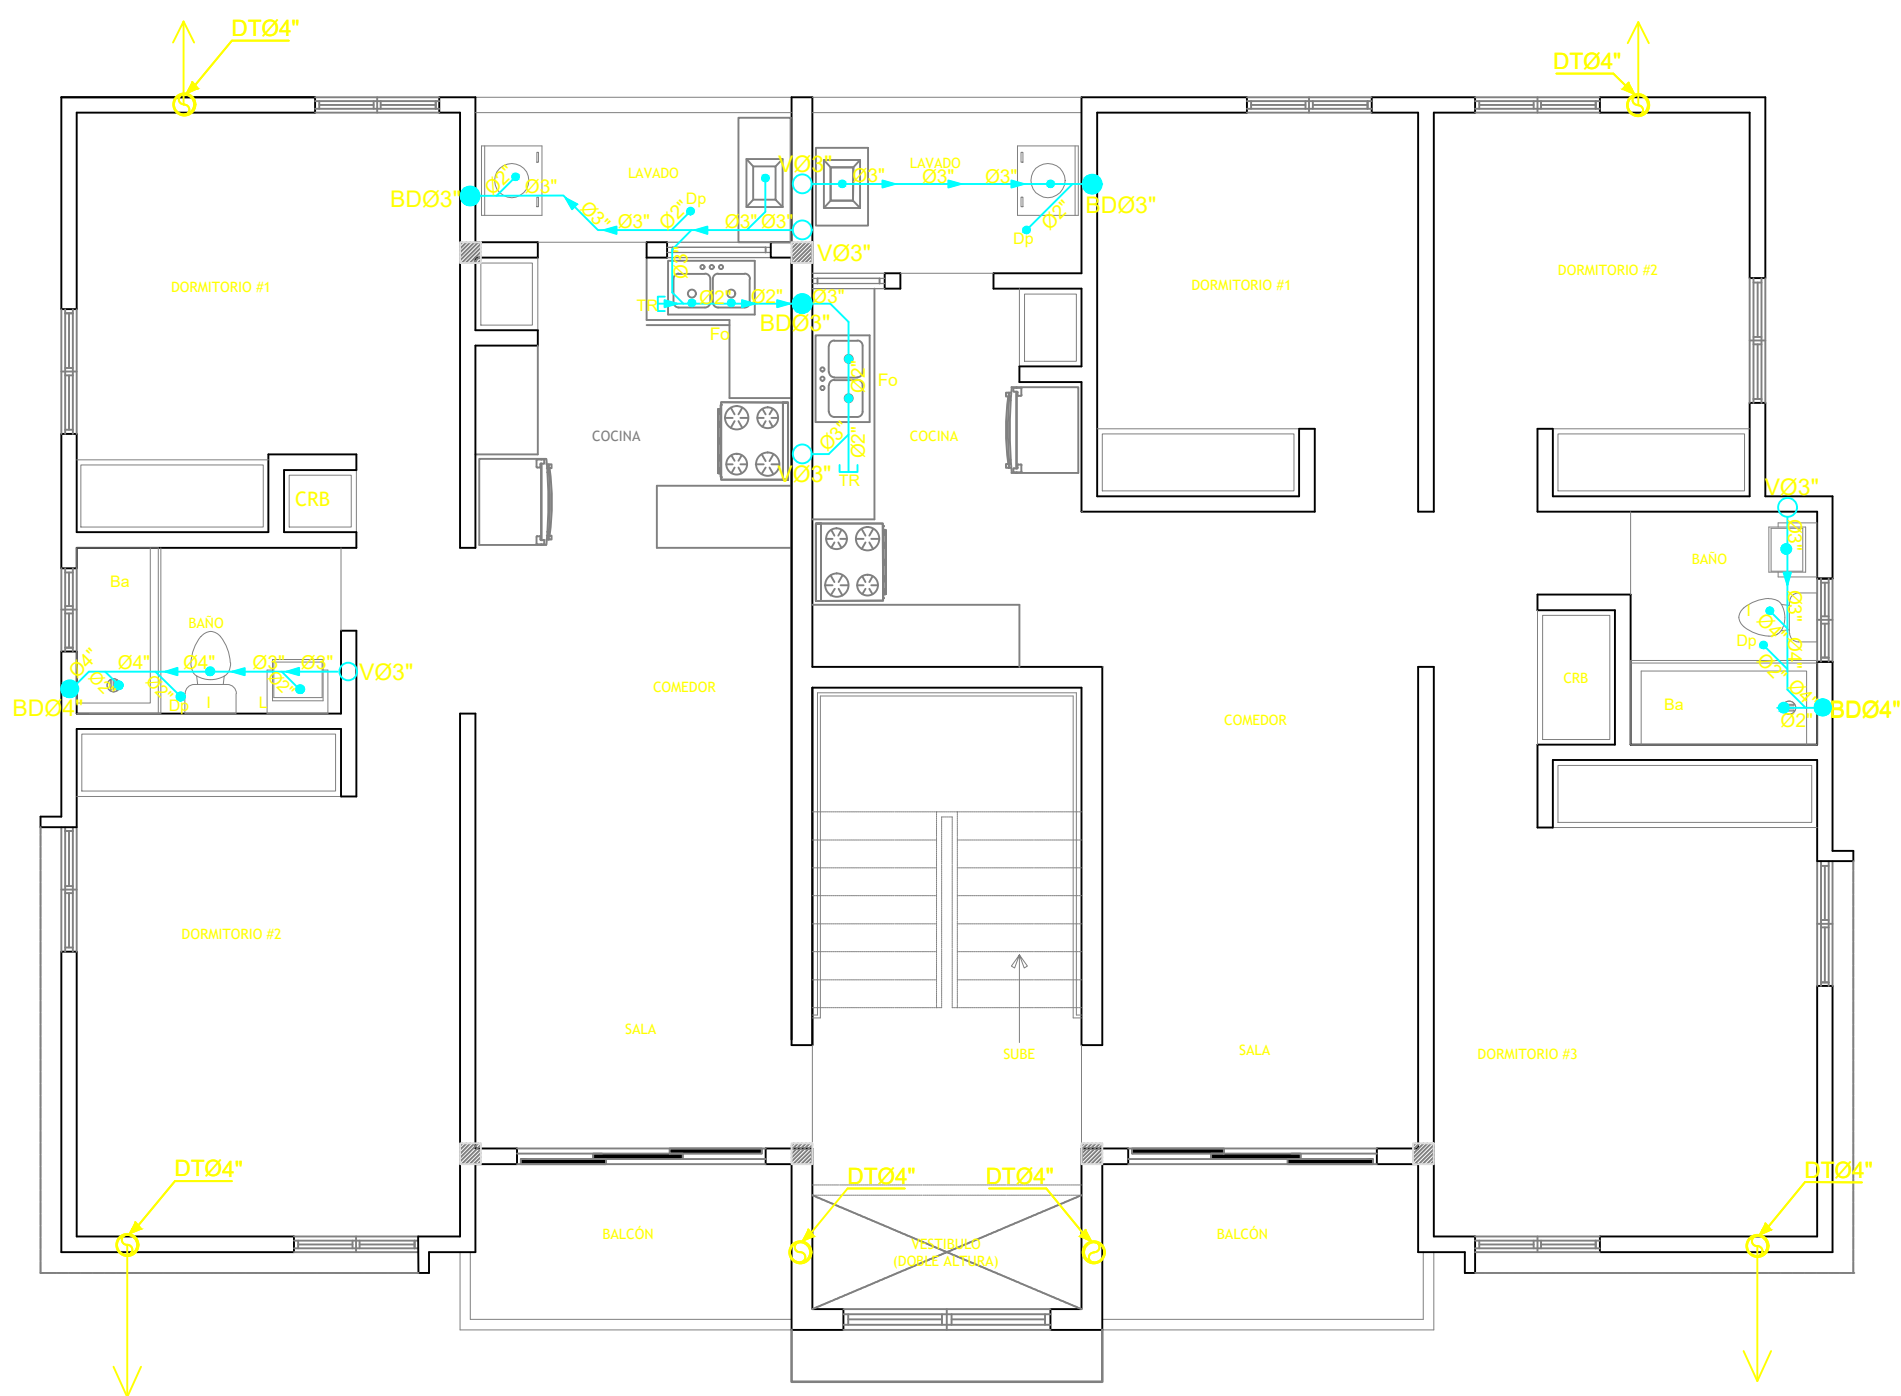

PLANTA RECOLECCION AGUAS RESIDUALES DE 4TO. NIVEL, BLOQUE A
ESCALA: 1:75

4
S02



diazmelo & asocs.
ARQUITECTOS

Presidente Billini # 12, Bani, R.D. 522-4989
E-mail: diazmelo@hotmail.com

COLABORACION:



ARQUITECTURA DIGITAL
DISEÑOS-CONSTRUCCION-DIGITACION
COMPROMETIDOS CON SU TIEMPO
C/JUAN SANCHEZ RAMIREZ #56,
LOCAL 5 ZONA UASD TEL:221-5400

PROPIETARIO :
**GRUPO EMPRESARIAL
BANILEJO S.R.L.
GEBSA**

PROYECTISTAS:

DISEÑO ARQUITECTONICO:
DIAZMELO & ASOCS.
Arq. ISMAEL DIAZ MELO
Codia: 9604

DISEÑO SANITARIO:
Arq. HAMLET TEJEDA
Codia: 18303

DISEÑO ESTRUCTURAL:
ING. ODELIN TEJEDA
Codia: 23937

DISEÑO ELECTRICO:
ING. VILLYS SANCHEZ
Codia: 19060

CONTENIDO:
PLANTAS SANITARIAS


PROYECTO:
RESIDENCIAL GEBSA IV

Fecha: **MARZO/2020**

UBICACION:
BANI, PROV. PERAVIA


Ref.: **Acad 2000** Hoja No. **6**
Escala: **INDICADA**

NOTAS:
TODAS LAS TERMINACIONES Y/O CAMBIOS EN EL SET DE DOCUMENTOS CONSTRUCTIVOS DEBERAN SER APROBADOS POR EL SUPERVISOR PREVIAMENTE A SU APLICACION EN LA OBRA.
TODAS LAS MEDIDAS DE HUECOS Y DE SUPERFICIE A SER REVESTIDAS SERAN RECTIFICADAS PREVIA FABRICACION DE LOS CERRRES O LA O LA INSTALACION DE LOS RECURRIMIENTOS
LAS TERMINACIONES Y / O DETALLES NO ESPECIFICADOS SERAN DEFINIDOS ENTRE EL DUEÑO Y EL AUTOR DEL PROYECTO.
EL CONTRATISTA NO PODRA TOMAR DECISIONES INCONSULTAS RESPECTO VARIACIONES EN EL CONTENIDO DE ESTE DOCUMENTO
LOS PLANOS ARQUITECTONICOS MANDARAN RESPECTO A LOS DEMAS A ANTE CUALQUIER DIFERENCIA, PRIMARA LA INFORMACIONCONTENIDA EN LOS MISMOS

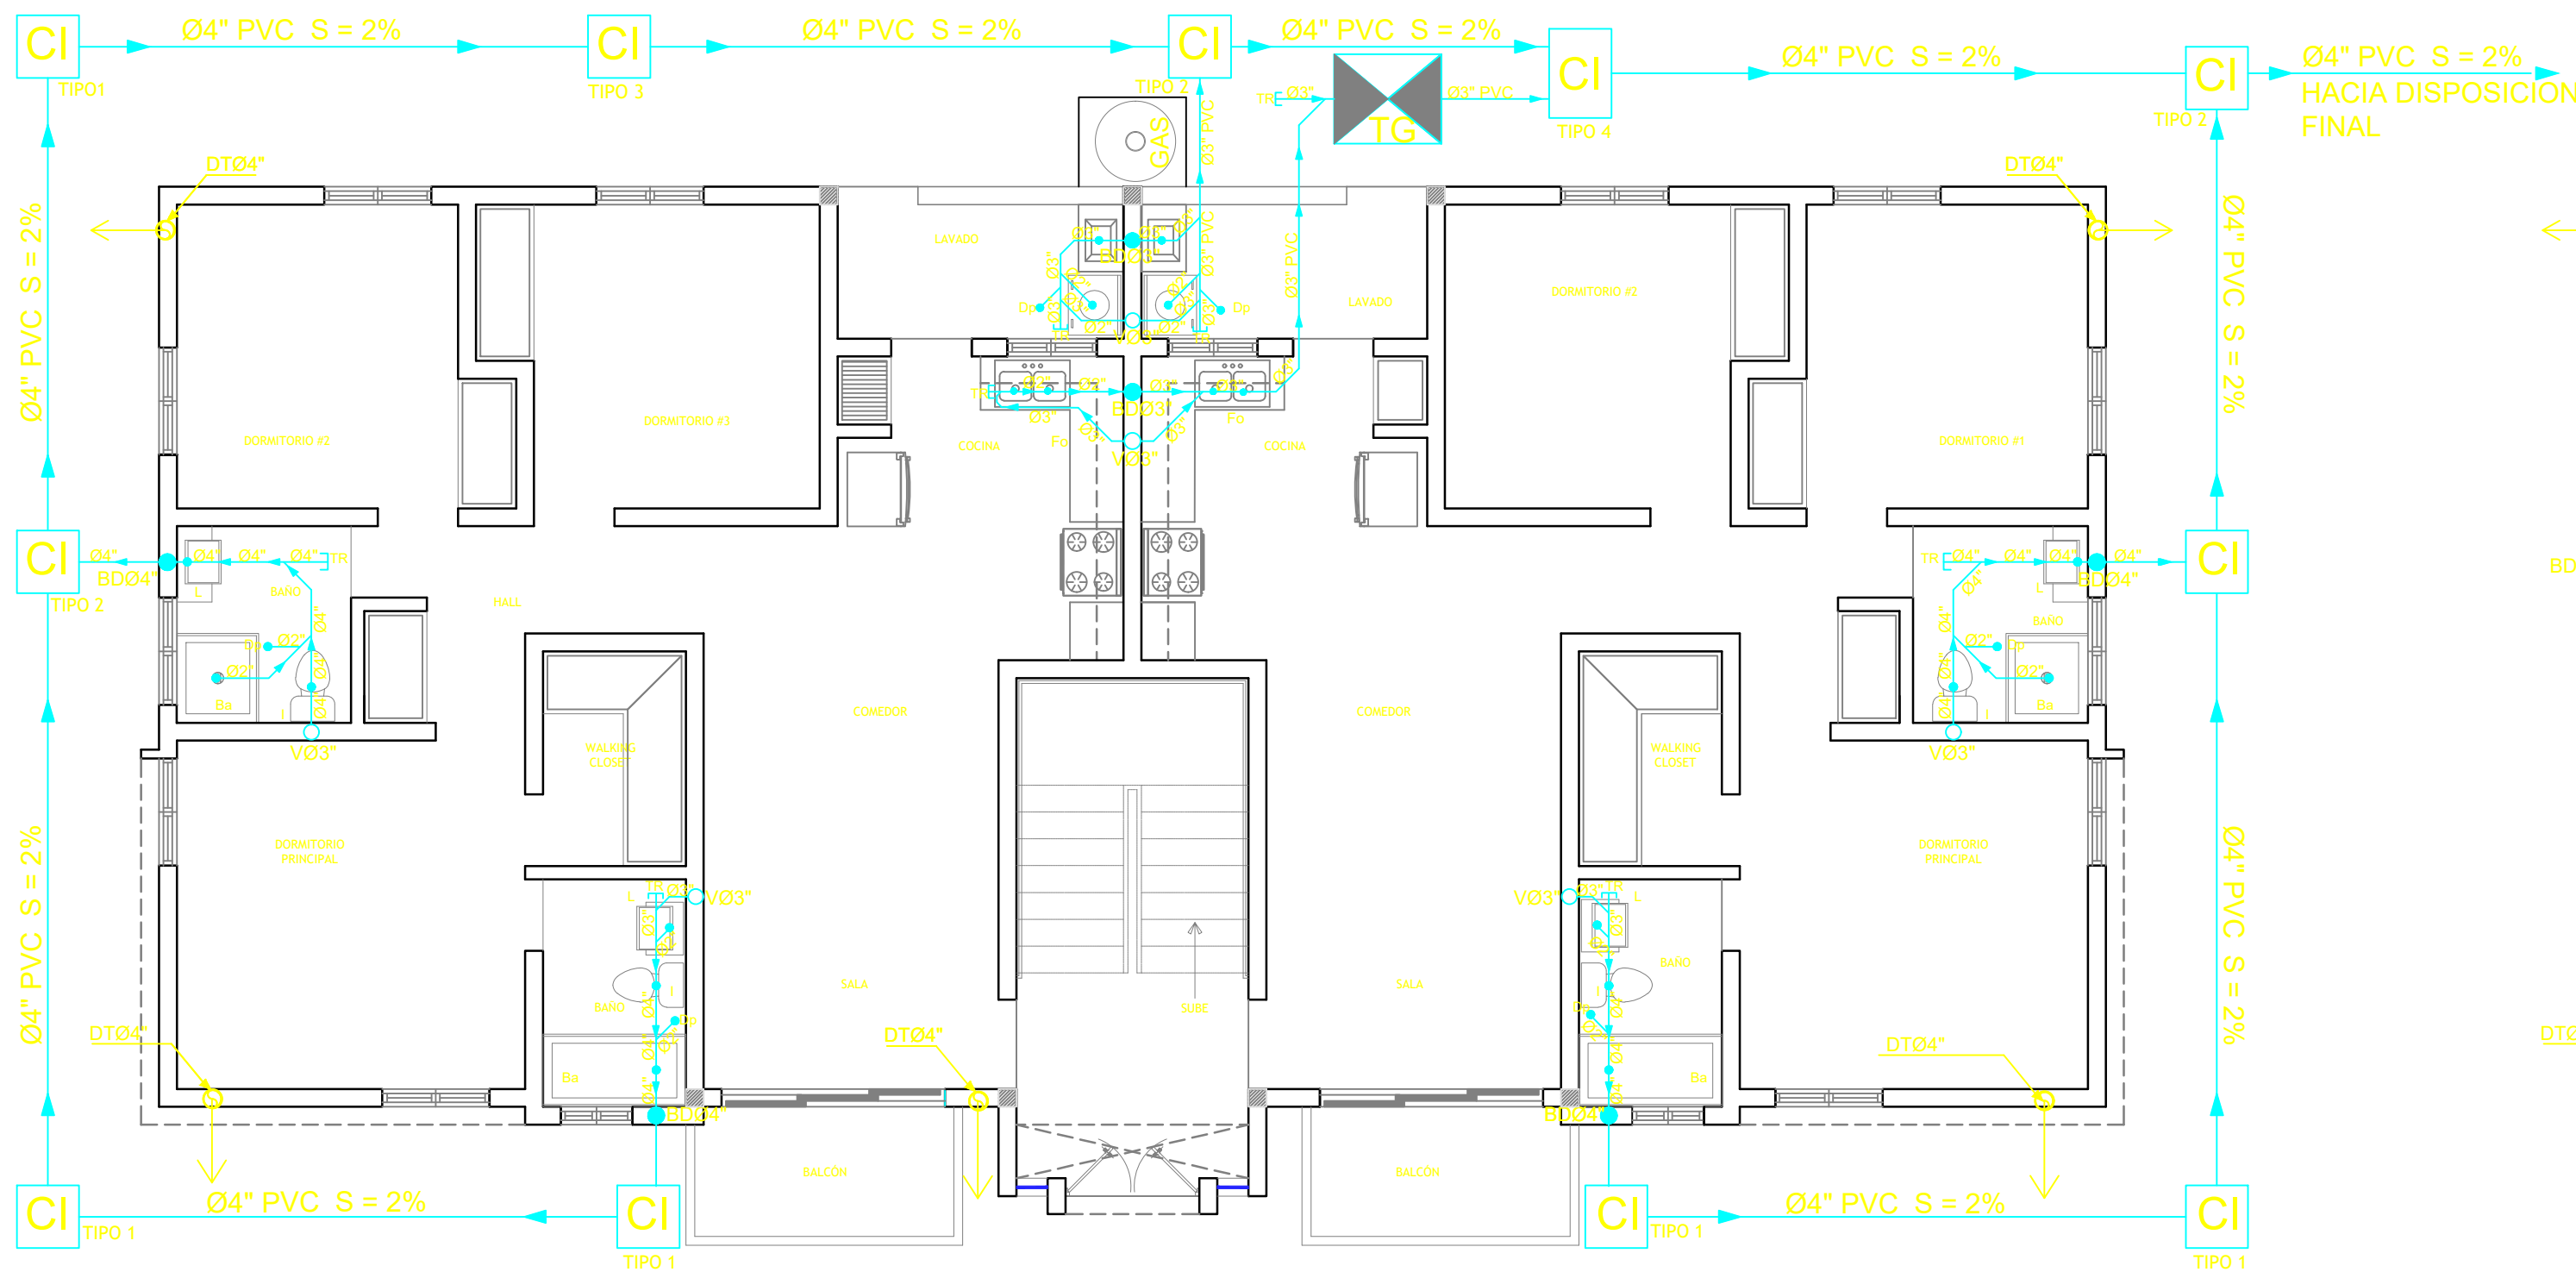


PLANTA RECOLECCION AGUAS RESIDUALES DE 1ER. NIVEL, BLOQUE B
ESCALA: 1:75

1
S03

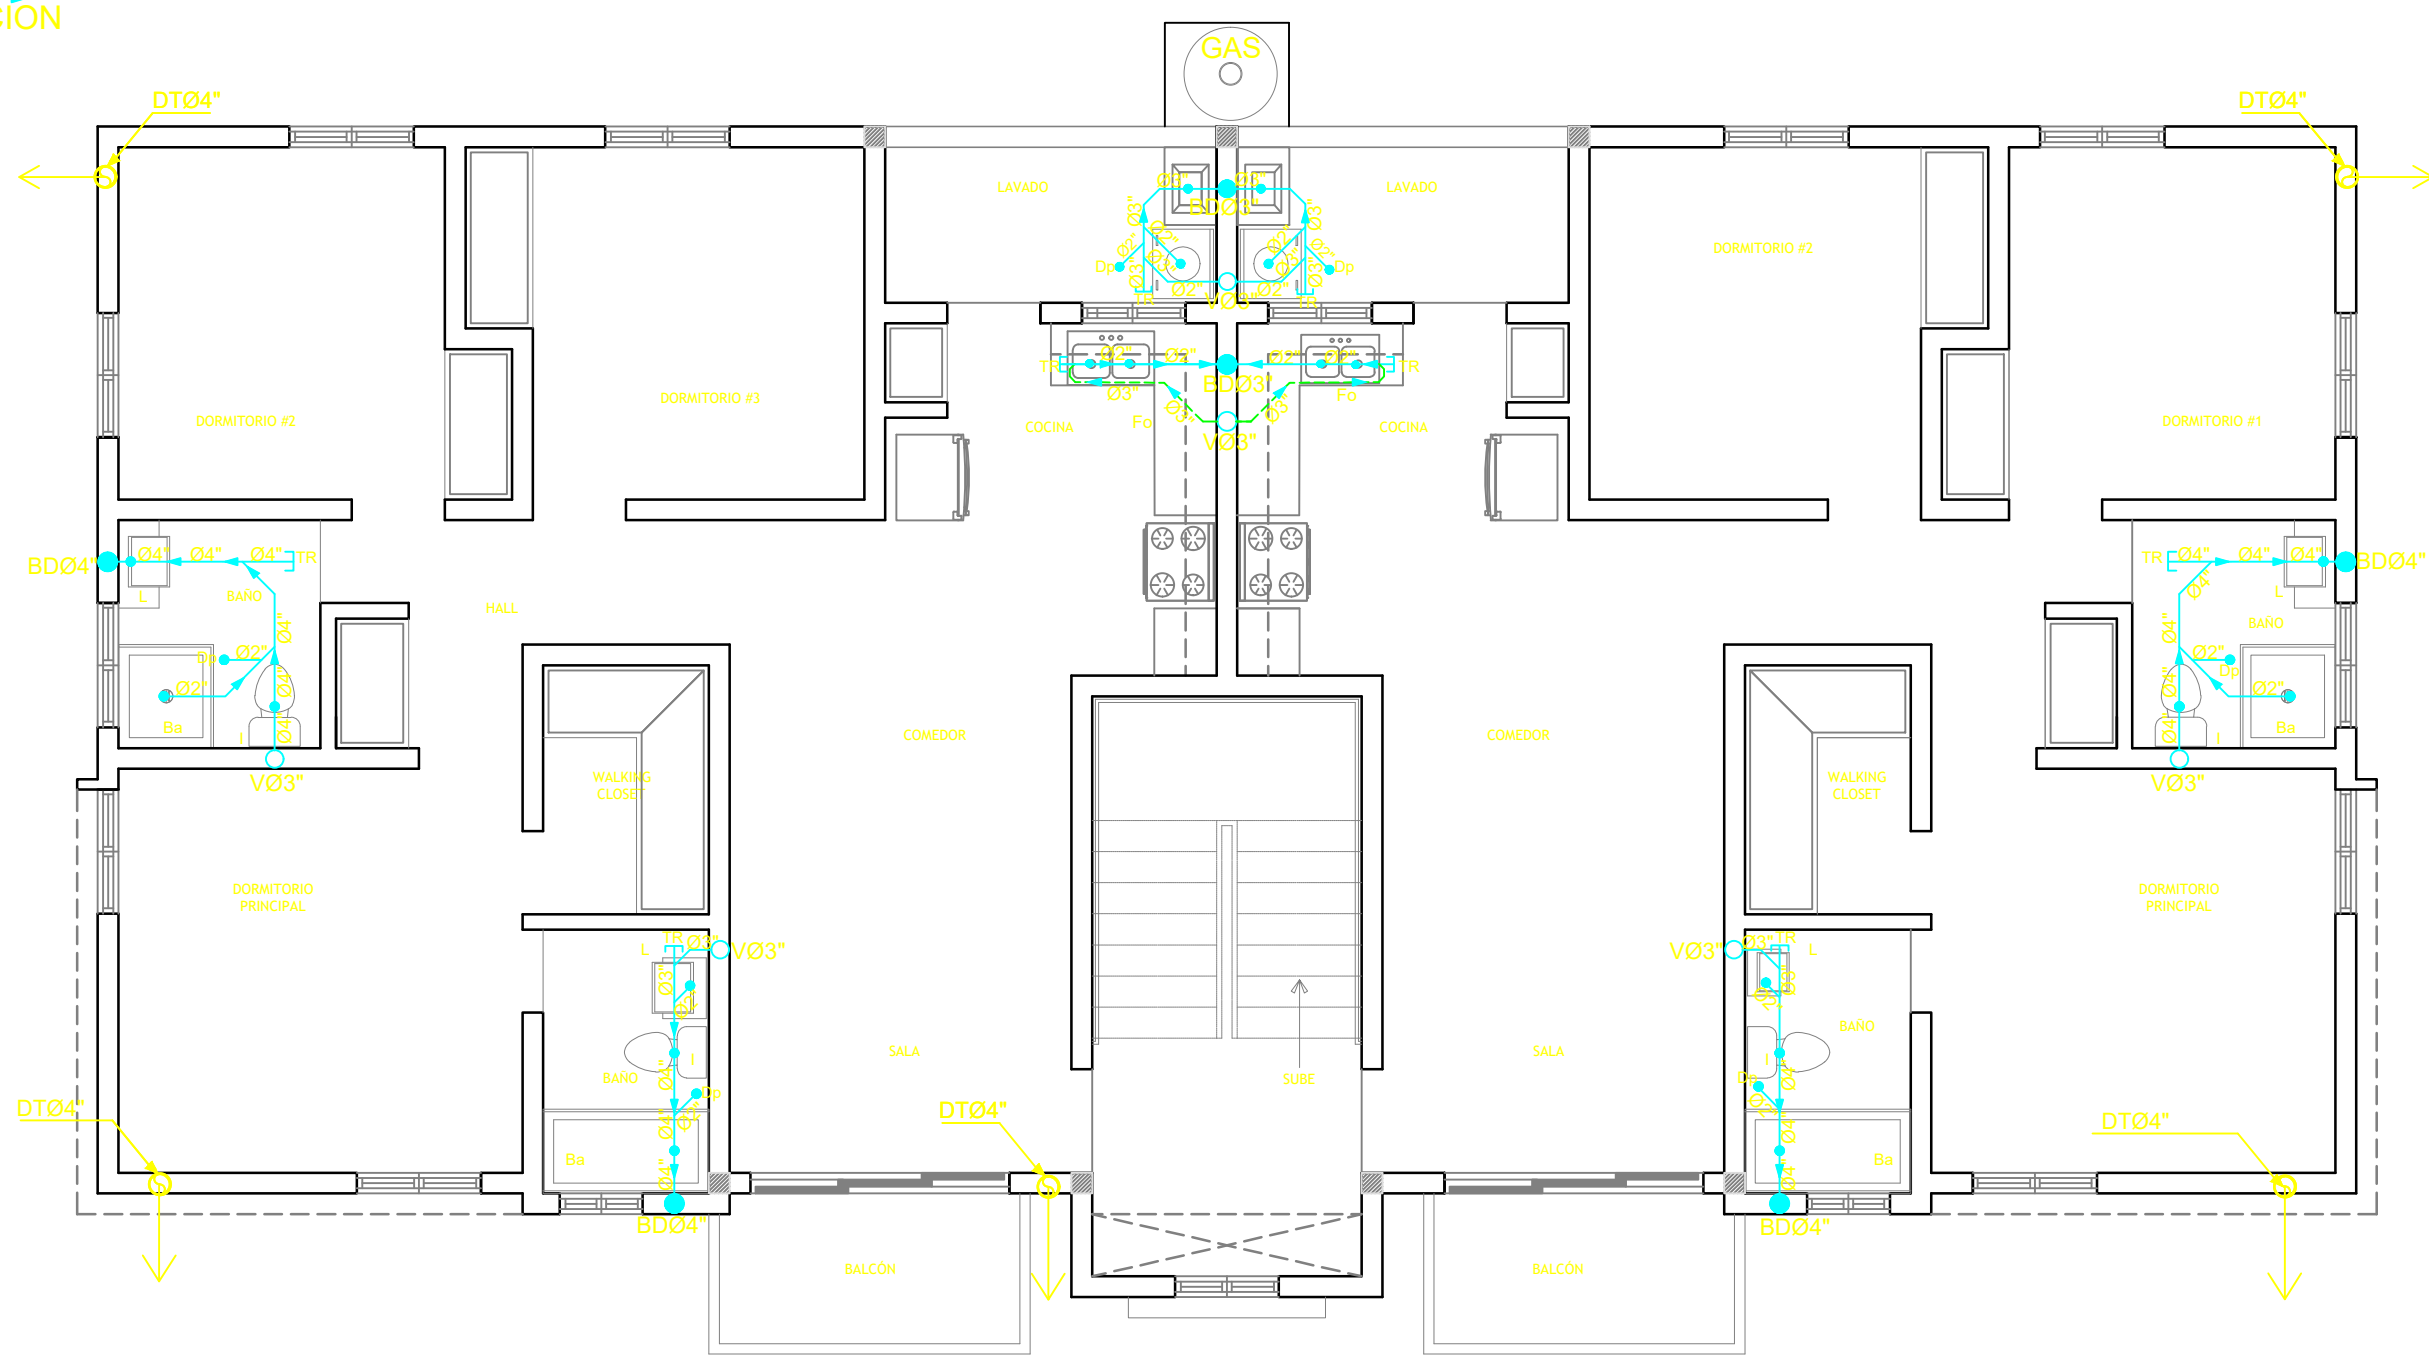



PLANTA RECOLECCION AGUAS RESIDUALES DE 2DO. NIVEL, BLOQUE B
ESCALA: 1:75

2
S03

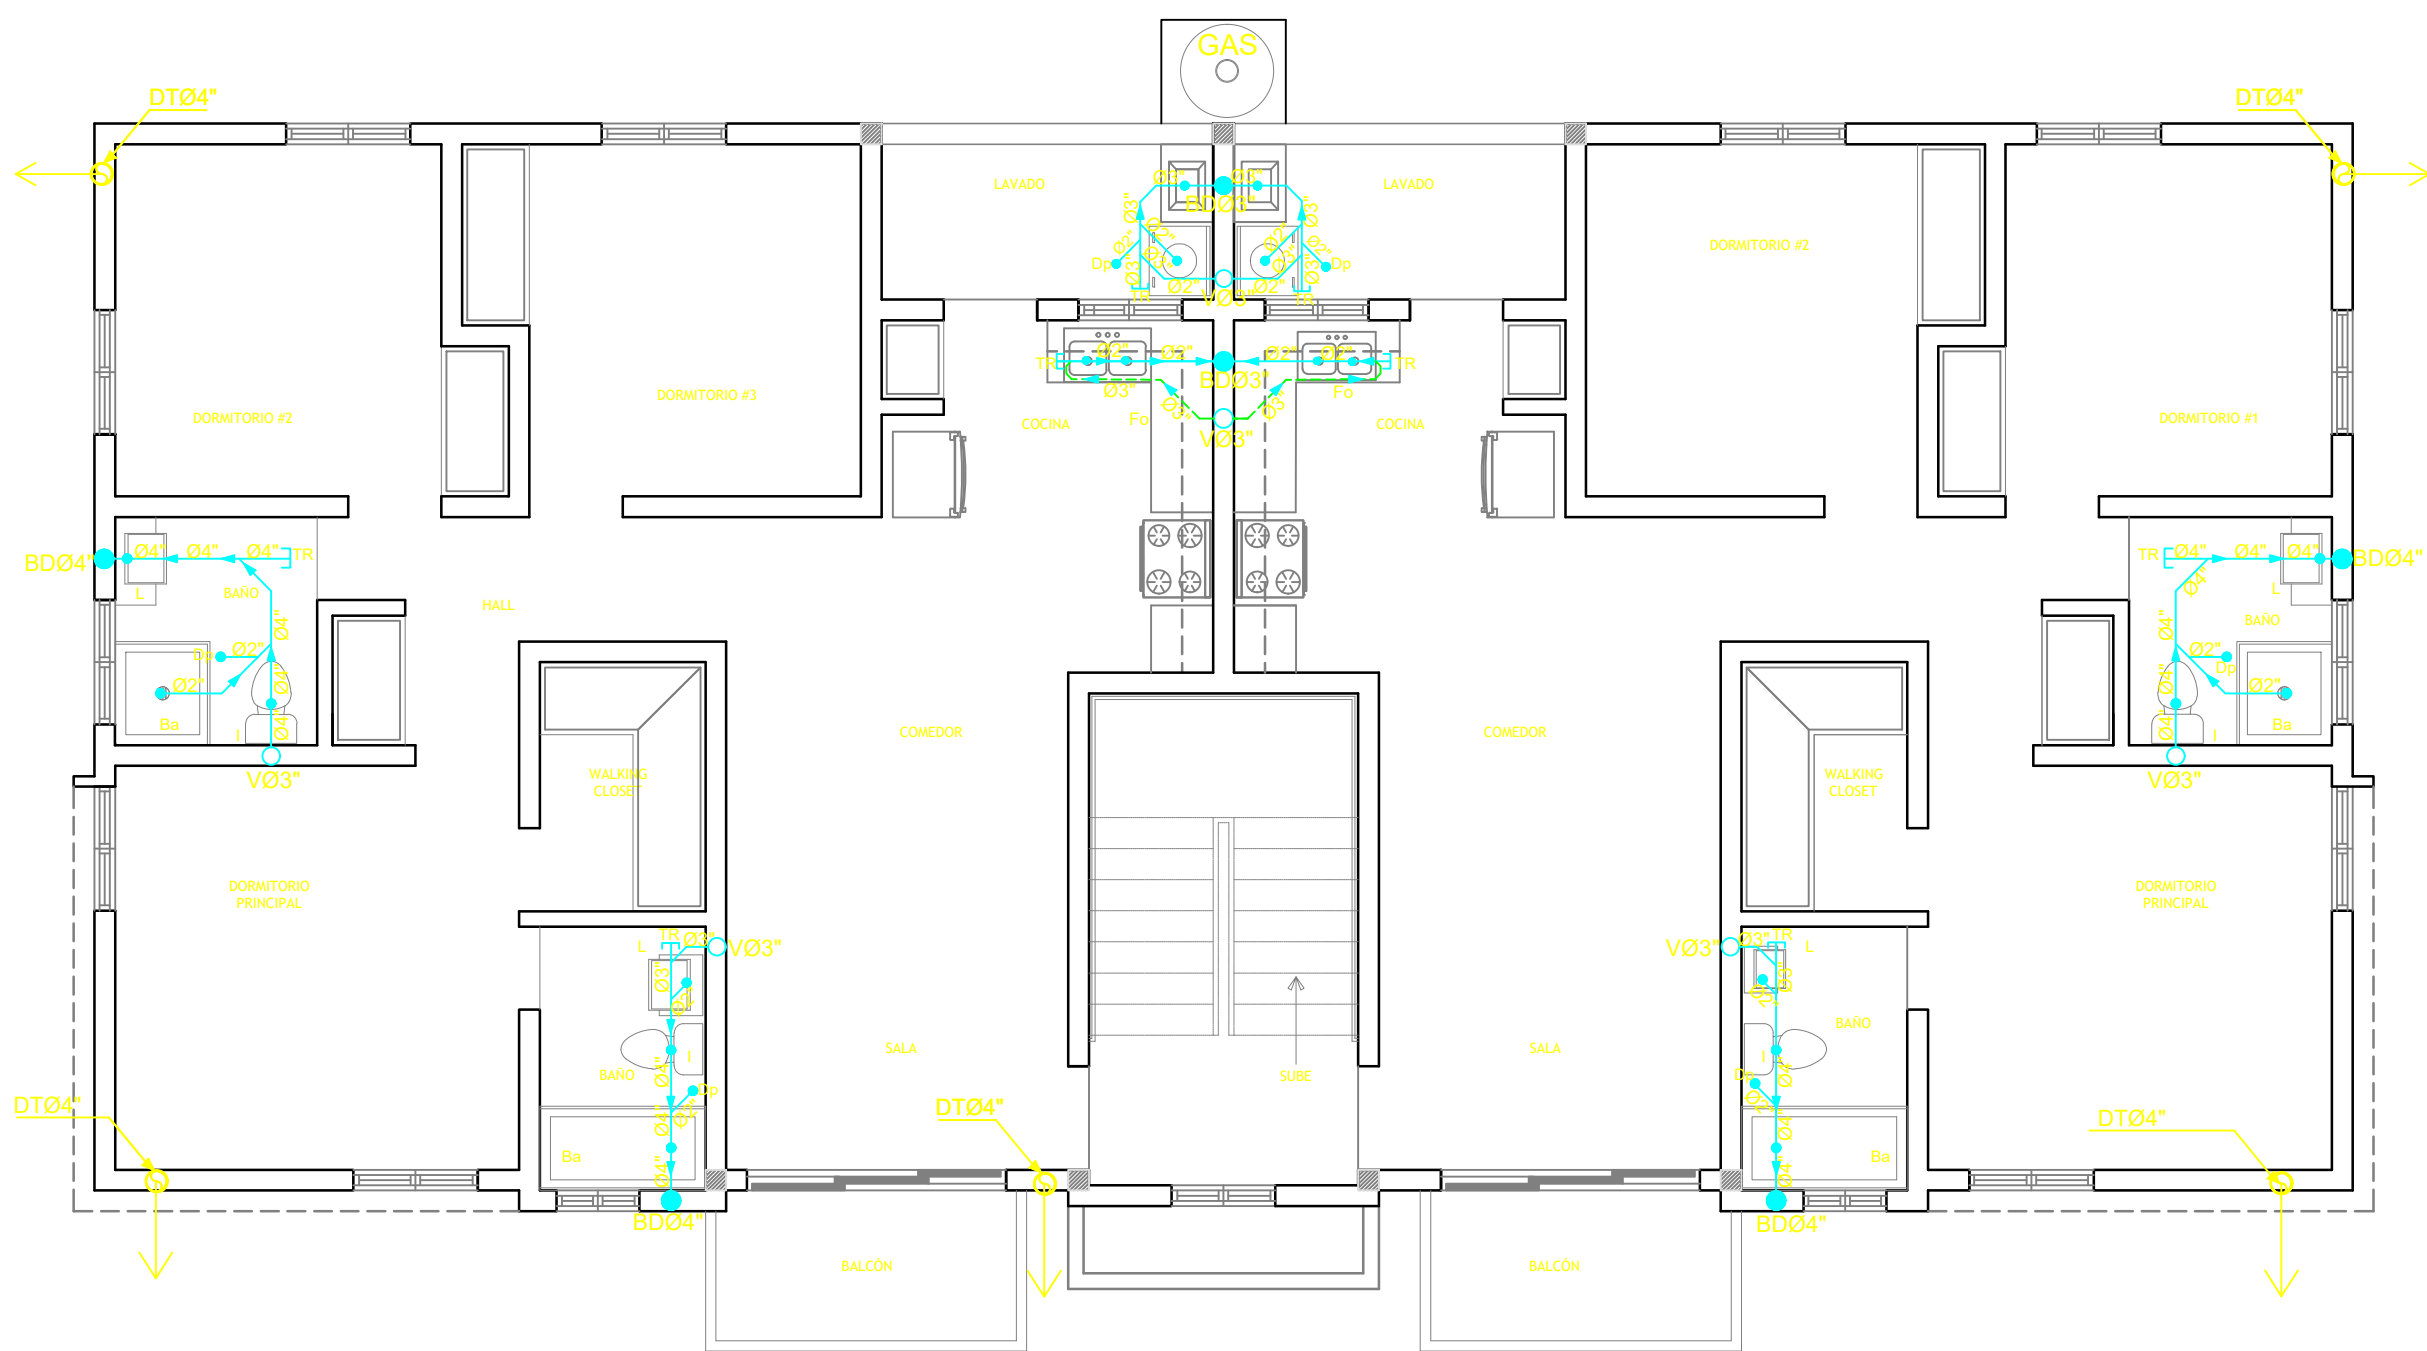

PLANTA RECOLECCION AGUAS RESIDUALES DE 3ER. NIVEL, BLOQUE B
ESCALA: 1:75

3
S03

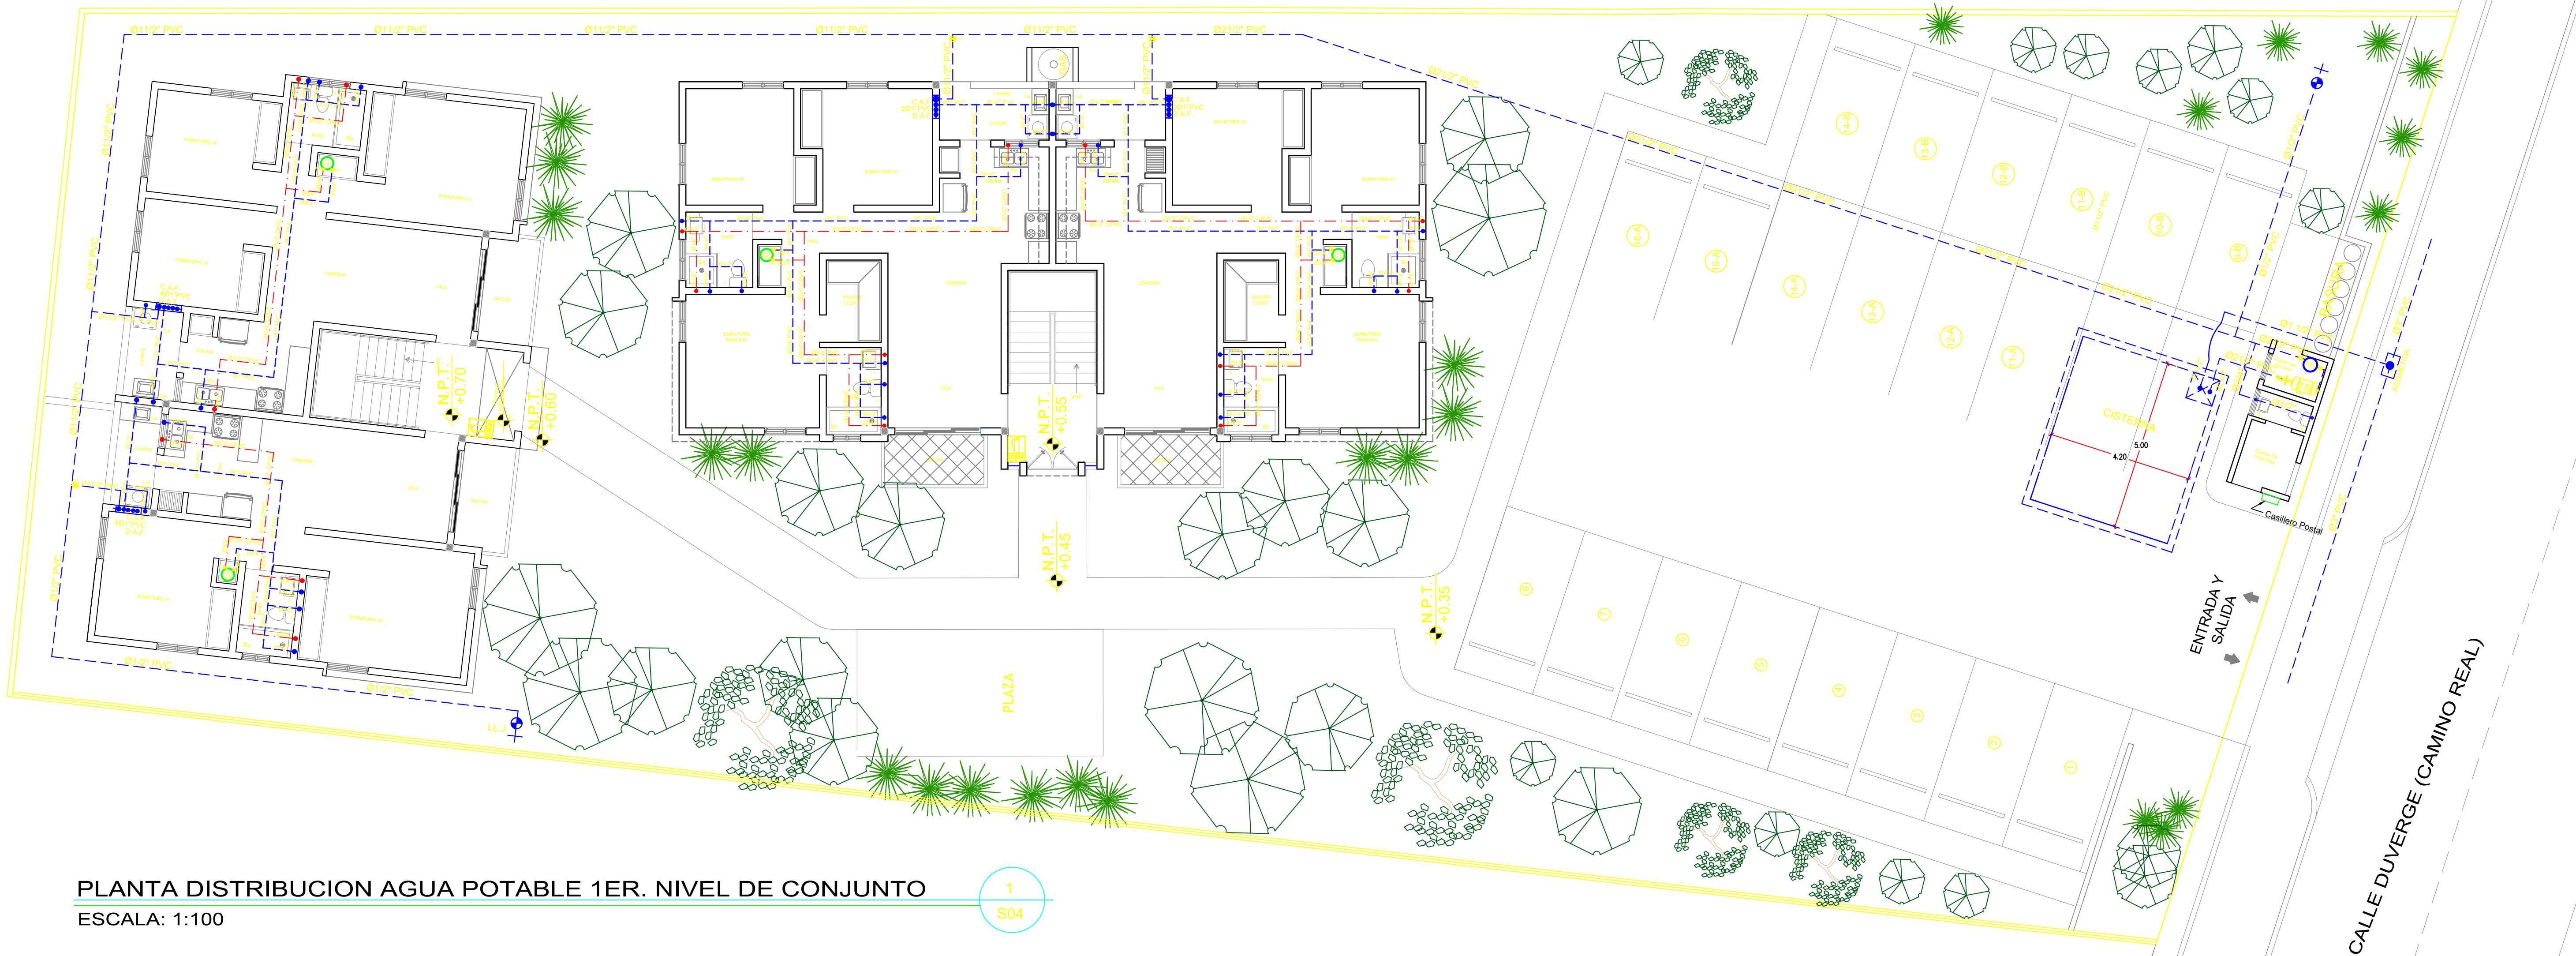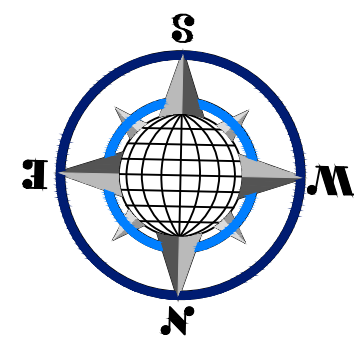

PLANTA DISTRIBUCION AGUA POTABLE 1ER. NIVEL DE CONJUNTO
ESCALA: 1:100

1
S04



diazmelo & asocs.
ARQUITECTOS
Presidente Billini # 12, Bani, R.D. 522-4989
E-mail: diazmelo@hotmail.com

COLABORACION:



ARQUITECTURA DIGITAL
DISEÑOS-CONSTRUCCION-DIGITACION
COMPROMETIDOS CON SU TIEMPO
C/JUAN SANCHEZ RAMIREZ #56,
LOCAL 5 ZONA UASD TEL:221-5400

PROPIETARIO:
**GRUPO EMPRESARIAL
BANILEJO S.R.L.
GEBSA**

PROYECTISTAS:

DISEÑO ARQUITECTONICO:
DIAZMELO & ASOCS.
Arq. ISMAEL DIAZ MELO
Codia: 9604

DISEÑO SANITARIO:
Arq. HAMLET TEJEDA
Codia: 18303

DISEÑO ESTRUCTURAL:
ING. ODELIN TEJEDA
Codia: 23937

DISEÑO ELECTRICO:
ING. VILLYS SANCHEZ
Codia: 19060

CONTENIDO:
**PLANT ARQUITECTONICA
1ER. NIVEL CONJUNTO**

PROYECTO:
RESIDENCIAL GEBSA IV


Fecha: MARZO/2020

UBICACION:
SOMBRERO, BANI, PROV. PERAVIA

Ref.: Acad 2000
Escala: INDICADA

Hoja No.
1

NOTAS:
TODAS LAS TERMINACIONES Y/O CAMBIOS EN EL SET DE DOCUMENTOS CONSTRUCTIVOS DEBERAN SER APROBADOS POR EL SUPERVISOR PREVIAMENTE A SU APLICACION EN LA OBRA.
TODAS LAS MEDIDAS DE HUECOS Y DE SUPERFICIE A SER REVESTIDAS SERAN RECTIFICADAS PREVIA FABRICACION DE LOS CERRRES O LA O LA INSTALACION DE LOS RECURRIMIENTOS
LAS TERMINACIONES Y / O DETALLES NO ESPECIFICADOS SERAN DEFINIDOS ENTRE EL DUEÑO Y EL AUTOR DEL PROYECTO.
EL CONTRATISTA NO PODRA TOMAR DECISIONES INCONSULTAS RESPECTO VARIACIONES EN EL CONTENIDO DE ESTE DOCUMENTO
LOS PLANOS ARQUITECTONICOS MANDARAN RESPECTO A LOS DEMAS A ANTE CUALQUIER DIFERENCIA, PRIMARA LA INFORMACIONCONTENIDA EN LOS MISMOS

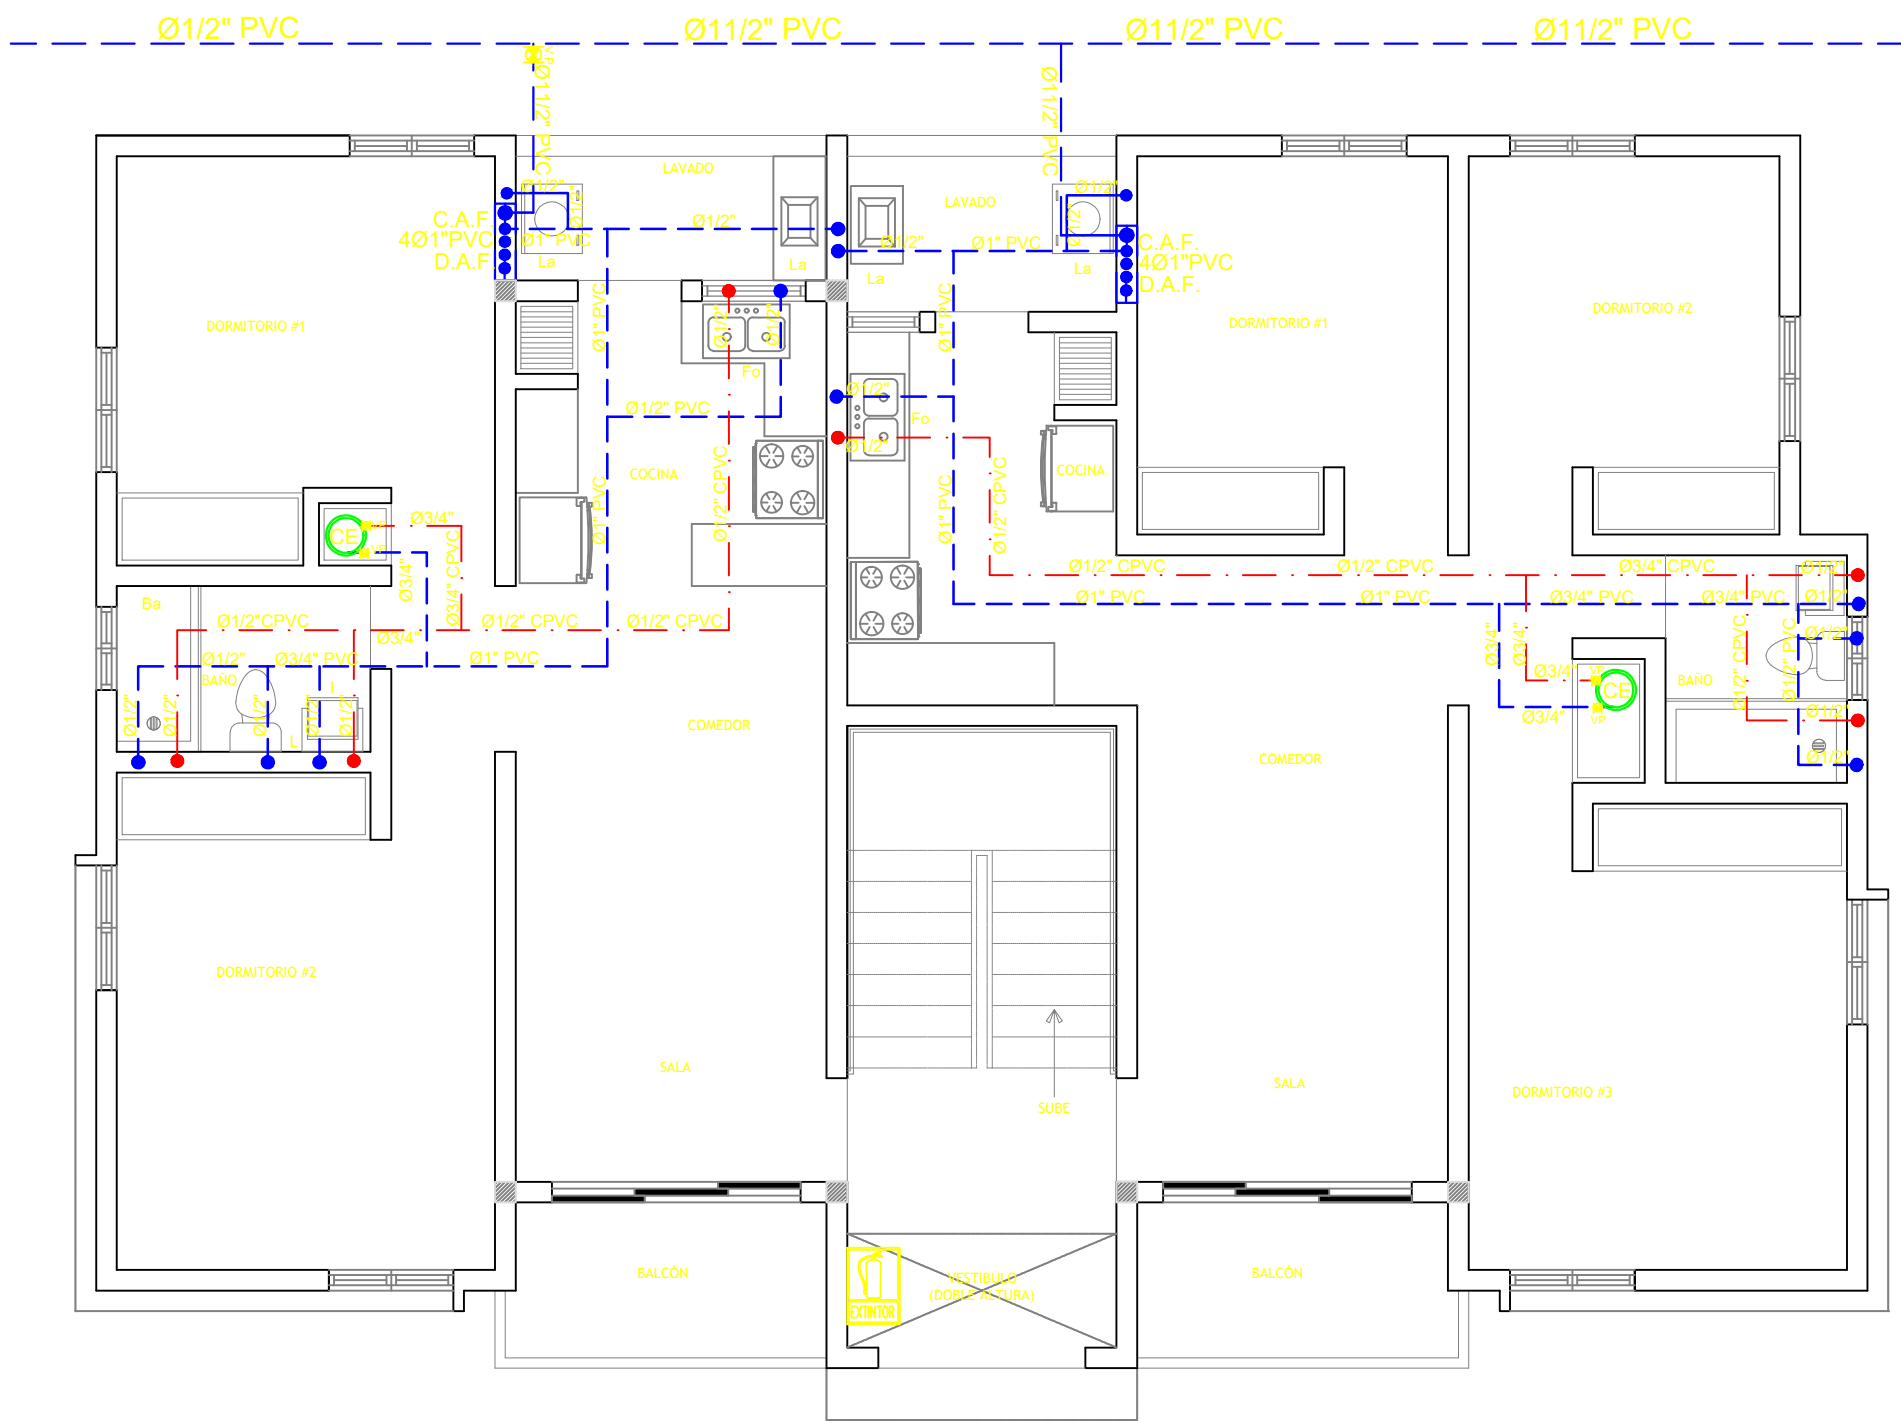


PLANTA DISTRIBUCION AGUA FRIA Y CALIENTE DE 1ER. NIVEL, BLOQUE A

ESCALA: 1:75

1

S05

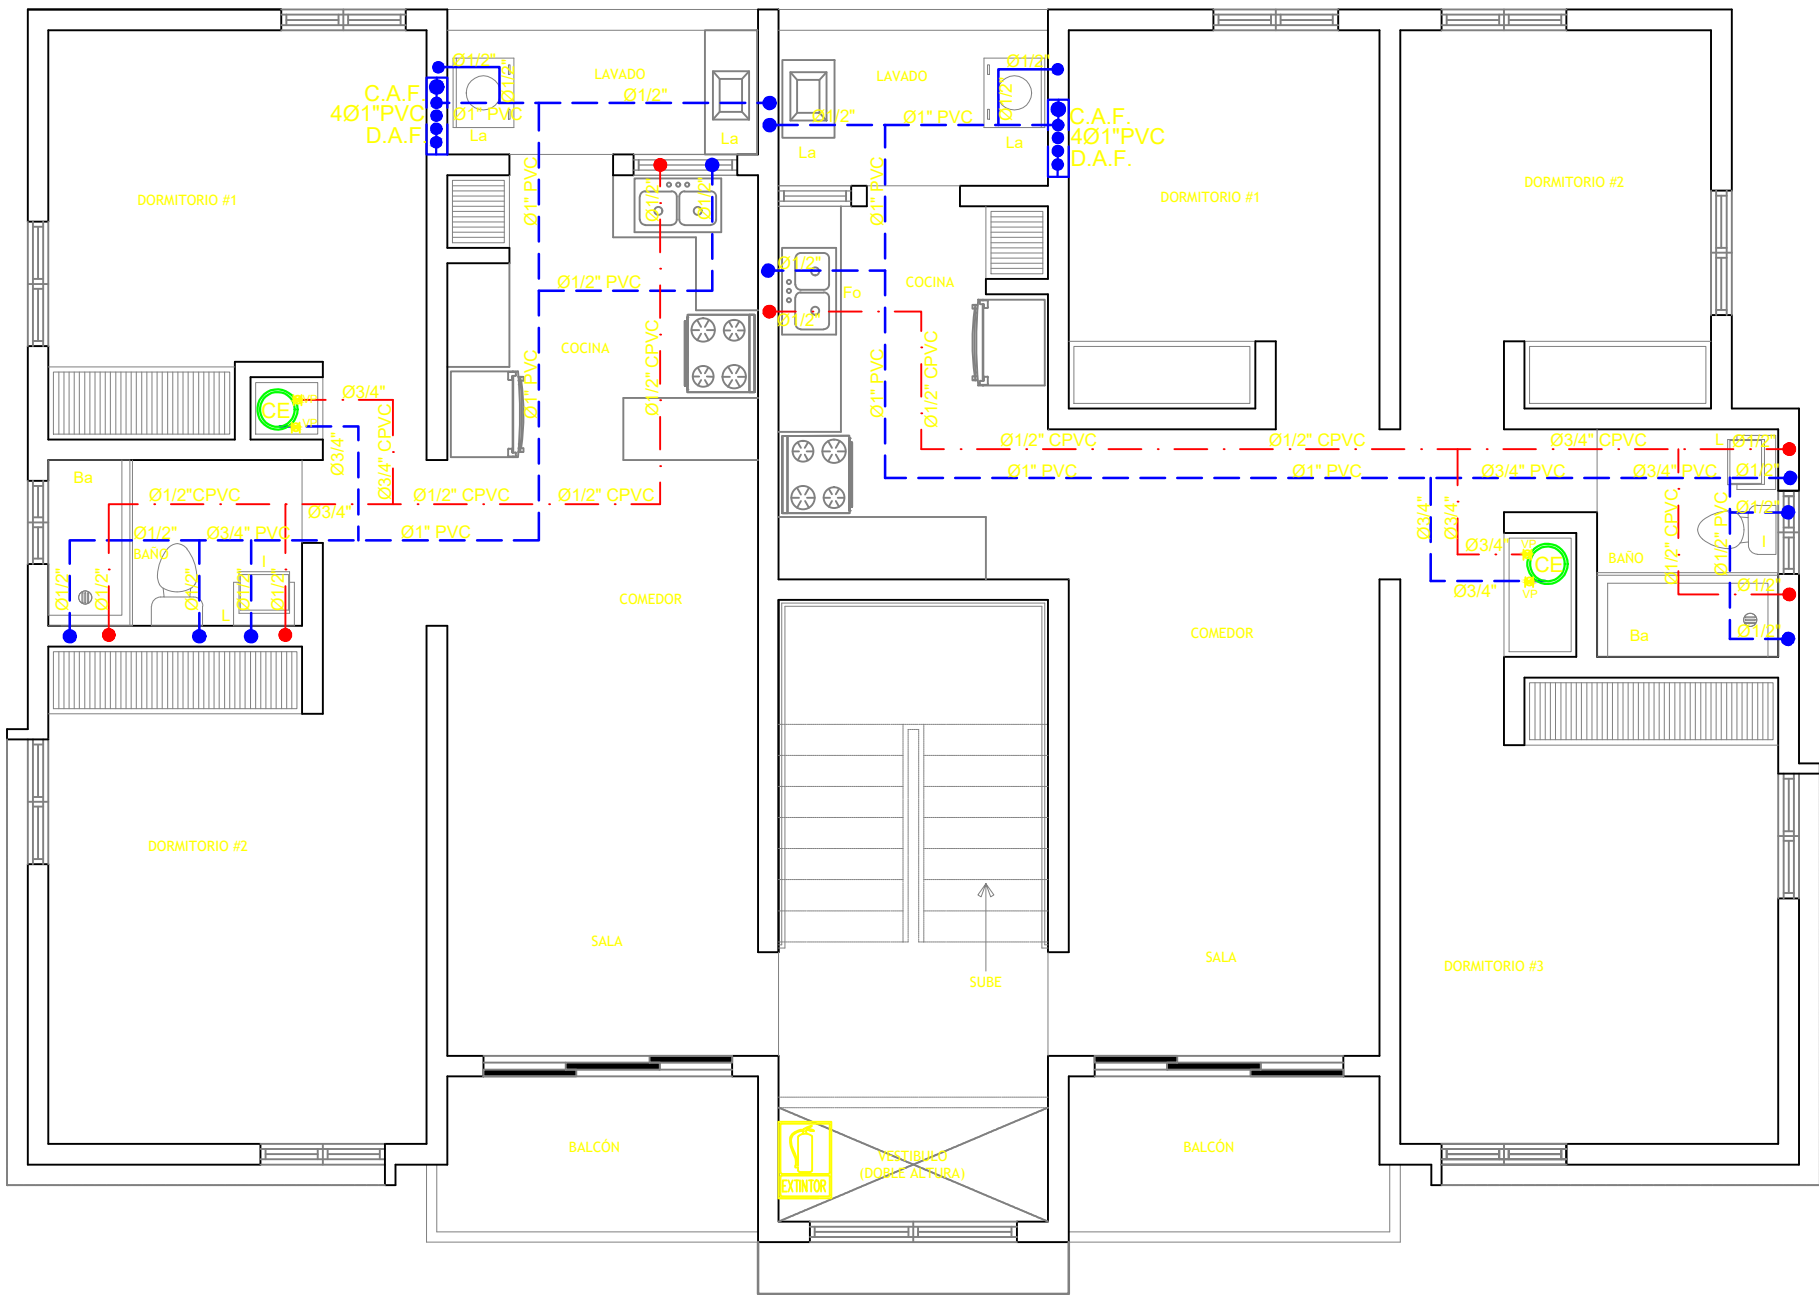


PLANTA DISTRIBUCION AGUA FRIA Y CALIENTE DE 2DO NIVEL, BLOQUE A

ESCALA: 1:75

2

S05

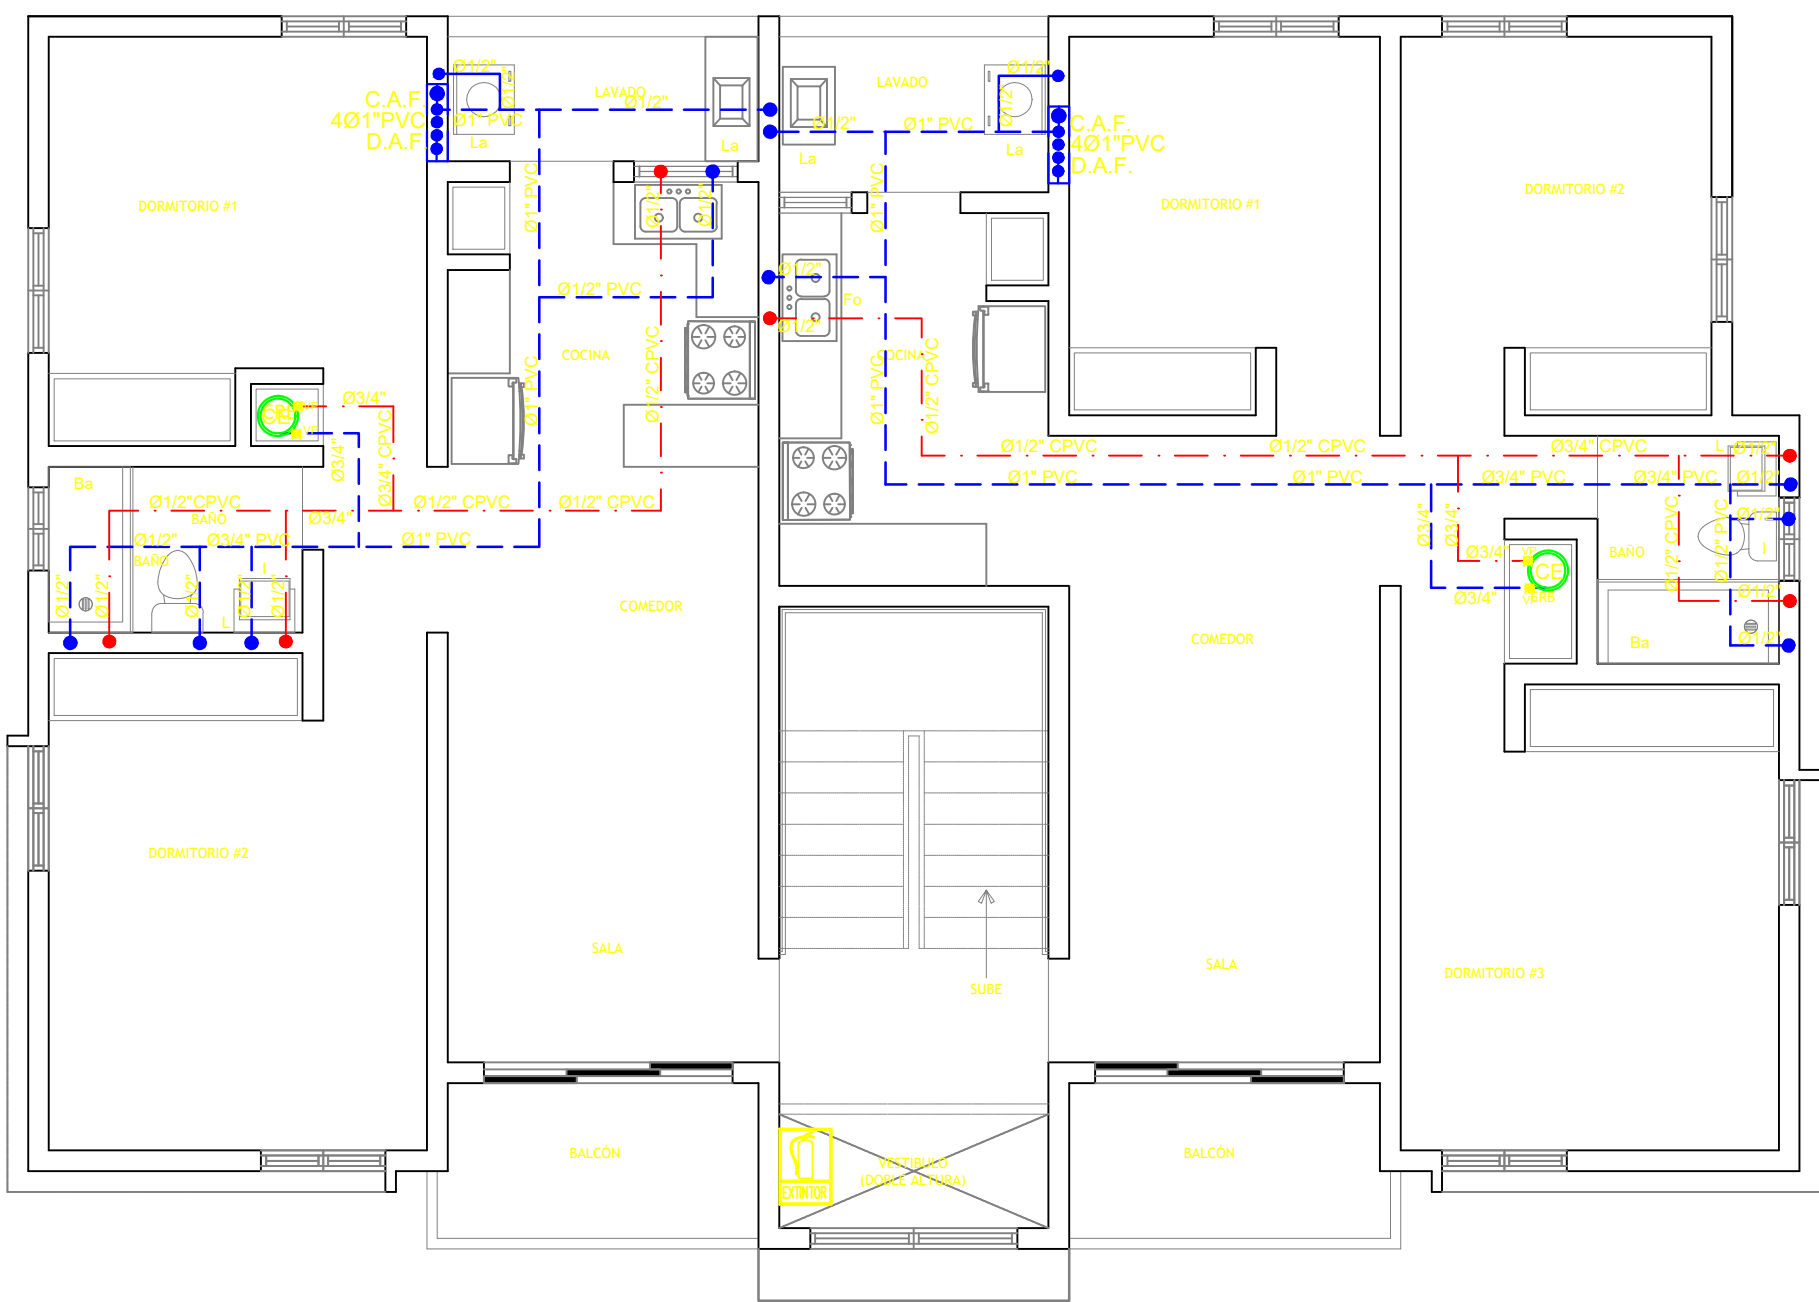


PLANTA DISTRIBUCION AGUA FRIA Y CALIENTE DE 3ER. NIVEL, BLOQUE A

ESCALA: 1:75

3

S05

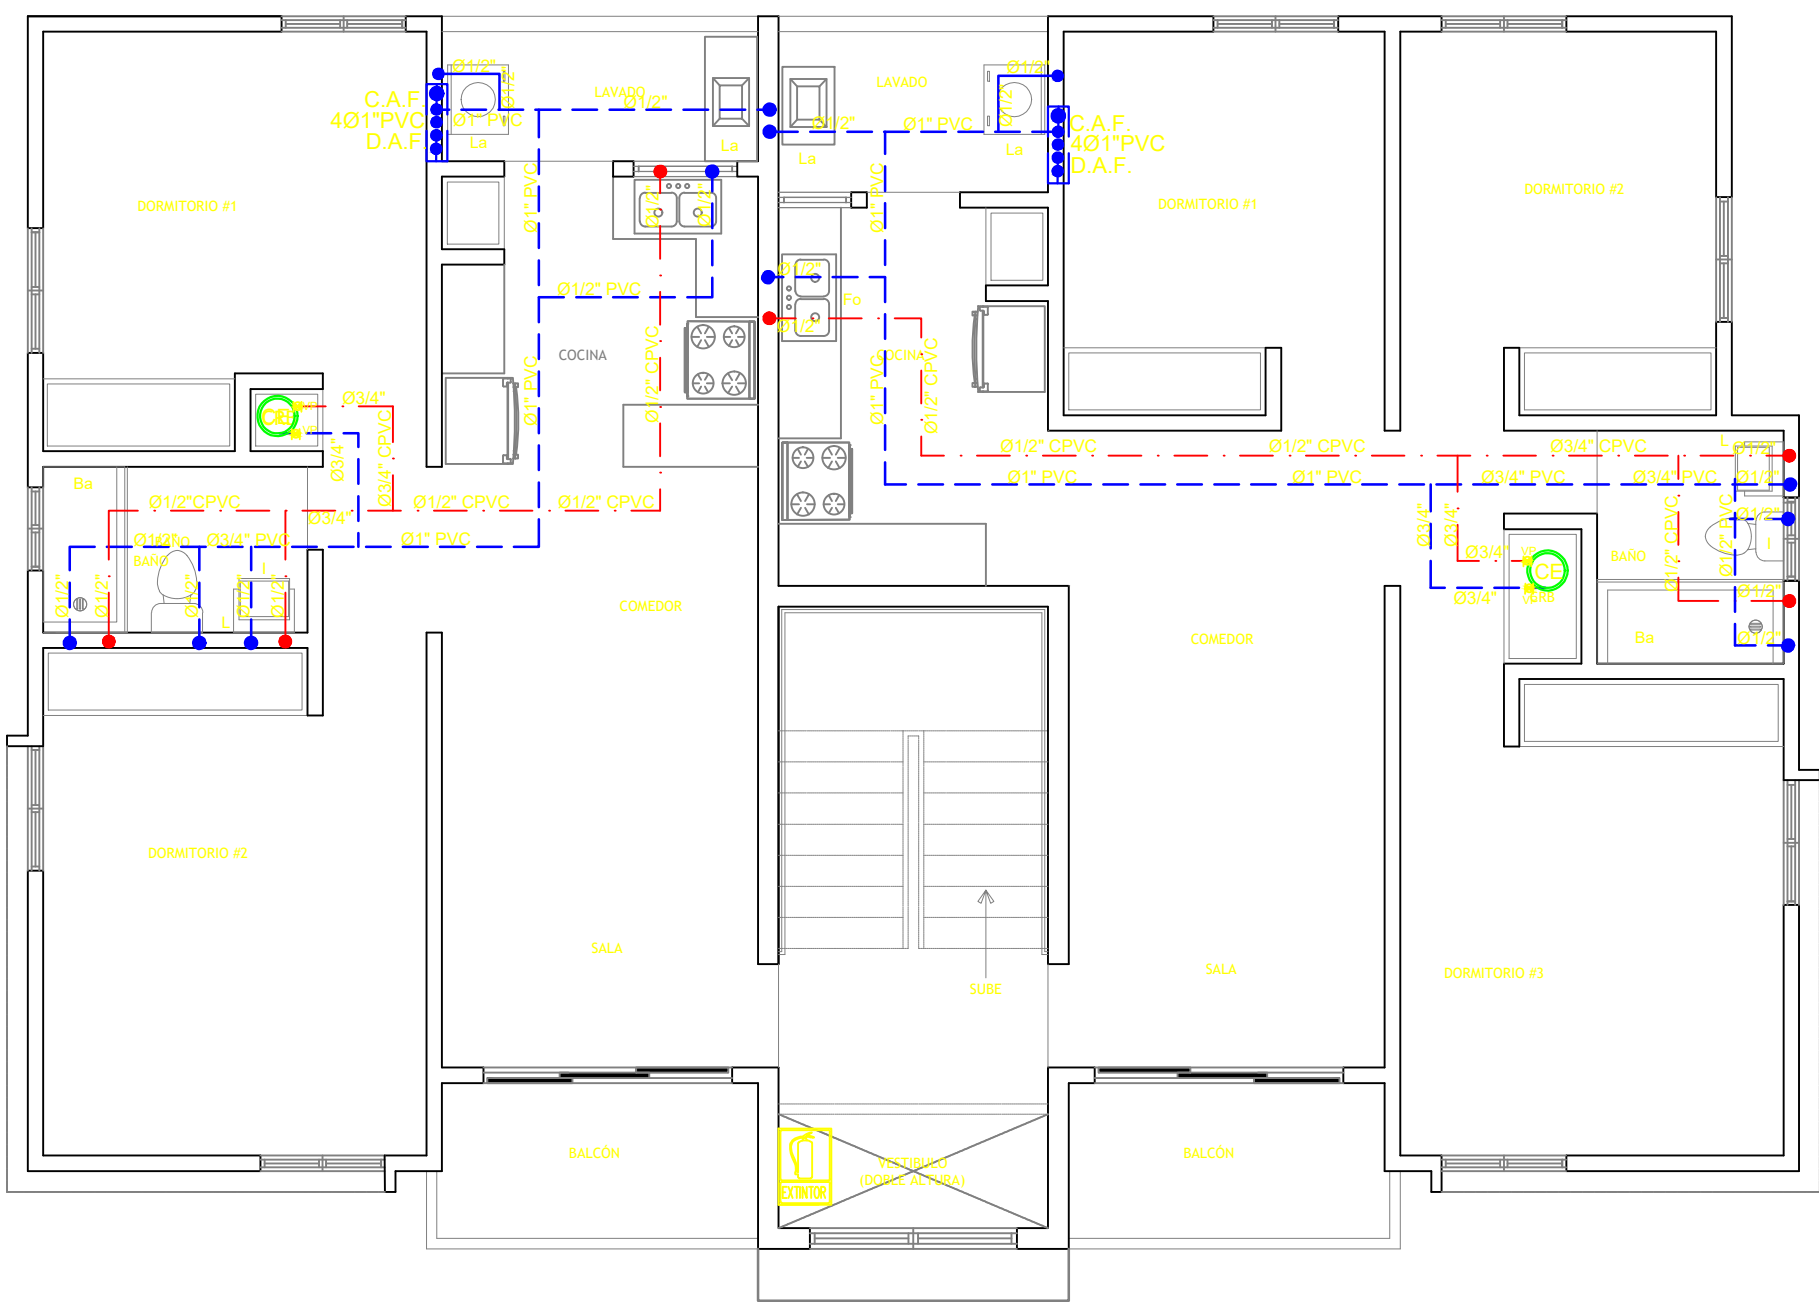

PLANTA DISTRIBUCION AGUA FRIA Y CALIENTE DE 4TO NIVEL, BLOQUE A

ESCALA: 1:75

4

S05



diazmeo & asocs.

ARQUITECTOS

Presidente Biliini # 12, Bani, R.D. 522-4989

E-mail: diazmeo@hotmail.com

COLABORACION:



ARQUITECTURA DIGITAL
DISEÑOS-CONSTRUCCION-DIGITACION
COMPROMETIDOS CON SU TIEMPO
C/JUAN SANCHEZ RAMIREZ #56,
LOCAL 5 ZONA UASD TEL:221-5400

PROPIETARIO :
**GRUPO EMPRESARIAL
BANILEJO S.R.L.
GEBSA**

PROYECTISTAS:

DISEÑO ARQUITECTONICO:
DIAZMELO & ASOCS.
Arq. ISMAEL DIAZ MELO
Codia: 9604

DISEÑO SANITARIO:
Arq. HAMLET TEJEDA
Codia: 18303

DISEÑO ESTRUCTURAL:
ING. ODELIN TEJEDA
Codia: 23937

DISEÑO ELECTRICO:
ING. VILLYS SANCHEZ
Codia: 19060

CONTENIDO:
PLANTAS AGUA POTABLE


PROYECTO:
RESIDENCIAL GEBSA IV

Fecha: **MARZO/2020**

UBICACION:
BANI, PROV. PERAVIA

Ref.: Acad 2000	Hoja No.
Escala: INDICADA	2


NOTAS:
TODAS LAS TERMINACIONES Y/O CAMBIOS EN EL SET. DE DOCUMENTOS CONSTRUCTIVOS DEBERAN SER APROBADOS POR EL SUPERVISOR PREVIAMENTE A SU APLICACION EN LA OBRA.
TODAS LAS MEDIDAS DE HUECOS Y DE SUPERFICIE A SER REVESTIDAS SERAN RECTIFICADAS PREVIA FABRICACION DE LOS CERRRES O LA O LA INSTALACION DE LOS RECURBIMIENTOS
LAS TERMINACIONES Y / O DETALLES NO ESPECIFICADOS SERAN DEFINIDOS ENTRE EL DUEÑO Y EL AUTOR DEL PROYECTO.
EL CONTRATISTA NO PODRA TOMAR DECISIONES INCONSULTAS RESPECTO VARIACIONES EN EL CONTENIDO DE ESTE DOCUMENTO
LOS PLANOS ARQUITECTONICOS MANDARAN RESPECTO A LOS DEMAS A ANTE CUALQUIER DIFERENCIA, PRIMARA LA INFORMACIONCONTENIDA EN LOS MISMOS

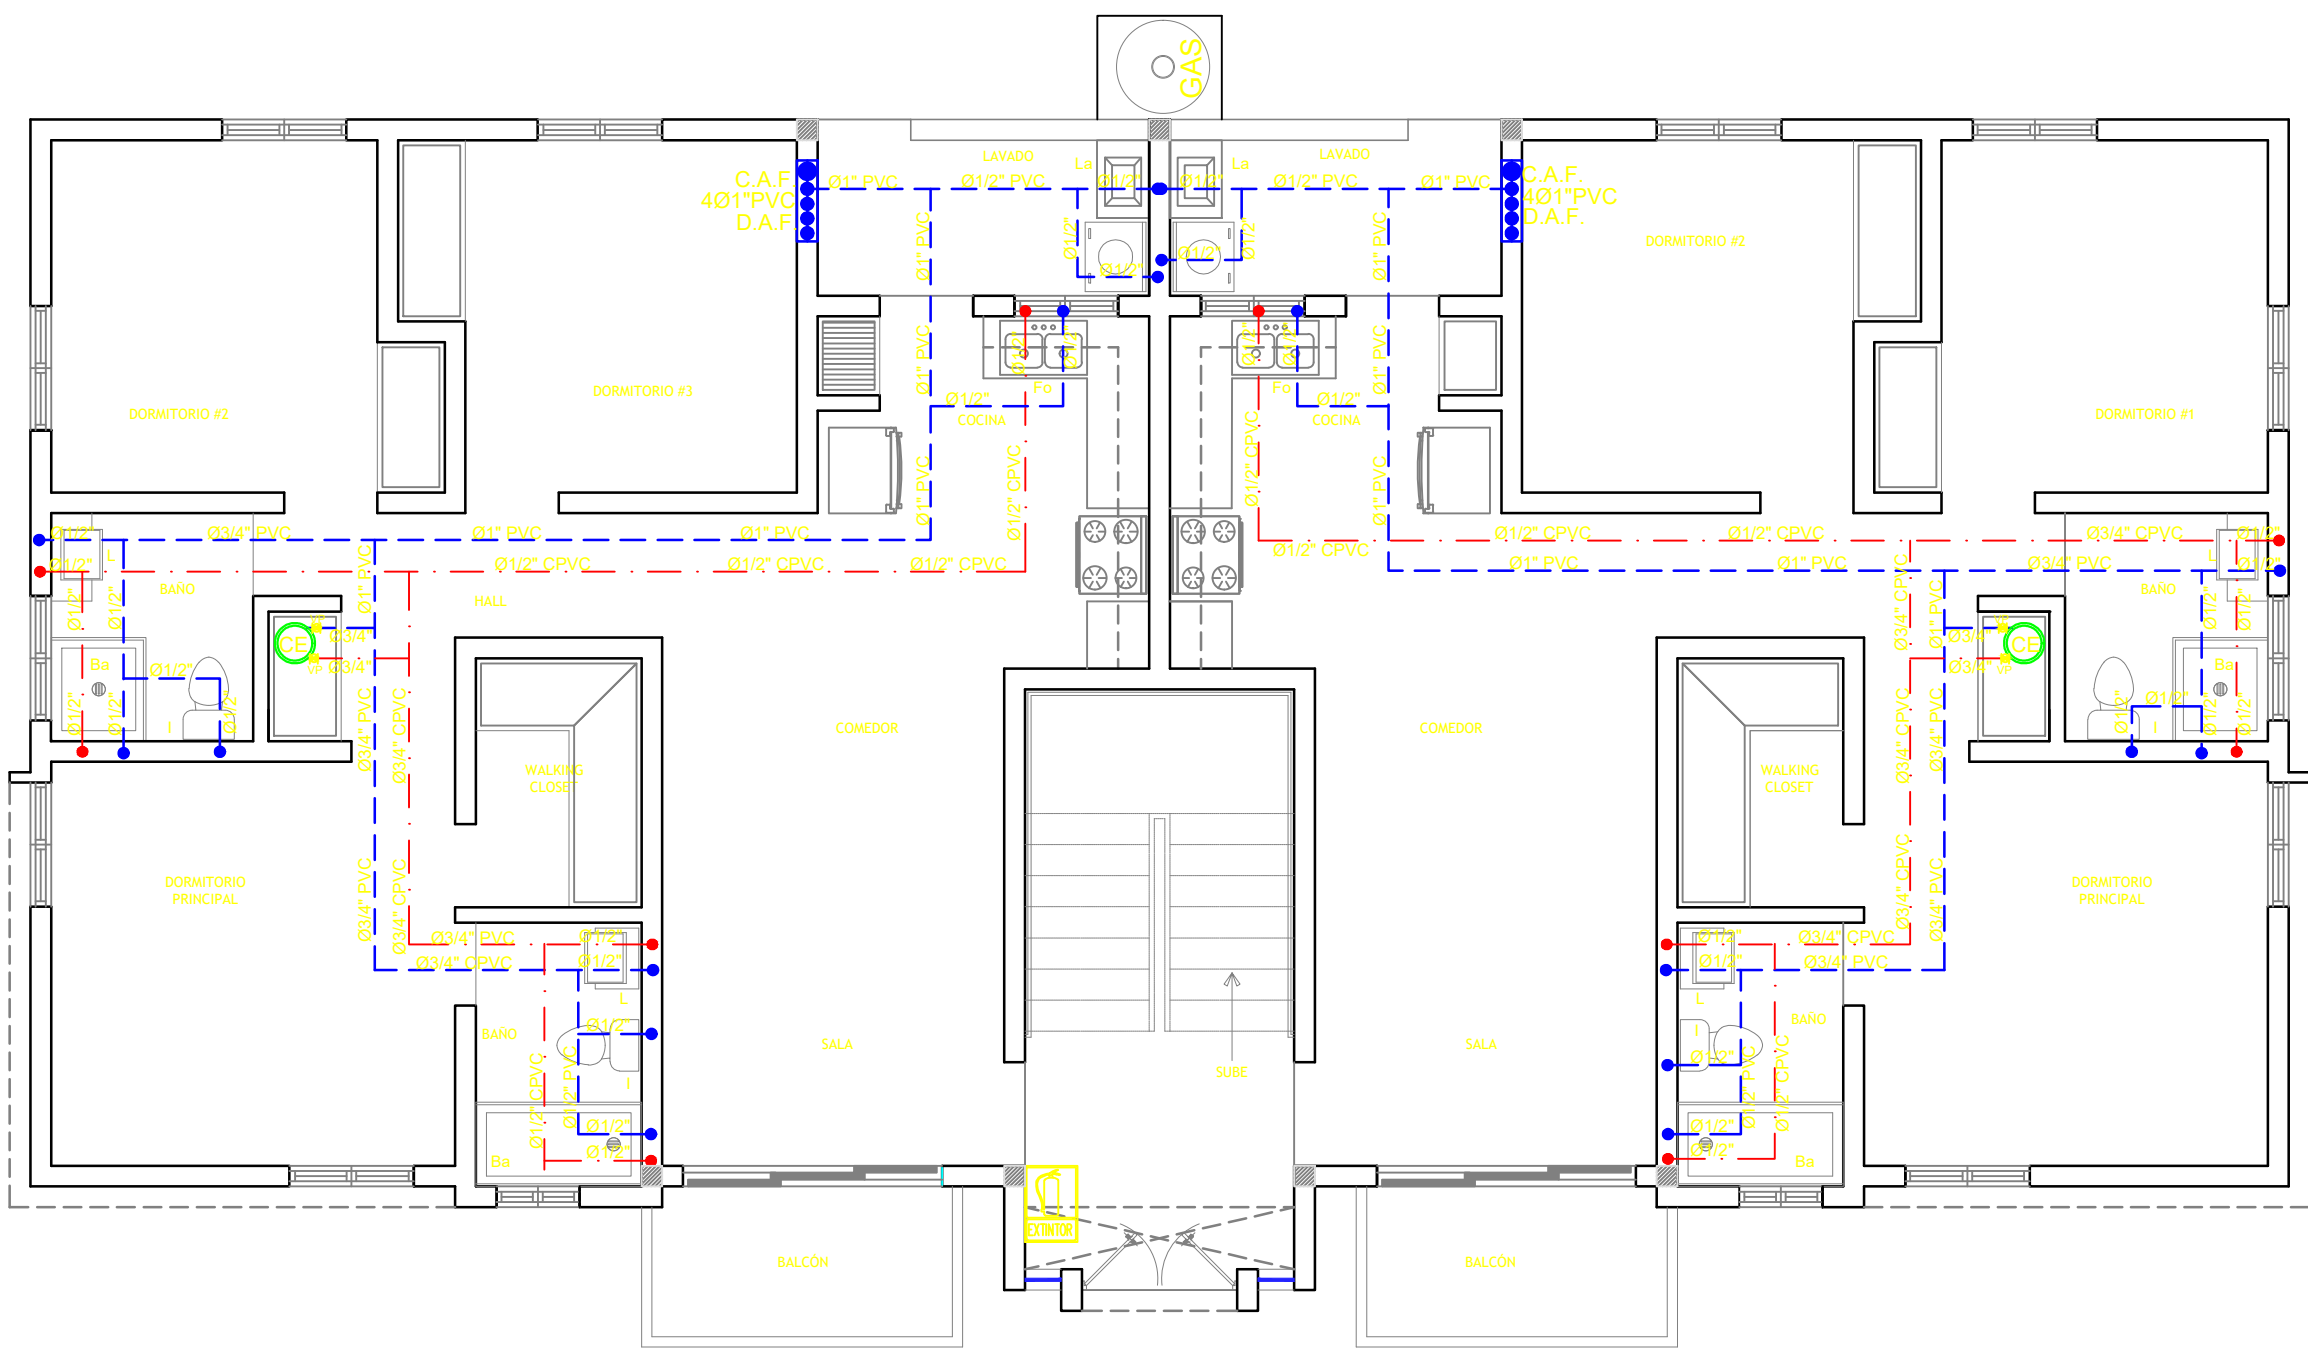

PLANTA DISTRIBUCION AGUA FRIA Y CALIENTE DE 1ER. NIVEL, BLOQUE B

1

S06

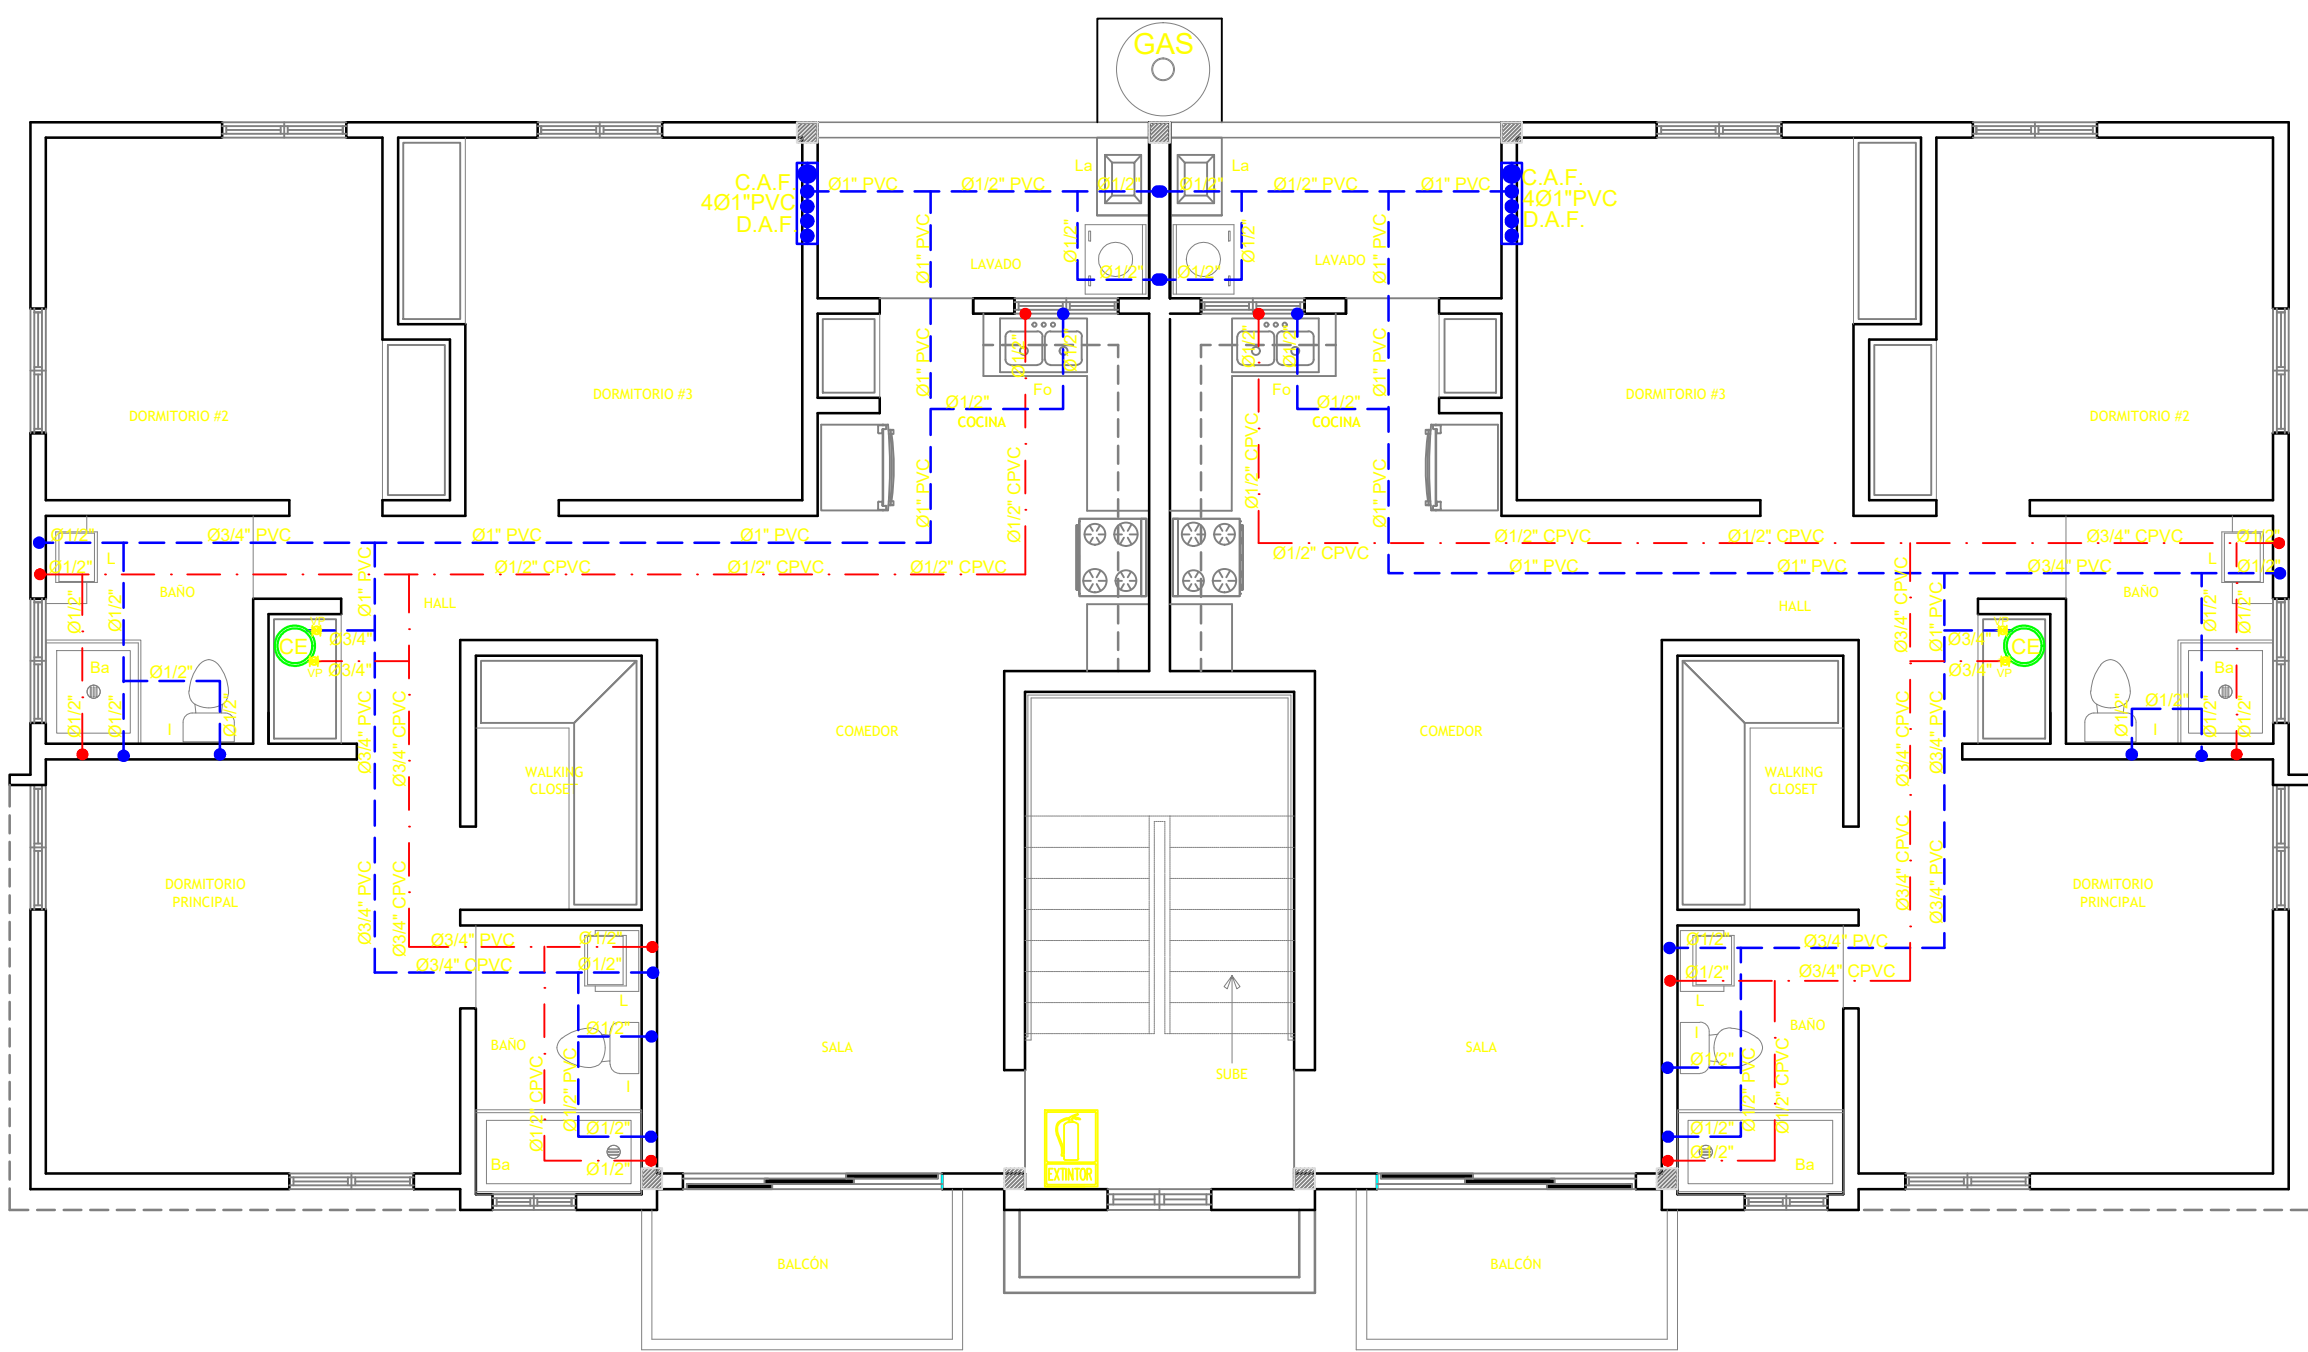


PLANTA DISTRIBUCION AGUA FRIA Y CALIENTE DE 3ER. NIVEL, BLOQUE B

3

S06

ESCALA: 1:75

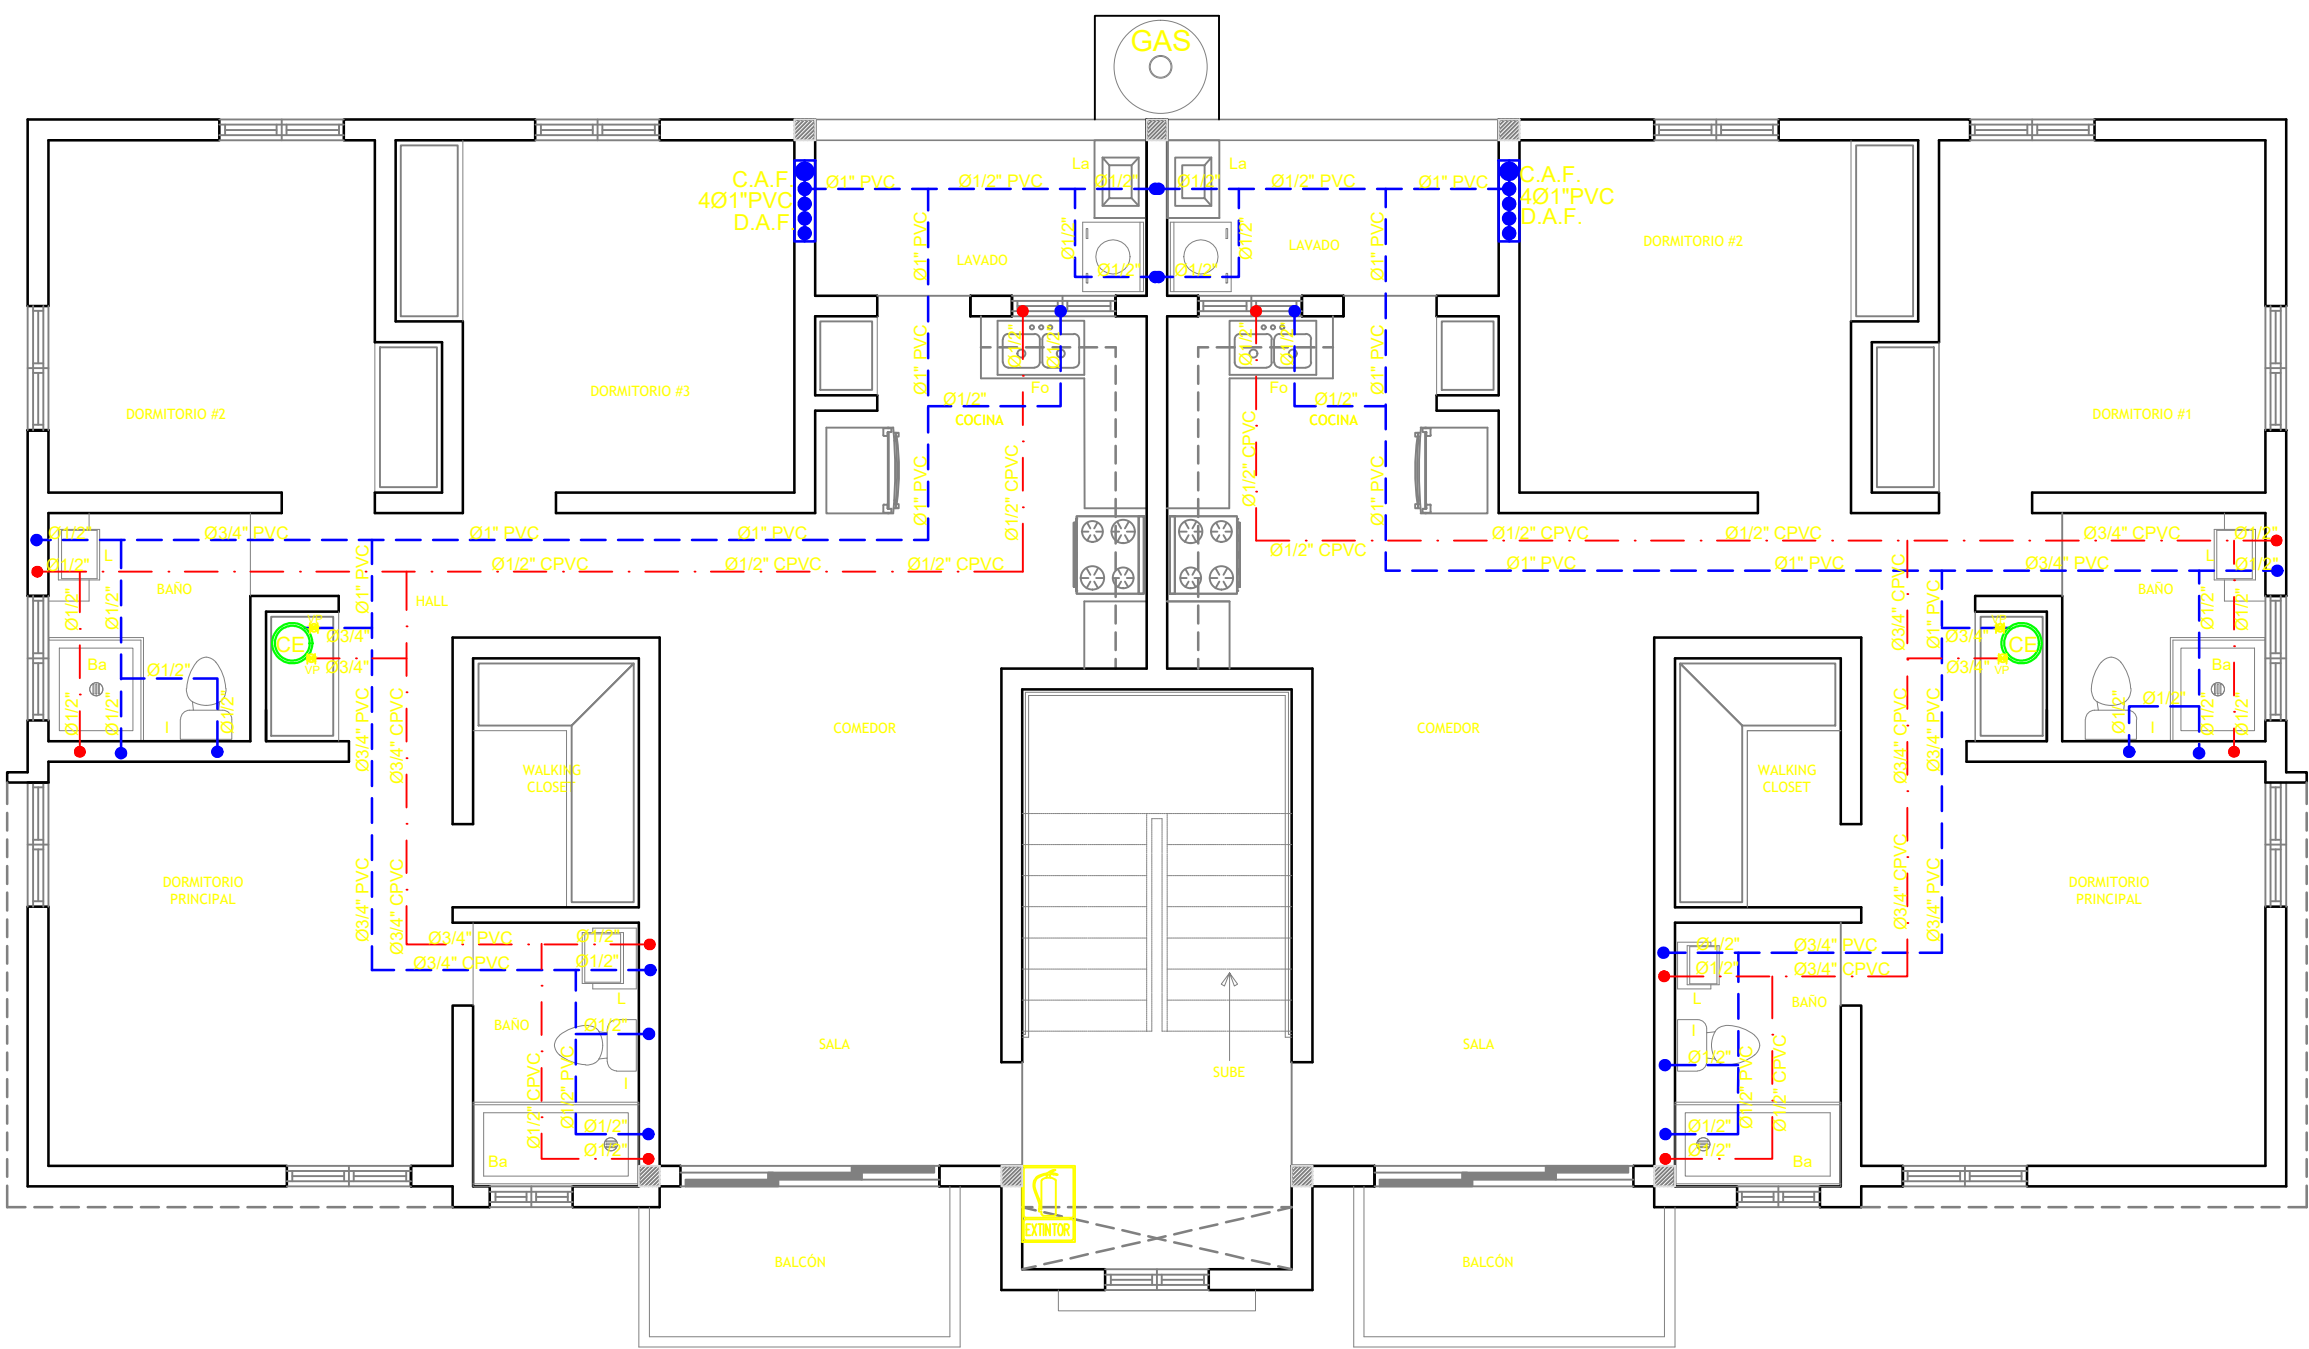

PLANTA DISTRIBUCION AGUA FRIA Y CALIENTE DE 2DO NIVEL, BLOQUE B

2

S06

ESCALA: 1:75

LEYENDA	
Bs	BANERA
BD	BAIANTE DESCARGA
L	LAVAMANO
CSP	CAMARA SEPTICA
U	UNIDORO
V	VENTILACION
D	DESAGUE DE PISO (DP)
T.B.	EQUIPO DE BOMBEO
V.R.H.	VALVULA RETENCION HORIZONTAL
V.R.V.	VALVULA RETENCION VERTICAL
L	COLUMNA AGUAS RESIDUALES
CAF	COLUMNA AGUA FRIA (CAF)
P.V.P.	CILINDRO DE POLIVINILO
CV	COLUMNA VERTICAL AGUA FRIA
O	ORINAL
VP	VALVULA DE PASO (VP)
T.R.	TAPON DE REGISTRO (TR)
C.V.	CAJA DE VALVULA
C.I.	CAJA DE INSPECCION (CI)
L.J.	LLAVE DE JARDIN
Ds	DUCHA
P.F.	POZO FILTRANTE (PF)
S	PENDIENTE
O	DIAMETRO
T.H.	TANQUE HIDRONEUMATICO
DP	DESAGUE DE PISO
F	FRIGADERO
L.V.	LAVADERO
L.A.	LAVADORA
CE	CALENTADOR ELECTRICO
DT	DESAGUE DE TECTO
L.H.	LIMA HOYA
L.T.	LIMA TESA
CI	CAJA DE INSPECCION
TG	TRAMPA DE GRASA
S	PENDIENTE
L.V.M.	TUBERIA EXTRACCION MECANICA
EX	EXTRACTOR MECANICO
D.A.F.	DISTRIBUIDOR AGUA FRIA - D.A.F.
D.G.L.P.	DISTRIBUIDOR G.L.P. - D.G.L.P.
C.C.I.	COLUMNA CONTRA INCENDIO
C.C.I.	CABINETE CONTRA INCENDIO
RED	RED DE AGUAS RESIDUALES
RED	RED DE AGUA FRIA
TANQUE DE GAS	TANQUE DE GAS

LEYENDA SANITARIA

S=1 NO ESCALA

NOTAS:
TODAS LAS TUBERIAS QUE USAN LOS SISTEMAS DE AGUAS RESIDUALES Y PLANTAL SERAN DE P.V.C.
LAS TUBERIAS DE DISTRIBUCION DE AGUA FRIA SERAN EN TUBERIA SCH-40 PVC.
Y LAS DE AGUAS RESIDUALES SERAN EN TUBERIA SCH-20.
LAS TUBERIAS DE DISTRIBUCION DE AGUA CALIENTE SERAN EN TUBERIA CPVC.
LA PENDIENTE PARA EL SISTEMA DE DESAGUE DE AGUAS RESIDUALES SERAN "A" 2%
EL AGUA PLANTAL DEL PRIMER NIVEL SERA SEA SACADA HACIA EL CONTENEDOR CON UNA PENDIENTE - 2%
LOS GABINETES CONTRA INCENDIO SE COLOCARAN EN CADA NIVEL, SERAN EN TUBERIA D3" E.G. CON MANGUERAS DE 100'



diaz melo & asocs.

ARQUITECTOS

Presidente Biliini # 12, Bari, R.D. 522-4989

E-mail: diazmelo@hotmail.com

COLABORACION:



ARQUITECTURA DIGITAL
DISEÑOS-CONSTRUCCION-DIGITACION
COMPROMETIDOS CON SU TIEMPO
C/JUAN SANCHEZ RAMIREZ #56,
LOCAL 5 ZONA UASD TEL:221-5400

PROPIETARIO:
GRUPO EMPRESARIAL
BANILEJO S.R.L.
GEBSA

PROYECTISTAS:

DISEÑO ARQUITECTONICO:
DIAZMELO & ASOCS.
Arq. ISMAEL DIAZ MELO
Codia: 9604

DISEÑO SANITARIO:
Arq. HAMLET TEJEDA
Codia: 18303

DISEÑO ESTRUCTURAL:
ING. ODELIN TEJEDA
Codia: 23937

DISEÑO ELECTRICO:
ING. VILLYS SANCHEZ
Codia: 19060

CONTENIDO:
PLANTAS AGUA POTABLE

PROYECTO:
RESIDENCIAL GEBSA IV

Fecha: MARZO/2020

UBICACION:

BANI, PROV. PERAVIA

Ref.: Acad 2000

Hoja No.

Escala: INDICADA

3

NOTAS:
TODAS LAS TERMINACIONES Y/O CAMBIOS EN EL SET. DE DOCUMENTOS CONSTRUCTIVOS DEBERAN SER APROBADOS POR EL SUPERVISOR PREVIAMENTE A SU APLICACION EN LA OBRA.
TODAS LAS MEDIDAS DE HUECOS Y DE SUPERFICIE A SER REVESTIDAS SERAN RECTIFICADAS PREVIA FABRICACION DE LOS BARRIOS O LA O LA INSTALACION DE LOS RECURBIMIENTOS
LAS TERMINACIONES Y /O DETALLES NO ESPECIFICADOS SERAN DEFINIDOS ENTRE EL DUEÑO Y EL AUTOR DEL PROYECTO.
EL CONTRATISTA NO PODRA TOMAR DECISIONES INCONSULTAS RESPECTO A LAS VARIACIONES EN EL CONTENIDO DE ESTE DOCUMENTO
LOS PLANOS ARQUITECTONICOS MANDARAN RESPECTO A LOS DEMAS A ANTE CUALQUIER DIFERENCIA, PRIMARA LA INFORMACIONCONTENIDA EN LOS MISMOS



diaz melo & asocs.
ARQUITECTOS

Presidente Billini # 12, Bani, R.D. 522-4989
E-mail: diazmelo@hotmail.com

COLABORACION:



ARQUITECTURA DIGITAL
DISEÑOS-CONSTRUCCION-DIGITACION
COMPROMETIDOS CON SU TIEMPO
C/JUAN SANCHEZ RAMIREZ #56,
LOCAL 5 ZONA UASD TEL:221-5400

PROPIETARIO:

**GRUPO EMPRESARIAL
BANILEJO S.R.L.
GEBSA**

PROYECTISTAS:

**DISEÑO ARQUITECTONICO:
DIAZMELO & ASOCS.**

Arq. ISMAEL DIAZ MELO
Codia: 9604

DISEÑO SANITARIO:

Arq. HAMLET TEJEDA
Codia: 18303

DISEÑO ESTRUCTURAL:

ING. ODELIN TEJEDA
Codia: 23937

DISEÑO ELECTRICO:

ING. VILLYS SANCHEZ
Codia: 19060

CONTENIDO:

RESIDENCIAL GEBSA IV

PROYECTO:

**EDIFICIO DE APARTAMENTOS
CONDOMINIOS DON ISIDRO**

Fecha: MARZO/2020

UBICACION:

SOMBRERO, BANI, PROV. PERAVIA

Ref.: Acad 2000

Hoja No.

Escala: INDICADA

7

NOTAS:



TODAS LAS TERMINACIONES Y/O CAMBIOS EN EL SET DE DOCUMENTOS
CONSTRUCTIVOS DEBERAN SER APROBADOS POR EL SUPERVISOR
PREVIAMENTE A SU APLICACION EN LA OBRA

TODAS LAS MEDIDAS DE HUECOS Y DE SUPERFICIE A SER REVESTIDAS
SERAN RECTIFICADAS PREVIA FABRICACION DE LOS CERRRES O LA
O LA INSTALACION DE LOS RECURBIMIENTOS

LAS TERMINACIONES Y/O DETALLES NO ESPECIFICADOS SERAN
DEFINIDOS ENTRE
EL DUEÑO Y EL AUTOR DEL PROYECTO

EL CONTRATISTA NO PODRA TOMAR DECISIONES
INCONSULTAS RESPECTO VARIACIONES EN EL CONTENIDO
DE ESTE DOCUMENTO

LOS PLANOS ARQUITECTONICOS MANDARAN RESPECTO A LOS DEMAS A
ANTE CUALQUIER
DIFERENCIA, PRIMARA LA INFORMACIONCONTENIDA EN LOS MISMOS

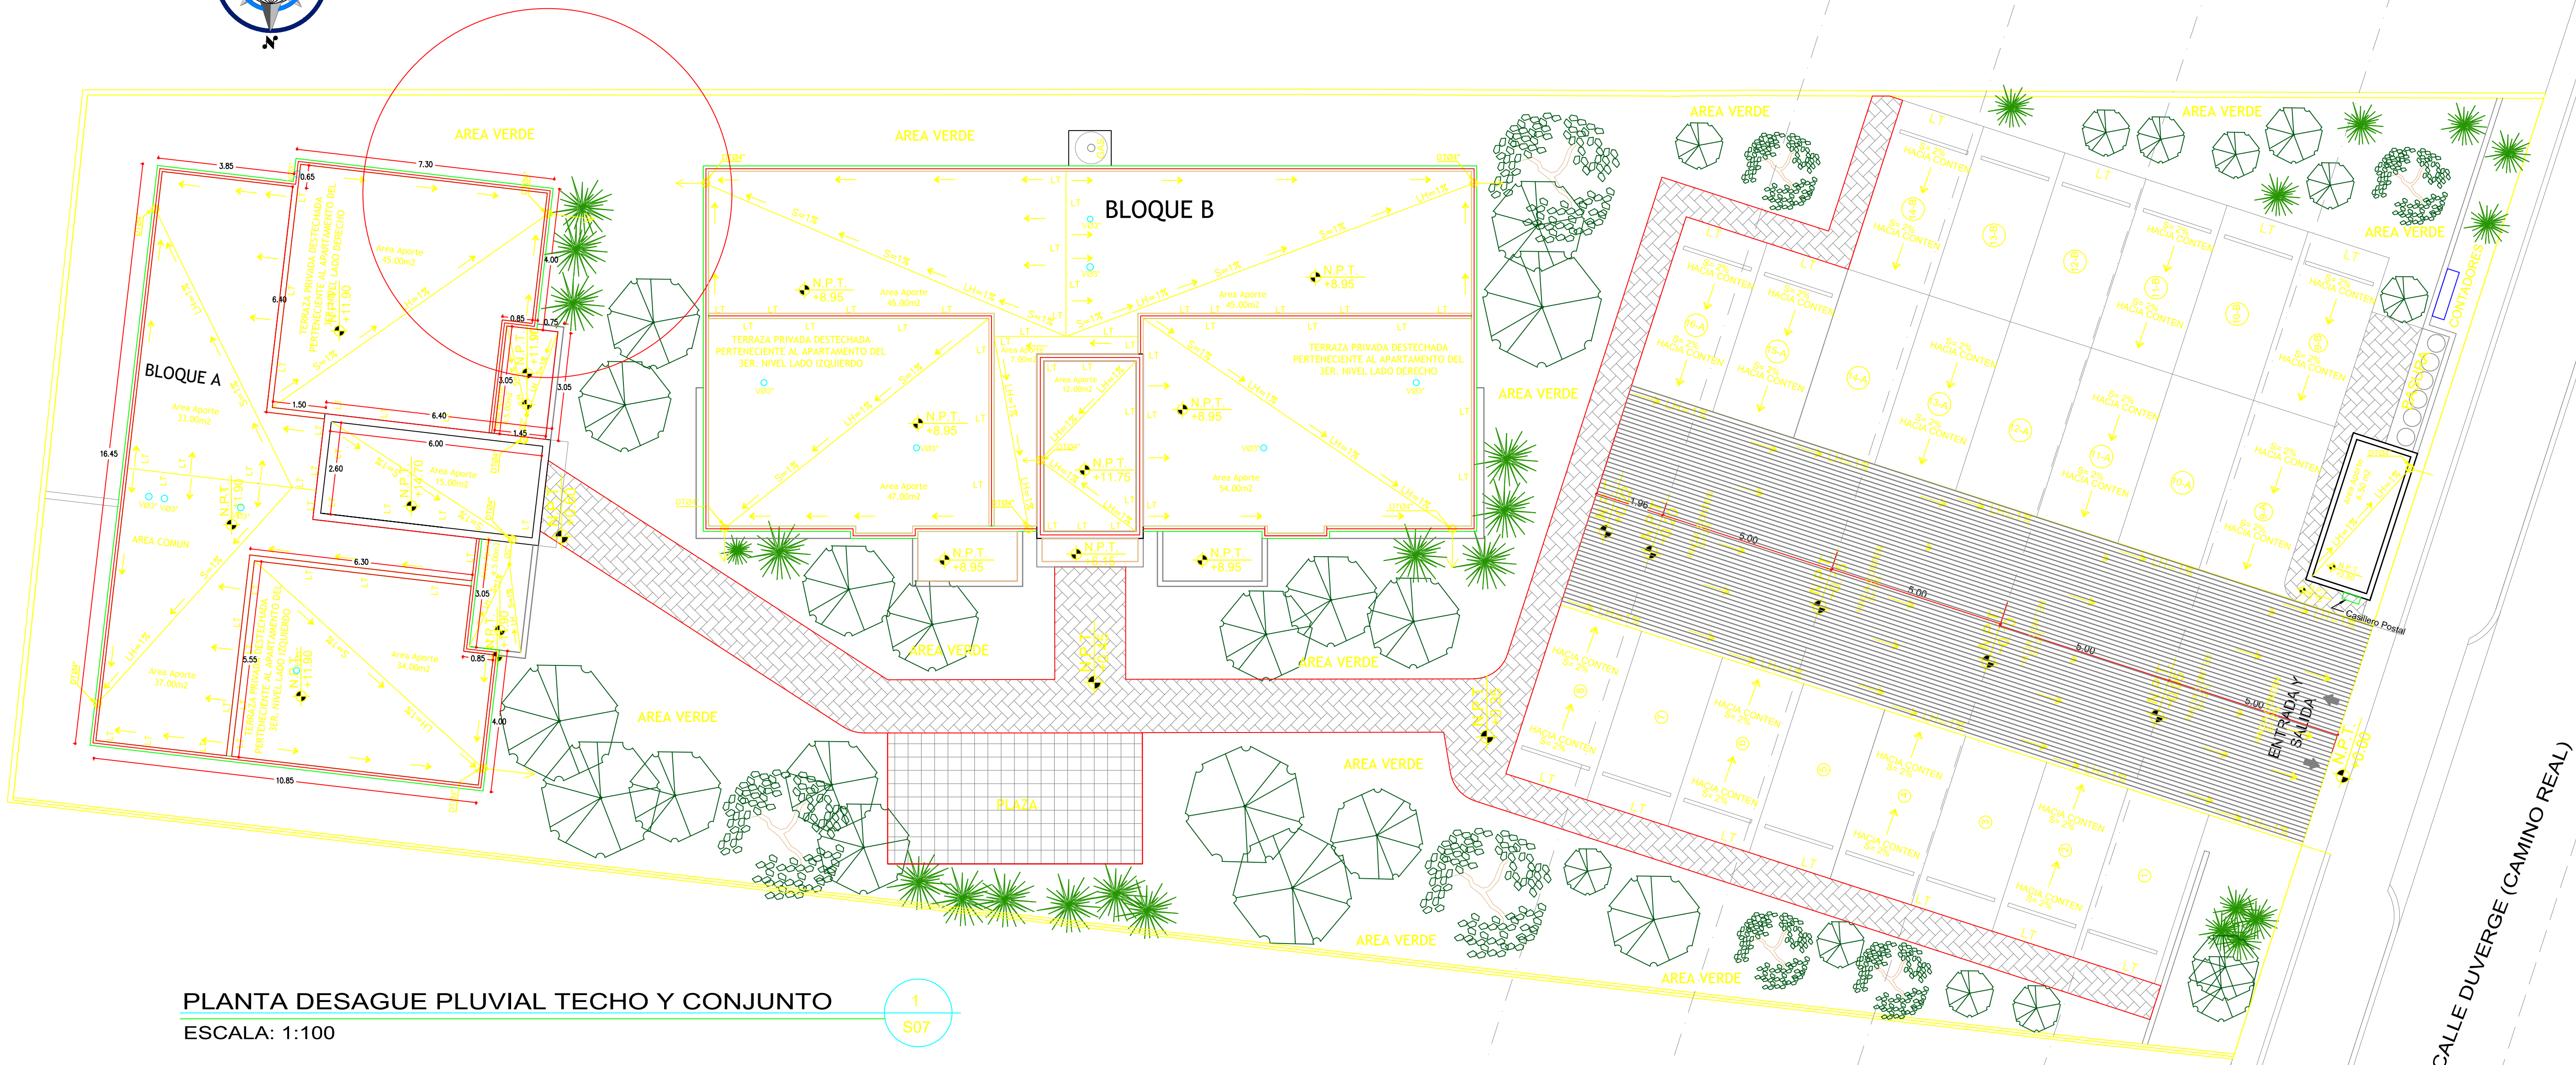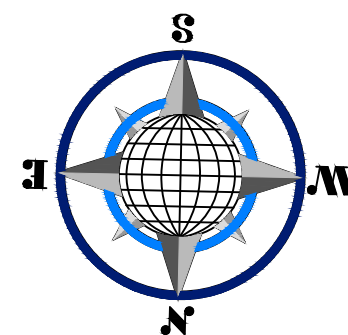


PLANTA DESAGUE PLUVIAL TECHO Y CONJUNTO

ESCALA: 1:100


1

S07

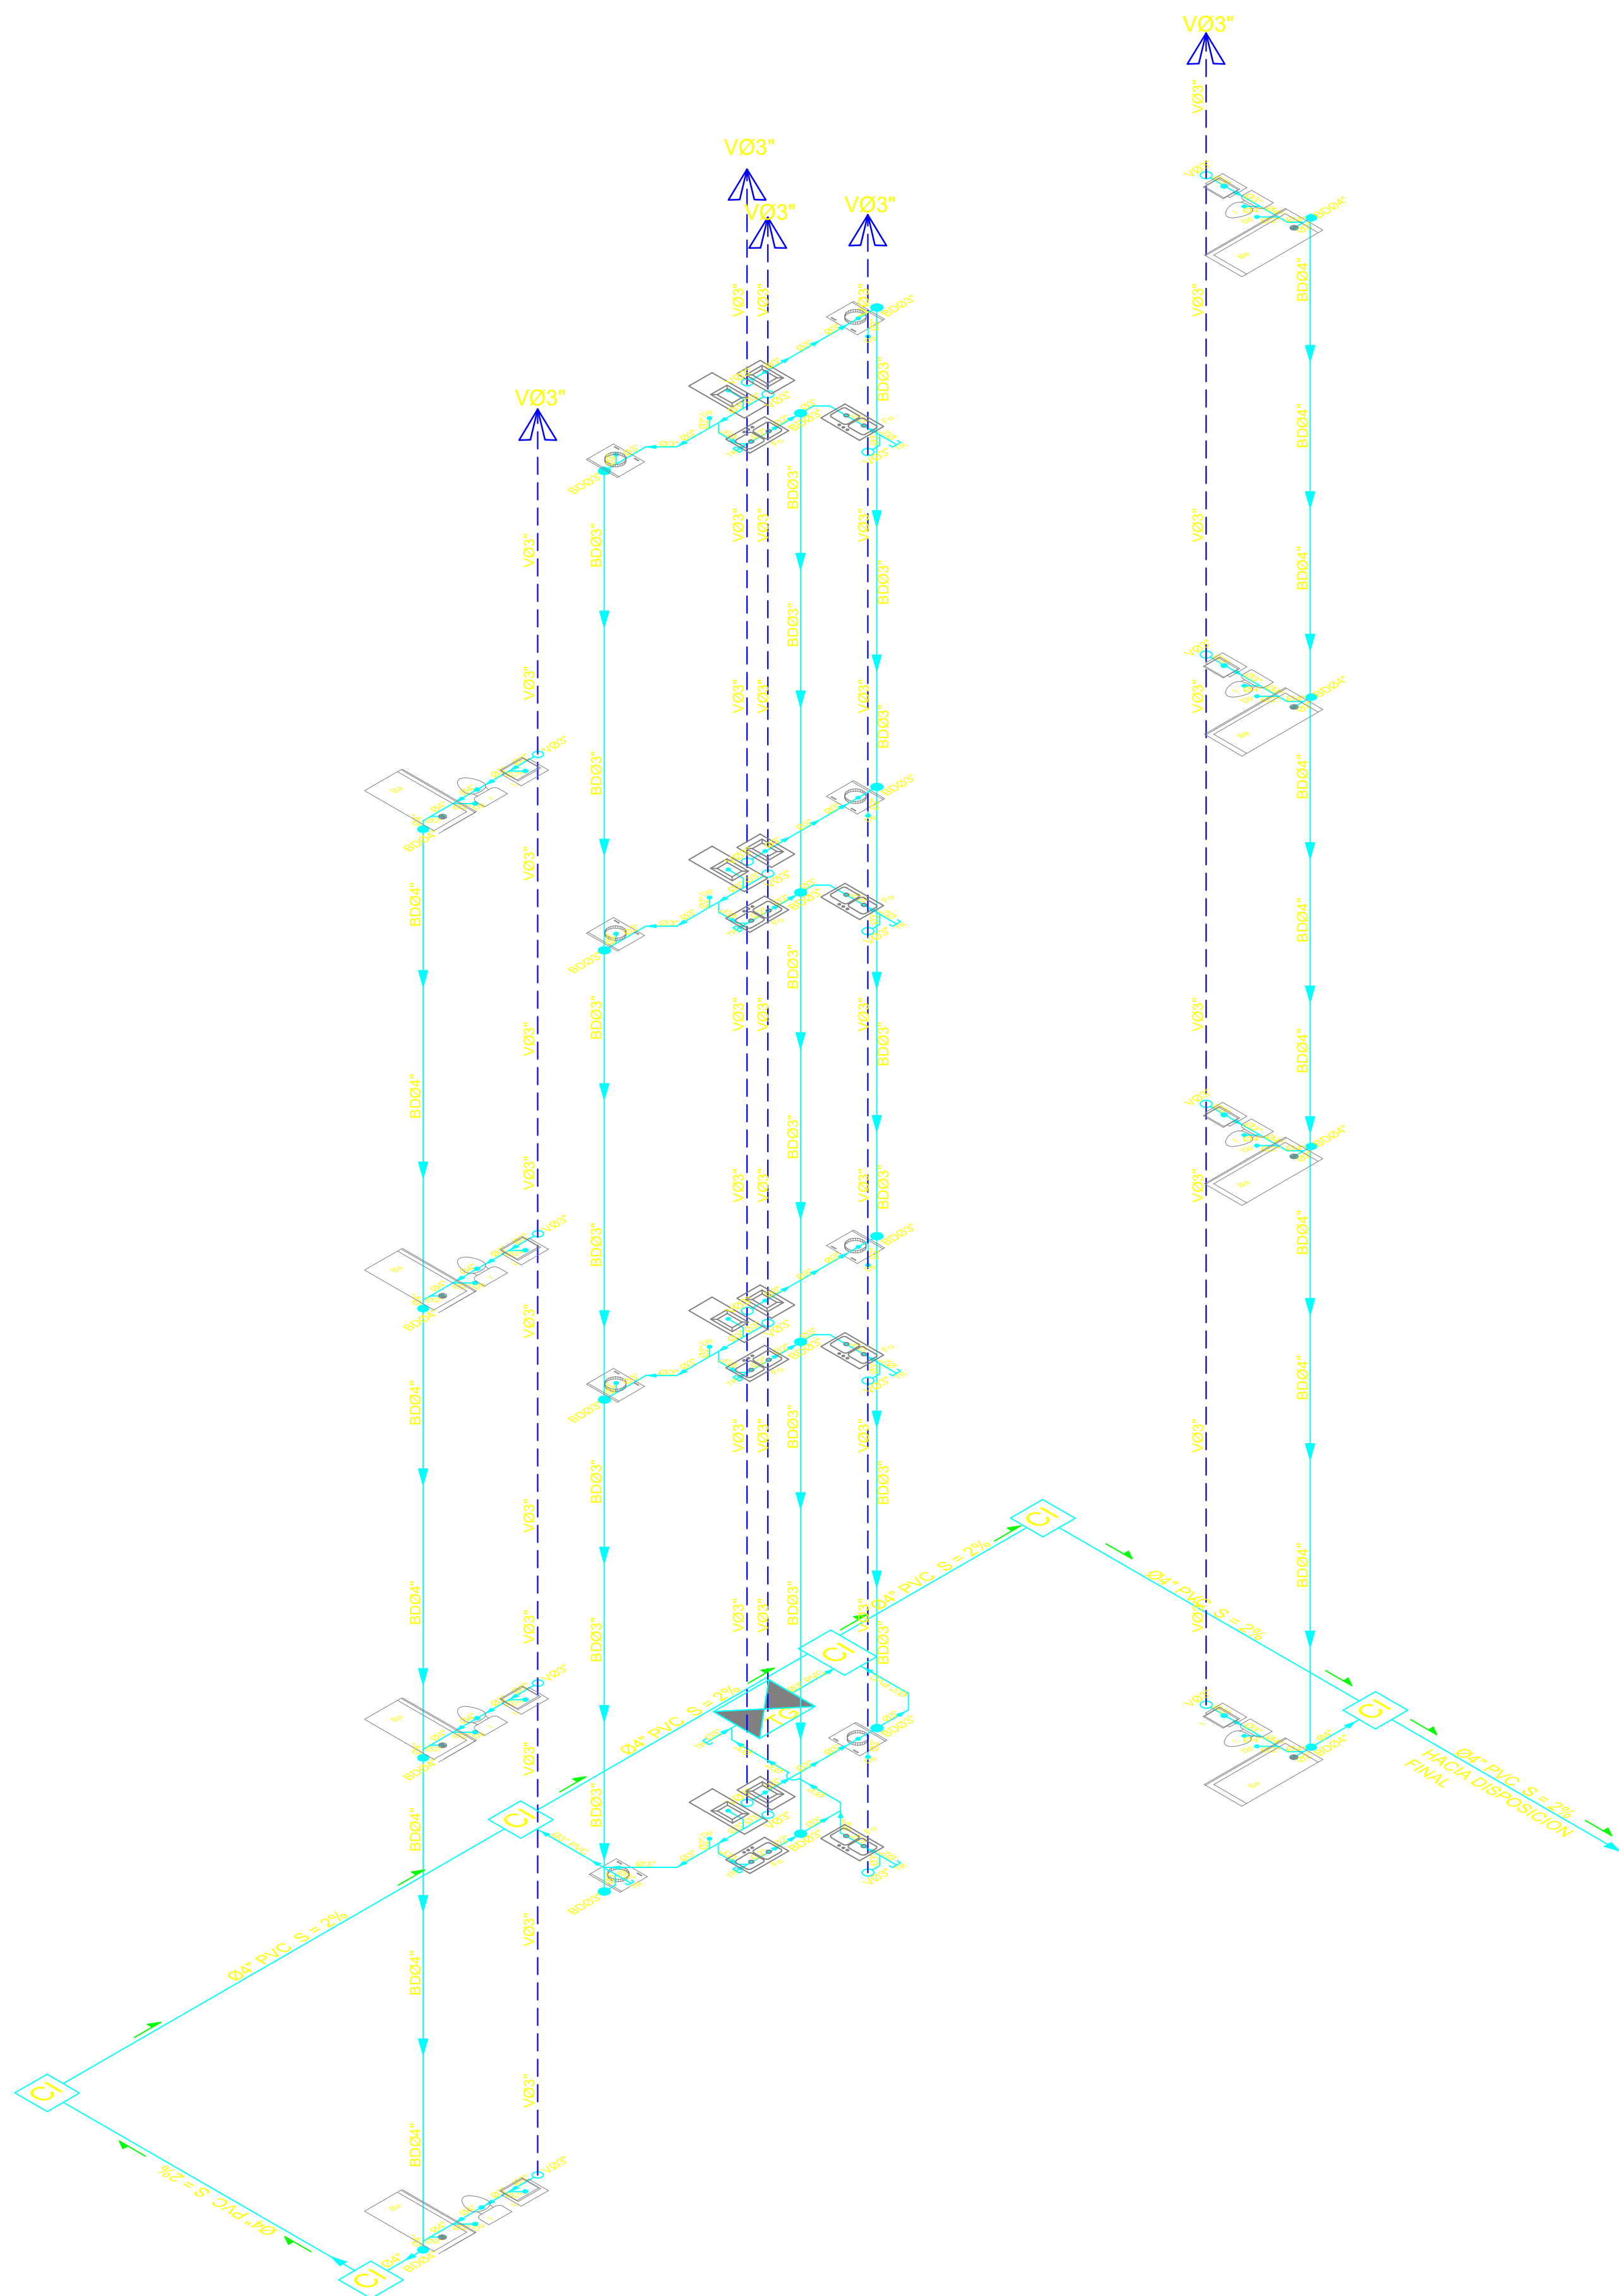

PERSPECTIVA ISOMETRICA AGUAS RESIDUALES BLOQUE B
NO ESCALA

1
S08

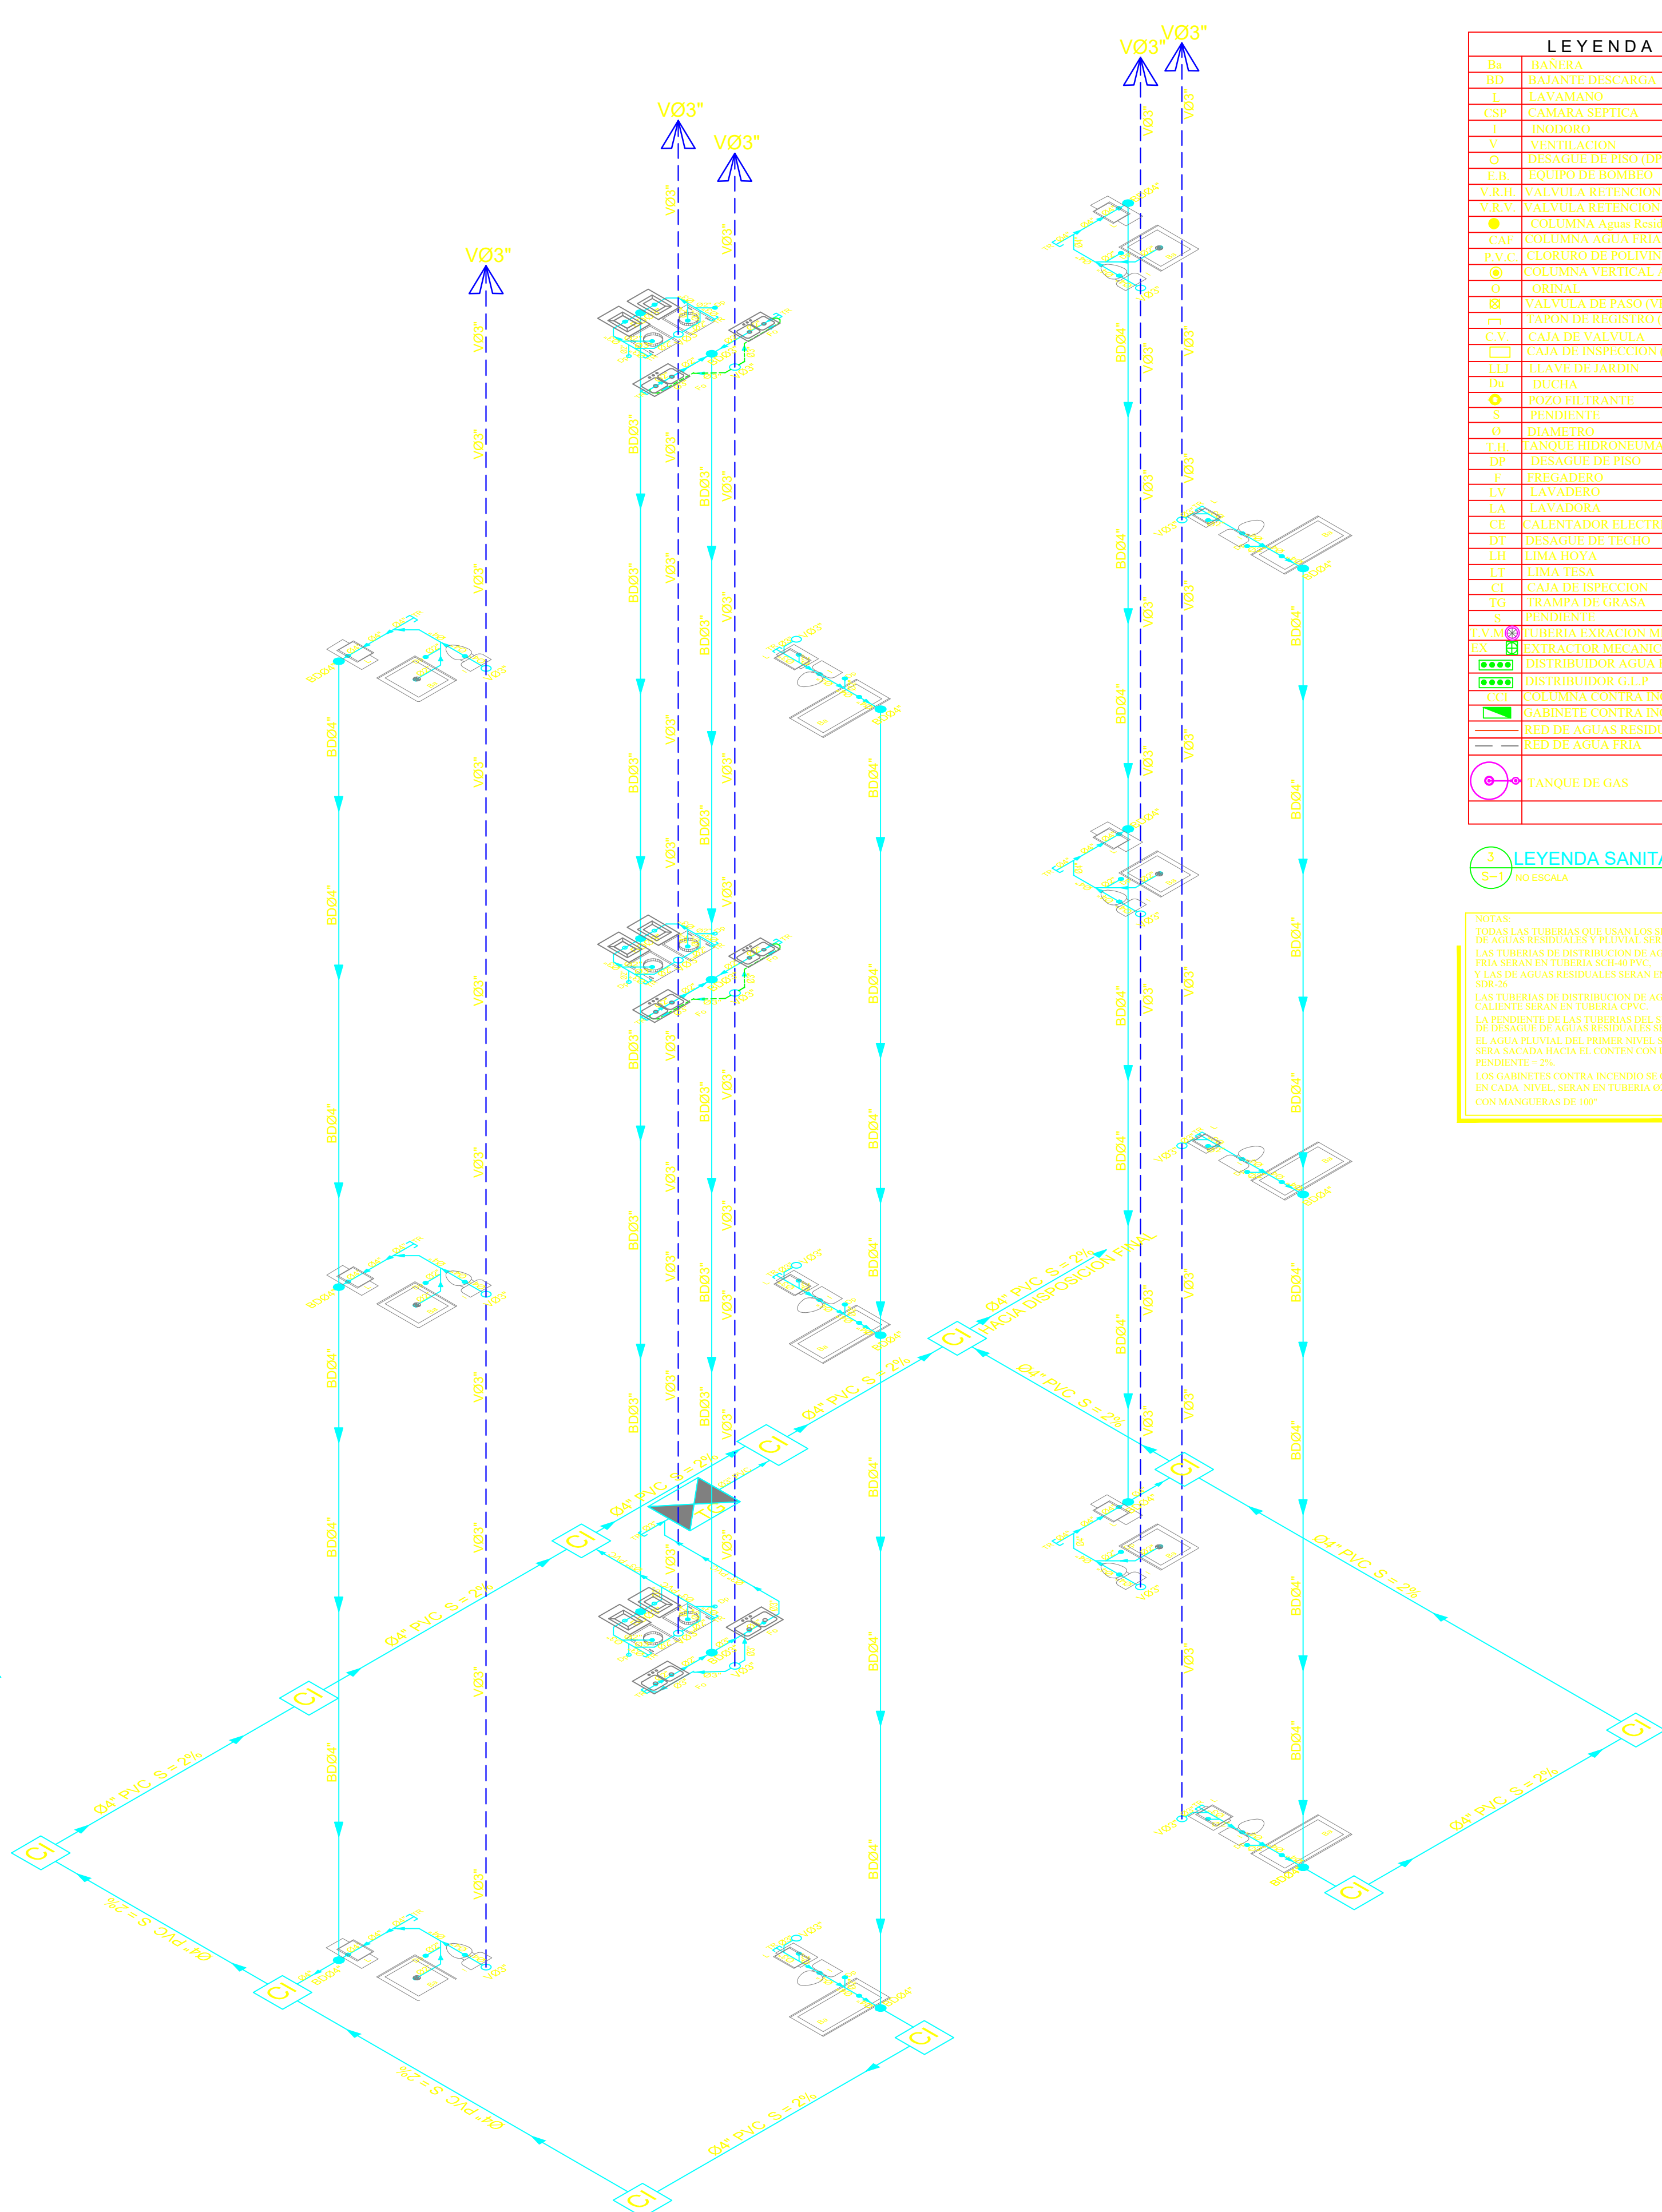

PERSPECTIVA ISOMETRICA AGUAS RESIDUALES BLOQUE A
NO ESCALA

1
S08

LEYENDA	
Ba	BANERA
BD	BAJANTE DESCARGA
T	TAVANADO
CSP	CAMARA SEPTICA
I	INODORO
V	VENTILACION
O	DESAGUE DE PISO (DP)
E.B.	EQUIPO DE BOMBEO
V.R.H.	VALVULA RETENCION HORIZONTAL
V.R.V.	VALVULA RETENCION VERTICAL
●	COLUMNA AGUAS RESIDUALES
CAF	COLUMNA AGUA FRIA (CAF)
P.V.C.	CLORURO DE POLIVINILO
●	COLUMNA VERTICAL AGUA FRIA
O	ORDINAL
S	VALVULA DE PASO (VP)
TP	TAPON DE REGISTRO (TR)
C.V.	CAJA DE VALVULA
CI	CAJA DE INSPECCION (C-I)
LIJ	LEVANT DE JARDIN
DI	DOCHA
●	BOZO FILTRANTE (PF)
S	PENDIENTE
D	DIAMETRO
TH	FANQUE HIDRONEUMATICO
DP	DESAGUE DE PISO
F	FREGADERO
LV	LAVADERO
LA	LAVABOIRA
CE	CALENTADOR ELECTRICO
DT	DESAGUE DE TECHO
DI	DIMA HOYA
LI	LIMA TISA
CI	CAJA DE INSPECCION
TG	TRAMPA DE GRASA
PD	PENDIENTE
EX	EXTRACTOR MECANICO
EX	EXTRACTOR MECANICO
●	DISTRIBUIDOR AGUA FRIA D.A.F.
●	DISTRIBUIDOR G.L.P. D.G.L.P.
●	COLUMNA CONTRA INCENDIO
●	GABINETE CONTRA INCENDIO
●	RED DE AGUAS RESIDUALES
●	RED DE AGUA FRIA
●	FANQUE DE GAS

LEYENDA SANITARIA

NO ESIGALA

NOTAS:

TODAS LAS TUBERIAS QUE USAN LOS SISTEMAS DE AGUAS RESIDUALES Y PIVOTAL SERAN DE P.V.C.

LAS TUBERIAS DE DISTRIBUCION DE AGUA FRIA SERAN EN TUBERIA SCH 40 P.V.C.

Y LAS DE AGUAS RESIDUALES SERAN EN TUBERIA SCH 40

LAS TUBERIAS DE DISTRIBUCION DE AGUA CALIENTE SERAN EN TUBERIA CPVC

LA PENDIENTE DE LAS TUBERIAS DEL SISTEMA DE DESAGUE DE AGUAS RESIDUALES SERAN A 2%

EL AGUA PLUVIAL DEL PRIMER NIVEL SERA SACADA HACIA EL CONTEN CON UNA PENDIENTE A 2%

LOS GABINETES CONTRA INCENDIO SE COLOCARAN EN CADA NIVEL SERAN EN TUBERIA 80\"/>

CON MANGUERAS DE 100"



diazmelo & asocs.
ARQUITECTOS
Presidente Billini # 12, Bani, R.D. 522-4989
E-mail: diazmelo@hotmail.com

COLABORACION:



ARQUITECTURA DIGITAL
DISEÑOS-CONSTRUCCION-DIGITACION
COMPROMETIDOS CON SU TIEMPO
C/JUAN SANCHEZ RAMIREZ #56,
LOCAL 5 ZONA UASD TEL:221-5400

PROPIETARIO:
GRUPO EMPRESARIAL
BANILEJO S.R.L.
GEBSA

PROYECTISTAS:

DISEÑO ARQUITECTONICO:
DIAZMELO & ASOCS.
Arq. ISMAEL DIAZ MELO
Codia: 9604

DISEÑO SANITARIO:
Arq. HAMLET TEJEDA
Codia: 18303

DISEÑO ESTRUCTURAL:
ING. ODELIN TEJEDA
Codia: 23937

DISEÑO ELECTRICO:
ING. VILLYS SANCHEZ
Codia: 19060

CONTENIDO:
ISOMETRICAS SANITARIAS

PROYECTO:
RESIDENCIAL GEBSA IV

Fecha: MARZO/2020

UBICACION:

BANI, PROV. PERAVIA


Ref.: Acad 2000

Escala: INDICADA

Hoja No.


9

NOTAS:
TODAS LAS TERMINACIONES Y/O CAMBIOS EN EL SET DE DOCUMENTOS
CONSTRUCTIVOS DEBERAN SER APROBADOS POR EL SUPERVISOR
PREVIAMENTE A SU APLICACION EN LA OBRA
TODAS LAS MEDIDAS DE HUECOS Y DE SUPERFICIE A SER REVESTIDAS
SERAN RECTIFICADAS PREVIA FABRICACION DE LOS CERRRES O LA
O LA INSTALACION DE LOS RECURBIMIENTOS
LAS TERMINACIONES Y/O DETALLES NO ESPECIFICADOS SERAN
DEFINIDOS ENTRE
EL DUEÑO Y EL AUTOR DEL PROYECTO
EL CONTRATISTA NO PODRA TOMAR DECISIONES
INCONSULTAS RESPECTO VARIACIONES EN EL CONTENIDO
DE ESTE DOCUMENTO
LOS PLANOS ARQUITECTONICOS MANDARAN RESPECTO A LOS DEMAS A
ANTE CUALQUIER
DIFERENCIA, PRIMARA LA INFORMACIONCONTENIDA EN LOS MISMOS

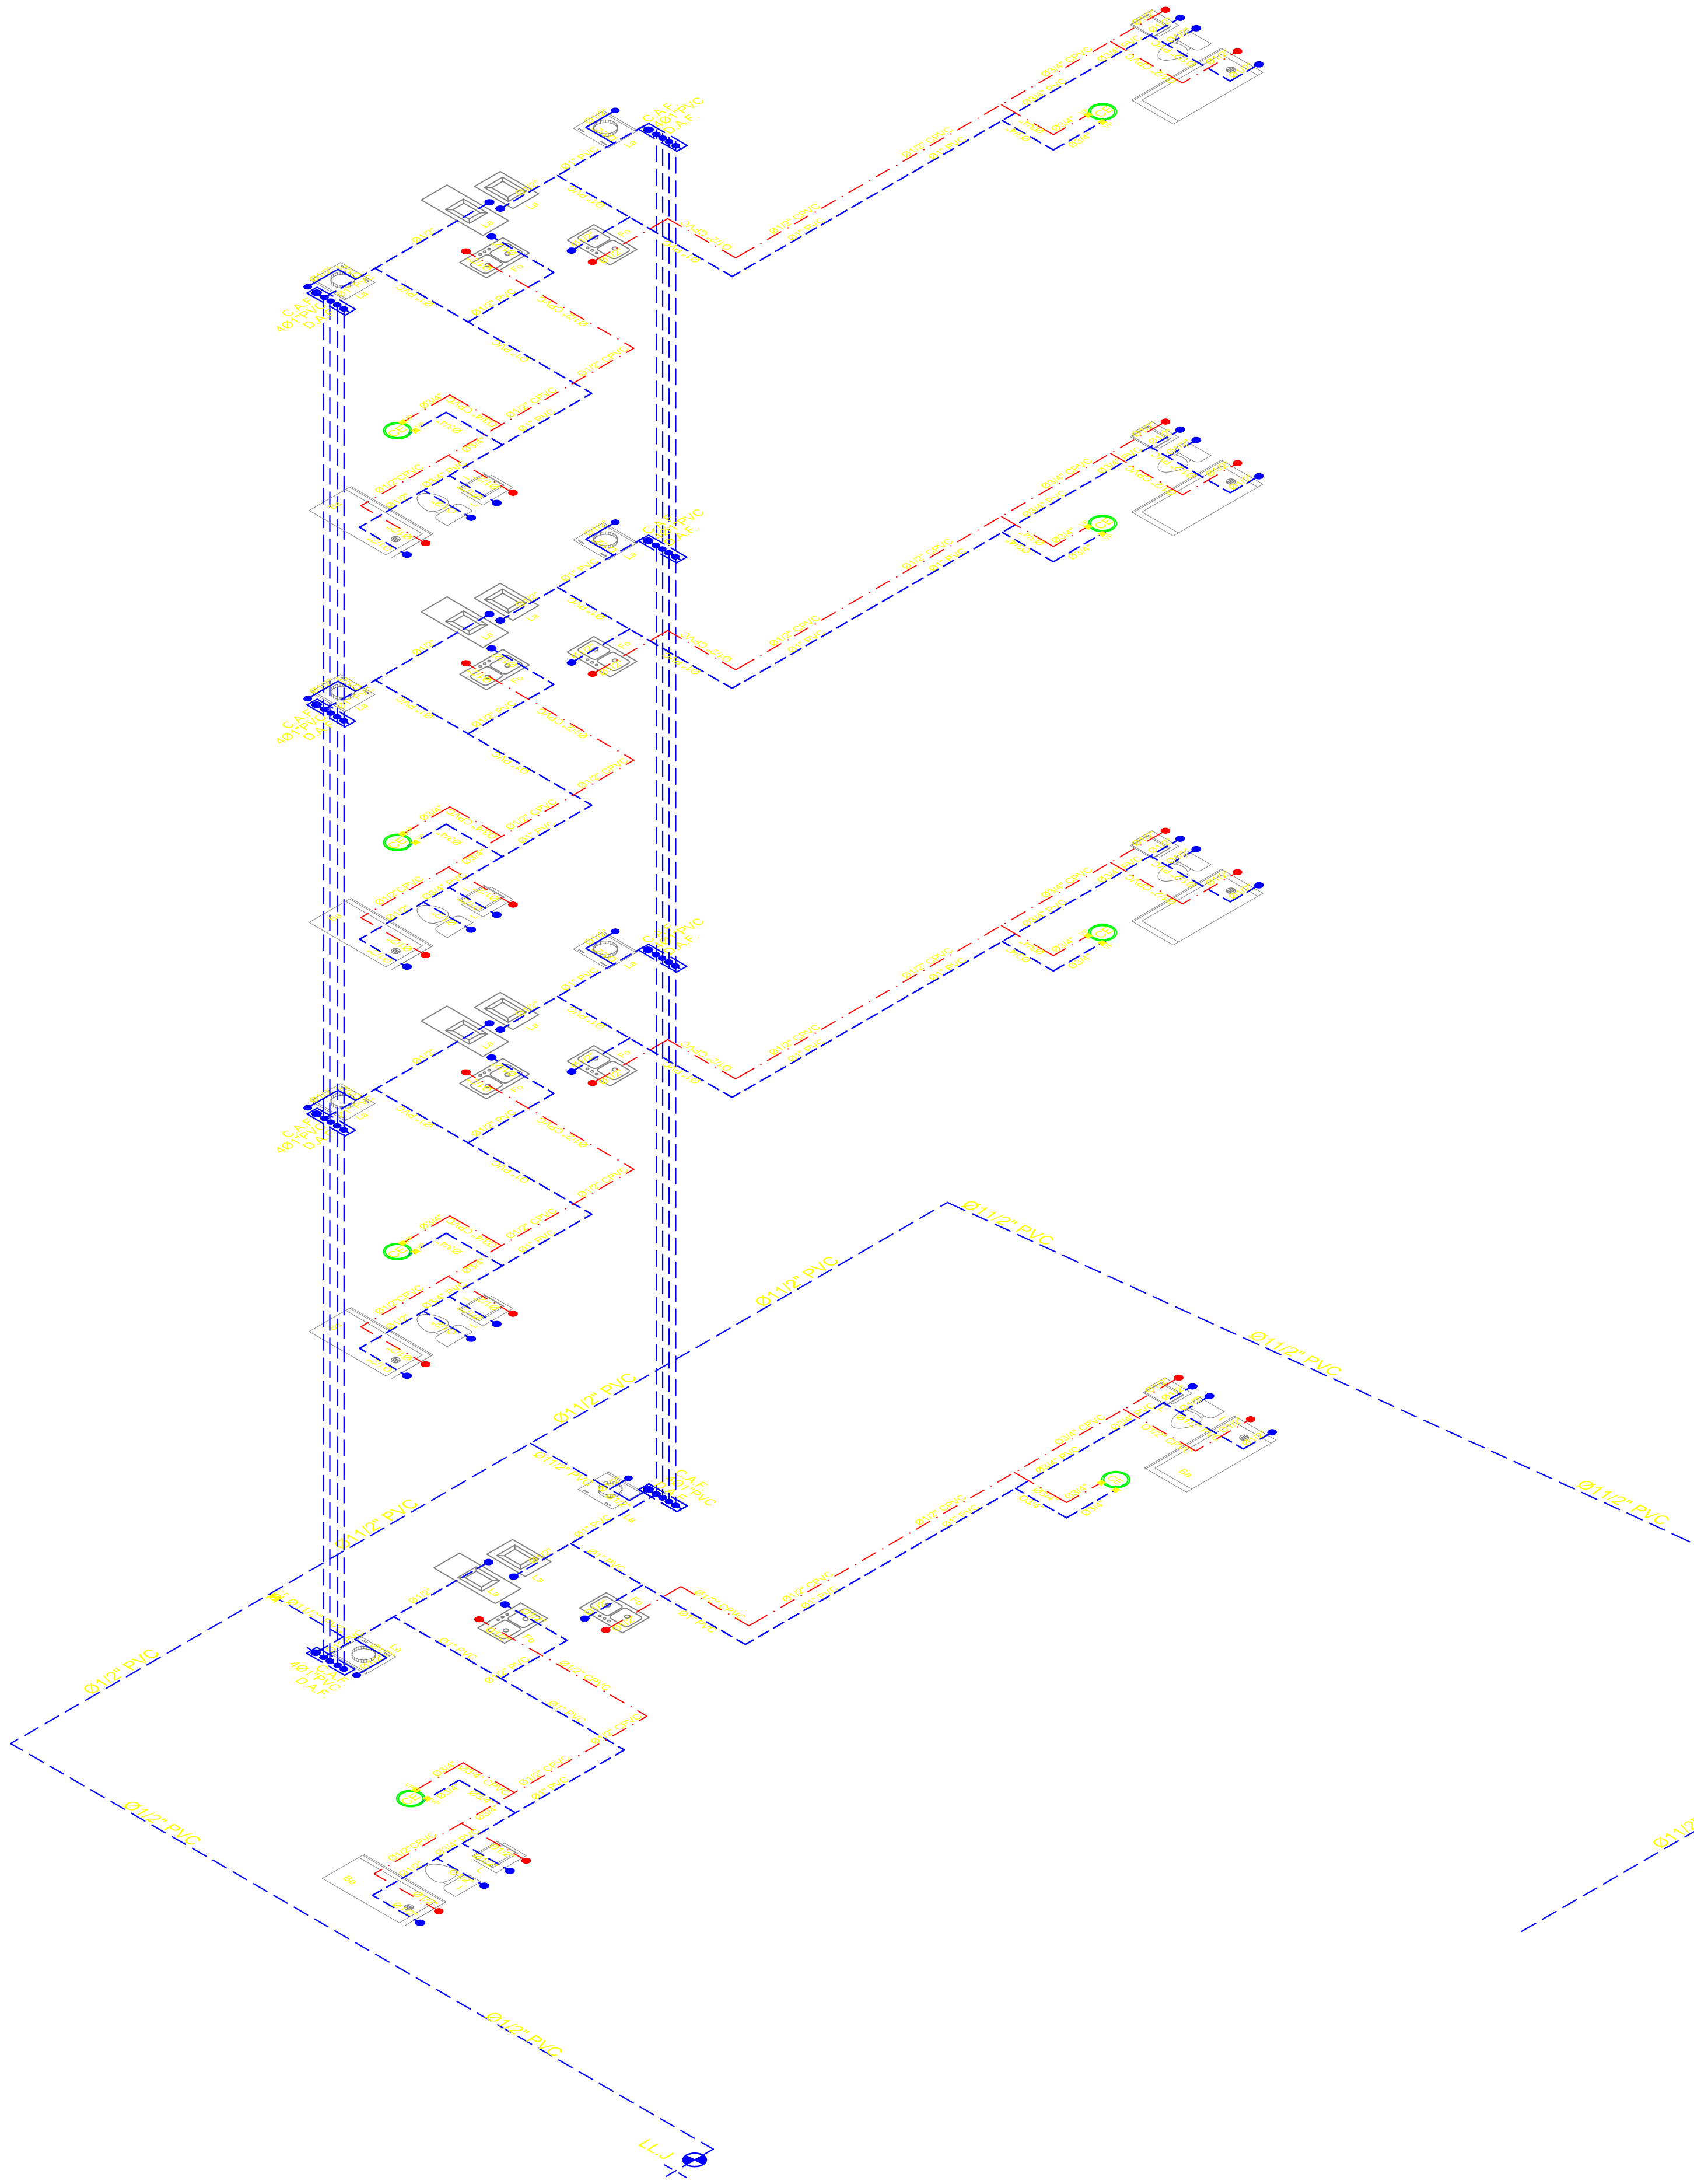

PERSPECTIVA ISOMETRICA AGUA FRIA Y CALIENTE BLOQUE B
NO ESCALA

1
S09

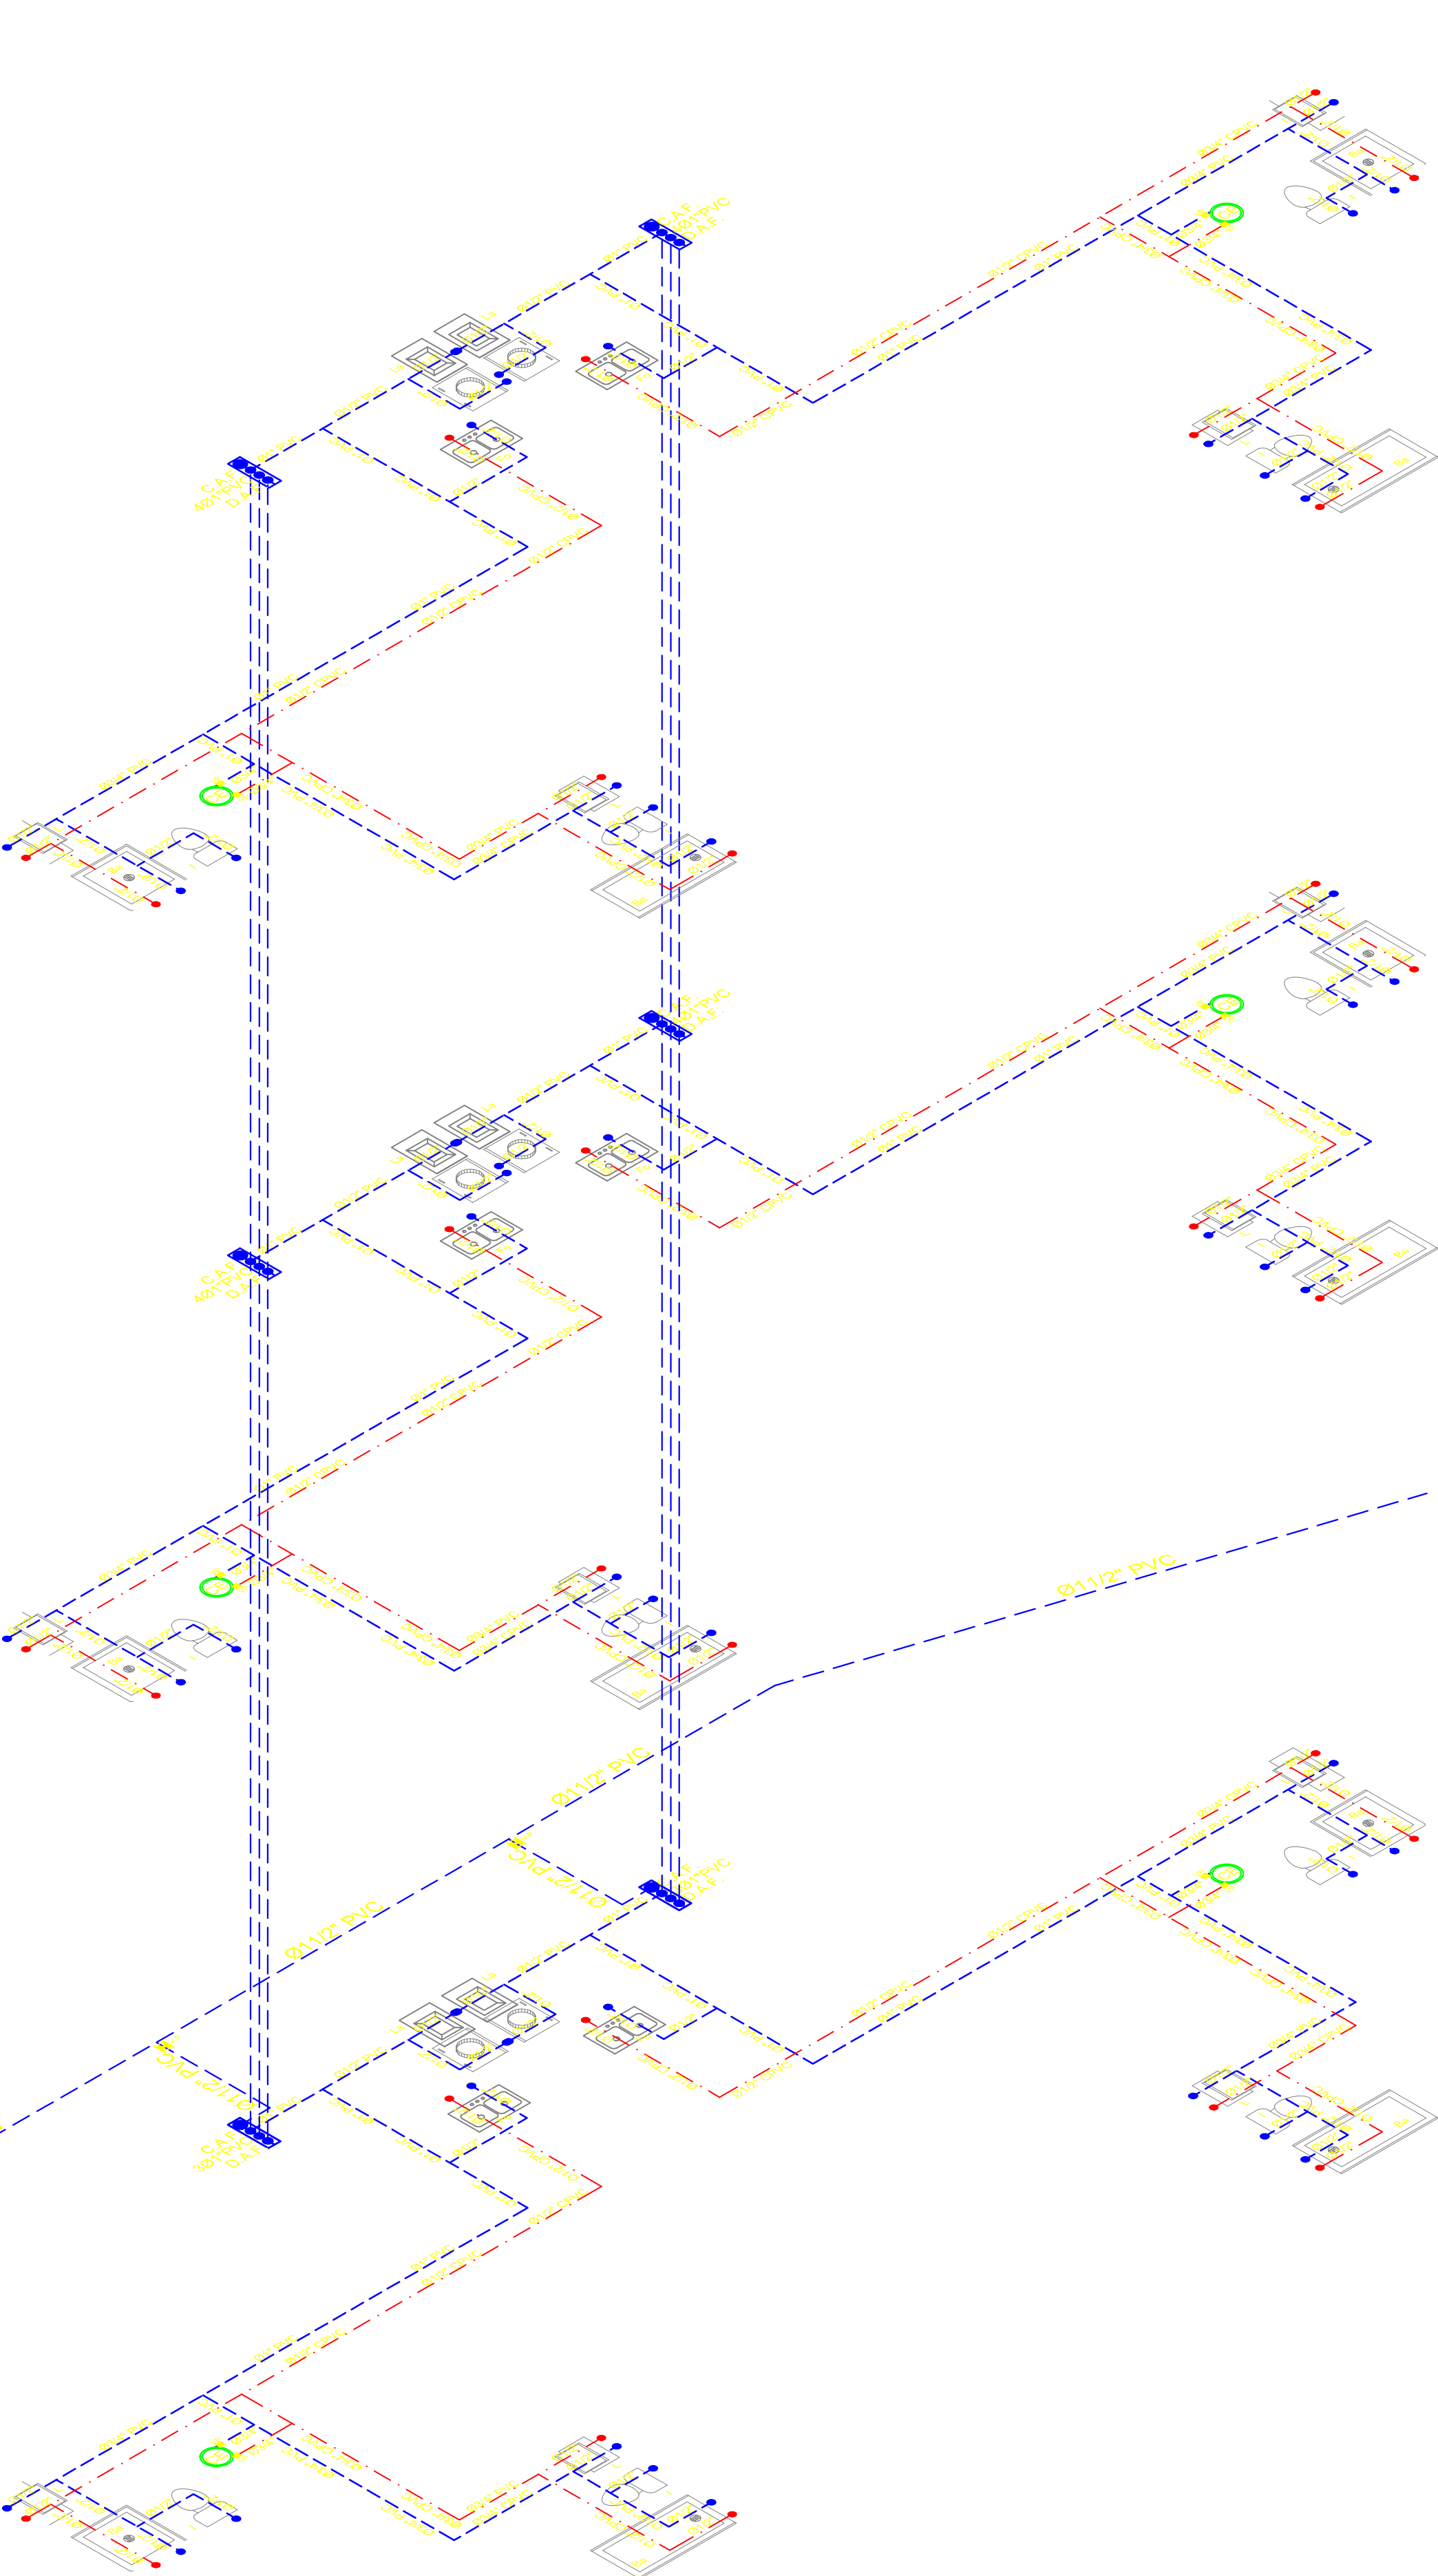

PERSPECTIVA ISOMETRICA AGUA FRIA Y CALIENTE BLOQUE A
NO ESCALA

1
S09

LEYENDA	
Ba	BANERA
BD	BAJANTE DISCARGA
T	TAVAMANGO
CSP	CAMARA SEPTICA
I	INODORO
V	VENTILACION
O	DESAGUE DE PISO (DP)
E.B.	EQUIPO DE BOMBEO
V.R.H.	VALVULA RETENCION HORIZONTAL
V.R.V.	VALVULA RETENCION VERTICAL
●	COLUMNA Agua Residual
CAF	COLUMNA AGUA FRIA (CAF)
P.V.C.	CLORURO DE POLIVINILO
●	COLUMNA VERTICAL AGUA FRIA
O	ORINAL
●	VALVULA DE PASO (VP)
●	TAPON DE REGISTRO (TR)
C.V.	CAJA DE VALVULA
■	CAJA DE INSPECCION (C.I.)
D.J.	LLAVE DE JARDIN
Dn	TRUCHA
●	POZO FILTRANTE (PF)
S	PENDIENTE
Ø	DIAMETRO
T.H.	TANQUE HIDRONEUMATICO
DP	DESAGUE DE PISO
F	FREGADERO
L.V.	LAVADERO
LA	LAVADORA
CE	CALENTADOR ELECTRICO
DT	DESAGUE DE TECHO
LH	LIMA HOYA
LI	LIMA TISA
CI	CAJA DE INSPECCION
IG	TRAMPA DE GRASA
S	PENDIENTE
EX	EXTRACTOR MECANICO
EX	EXTRACTOR MECANICO
●	DISTRIBUIDOR AGUA FRIA - D.A.F.
●	DISTRIBUIDOR G.L.P. - D.G.L.P.
●	CAJONERA CONTRA INCENDIO
■	GABINETE CONTRA INCENDIO
■	RED DE AGUAS RESIDUALES
■	RED DE AGUA FRIA
●	TANQUE DE GAS

LEYENDA SANITARIA	
3	NOTES
S-17	NOTES
NOTAS:	
TODAS LAS TUBERIAS QUE USAN LOS SISTEMAS	
DE AGUAS RESIDUALES Y TUBERIAS DE PVC	
LAS TUBERIAS DE DISTRIBUCION DE AGUA	
FRIA SERAN EN TUBERIA DE PVC	
LAS TUBERIAS DE AGUAS RESIDUALES SERAN EN TUBERIA	
DE PVC	
LAS TUBERIAS DE DISTRIBUCION DE AGUA	
CALIENTE SERAN EN TUBERIA DE PVC	
LA PENDIENTE DE LAS TUBERIAS DEL SISTEMA	
DE DESAGUE DE AGUAS RESIDUALES SERAN - A 2%	
EL AGUA PLOVAL DEL PRIMER NIVEL SERA	
SERA SACADA HACIA EL CONTEN CON UNA	
PENDIENTE - 2%	
LOS GABINETES CONTRA INCENDIO SE COLOCARAN	
EN CADA NIVEL SERAN EN TUBERIA DE 1/2"	
CON ANGULES DE 90°	



diaz melo & asocs.
ARQUITECTOS
Presidente Bilini # 12, Bani, R.D. 522-4989
E-mail: diazmelos@hotmail.com

COLABORACION:



ARQUITECTURA DIGITAL
DISEÑOS-CONSTRUCCION-DIGITACION
COMPROMETIDOS CON SU TIEMPO
C/JUAN SANCHEZ RAMIREZ #56,
LOCAL 5 ZONA UASD TEL:221-5400

PROPIETARIO:
GRUPO EMPRESARIAL
BANILEJO S.R.L.
GEBSA

PROYECTISTAS:

DISEÑO ARQUITECTONICO:
DIAZMELO & ASOCS.
Arq. ISMAEL DIAZ MELO
Codia: 9604

DISEÑO SANITARIO:
Arq. HAMLET TEJEDA
Codia: 18303

DISEÑO ESTRUCTURAL:
ING. ODELIN TEJEDA
Codia: 23937

DISEÑO ELECTRICO:
ING. VILLYS SANCHEZ
Codia: 19060

CONTENIDO:
ISOMETRICAS SANITARIAS

PROYECTO:
RESIDENCIAL GEBSA IV







Fecha: MARZO/2020

UBICACION:
BANI, PROV. PERAVIA

Ref.: Acad 2000
Escala: INDICADA

Hoja No.
9



NOTAS:
TODAS LAS TERMINACIONES Y/O CAMBIOS EN EL SET DE DOCUMENTOS
CONSTRUCTIVOS DEBERAN SER APROBADOS POR EL SUPERVISOR
PREVIAMENTE A SU APLICACION EN LA OBRA
TODAS LAS MEDIDAS DE HUECOS Y DE SUPERFICIE A SER REVESTIDAS
SERAN RECTIFICADAS PREVIA FABRICACION DE LOS CERRES O LA
O LA INSTALACION DE LOS RECURBIMIENTOS
LAS TERMINACIONES Y/O DETALLES NO ESPECIFICADOS SERAN
DEFINIDOS ENTRE
EL DUEÑO Y EL AUTOR DEL PROYECTO
EL CONTRATISTA NO PODRA TOMAR DECISIONES
INCONSULTAS RESPECTO VARIACIONES EN EL CONTENIDO
DE ESTE DOCUMENTO
LOS PLANOS ARQUITECTONICOS MANDARAN RESPECTO A LOS DEMAS A
ANTE CUALQUIER
DIFERENCIA, PRIMARA LA INFORMACIONCONTENIDA EN LOS MISMOS

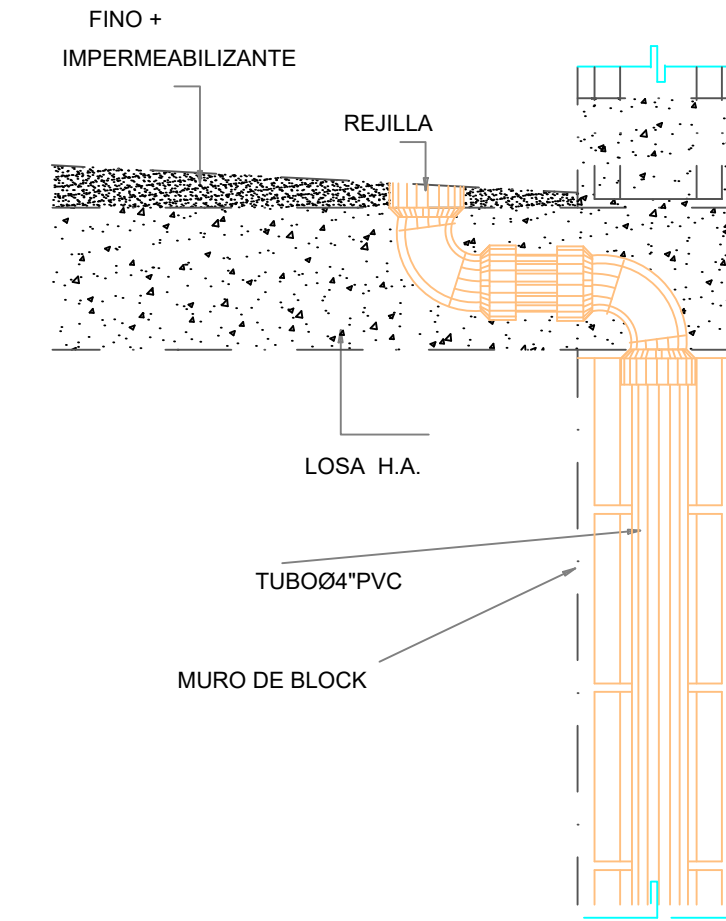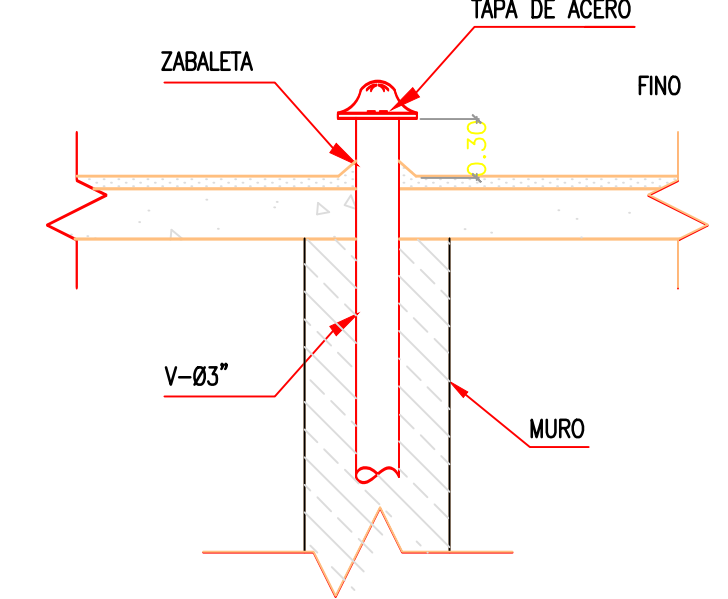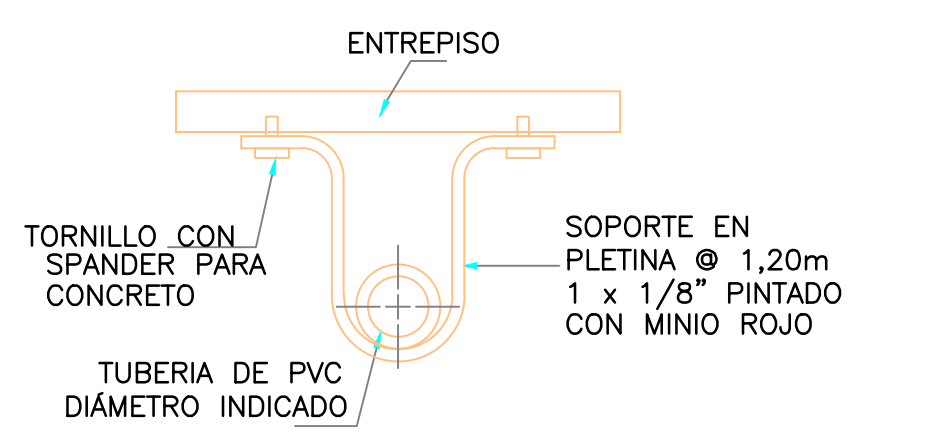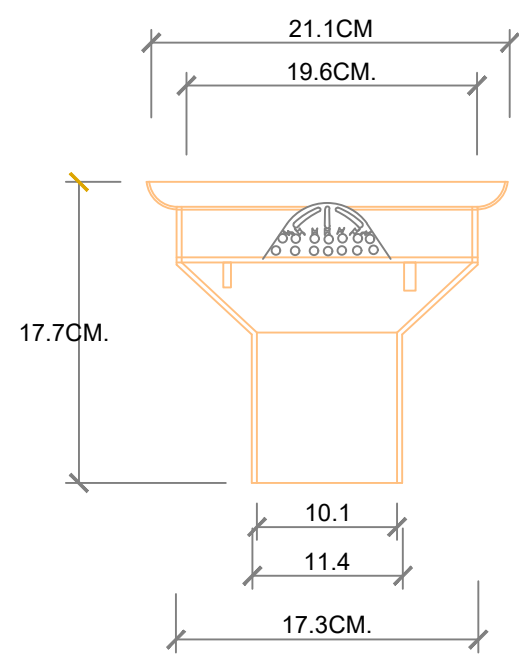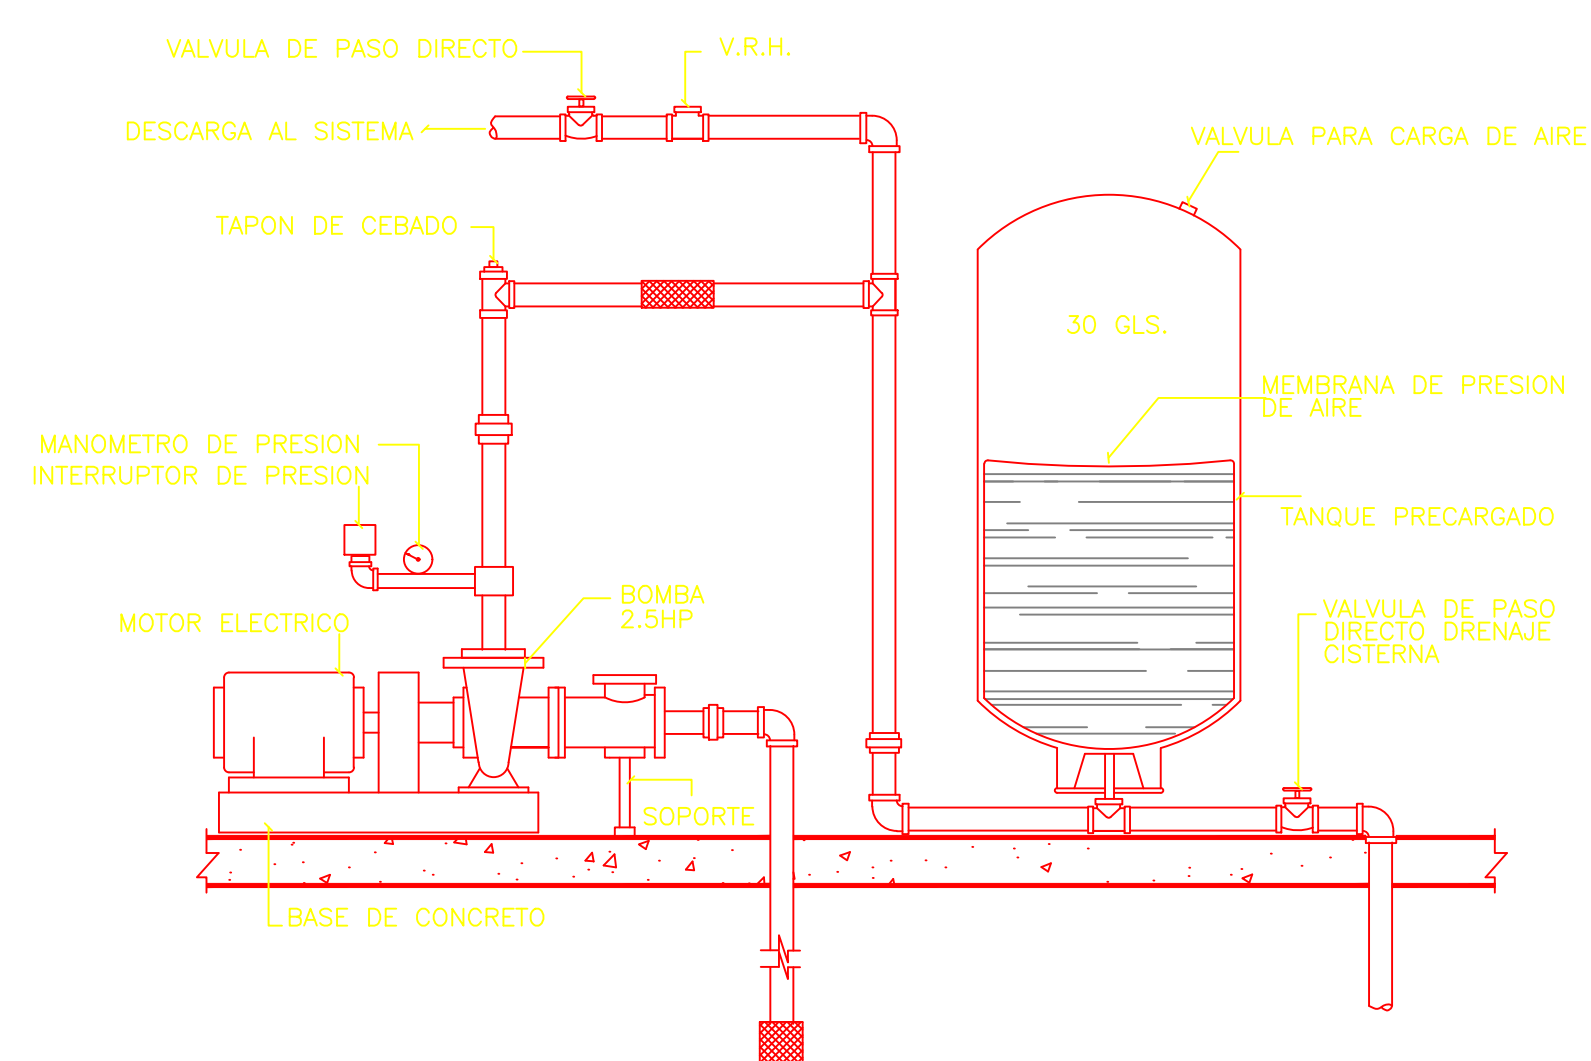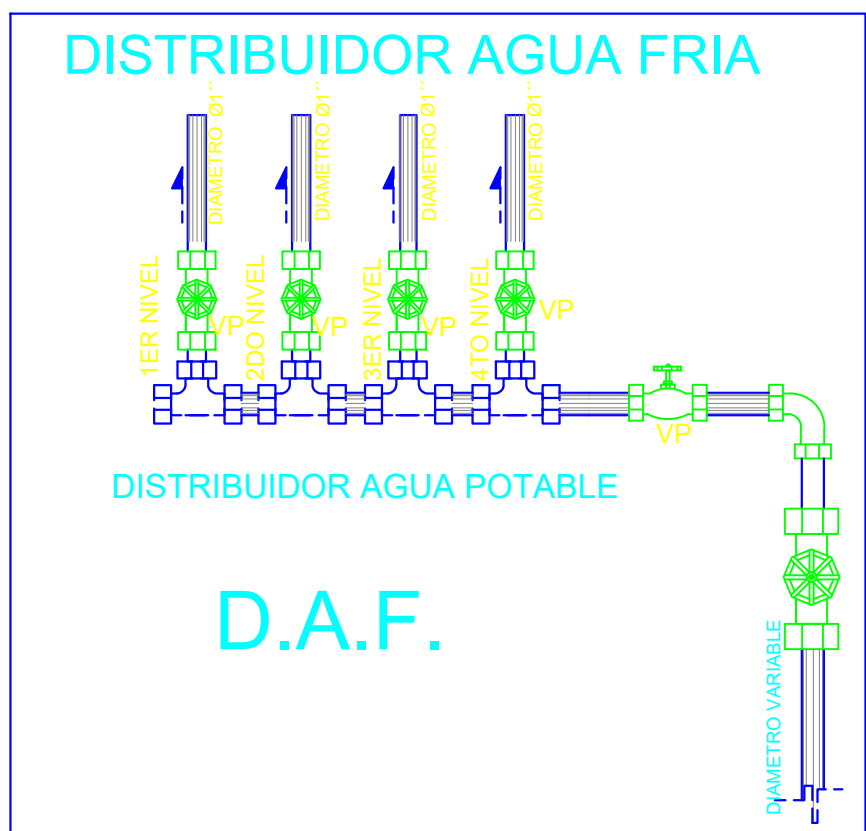

LEYENDA	
Ba	BANERA
BD	BOMBENTE DESCARGA
L	LAVAMANO
CSP	CAMARA SEPTICA
I	INODORO
V	VENTILACION
O	DESAGUE DE PISO (DP)
E.B.	TIPO DE BOMBEO
V.R.I	VALVULA RETENCION HORIZONTAL
V.R.V	VALVULA RETENCION VERTICAL
☉	COLUMNA AGUA FRIA (CAF)
☉	COLUMNA AGUA FRIA (CAF)
P.V.C	CLORURO DE POLIVINIL
☉	COLUMNA VERTICAL AGUA FRIA
O	ORNAL
☉	VALVULA DE PASO (VP)
☉	TAJON DE REGISTRO (TR)
C.V.	CAJA DE VALVULA
☉	CAJA DE INSPECCION (C.I)
LD	LEVI DE JARDIN
Db	DUCHA
☉	POZO FILTRANTE (PF)
S	PENDIENTE
O	DIAMETRO
T.H.	TUBO HIDRONEUMATICO
DP	DESAGUE DE PISO
F	FREGADERO
LV	LAVADERO
LA	LAVABORA
CE	CALENTADOR ELECTRICO
DT	DESAGUE DE TECHO
LH	LIMA HOYA
L	LIMA TESA
CI	CAJA DE INSPECCION
TG	TRAMPA DE GRASA
S	PENDIENTE
—	SEÑAL DE FRACCION MECANICA
EX	EXTRACTOR MECANICO
☉	DISTRIBUIDOR AGUA FRIA D.A.F.
☉	DISTRIBUIDOR G.L.P. D.G.L.P
☉	COLUMNA CON FIA INCENDIO
☉	COLUMNA CON FIA INCENDIO
—	RED DE AGUAS RESIDUALES
—	RED DE AGUA FRIA
☉	TANQUE DE GAS


3 LEYENDA SANITARIA
S-1 NO ESCALA

DETALLE CAJA DE INSPECCION

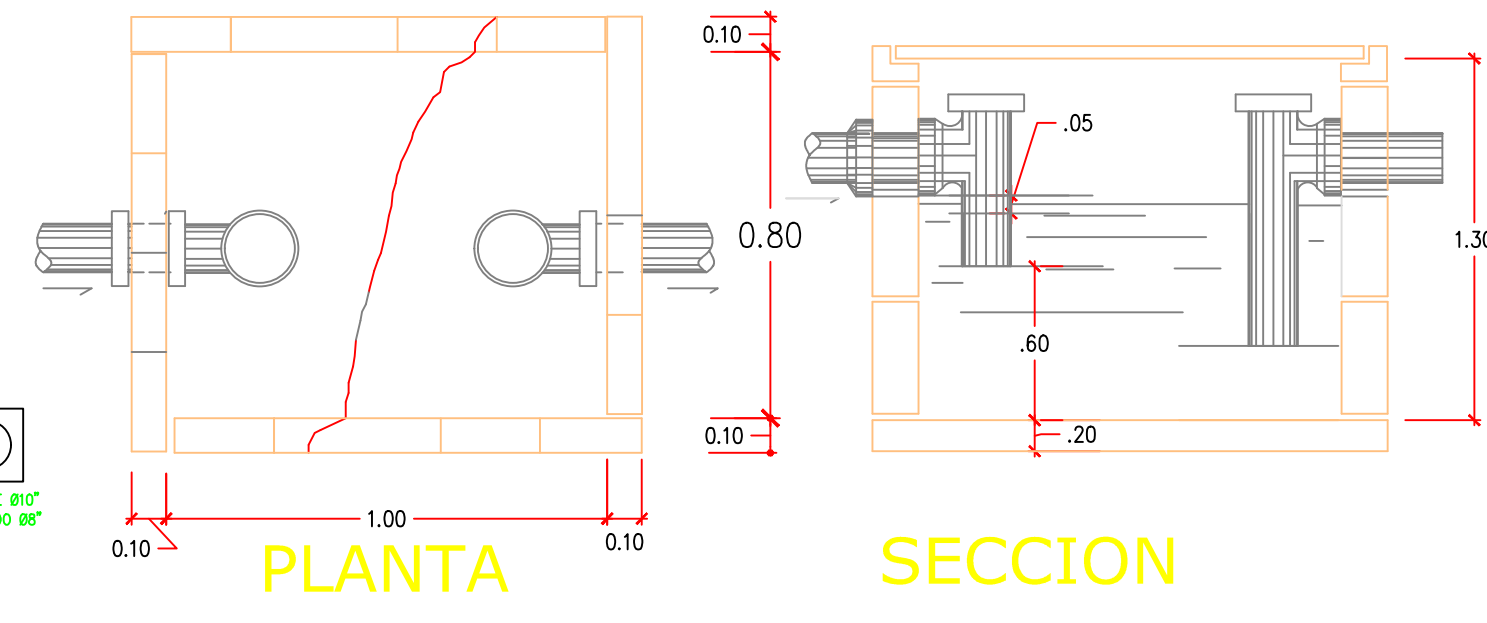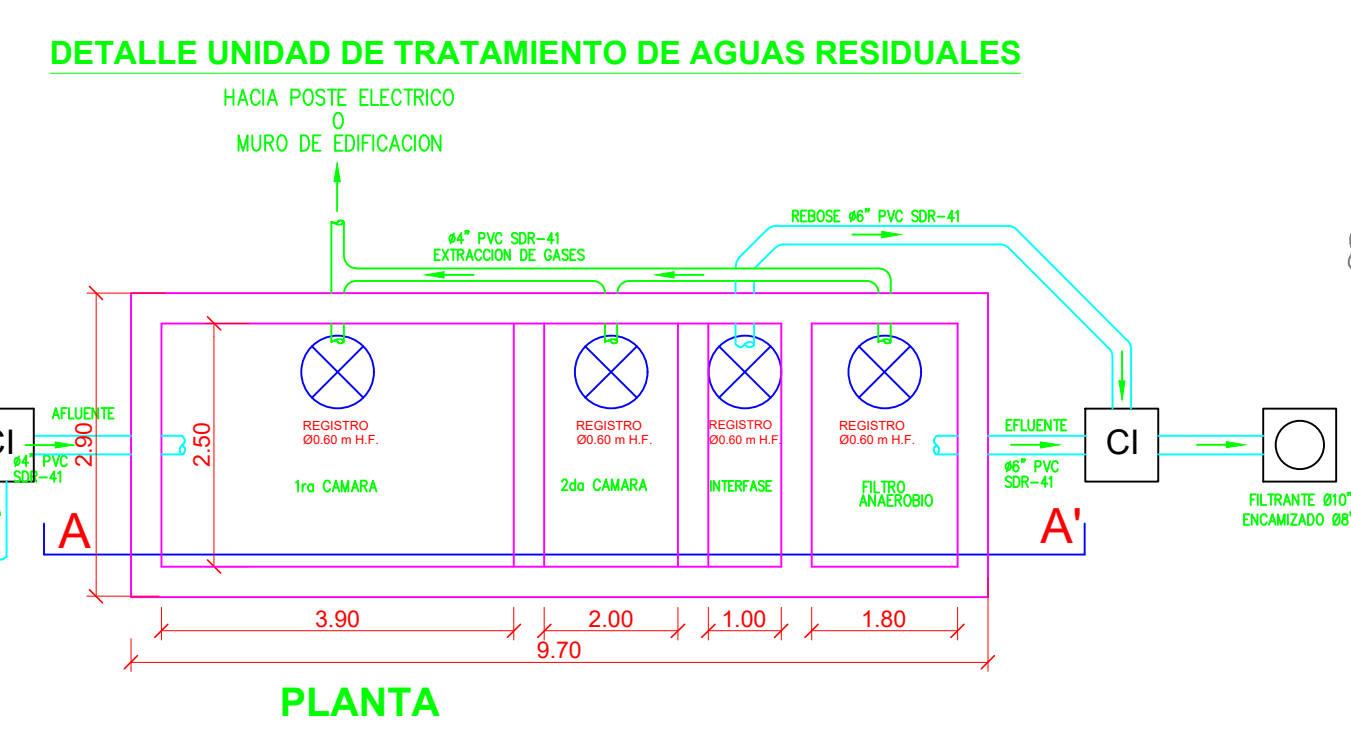

PLANTA SECCION

DETALLE TRAMPA DE GRASA

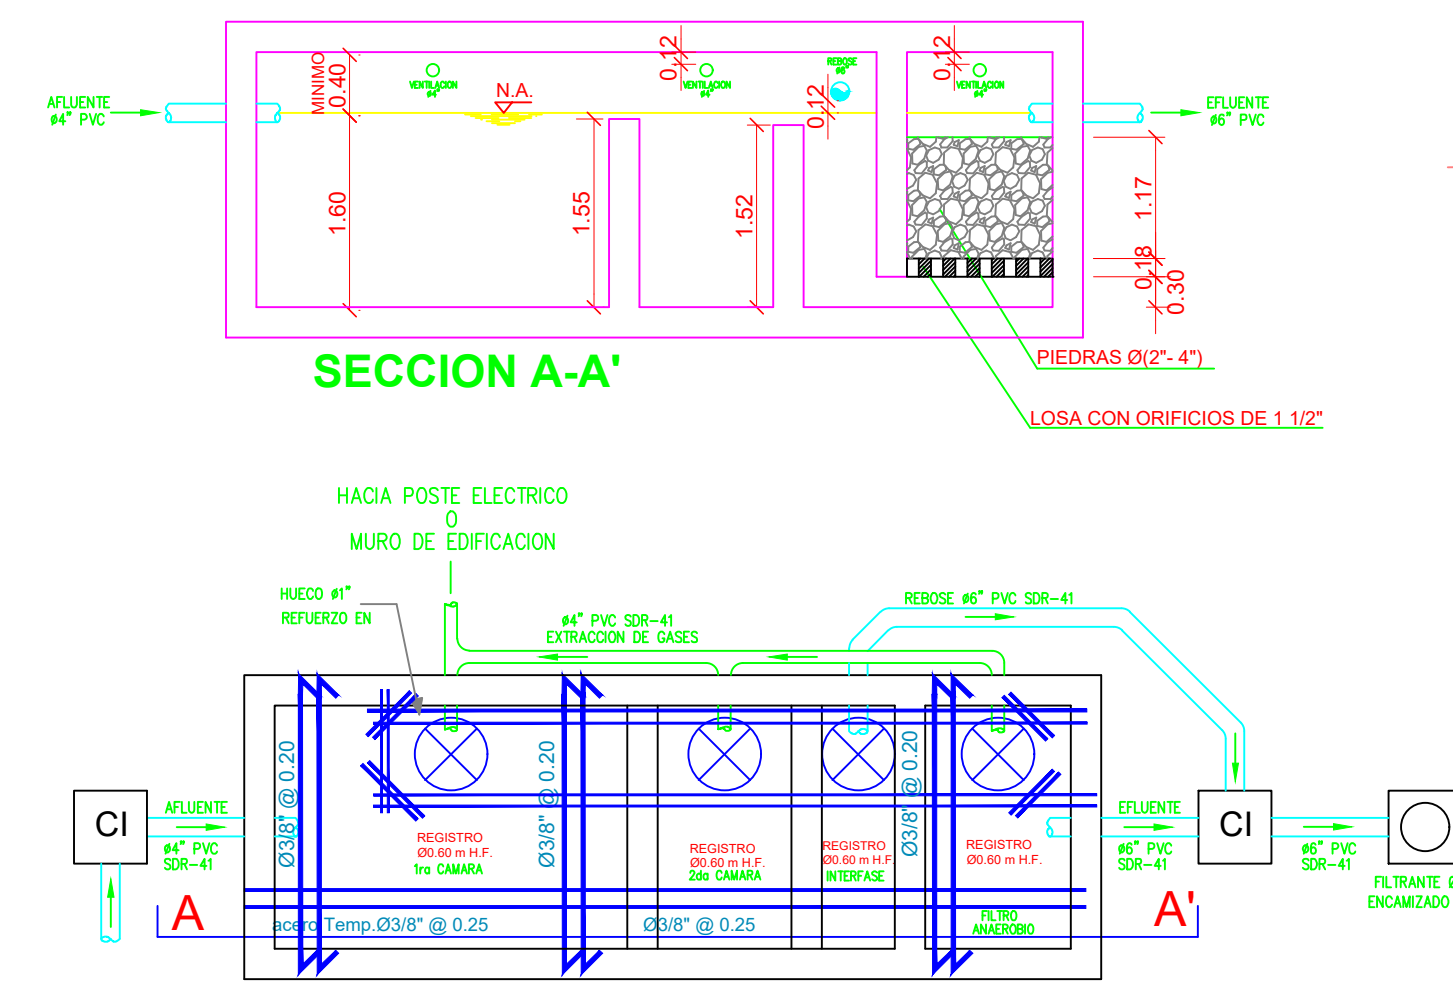

PLANTA ESTRUCTURAL

**DETALLE ZANJA PARA TUBERIA PVC
ALCANTARILLADO SANITARIO Y PLUVIAL**

DIMENSIONES DE ZANJAS				
NOMINAL (")	ANCHO (cm)	PROFUNDIDAD (h=cm)	asiento de arena	volumen (m3/ml)
hasta 2"	0.50	1.05	0.10	0.63
hasta 3"	0.60	1.08	0.10	0.65
hasta 4"	0.60	1.10	0.10	0.66
hasta 6"	0.70	1.15	0.10	0.81
hasta 8"	0.75	1.20	0.10	0.90

Fecha: MARZO/2020	
UBICACION: BANI, PROV. PERAVIA	
Ref.: Acad 2000	Hoja No.
Escala: INDICADA	10

NOTAS:


TODAS LAS TERMINACIONES Y/O CAMBIOS EN EL SET. DE DOCUMENTOS CONSTRUCTIVOS DEBERAN SER APROBADOS POR EL SUPERVISOR PREVIA SU APLICACION EN LA OBRA.

TODAS LAS MEDIDAS DE HUECOS Y DE SUPERFICIE A SER REVESTIDAS SERAN RECTIFICADAS PREVIA FIRMACION DE LOS CIERRES O LA O LA INSTALACION DE LOS RECUBRIMIENTOS

LAS TERMINACIONES Y/O DETALLES NO ESPECIFICADOS SERAN DEFINIDOS ENTRE EL DUEÑO Y EL AUTOR DEL PROYECTO.


EL CONTRATISTA NO PODRA TOMAR DECISIONES INCONSISTENTES RESPECTO A LA FORMA EN EL CONTENIDO DE ESTE DOCUMENTO

LOS PLANOS ARQUITECTONICOS MANDARAN RESPECTO A LOS DEMAS A NIVEL DE CUALQUIER DIFERENCIA, PRIMARA LA INFORMACION CONTENIDA EN LOS MISMO

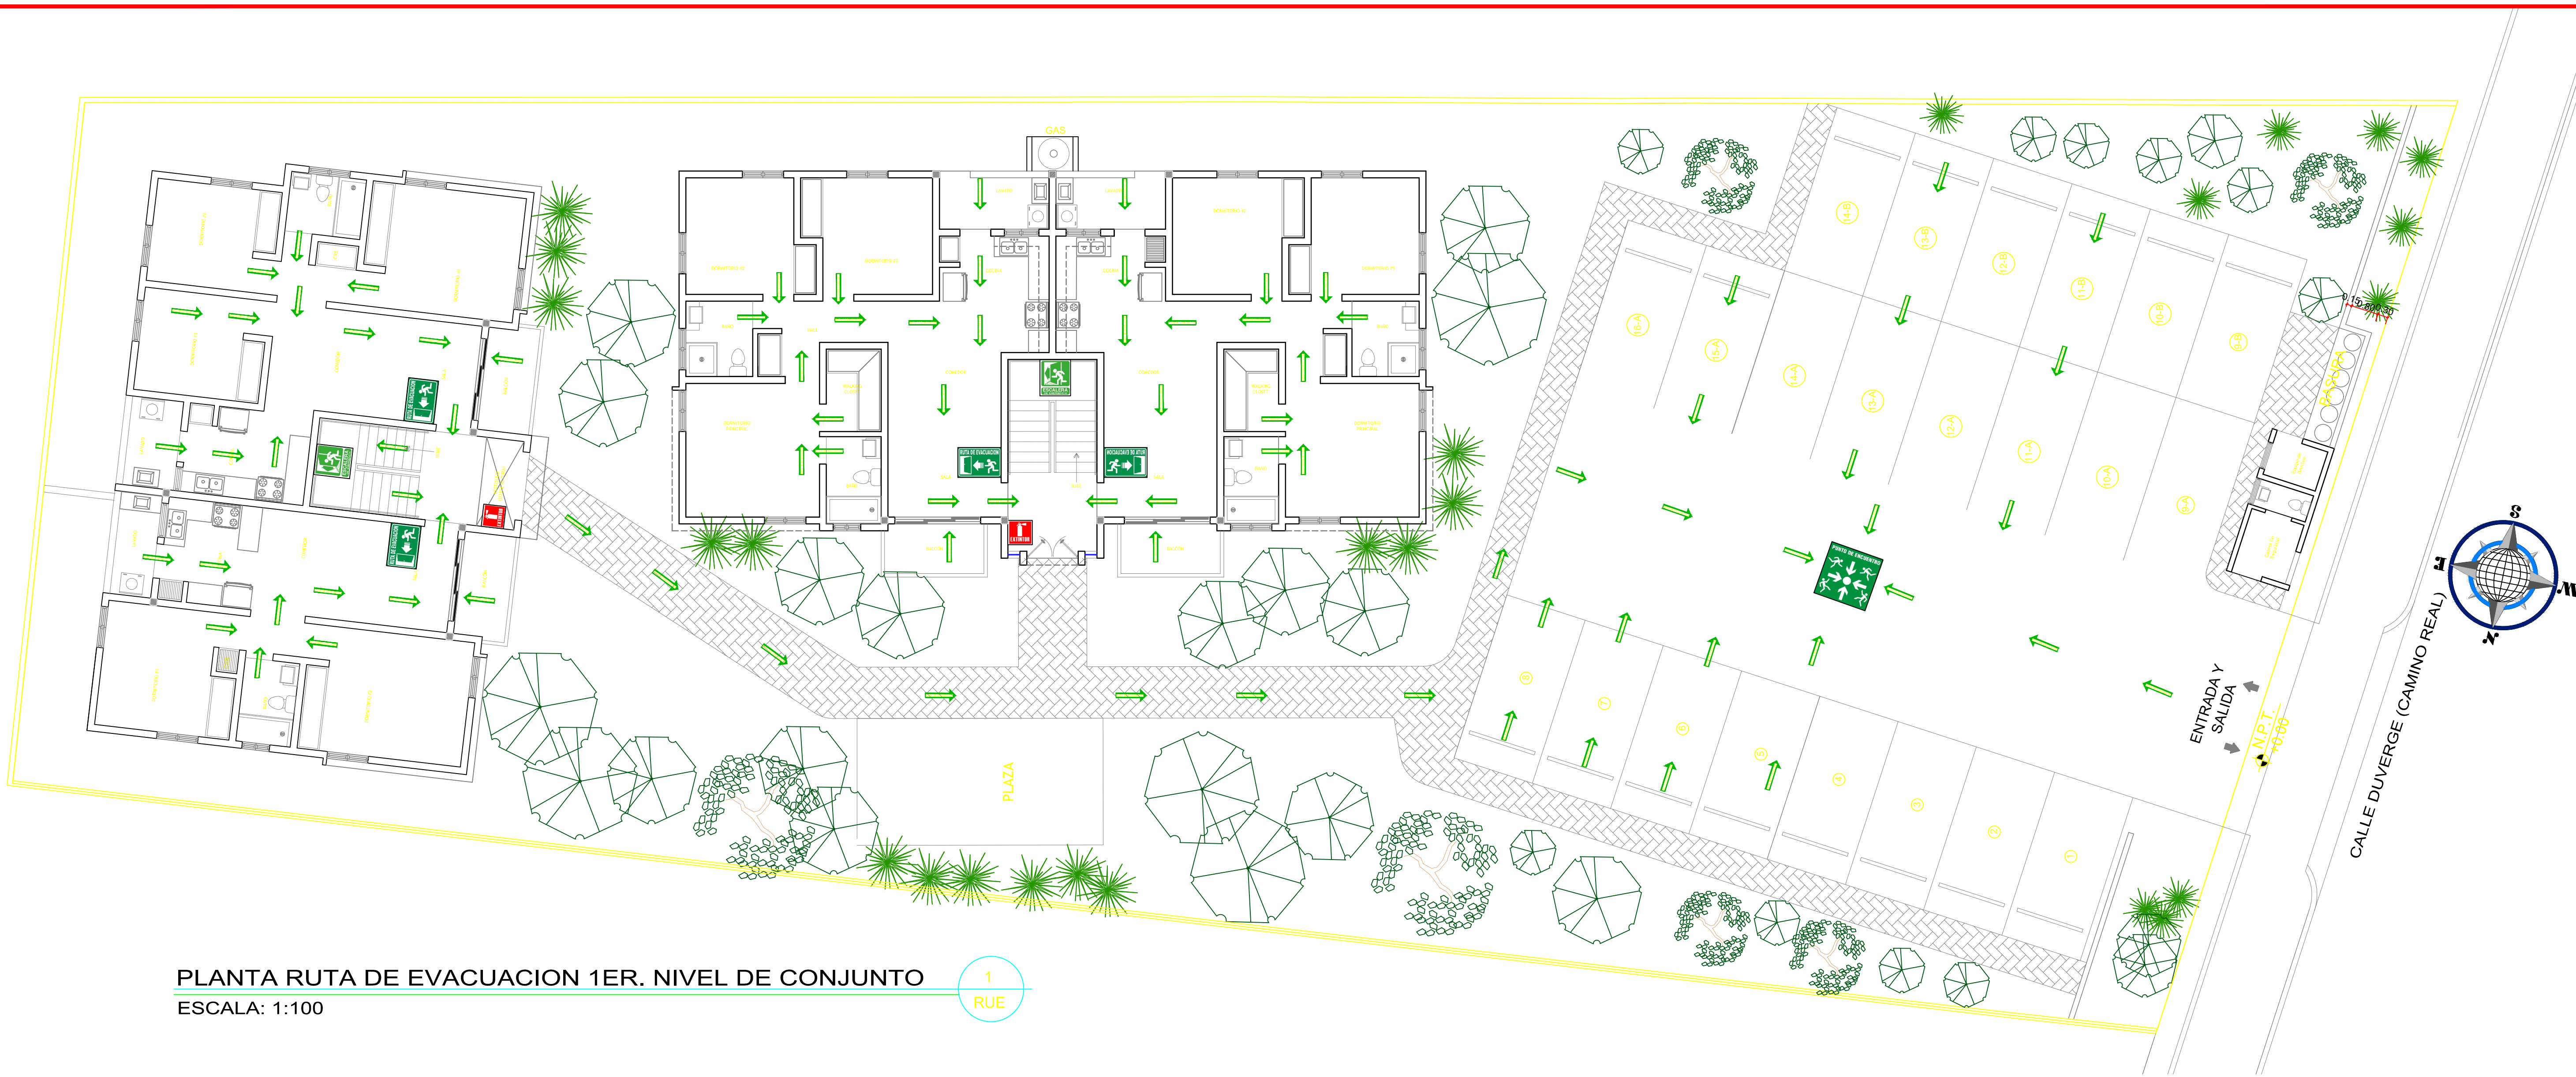


PLANTA RUTA DE EVACUACION 1ER. NIVEL DE CONJUNTO
ESCALA: 1:100

1
RUE

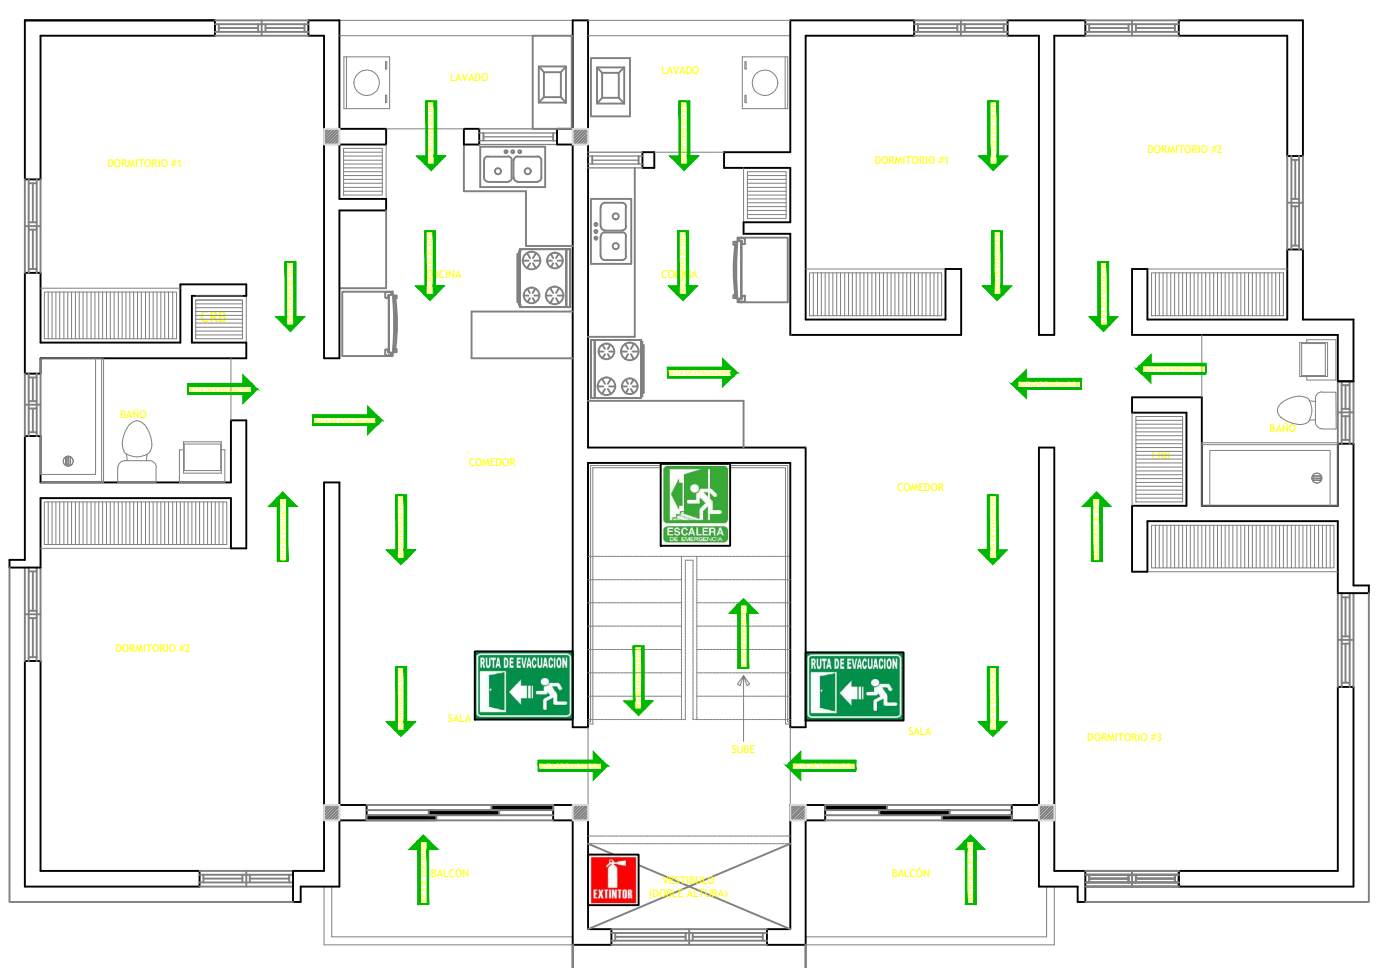

PLANTA RUTA EVACUACION 2DO.AL 4TO NIVEL NIVEL, BLOQUE A
ESCALA: 1:75

2
RUE

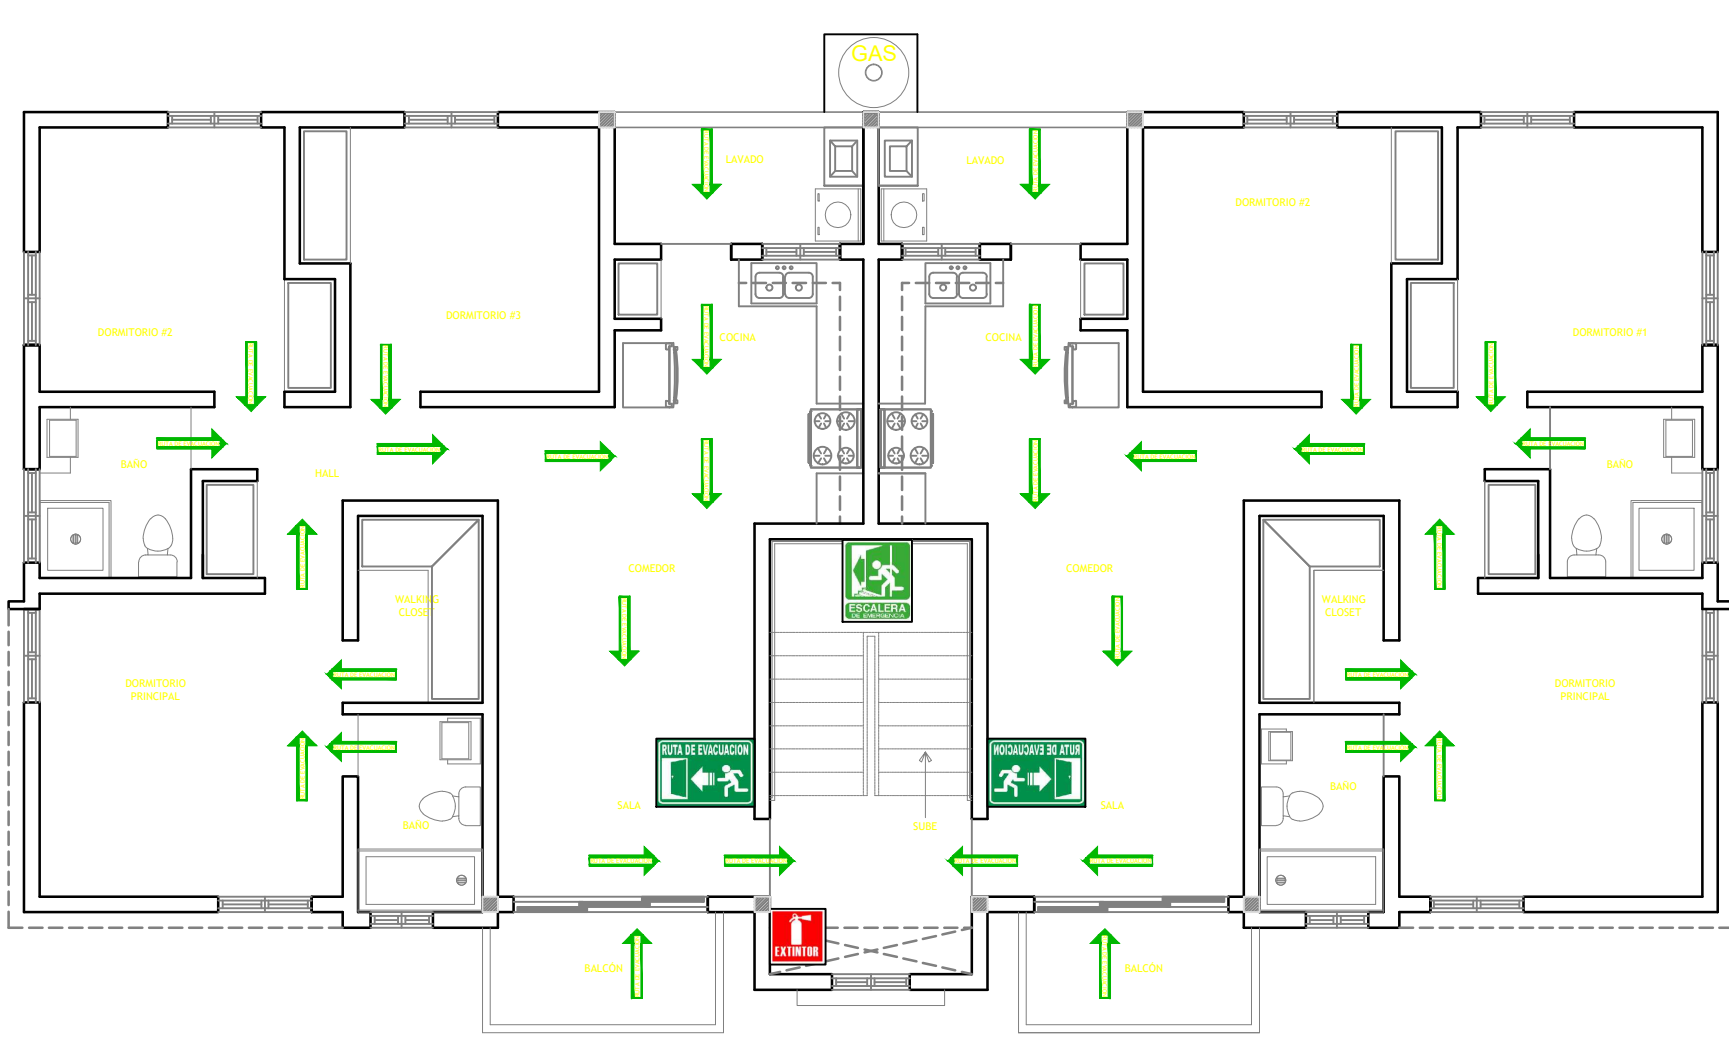

PLANTA RUTA EVACUACION 2DO. AL 3ER NIVEL, BLOQUE B
ESCALA: 1:75

3
RUE

LEYENDA Y SIMBOLOGIA DE RUTA DE EVACUACION:

	PUNTO DE ENCUENTRO
	ESCALERA DE EMERGENCIA
	EXTINTOR CONTRA INCENDIO
	RUTA DE EVACUACION
	ZONA DE SEGURA EN CASO DE SISMO
	RUTA DE EVACUACION

diaz melo & asocs.
ARQUITECTOS
Presidente Biliini # 12, Bani, R.D. 522-4989
E-mail: diazmelo@hotmail.com

COLABORACION:

ARQUITECTURA DIGITAL
DISEÑOS-CONSTRUCCION-DIGITACION
COMPROMETIDOS CON SU TIEMPO
C/JUAN SANCHEZ RAMIREZ #56,
LOCAL 5 ZONA UASD TEL:221-5400

PROPIETARIO:
GRUPO EMPRESARIAL
BANILEJO S.R.L.
GEBSA

PROYECTISTAS:

DISEÑO ARQUITECTONICO:
DIAZMELO & ASOCS.
Arq. ISMAEL DIAZ MELO
Codia: 9604

DISEÑO SANITARIO:
Arq. HAMLET TEJEDA
Codia: 18303

DISEÑO ESTRUCTURAL:
ING. ODELIN TEJEDA
Codia: 23937

DISEÑO ELECTRICO:
ING. VILLYS SANCHEZ
Codia: 19060

CONTENIDO:
PLANTAS RUTA DE EVACUACION



PROYECTO:
RESIDENCIAL GEBSA IV

Fecha: MARZO/2020

UBICACION:
SOMBRERO, BANI, PROV. PERAVIA


Ref.: Acad 2000	Hoja No.
Escala: INDICADA	11

NOTAS:
TODAS LAS TERMINACIONES Y/O CAMBIOS EN EL SET DE DOCUMENTOS CONSTRUCTIVOS DEBERAN SER APROBADOS POR EL SUPERVISOR PREVIAMENTE A SU APLICACION EN LA OBRA.
TODAS LAS MEDIDAS DE HUECOS Y DE SUPERFICIE A SER REVESTIDAS SERAN RECTIFICADAS PREVIA FABRICACION DE LOS CERRRES O LA O LA INSTALACION DE LOS RECURBIMIENTOS
LAS TERMINACIONES Y / O DETALLES NO ESPECIFICADOS SERAN DEFINIDOS ENTRE EL DUEÑO Y EL AUTOR DEL PROYECTO.
EL CONTRATISTA NO PODRA TOMAR DECISIONES INCONSULTAS RESPECTO VARIACIONES EN EL CONTENIDO DE ESTE DOCUMENTO
LOS PLANOS ARQUITECTONICOS MANDARAN RESPECTO A LOS DEMAS A ANTE CUALQUIER DIFERENCIA, PRIMARA LA INFORMACIONCONTENIDA EN LOS MISMOS

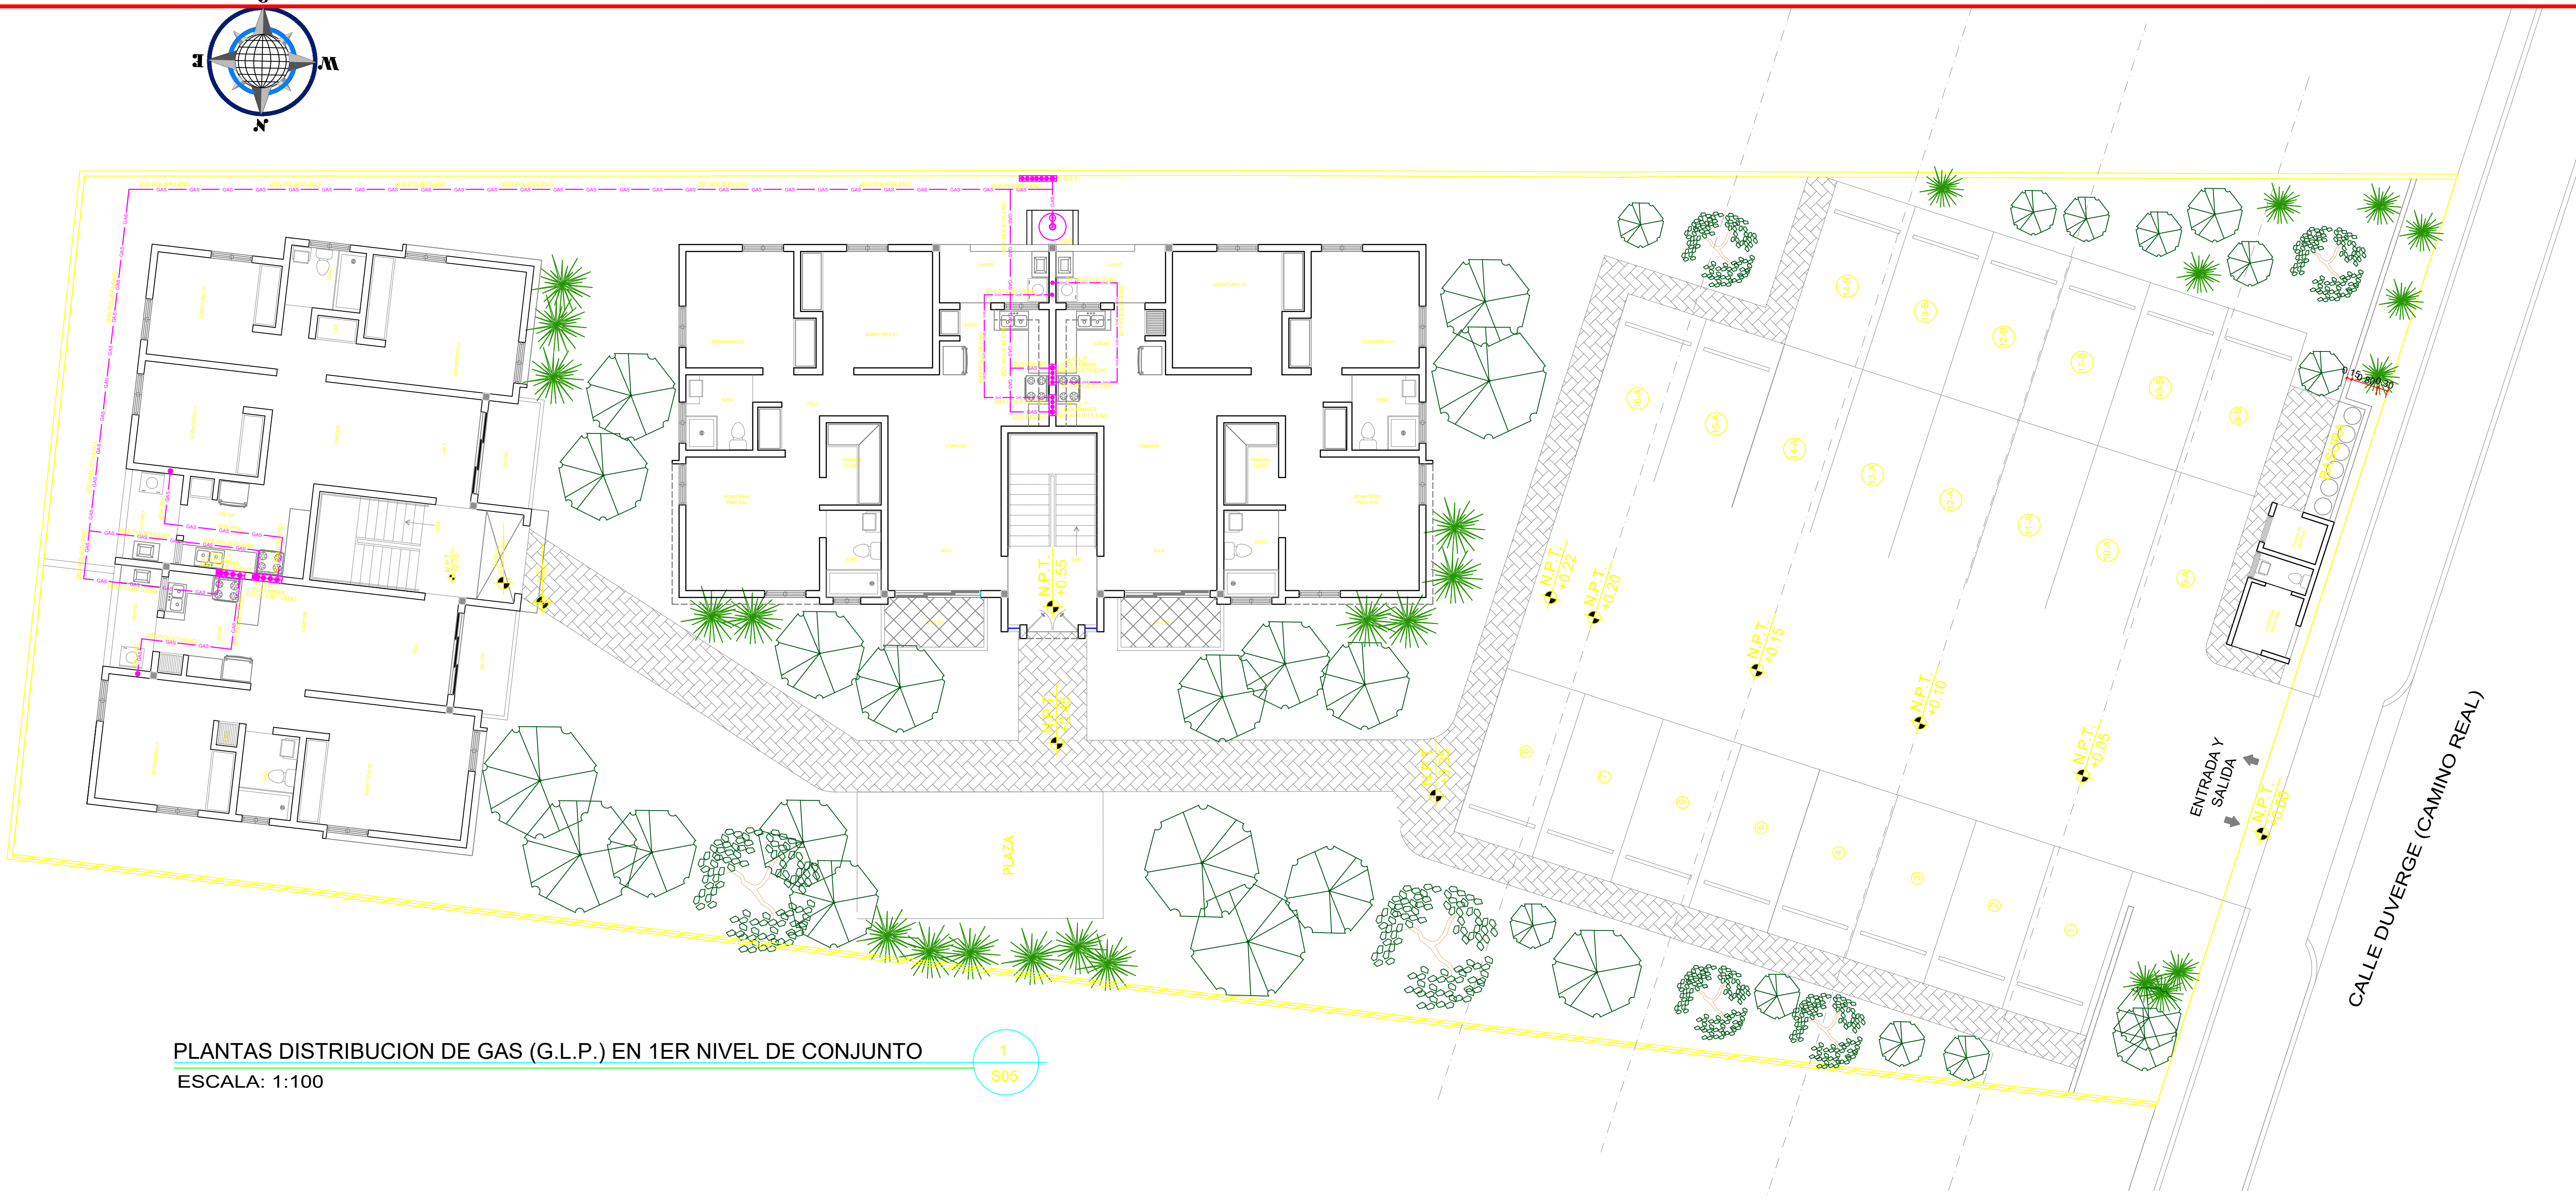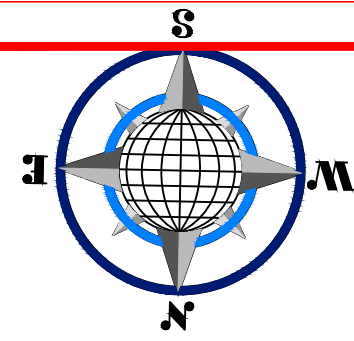


PLANTAS DISTRIBUCION DE GAS (G.L.P.) EN 1ER NIVEL DE CONJUNTO
ESCALA: 1:100

1
S05

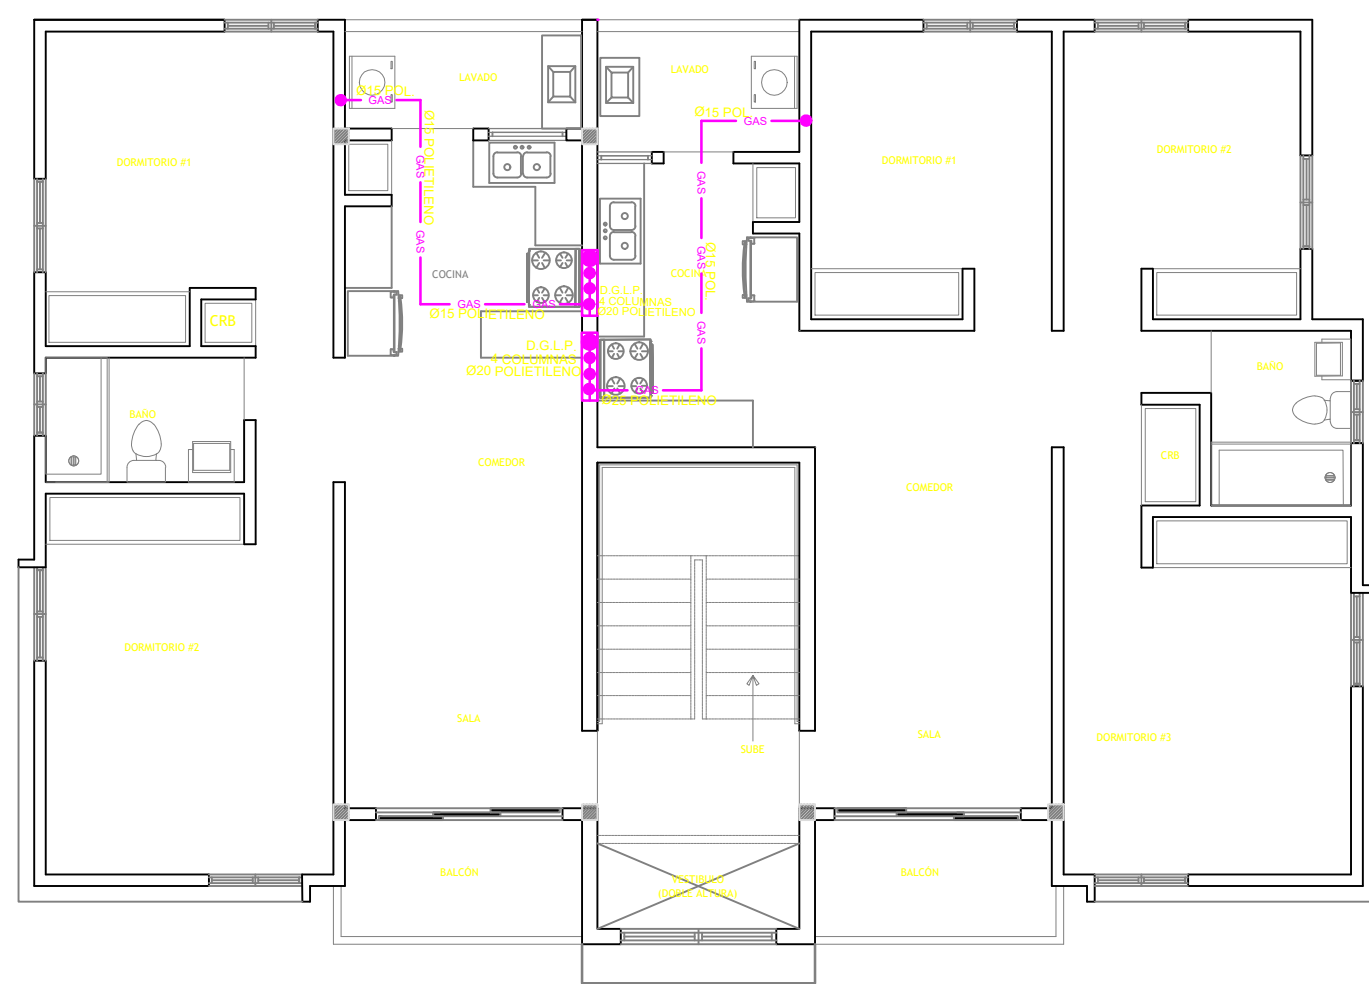




PLANTAS DISTRIBUCION DE GAS (G.L.P.) DE 2DO AL 4TO NIVEL BLOQUE A
ESCALA: 1:100

1
S05

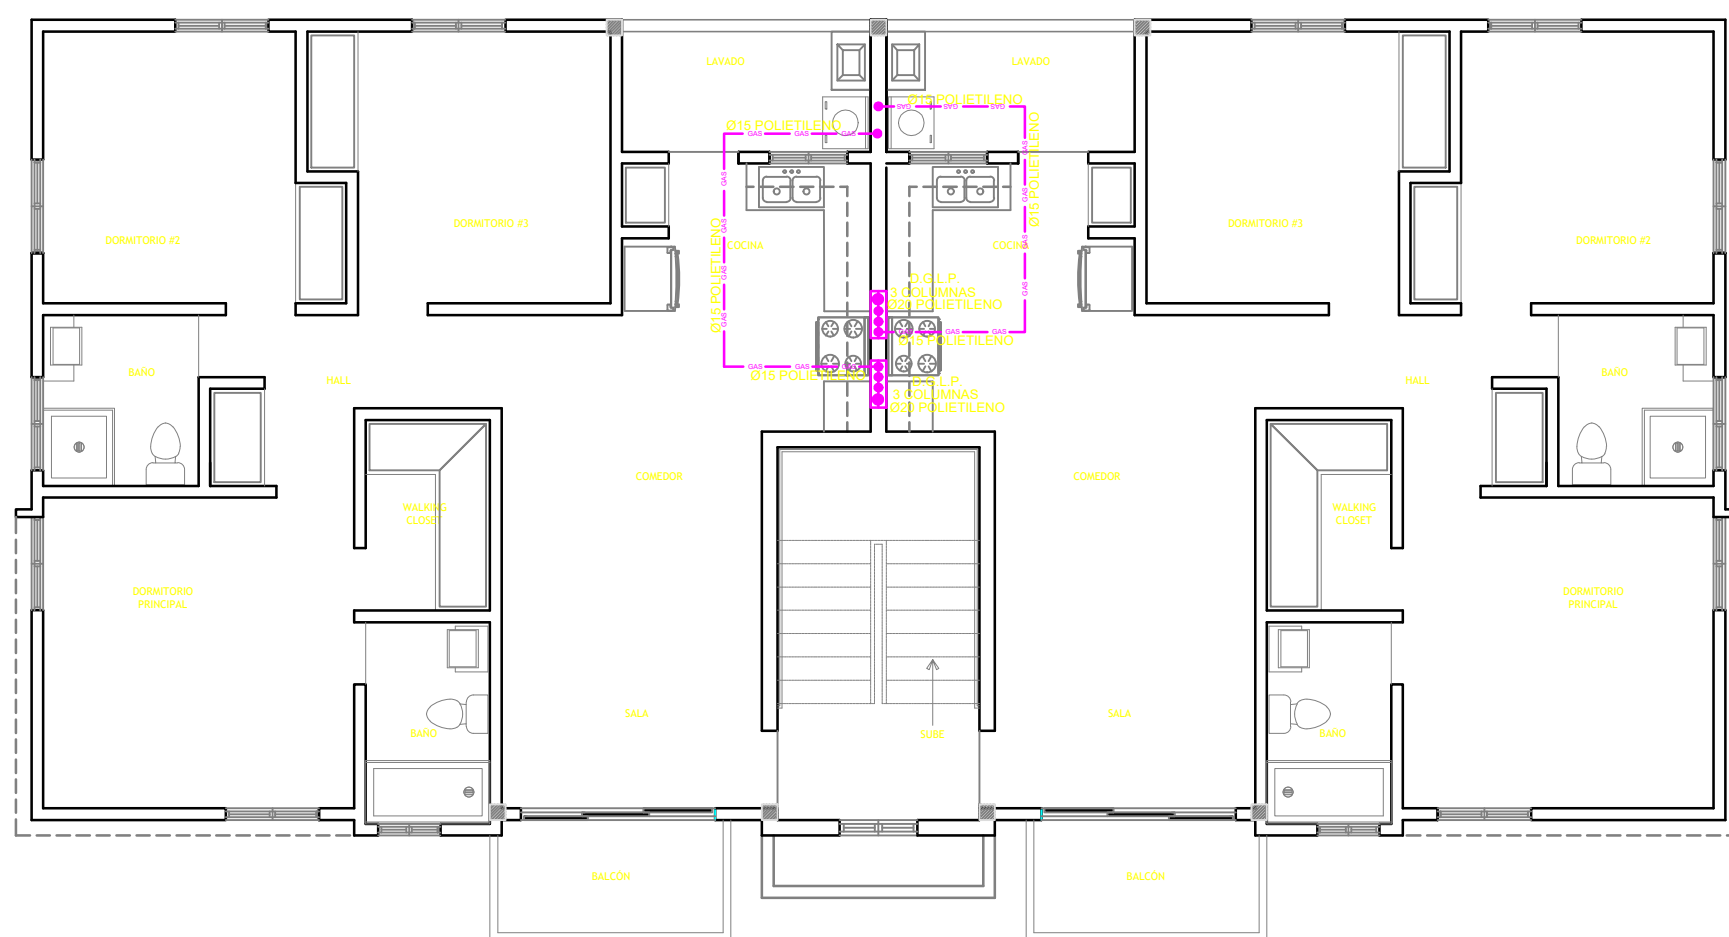

PLANTAS DISTRIBUCION DE GAS (G.L.P.) DE 2DO AL 3ER NIVEL BLOQUE B
ESCALA: 1:100

1
S05

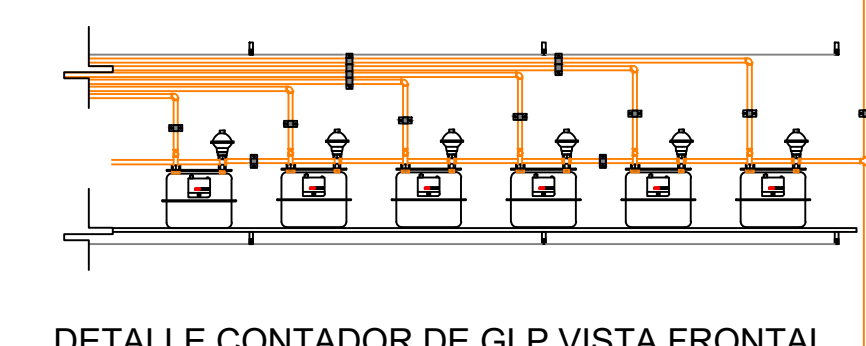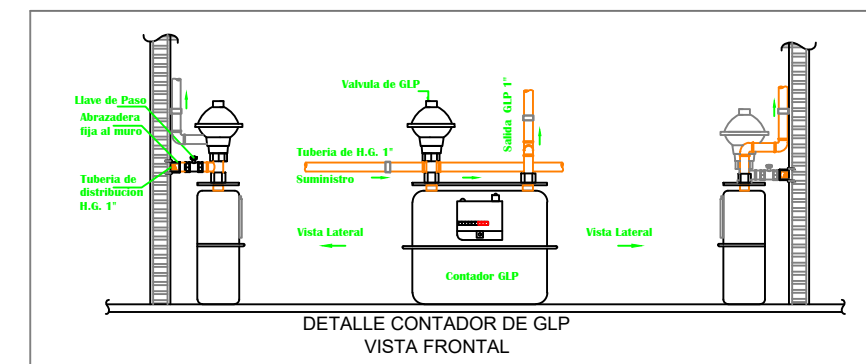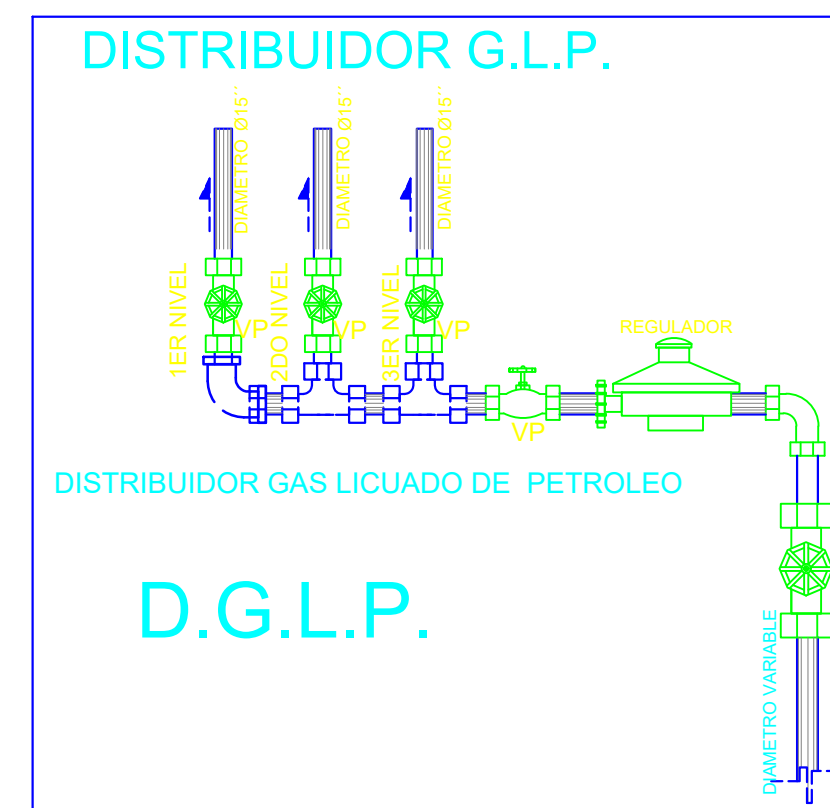

EQUIVALENCIAS DE PULGADAS A MEDIDAS EN POLIETILENO	
Ø1/2" POLIETILENO	Ø15 POLIETILENO
Ø1" POLIETILENO	Ø25 POLIETILENO



diaz melo & asocs.
ARQUITECTOS
Presidente Billini # 12, Bani, R.D. 522-4989
E-mail: diazmelohotmail.com

COLABORACION:



ARQUITECTURA DIGITAL
DISEÑOS-CONSTRUCCION-DIGITACION
COMPROMETIDOS CON SU TIEMPO
C/JUAN SANCHEZ RAMIREZ #56,
LOCAL 5 ZONA UASD TEL:221-5400

PROPIETARIO:
**GRUPO EMPRESARIAL
BANILEJO S.R.L.
GEBSA**

PROYECTISTAS:

DISEÑO ARQUITECTONICO:
DIAZMELO & ASOCS.
Arq. ISMAEL DIAZ MELO
Codia: 9604

DISEÑO SANITARIO:
Arq. HAMLET TEJEDA
Codia: 18303

DISEÑO ESTRUCTURAL:
ING. ODELIN TEJEDA
Codia: 23937

DISEÑO ELECTRICO:
ING. VILLYS SANCHEZ
Codia: 19060

CONTENIDO:
PLANTAS DE GAS

PROYECTO:
RESIDENCIAL GEBSA IV

Fecha: MAYO/2018

UBICACION:
SOMBRERO, BANI, PROV. PERAVIA

Ref.: Acad 2000 Hoja No.
Escala: INDICADA 12

NOTAS:
TODAS LAS TERMINACIONES Y/O CAMBIOS EN EL SET DE DOCUMENTOS
CONSTRUCTIVOS DEBERAN SER APROBADOS POR EL SUPERVISOR
PREVIAMENTE A SU APLICACION EN LA OBRA
TODAS LAS MEDIDAS DE HUECOS Y DE SUPERFICIE A SER REVESTIDAS
SERAN RECTIFICADAS PREVIA FABRICACION DE LOS CORRIERES O LA
O LA INSTALACION DE LOS RECURRIMIENTOS
LAS TERMINACIONES Y/O DETALLES NO ESPECIFICADOS SERAN
DEFINIDOS ENTRE
EL DUEÑO Y EL AUTOR DEL PROYECTO
EL CONTRATISTA NO PODRA TOMAR DECISIONES
INCONSULTAS RESPECTO VARIACIONES EN EL CONTENIDO
DE ESTE DOCUMENTO
LOS PLANOS ARQUITECTONICOS MANDARAN RESPECTO A LOS DEMAS A
ANTE CUALQUIER
DIFERENCIA, PRIMARA LA INFORMACIONCONTENIDA EN LOS MISMOS