



PROYECTO:

UBICACION:

PROPIETARIO:

FIRMA:

DISEÑO ARQ:

ARQ. JANET ABREU DESANGLES

DISEÑO INTERIOR:

DISEÑO ESTRUCTURAL:

DISEÑO SANITARIO:

CODIA: 11027


RESPONSABLE DE OBRA:

TIPOLOGIA:


ESCALA:
1:100

Nº DE HOJA:
E-1.1

FECHA:
NOV 17 2025

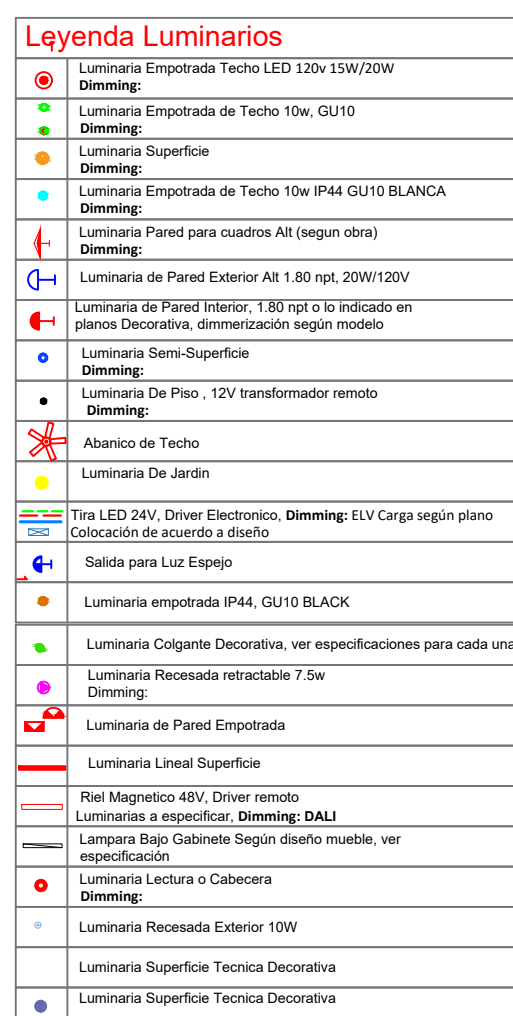

PLANTA ILUMINACION 1ER NIVEL
ESC. 1:100

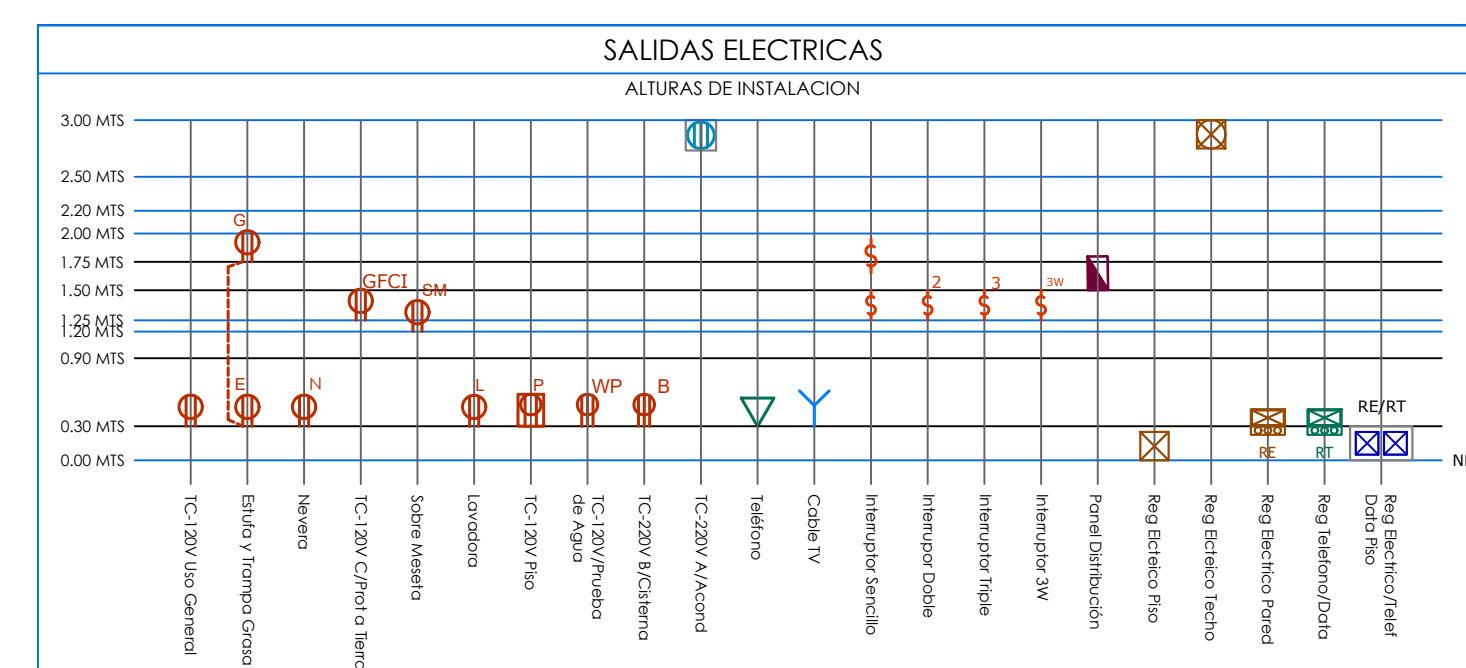

LEYENDA			
	SALIDA LUZ CENTAL		SALIDA TELEFONO
	SALIDA LUZ DE PARED		SALIDA CABLE TV
	SALIDA LUZ DE PARED EXTERIOR		CONTROL ABANICO
	SALIDA LUZ JARDIN		PUESTA A TIERRA
	SALIDA LUZ PISCINA		TUBERIA EMPOTRADA EN LOSA
	SALIDA INTERRUPTOR SENCILLO		TUBERIA EMPOTRADA EN PISO
	SALIDA INTERRUPTOR DOBLE		TUBERIA TELEFONICA EMP EN PISO
	SALIDA INTERRUPTOR TRES VIAS		TUBERIA EMPOTRADA EN PISO
	SALIDA TC-110V USO GENERAL		PANEL DE DISTRIBUCION
	SALIDA NEVERA		PANEL BOARD
	SALIDA ESTUFA		MAIN BRAKER
	SALIDA TC-110V SOBRE MESETA		REGISTRO ELECTRICO
	SALIDA LAVADORA		REGISTRO TELEFONICO
	SALIDA SECADORA		
	SALIDA TC-220V A/ACond		
	SALIDA CALENTADOR		
	SALIDA TC-110V C/PROTECCION A TIERRA		



Galerías Puntacona 65
Puntacona Village
La Altagracia, República Dominicana
Tel: 809 831 0903
Cels: 809 350 1696 / 809 753 2262
E: desanglesabreuarquitectos@gmail.com

PROYECTO:

CASA ERNA
LAS NASAS 09

UBICACION:

LAS NASAS
PUNTAONA RESORT & CLUB

PROPIETARIO:

MR. JON KNAPP
MRS. MELISSA RACITI

FIRMA:

DISEÑO ARQ:

ARQ. MARIO E. DESANGLES
CODIA: 12067

ARQ. JANET ABREU DESANGLES

COLABORACION: ARQ. LADDY Y. BERROA
ARQ. MARIA C. FABIAN

DISEÑO INTERIOR:

DISEÑO ESTRUCTURAL:

DISEÑO SANITARIO:

DISEÑO ELECTRICO:
ING. ONESIMO RIVERA
CODIA: 11027

RESPONSABLE DE OBRA:

DISCIPLINA: PLANOS ELECTRICOS

TIPOLOGIA: PLANTA ILUMINACION
SEGUNDO NIVEL

ESCALA:



1:75

Nº DE HOJA:

E-1.2

FECHA:

NOV 17 2025

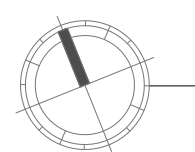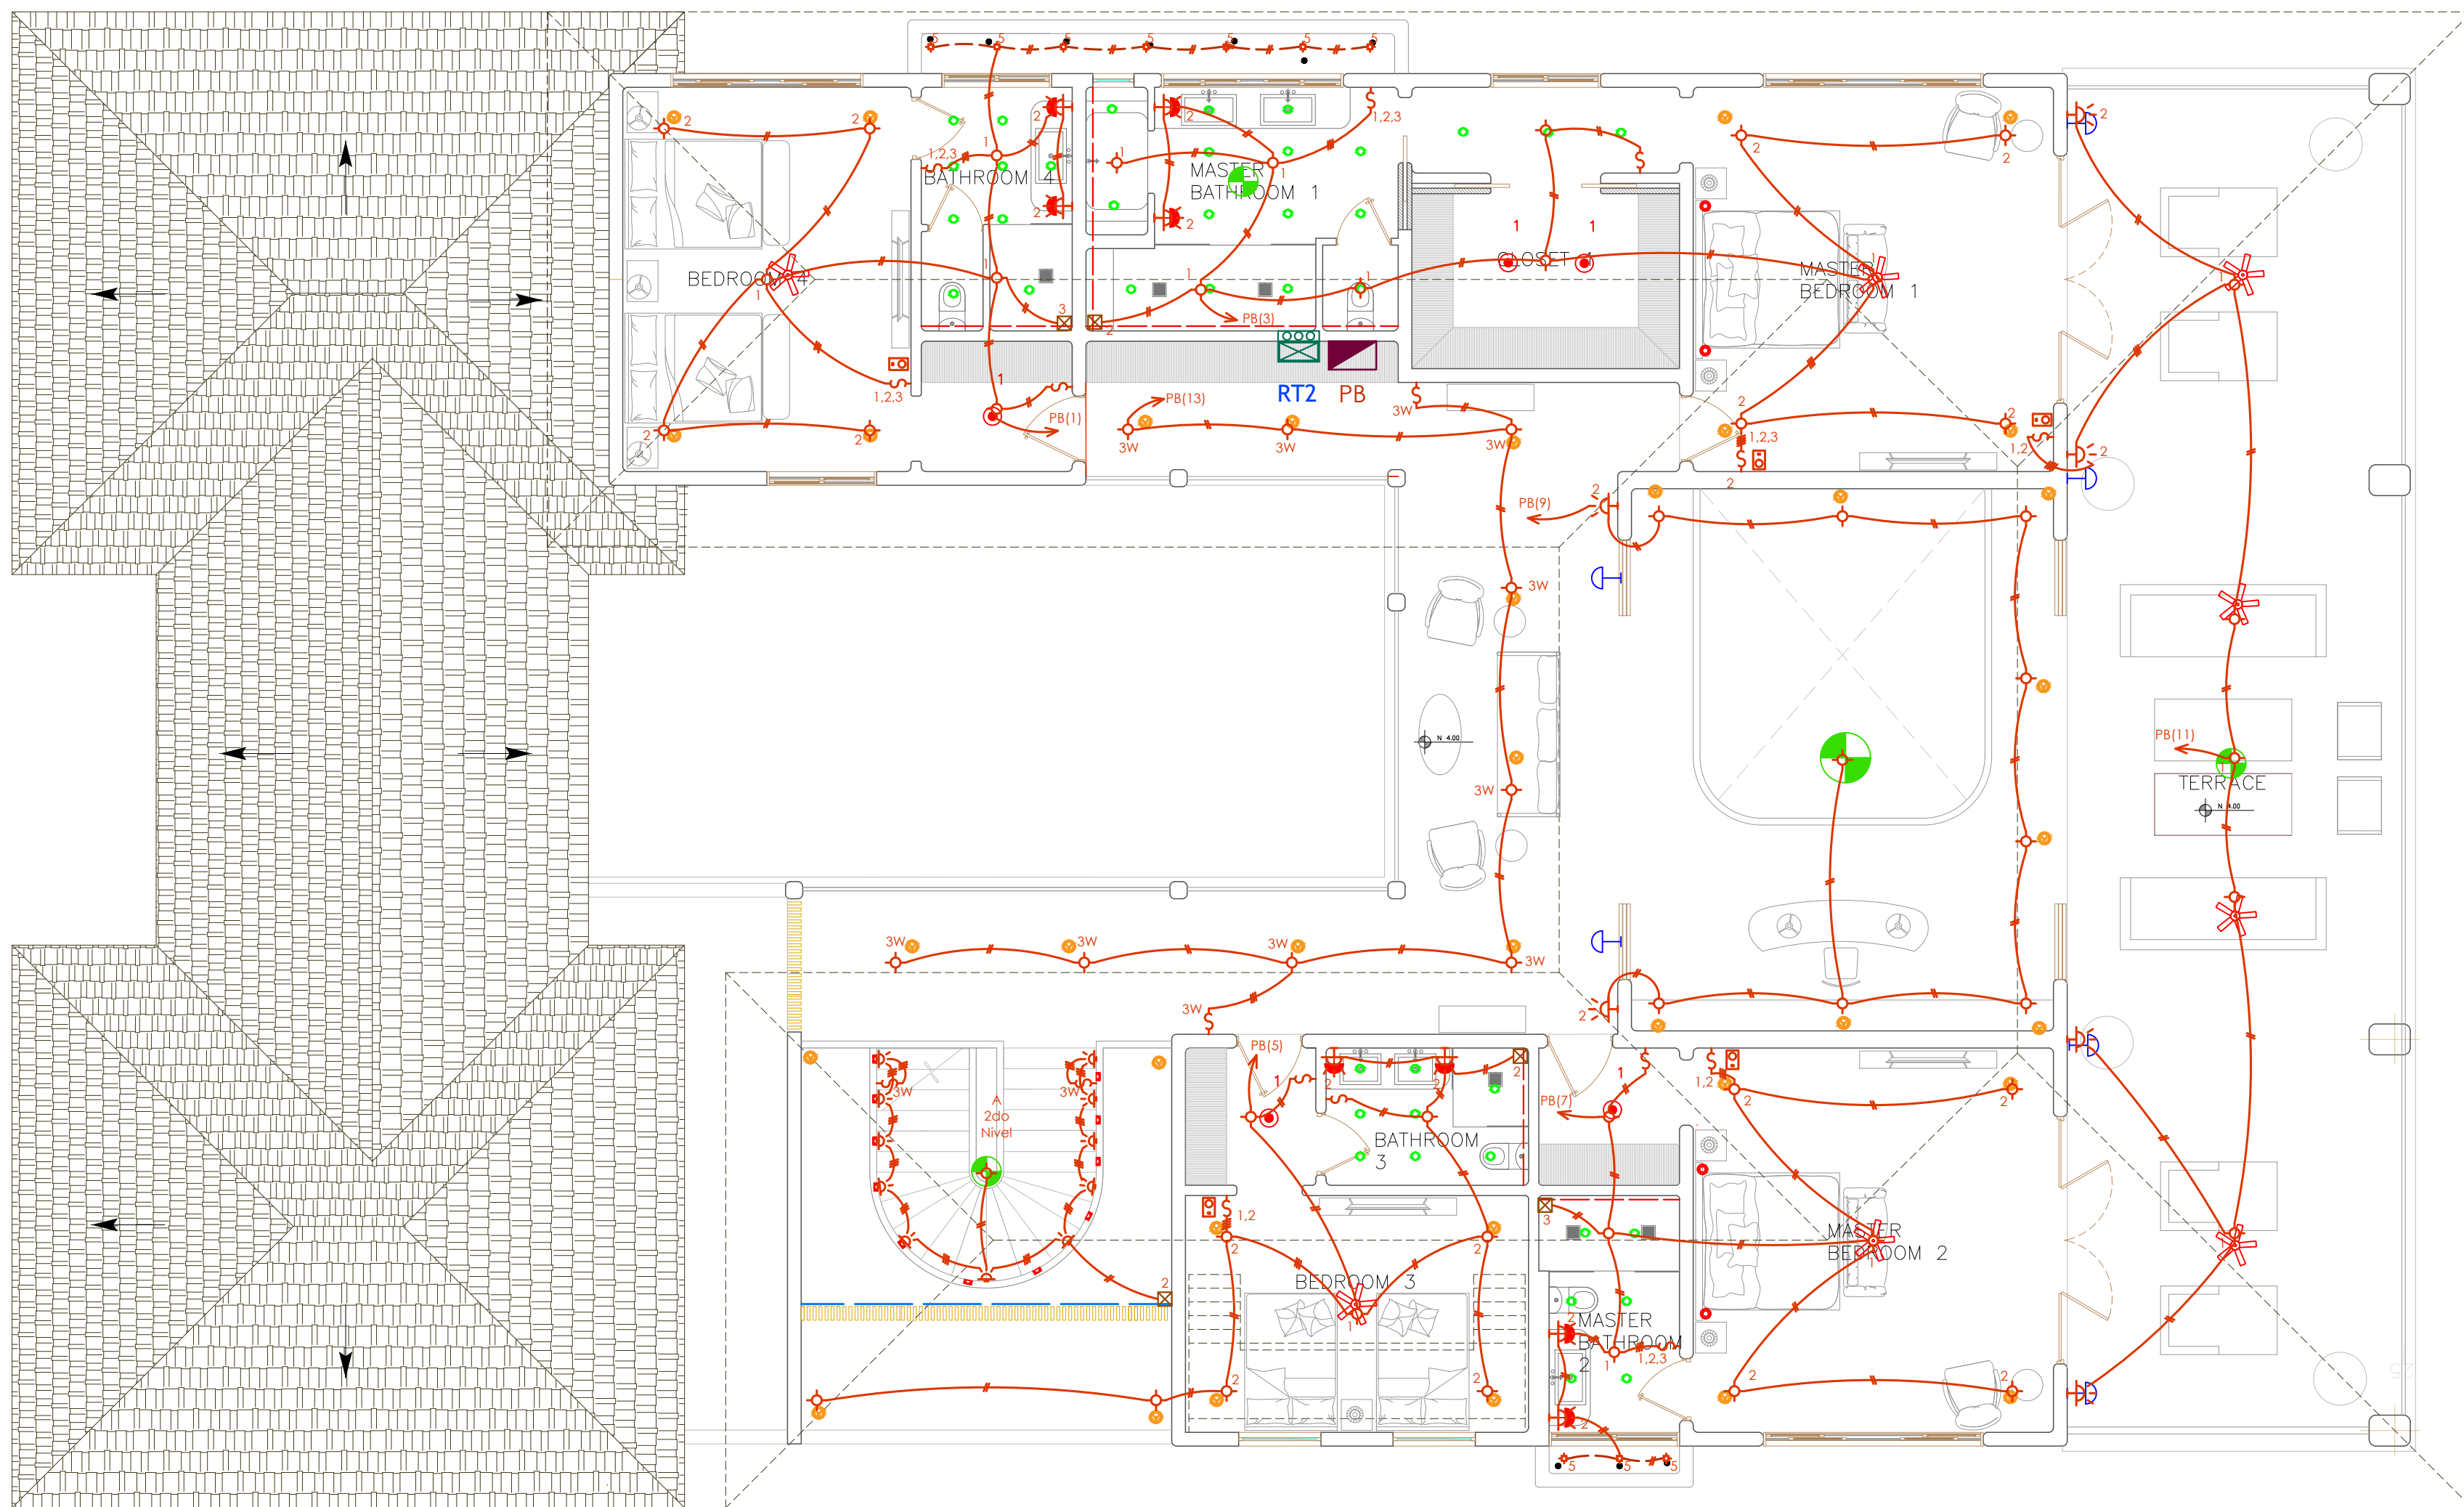


PLANTA ILUMINACION SEGUNDO NIVEL

ESC. 1:75

Leyenda Luminarios

	Luminaria Empotrada Techo LED 120v 15W/20W
	Dimming:
	Luminaria Empotrada de Techo 10w, GU10
	Dimming:
	Luminaria Superficie
	Dimming:
	Luminaria Empotrada de Techo 10w IP44 GU10 BLANCA
	Dimming:
	Luminaria de Pared Exterior Alt 1.80 rpt, 20W/120V
	Dimming:
	Luminaria de Pared Interior, 1.80 rpt o lo indicado en planos Decorativa, dimmerización según modelo
	Luminaria Semi-Superficie
	Dimming:
	Luminaria De Piso, 12V transformador remoto
	Dimming:
	Abanico de Techo
	Luminaria de Jardín
	Tira LED 24V, Driver Electronico, Dimming: ELV Carga según plano
	Colocación de acuerdo a diseño
	Salida para Luz Espejo
	Luminaria empotrada IP44, GU10 BLACK
	Luminaria Colgante Decorativa, ver especificaciones para cada una
	Luminaria Recessada retractable 7.5w
	Dimming:
	Luminaria de Pared Empotrada
	Luminaria Lineal Superficie
	Rel Magnético 48V, Driver remoto
	Luminarias a especificar, Dimming: DALI
	Lampara Bajo Gabinete Según diseño mueble, ver especificación
	Luminaria Lectura o Cabeceira
	Dimming:
	Luminaria Recessada Exterior 10W
	Luminaria Superficie Tecnica Decorativa
	Luminaria Superficie Tecnica Decorativa

	Sensor de Encendido
	Potible Botonera de Control de Iluminación
	Interruptor O botonera Sencillo, del Sistema de Control

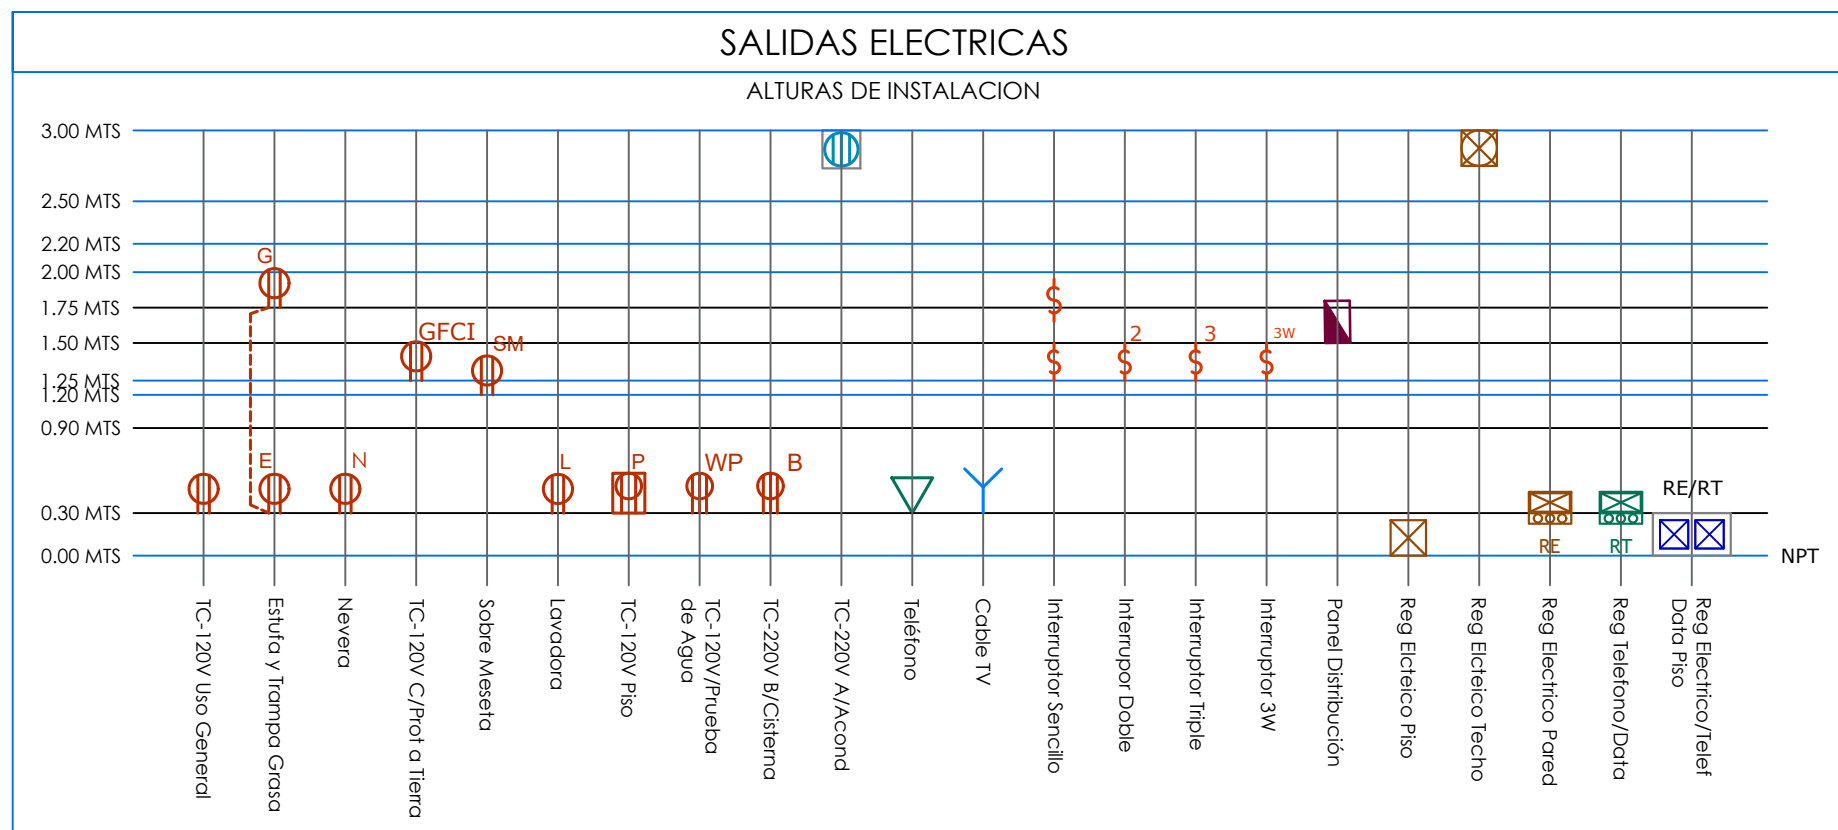

LEYENDA

	SALIDA LUZ CENTRAL		SALIDA TELEFONO
	SALIDA LUZ DE PARED		SALIDA CABLE TV
	SALIDA LUZ DE PARED EXTERIOR		CONTROL ABANICO
	SALIDA LUZ JARDIN		PUESTA A TIERRA
	SALIDA LUZ PISCINA		TUBERIA EMPOTRADA EN LOSA
	SALIDA INTERRUPTOR SENCILLO		TUBERIA EMPOTRADA EN PISO
	SALIDA INTERRUPTOR DOBLE		TUBERIA TELEFONICA EMP EN PISO
	SALIDA INTERRUPTOR TRES VIAS		TUBERIA EMPOTRADA EN PISO
	SALIDA TC-110V USO GENERAL		PANEL DE DISTRIBUCION
	SALIDA NEVERA		PANEL BOARD
	SALIDA ESTUFA		MAIN BRAKER
	SALIDA TC-110V SOBRE MESETA		REGISTRO ELECTRICO
	SALIDA LAVADORA		REGISTRO TELEFONICO
	SALIDA SECADORA		
	SALIDA TC-220V A/ACond		
	SALIDA CALENTADOR		
	SALIDA TC-110V C/PROTECCION A TIERRA		



Galerías Puntacana 65
Puntacana Village
La Altagracia, República Dominicana
Tel: 809 831 0903
Cels: 809 350 1696 / 809 753 2262
E: desanglesabreuarquitectos@gmail.com

PROYECTO:
CASA ERNA
LAS NASAS 09

UBICACION:
LAS NASAS
PUNTACANA RESORT & CLUB

PROPIETARIO:
MR. JON KNAPP
MRS. MELISSA RACITI
FIRMA:

DISEÑO ARQ:
ARQ. MARIO E. DESANGLES
CODIA: 12067

ARQ. JANET ABREU DESANGLES

COLABORACION: ARQ. LADDY Y. BERROA
ARQ. MARIA C. FABIAN

DISEÑO INTERIOR:

DISEÑO ESTRUCTURAL:

DISEÑO SANITARIO:

DISEÑO ELECTRICO:
ING. ONESIMO RIVERA
CODIA: 11027

RESPONSABLE DE OBRA:


DISCIPLINA: PLANOS ELECTRICOS

TIPOLOGIA: PLANTA TOMACORRIENTES
PRIMER NIVEL

ESCALA:
1:100


Nº DE HOJA:
E-1.3

FECHA:
NOV 17 2025

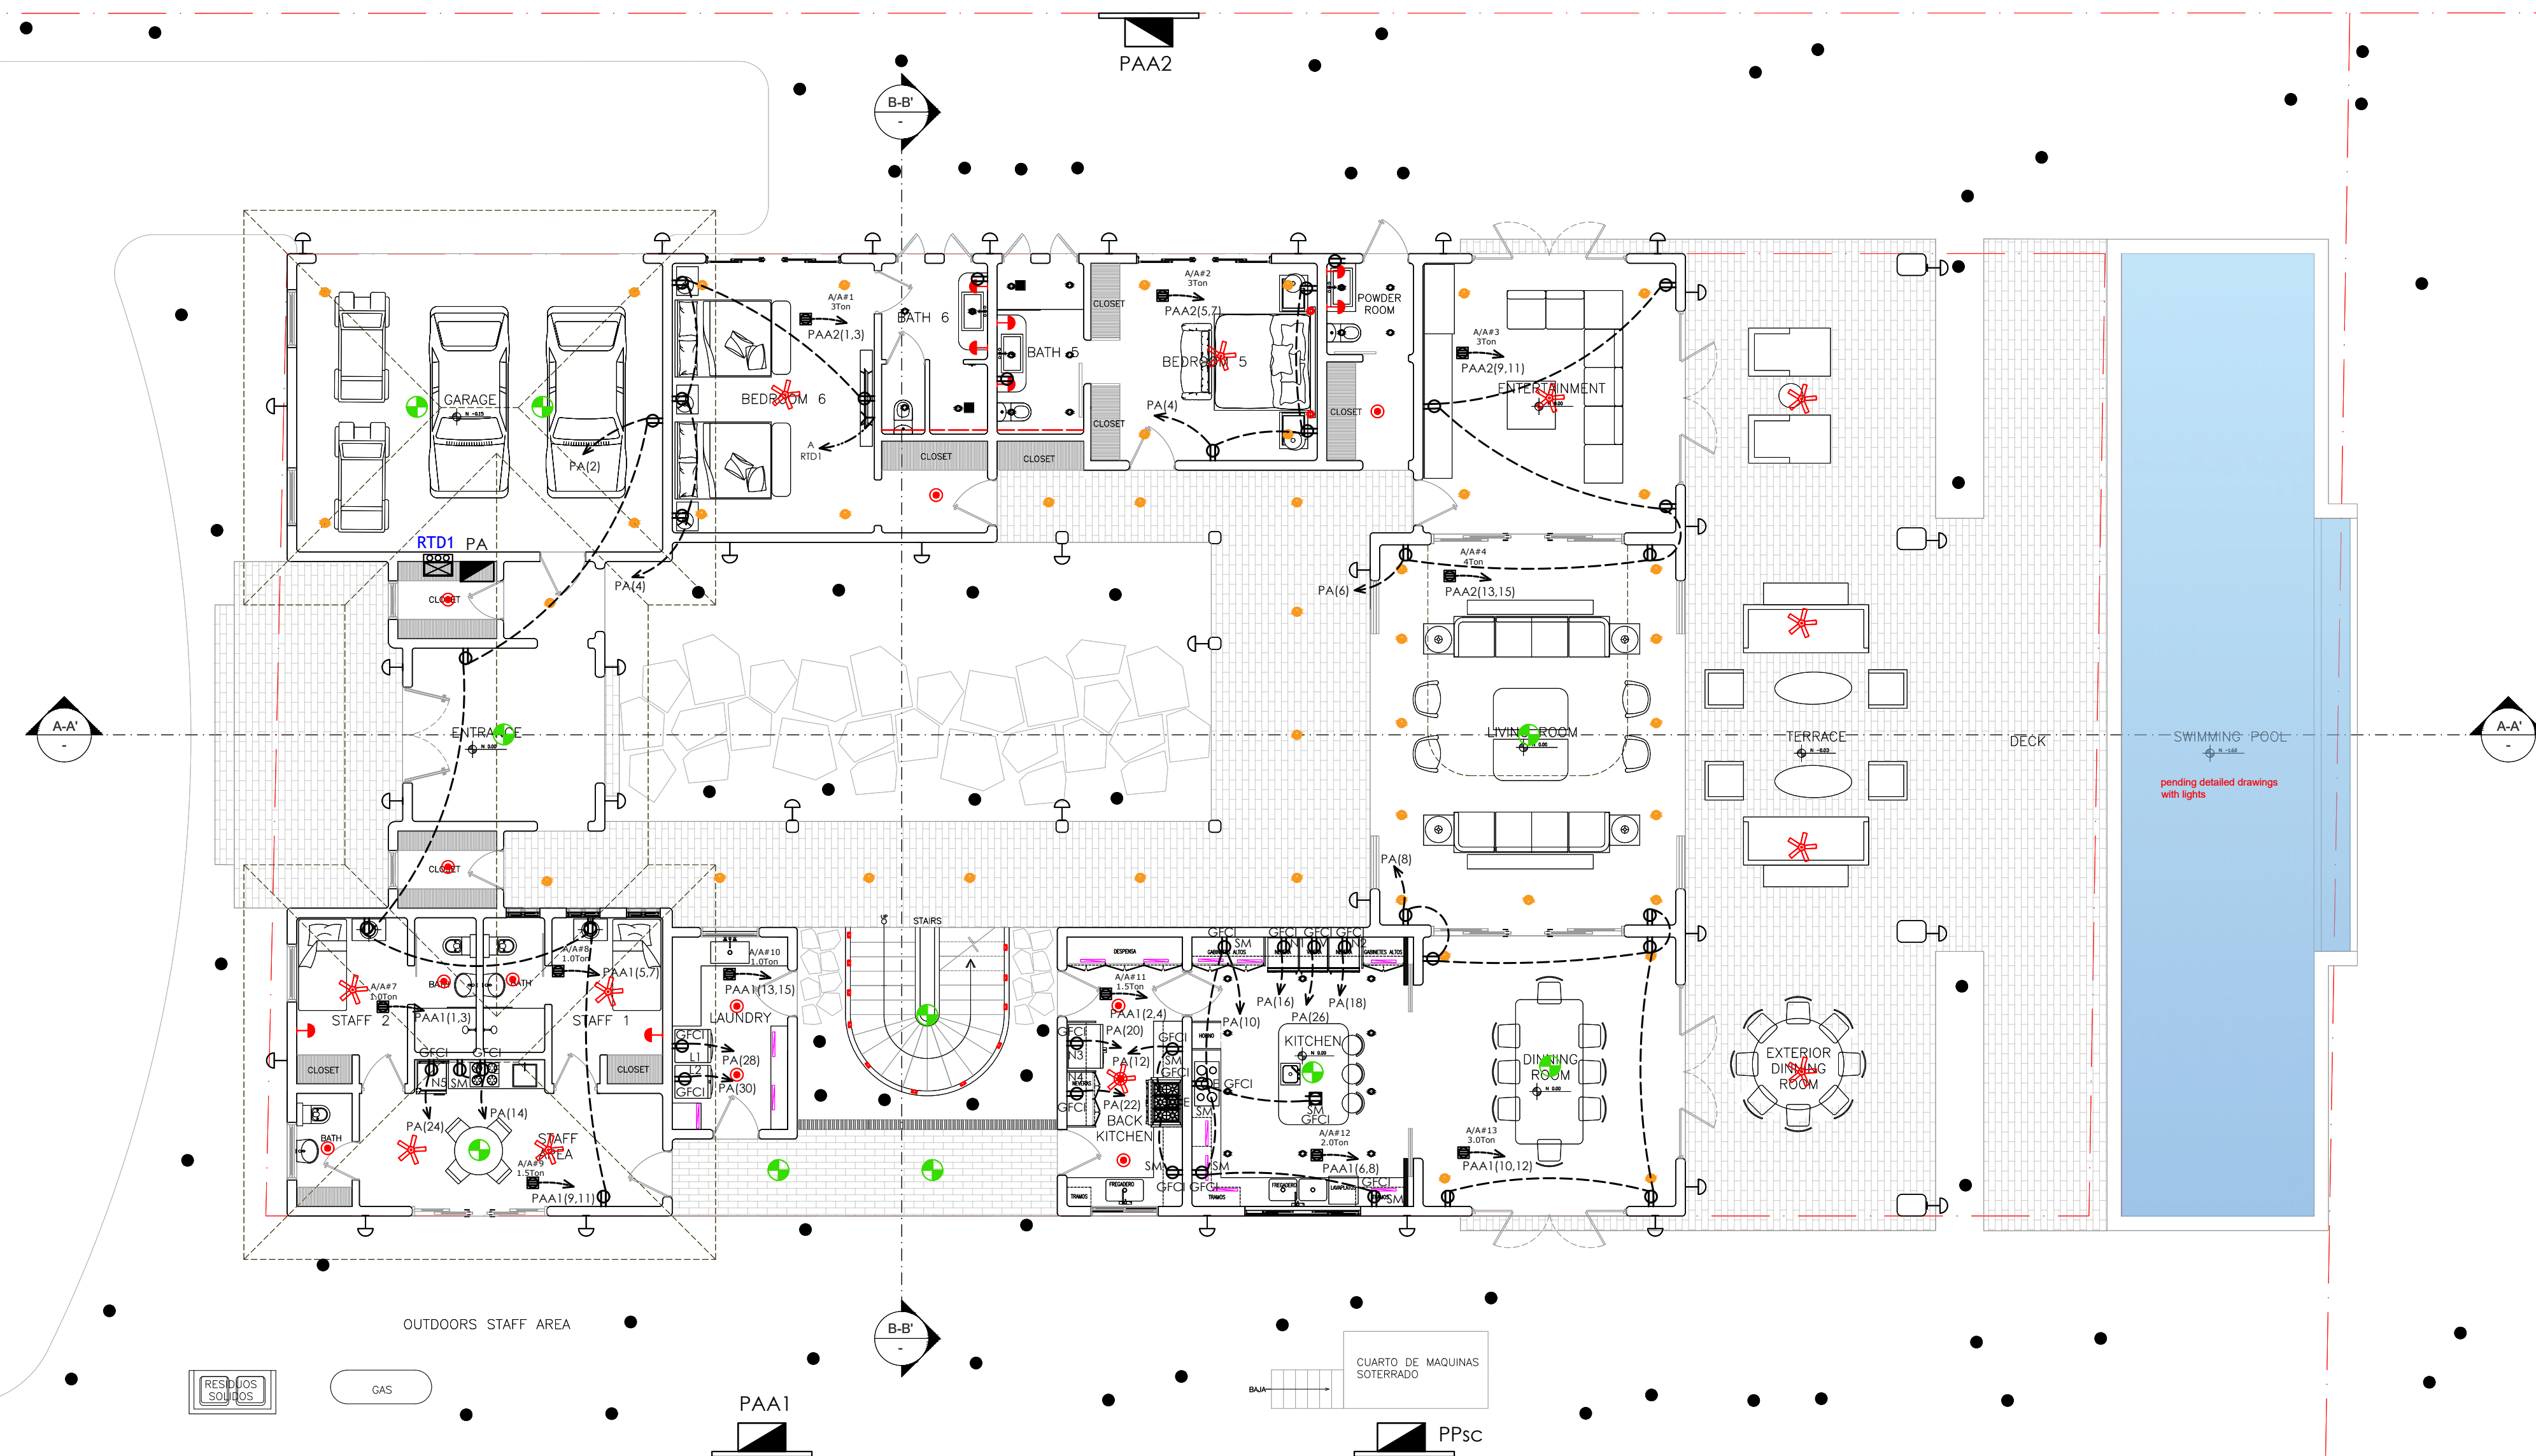

Leyenda Luminarios	
	Luminaria Empotrada Techo LED 15w/20w Dimming
	Luminaria Empotrada de Techo 10w GU10 Dimming
	Luminaria Superficie Dimming
	Luminaria Empotrada de Techo 10w IP44 GU10 BLANCA Dimming
	Luminaria Pared para cuadros Art (segun obra) Dimming
	Luminaria de Pared Exterior Art 1.80 opt. 20W/120V Dimming
	Luminaria de Pared Interior 1.80 opt. o lo modificado en planos Decorativos, dimencionamiento segun modelo
	Luminaria Semi-Superficie Dimming
	Luminaria De Piso, 12V transformador remoto Dimming
	Abanico de Techo
	Luminaria De Jardin
	Tubo LED 24V, Driver Electronico, Dimming: ELV Cargo segun plano Colocacion de accesorios a estudio
	Salida para Luz Empotrada
	Luminaria empotrada IP44, GU10 BLACK
	Luminaria Colgante Decorativa, ver especificaciones para cada una
	Luminaria Recessada retráctil 7.5w Dimming
	Luminaria de Pared Empotrada
	Luminaria Lineal Superficie
	Tubo Magnético 48V, Driver remoto
	Luminaria a especificar, Dimming: DALI
	Lampara Bajo Gabinete Segun diseño mueble, ver especificacion
	Luminaria Lectura o Cateadora Dimming
	Luminaria Recessada Exterior 10W
	Luminaria Superficie Tecnica Decorativa
	Luminaria Superficie Tecnica Decorativa

PLANTA TOMACORRIENTES PRIMER NIVEL
ESC. 1:100

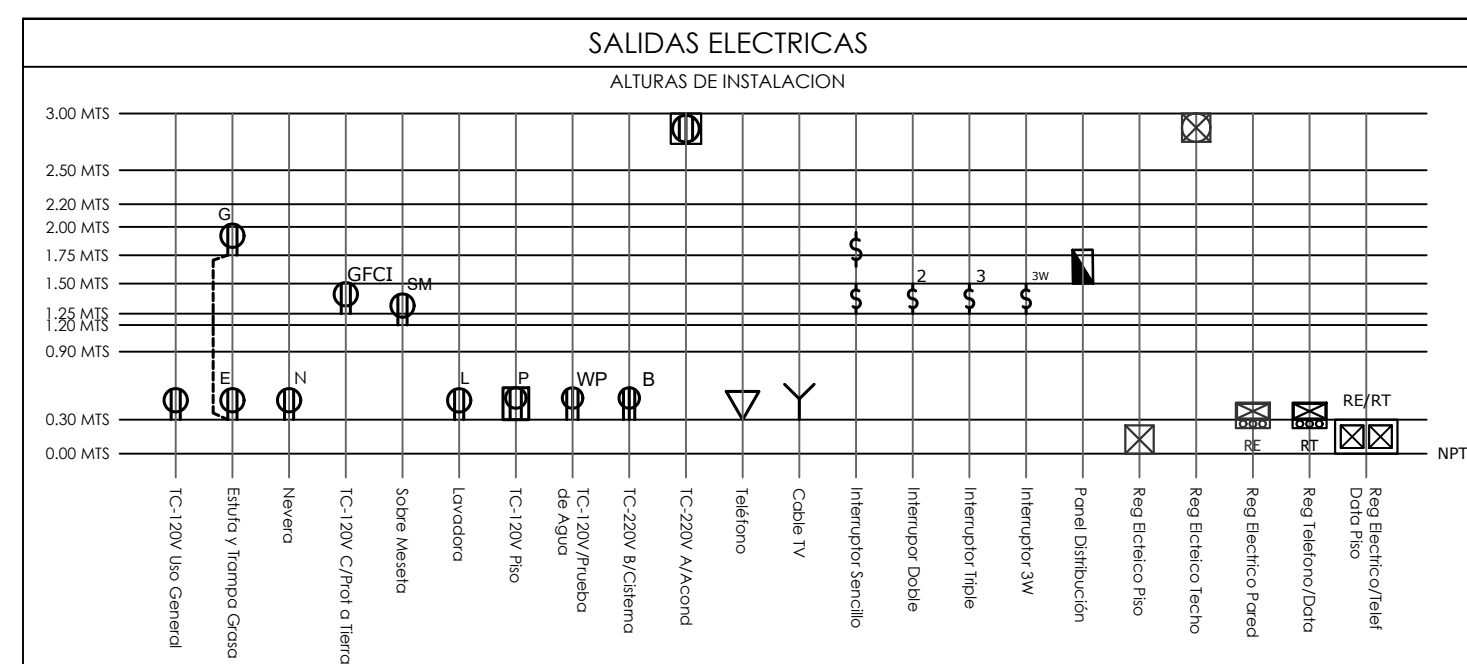

LEYENDA	
	SALIDA LUZ CENTRAL
	SALIDA LUZ DE PARED
	SALIDA LUZ DE PARED EXTERIOR
	SALIDA LUZ JARDIN
	SALIDA LUZ PISCINA
	SALIDA INTERRUPTOR SENCILLO
	SALIDA INTERRUPTOR DOBLE
	SALIDA INTERRUPTOR TRES VIAS
	SALIDA TC-110V USO GENERAL
	SALIDA NEVERA
	SALIDA ESTUFA
	SALIDA TC-110V SOBRE MESETA
	SALIDA LAVADORA
	SALIDA SECADORA
	SALIDA TC-220V A/Cond
	SALIDA CALENTADOR
	SALIDA TC-110V C/PROTECCION A TIERRA
	SALIDA TELEFONO
	SALIDA CABLE TV
	CONTROL ABANICO
	PUESTA A TIERRA
	TUBERIA EMPOTRADA EN LOSA
	TUBERIA EMPOTRADA EN PISO
	TUBERIA TELEFONICA EMP EN PISO
	TUBERIA EMPOTRADA EN PISO
	PANEL DE DISTRIBUCION
	PANEL BOARD
	MAIN BRAKER
	REGISTRO ELECTRICO
	REGISTRO TELEFONICO



Galerías Puntacana 65
Puntacana Village
La Altagracia, República Dominicana
Tel: 809 831 0903
Cels: 809 350 1696 / 809 753 2262
E: desanglesabreuarquitectos@gmail.com

PROYECTO:

CASA ERNA
LAS NASAS 09

UBICACION:

LAS NASAS
PUNTACANA RESORT & CLUB

PROPIETARIO:

MR. JON KNAPP
MRS. MELISSA RACITI

FIRMA:

DISEÑO ARQ:

ARQ. MARIO E. DESANGLES
CODIA: 12067

ARQ. JANET ABREU DESANGLES

COLABORACION: ARQ. LADDY Y. BERROA
ARQ. MARIA C. FABIAN

DISEÑO INTERIOR:

DISEÑO ESTRUCTURAL:

DISEÑO SANITARIO:

DISEÑO ELECTRICO:
ING. ONESIMO RIVERA
CODIA: 11027

RESPONSABLE DE OBRA:

DISCIPLINA: PLANOS ELECTRICOS

TIPOLOGIA: PLANTA TOMACORRIENTES
SEGUNDO NIVEL

ESCALA:



1:75

Nº DE HOJA:

E-1.4

FECHA:

NOV 17 2025

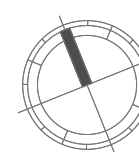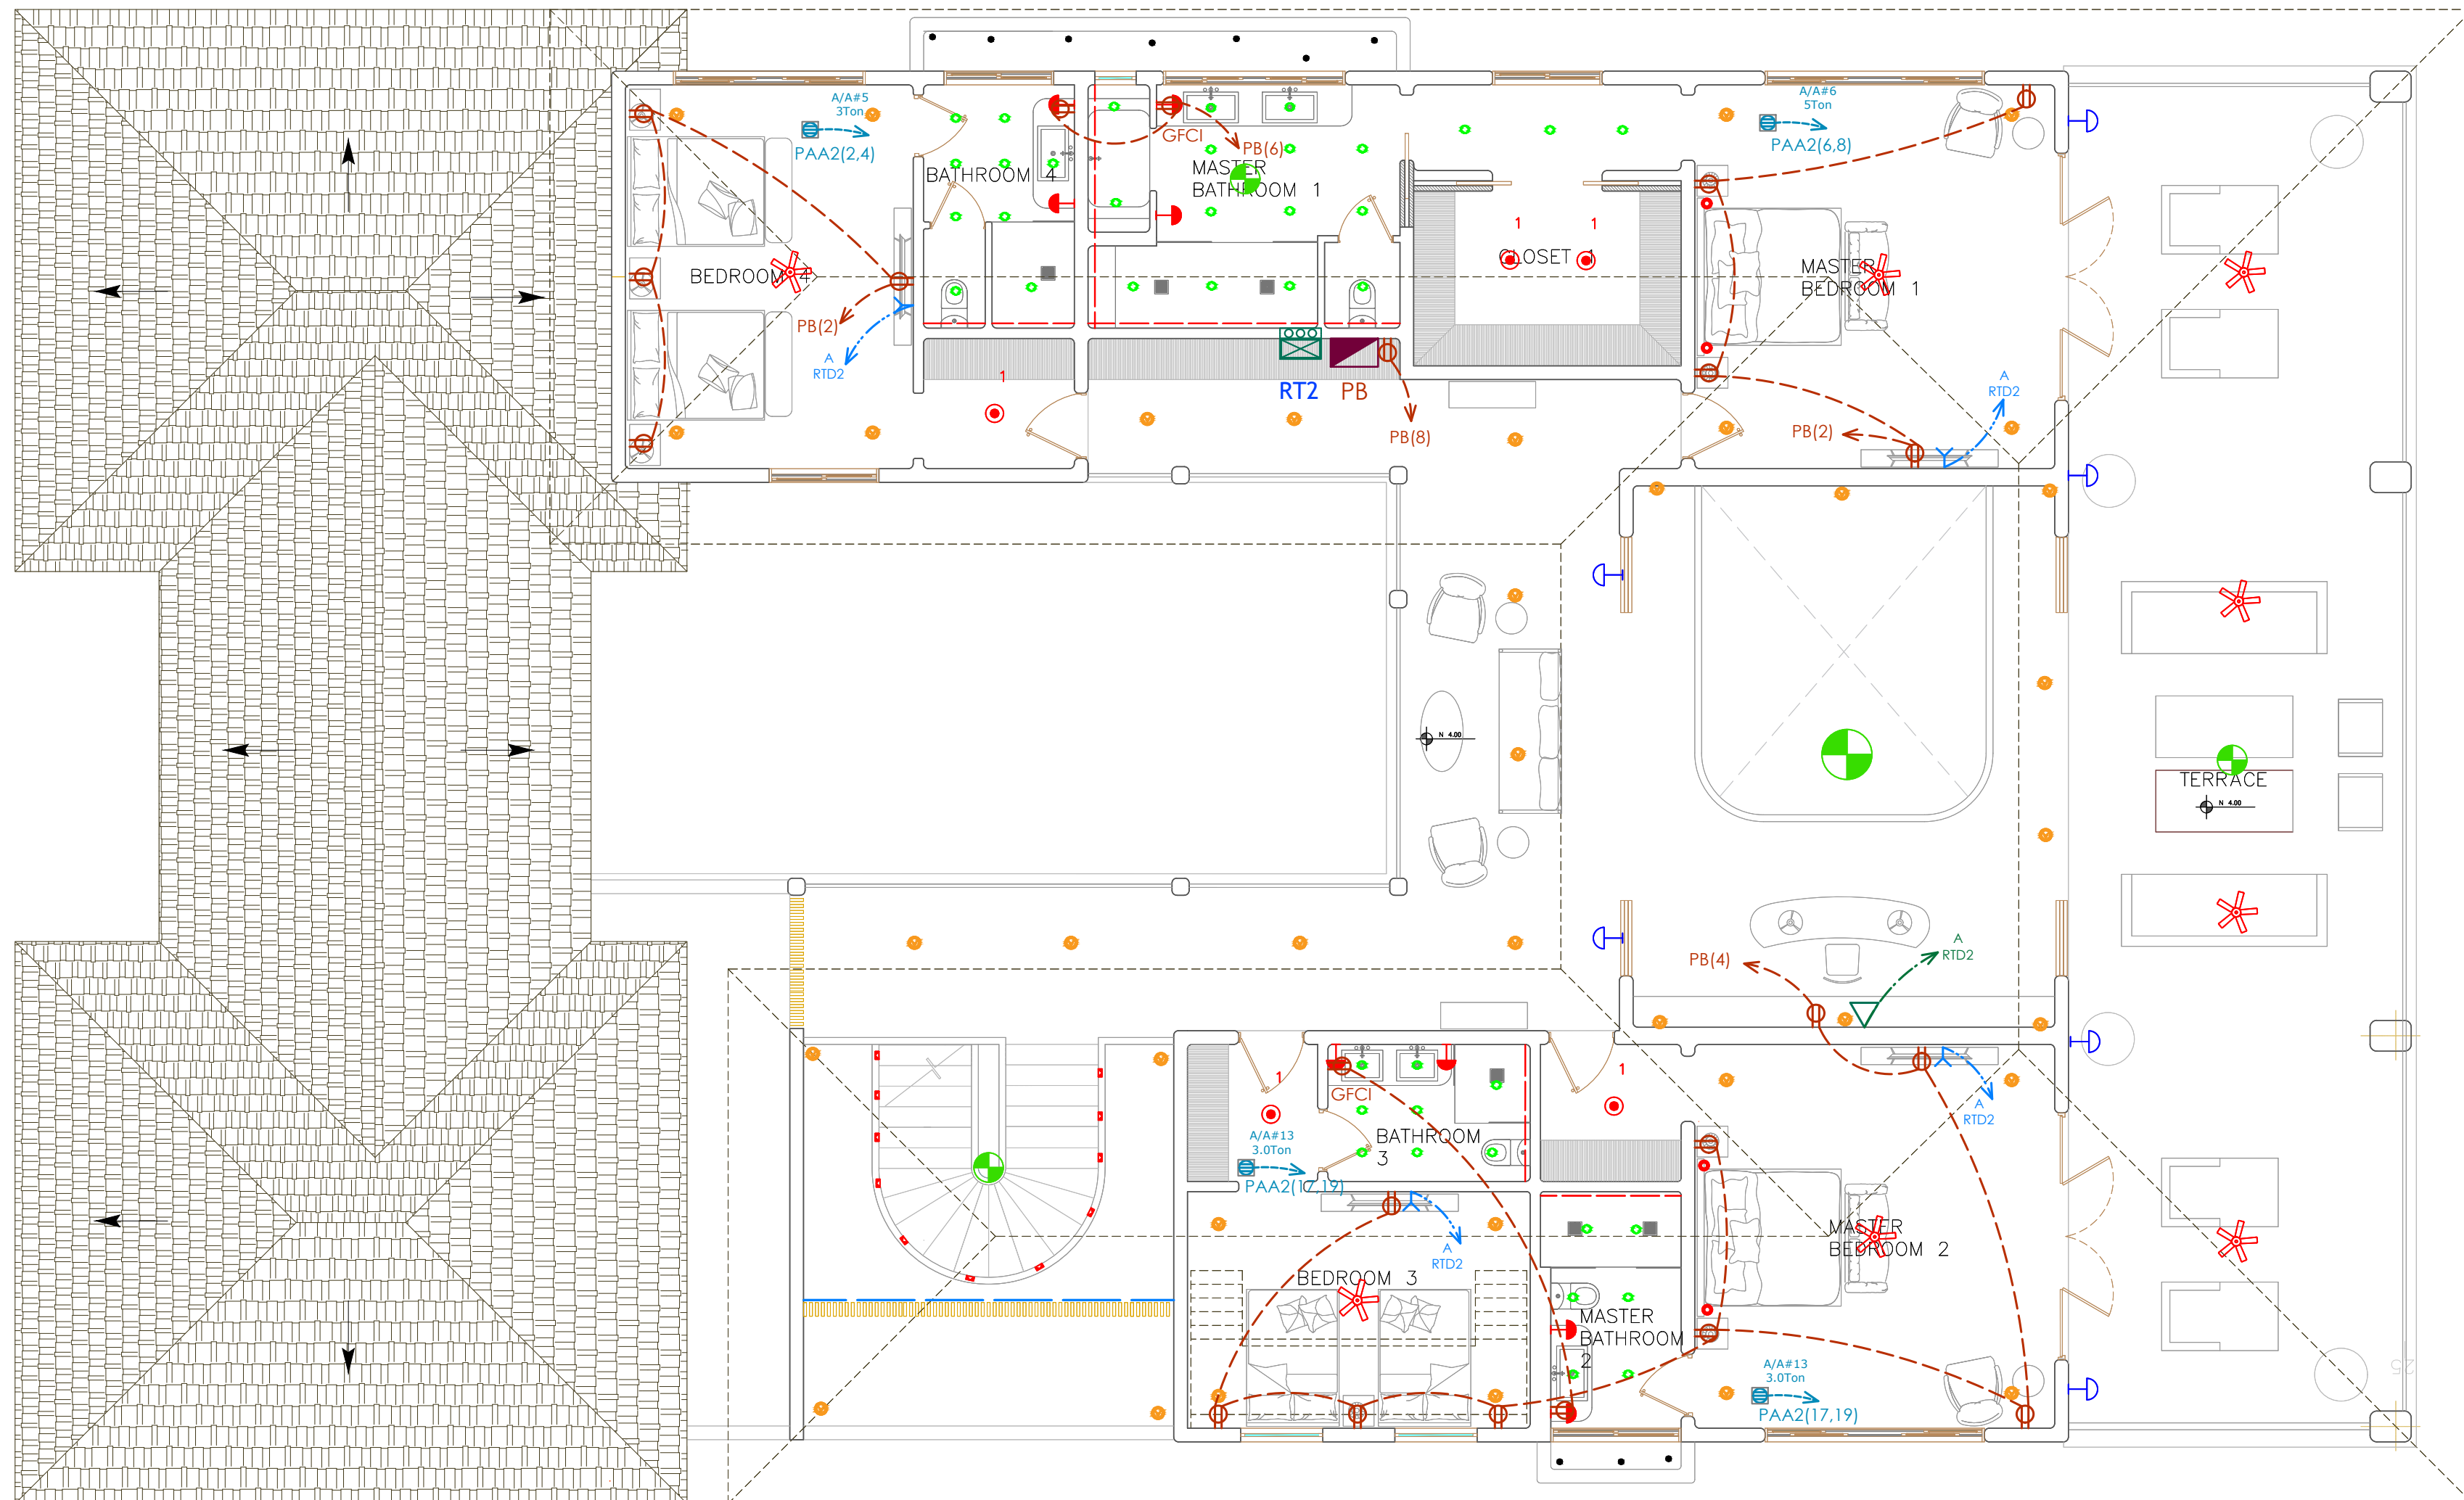


PLANTA TOMACORRIENTES SEGUNDO NIVEL

ESC. 1:75

Leyenda Luminarios	
	Luminaria Empotrada Techo LED 120v 15W/20W
	Dimming:
	Luminaria Empotrada de Techo 10w, GU10
	Dimming:
	Luminaria Superficie
	Dimming:
	Luminaria Empotrada de Techo 10w IP44 GU10 BLANCA
	Dimming:
	Luminaria Pared para cuadros A8 (segun obra)
	Dimming:
	Luminaria de Pared Exterior A8 1.80 rpt, 20W/120V
	Dimming:
	Luminaria de Pared Interior: 1.80 rpt o lo indicado en planos Decorativa, dimmerización según modelo
	Dimming:
	Luminaria Semi-Superficie
	Dimming:
	Luminaria De Piso, 12V transformador remoto
	Dimming:
	Abanico de Techo
	Luminaria De Jardin
	Tira LED 24V, Driver Electronico, Dimming: ELV Carga según plano
	Colocación de acuerdo a diseño
	Salida para Luz Espejo
	Luminaria empotrada IP44, GU10 BLACK
	Luminaria Colgante Decorativa, ver especificaciones para cada una
	Luminaria Recessada retractable 7.5w
	Dimming:
	Luminaria de Pared Empotrada
	Luminaria Lineal Superficie
	Riel Magnético 48V, Driver remoto
	Luminarias a especificar, Dimming: DALI
	Lampara Bajo Gabinete Según diseño mueble, ver especificación
	Luminaria Lectura o Cabeceira
	Dimming:
	Luminaria Recessada Exterior 10W
	Luminaria Superficie Tecnica Decorativa
	Luminaria Superficie Tecnica Decorativa

	Sensor de Encendido
	Posible Botones de Control de Iluminación
	Interruptor O botones Sencillos del Sistema de Control

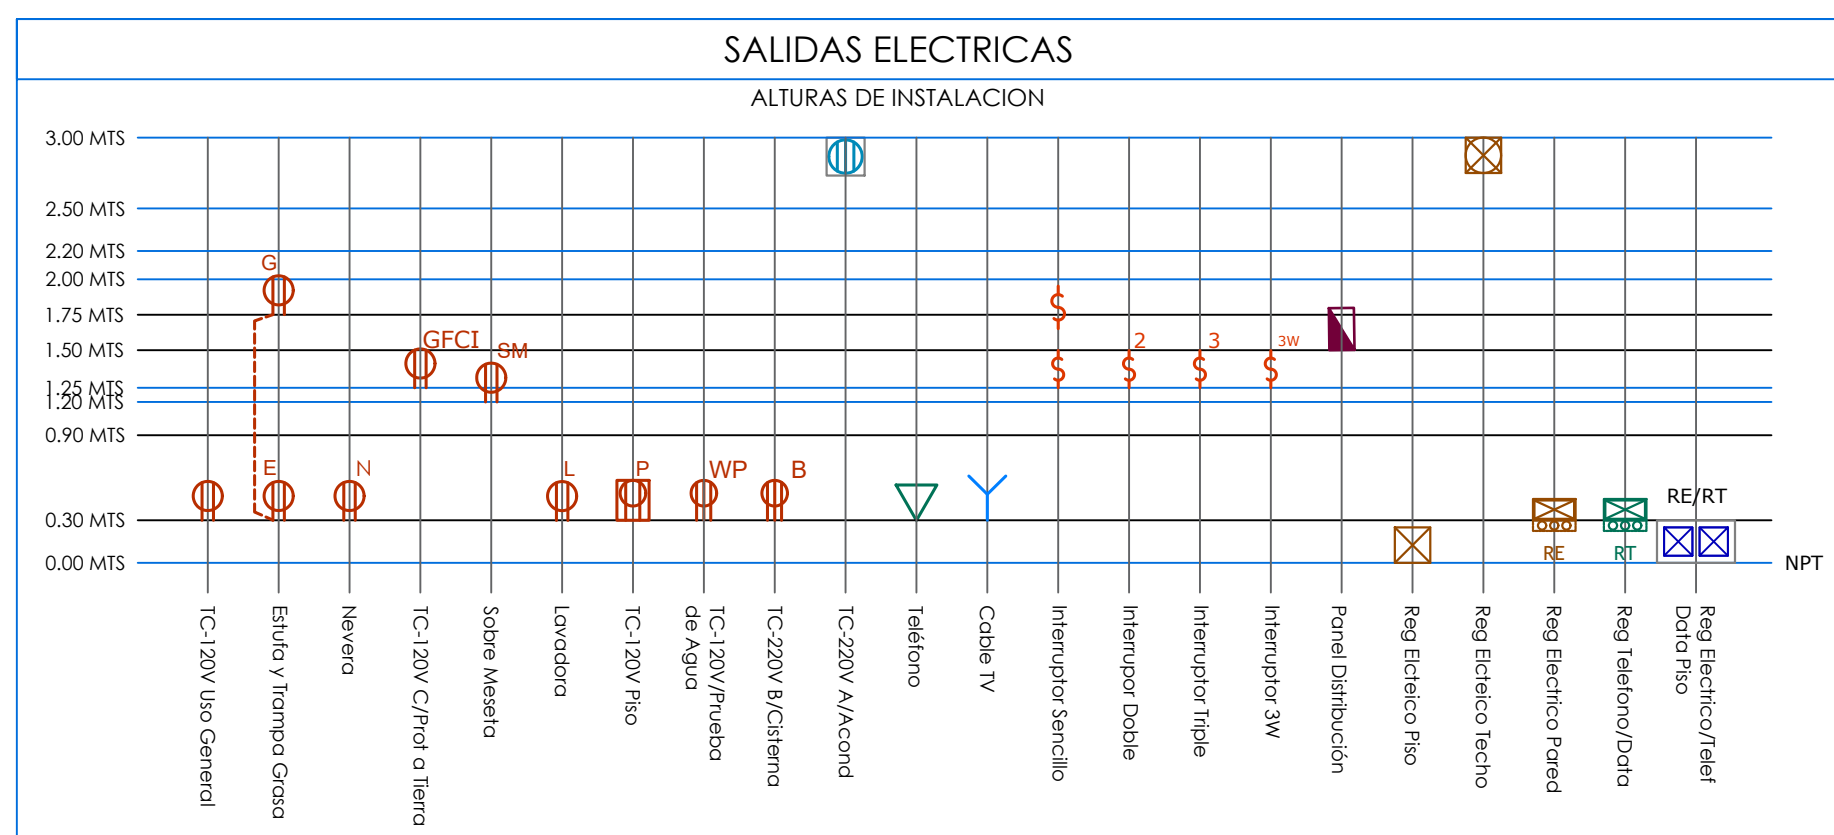

LEYENDA			
	SALIDA LUZ CENITAL		SALIDA TELEFONO
	SALIDA LUZ DE PARED		SALIDA CABLE TV
	SALIDA LUZ DE PARED EXTERIOR		CONTROL ABANICO
	SALIDA LUZ JARDIN		PUESTA A TIERRA
	SALIDA LUZ PISCINA		TUBERIA EMPOTRADA EN LOSA
	SALIDA INTERRUPTOR SENCILLO		TUBERIA EMPOTRADA EN PISO
	SALIDA INTERRUPTOR DOBLE		TUBERIA TELEFONICA EMP EN PISO
	SALIDA INTERRUPTOR TRES VIAS		TUBERIA EMPOTRADA EN PISO
	SALIDA TC-110V USO GENERAL		PANEL DE DISTRIBUCION
	SALIDA NEVERA		PANEL BOARD
	SALIDA ESTUFA		MAIN BRAKER
	SALIDA TC-110V SOBRE MESETA		REGISTRO ELECTRICO
	SALIDA LAVADORA		REGISTRO TELEFONICO
	SALIDA SECADORA		
	SALIDA TC-220V A/ACond		
	SALIDA CALENTADOR		
	SALIDA TC-110V C/PROTECCION A TIERRA		



Galerías Puntacana 65
Puntacana Village
La Altagracia, República Dominicana
Tel: 809 831 0903
Cels: 809 350 1696 / 809 753 2262
E: desanglesabreuarquitectos@gmail.com

PROYECTO:

CASA ERNA
LAS NASAS 09

UBICACION:

LAS NASAS
PUNTACANA RESORT & CLUB

PROPIETARIO:

MR. JON KNAPP
MRS. MELISSA RACITI

FIRMA:

DISEÑO ARQ:

ARQ. MARIO E. DESANGLES
CODIA: 12067

ARQ. JANET ABREU DESANGLES

COLABORACION: ARQ. LADDY Y. BERROA
ARQ. MARIA C. FABIAN

DISEÑO INTERIOR:

DISEÑO ESTRUCTURAL:

DISEÑO SANITARIO:

DISEÑO ELECTRICO:
ING. ONESIMO RIVERA
CODIA: 11027

RESPONSABLE DE OBRA:


DISCIPLINA: PLANOS ELECTRICOS

TIPOLOGIA: PLANTA DISTRIBUCION
ELECTRICA DE CONJUNTO


ESCALA:
1:100

Nº DE HOJA:
E-1.5

FECHA:
NOV 17 2025

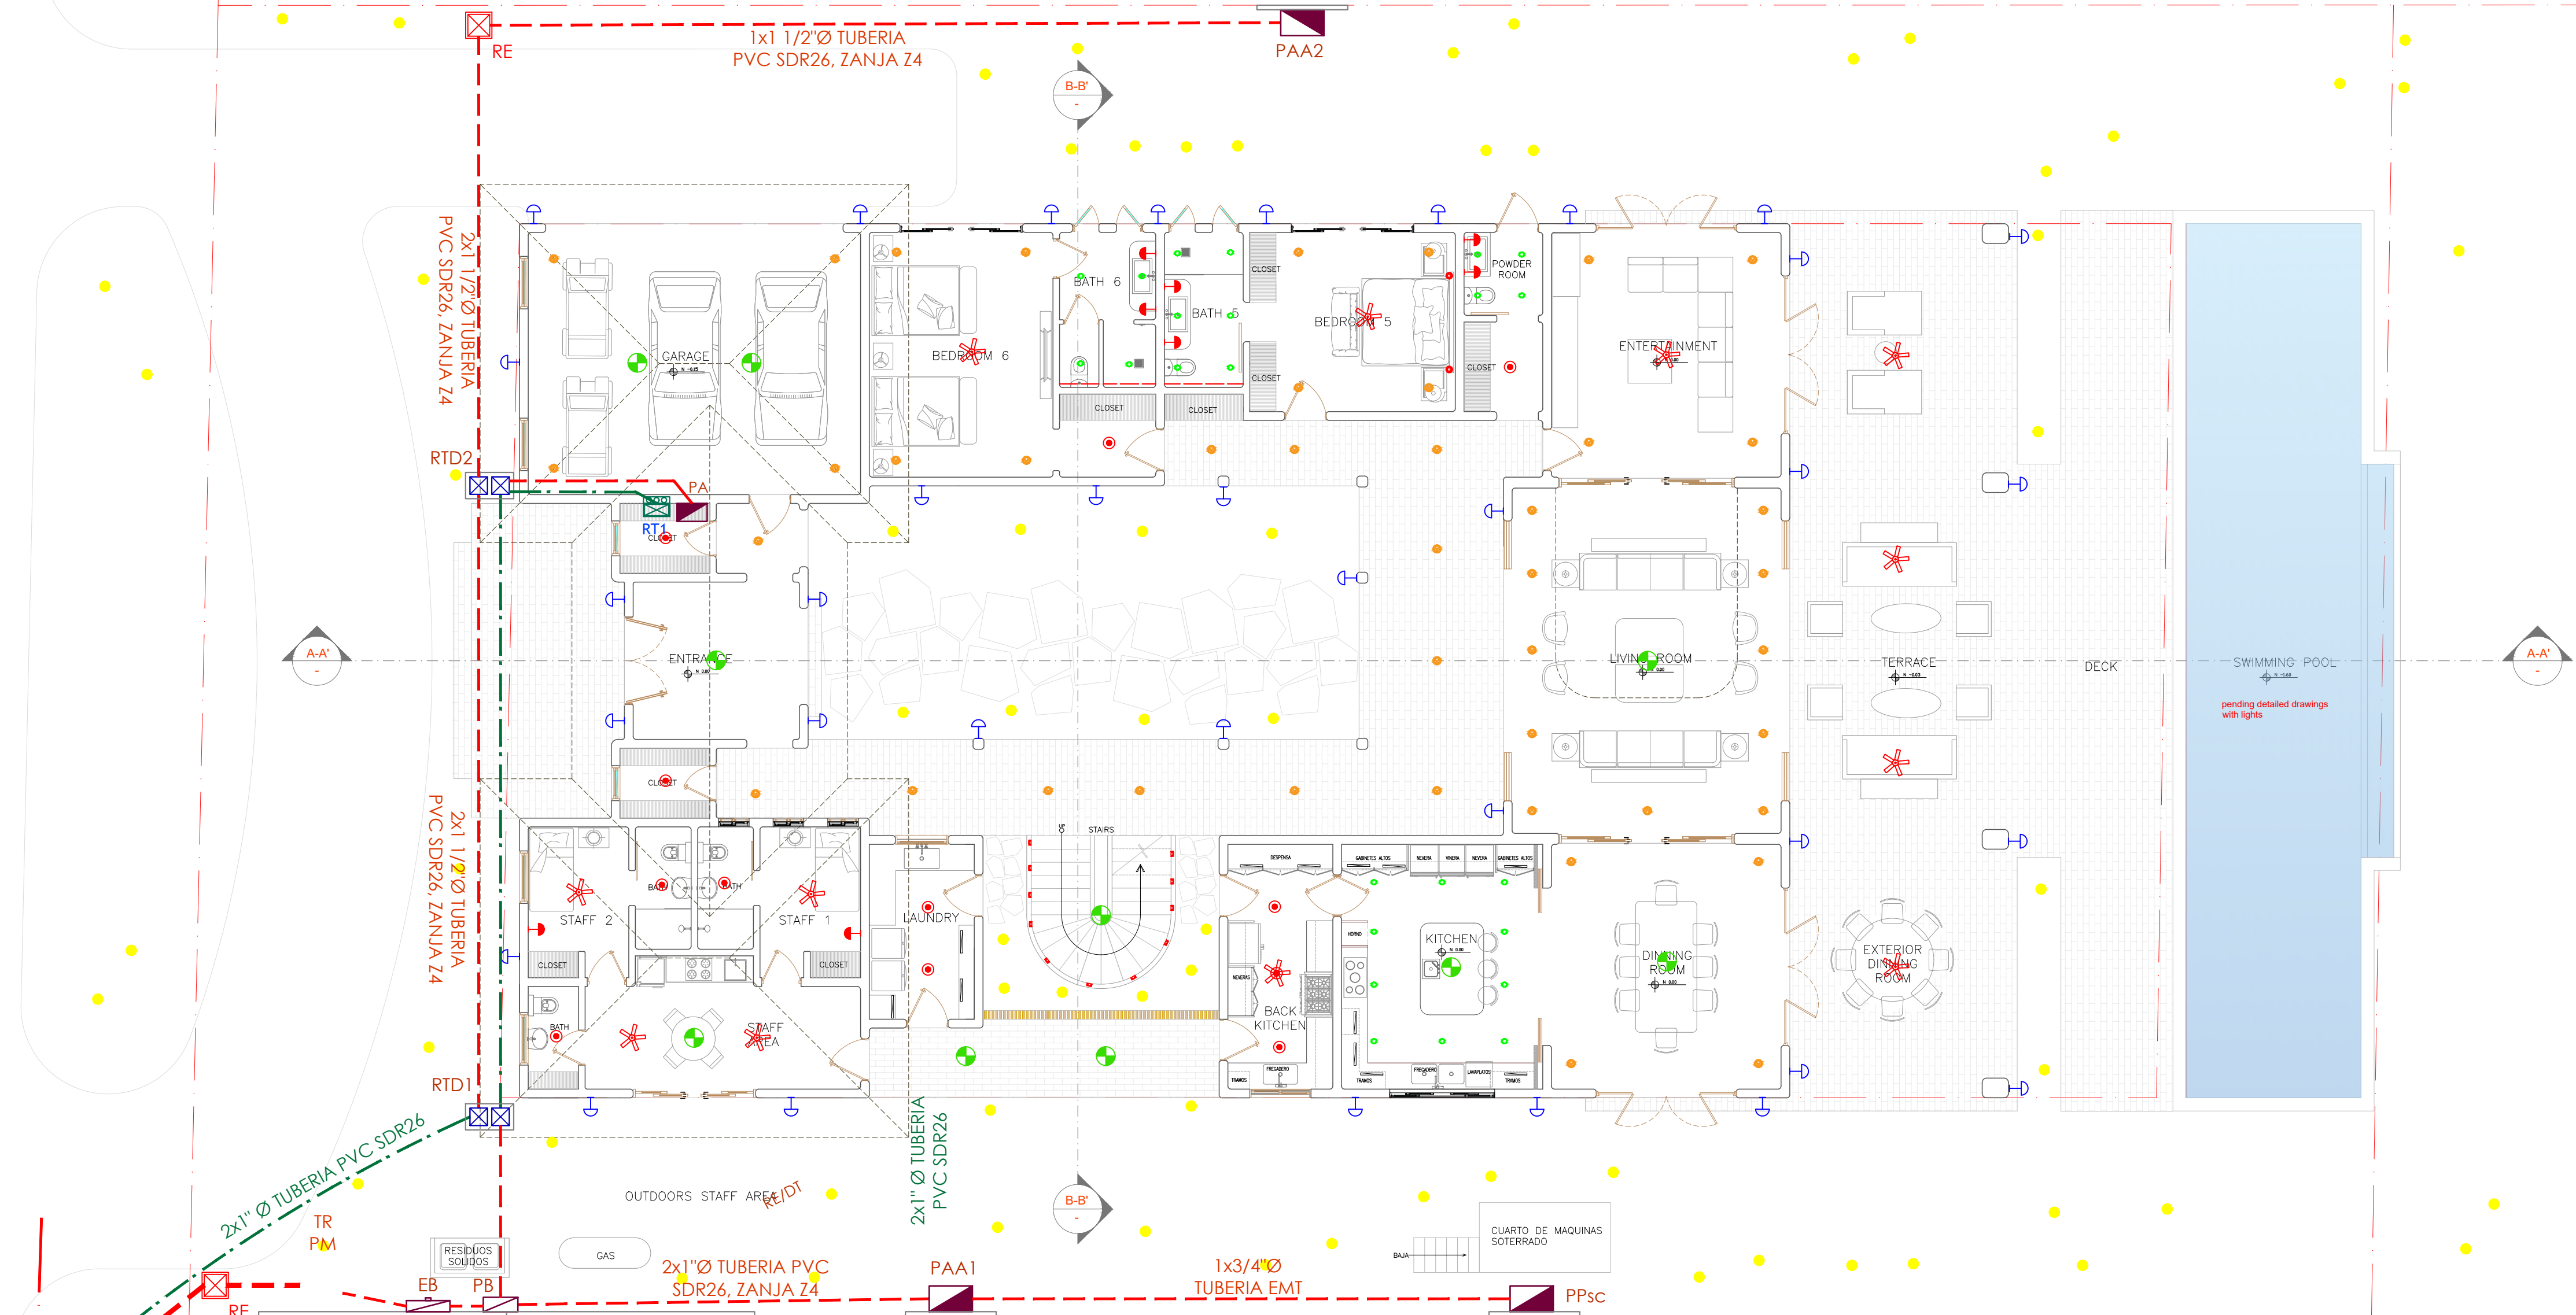





Leyenda Luminarios	
	Luminaria Empotrada Techo LED 120v 15W/25W/Dimming
	Luminaria Superficie Dimming
	Luminaria Empotrada de Techo 10w IP44 GU10 BLANCA Dimming
	Luminaria Panel para cuadros AI (según obra) Dimming
	Luminaria de Panel Exterior AI 1.80 rpt. 20W/120V Dimming
	Luminaria de Panel Interior 1.80 rpt. 10 in plan Decorativa, dimmerización según modelo
	Luminaria Semi-Superficie Dimming
	Luminaria De Piso - 12V transformador remoto Dimming
	Abanico de Techo
	Luminaria De Jardín
	Tira LED 24V, Driver Electronics, Dimming: EIV Corge según plano Colocación de acuerdo a diseño
	Salida para Luz Espejo
	Luminaria empotrada IP44, GU10 BLACK
	Luminaria Colgante Decorativa, ver especificaciones para cada una
	Luminaria Recessada retractable 7.5w Dimming
	Luminaria de Panel Empotrada
	Luminaria Lineal Superficie
	Rel Magnético 48V, Driver remoto
	Luminaria a especificar, Dimming DALI
	Luminaria Bajo Gabinete según diseño visible, ver especificación
	Luminaria Lectura o Cabañero Dimming
	Luminaria Recessada Exterior 10W
	Luminaria Superficie Técnica Decorativa
	Luminaria Superficie Técnica Decorativa

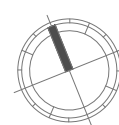


PLANTA DISTRIBUCION ELECTRICA CONJUNTO
ESC. 1:100

LEYENDA

	POSTE PROPUESTO
	PARARRAYOS KV
	SECCIONADOR FUSIBLE 100A
	DEVANADO TRANSFORMADOR
	TRANSFORMADOR T/PM
	MAIN BREAKER
	BASE DE CONTADOR
	PANEL DIST EMPOTRADO EN PARED
	PANEL BOARD
	CONEXION A TIERRA

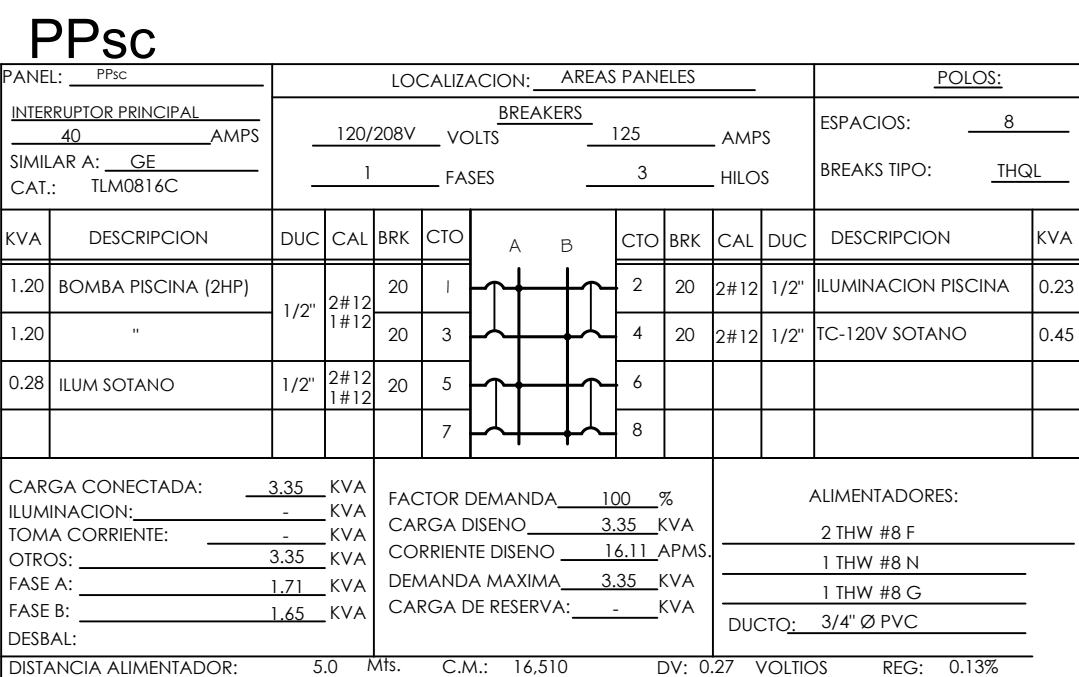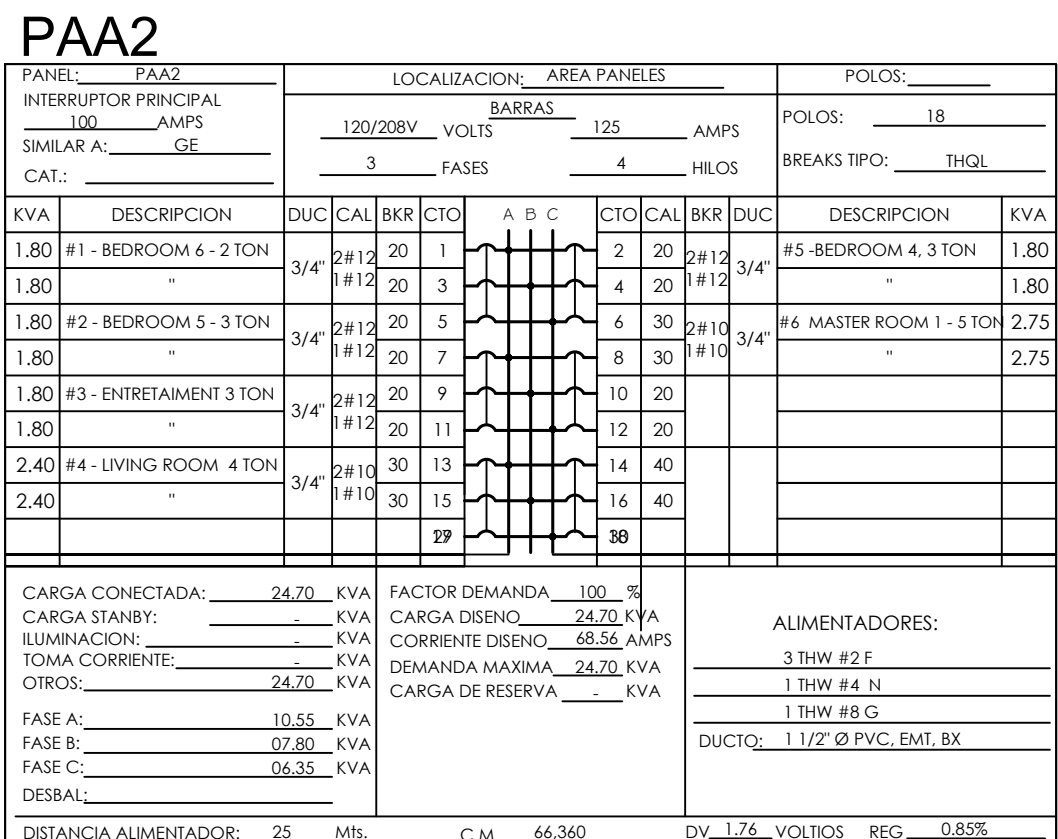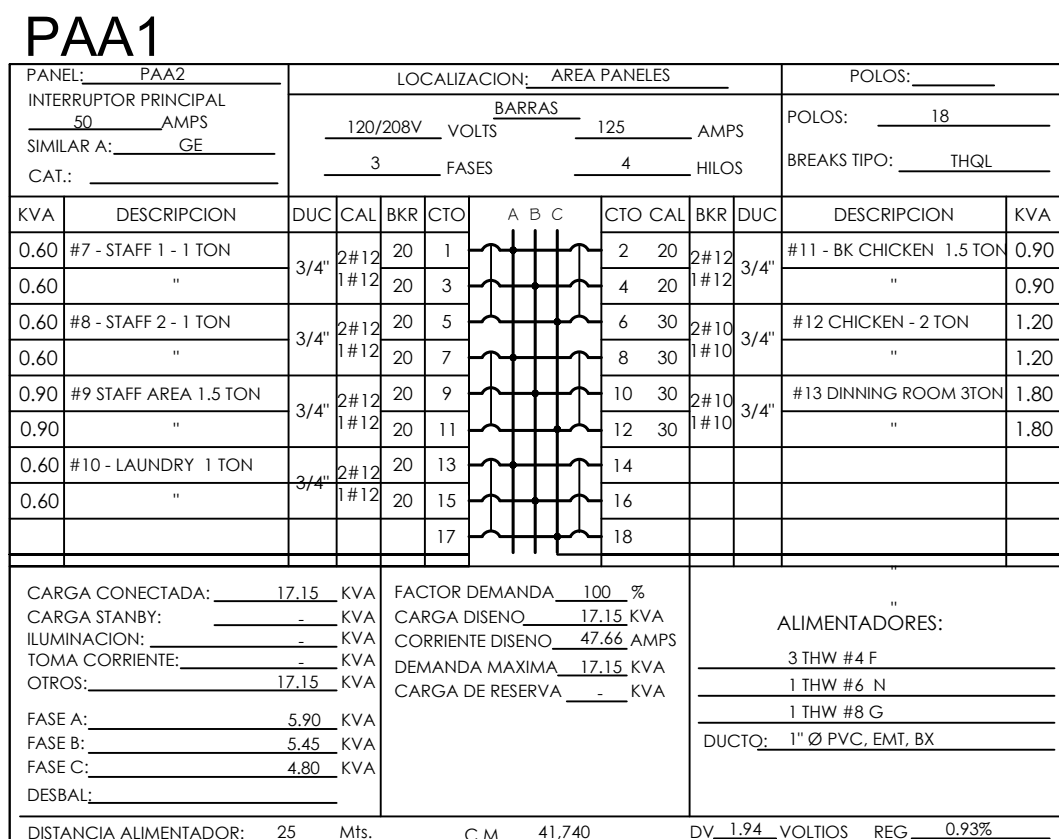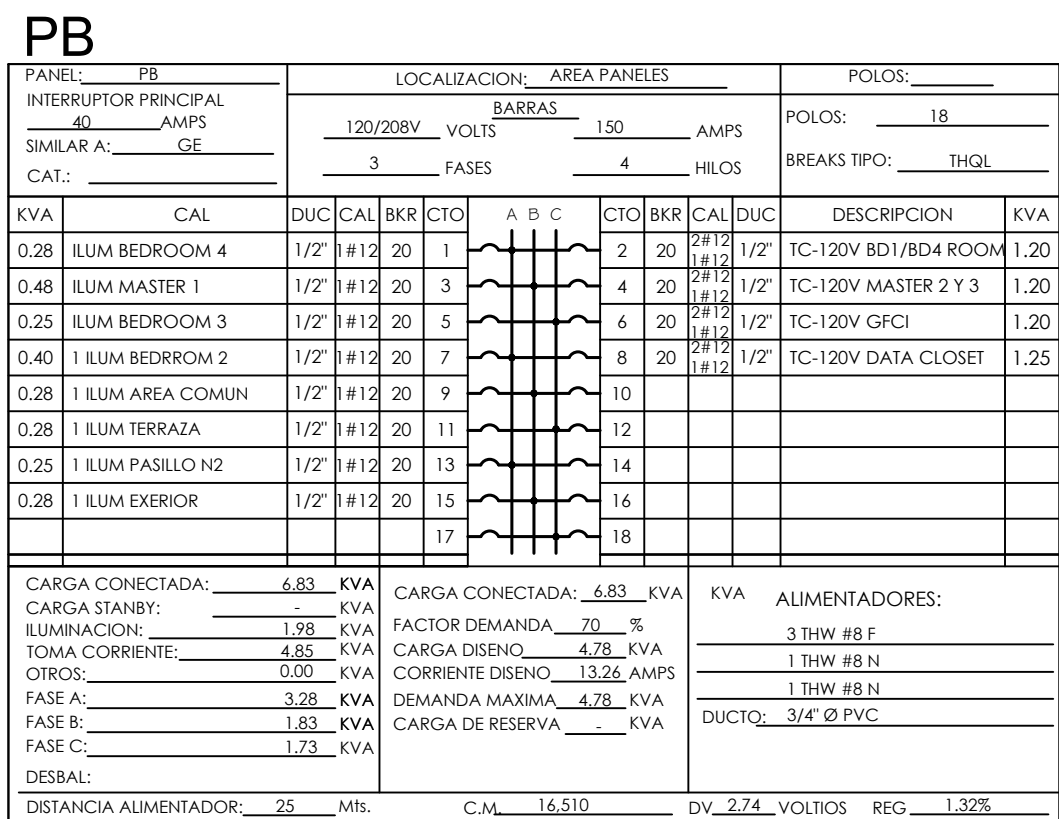

LEYENDA	
	POSTE PROPUESTO
	PARARRAYOS kV
	SECCIONADOR FUSIBLE 100A
	DEVANADO TRANSFORMADOR
	TRANSFORMADOR T/PM
	MAIN BREAKER
	BASE DE CONTADOR
	PANEL DIST EMPOTRADO EN PARED
	PANEL BOARD
	CONEXION A TIERRA

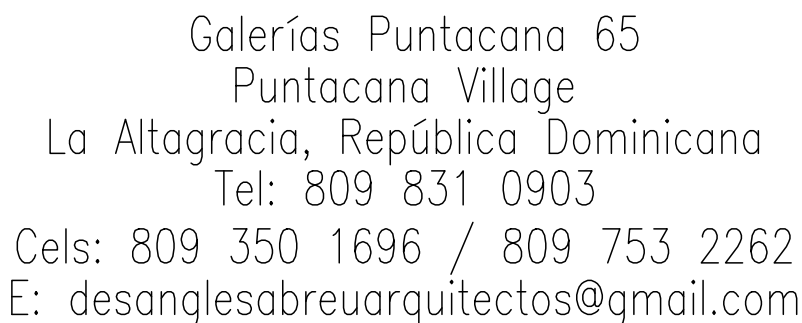

CASA ERNA
LAS NASAS 09

LAS NASAS
PUNTACANA RESORT & CLUB

MR. JON KNAPP
MRS. MELISSA RACITI

FIRMA:

ARQ. MARIO E. DESANGLES
CODIA: 12067

ARQ. JANET ABREU DESANGLES

COLABORACION: ARQ. LADDY Y. BERROA
ARQ. MARIA C. FABIAN

DISEÑO ELECTRICO:
ING. ONESIMO RIVERA
CODIA: 11027

RESPONSABLE DE OBRA:

DISCIPLINA: PLANOS ELÉCTRICOS

TIPOLOGIA: DIAGRAMA UNIFILAR Y PANELES

ESCALA:	Nº DE HOJA:	FECHA:
—	E-1.6	NOV 17 2025