



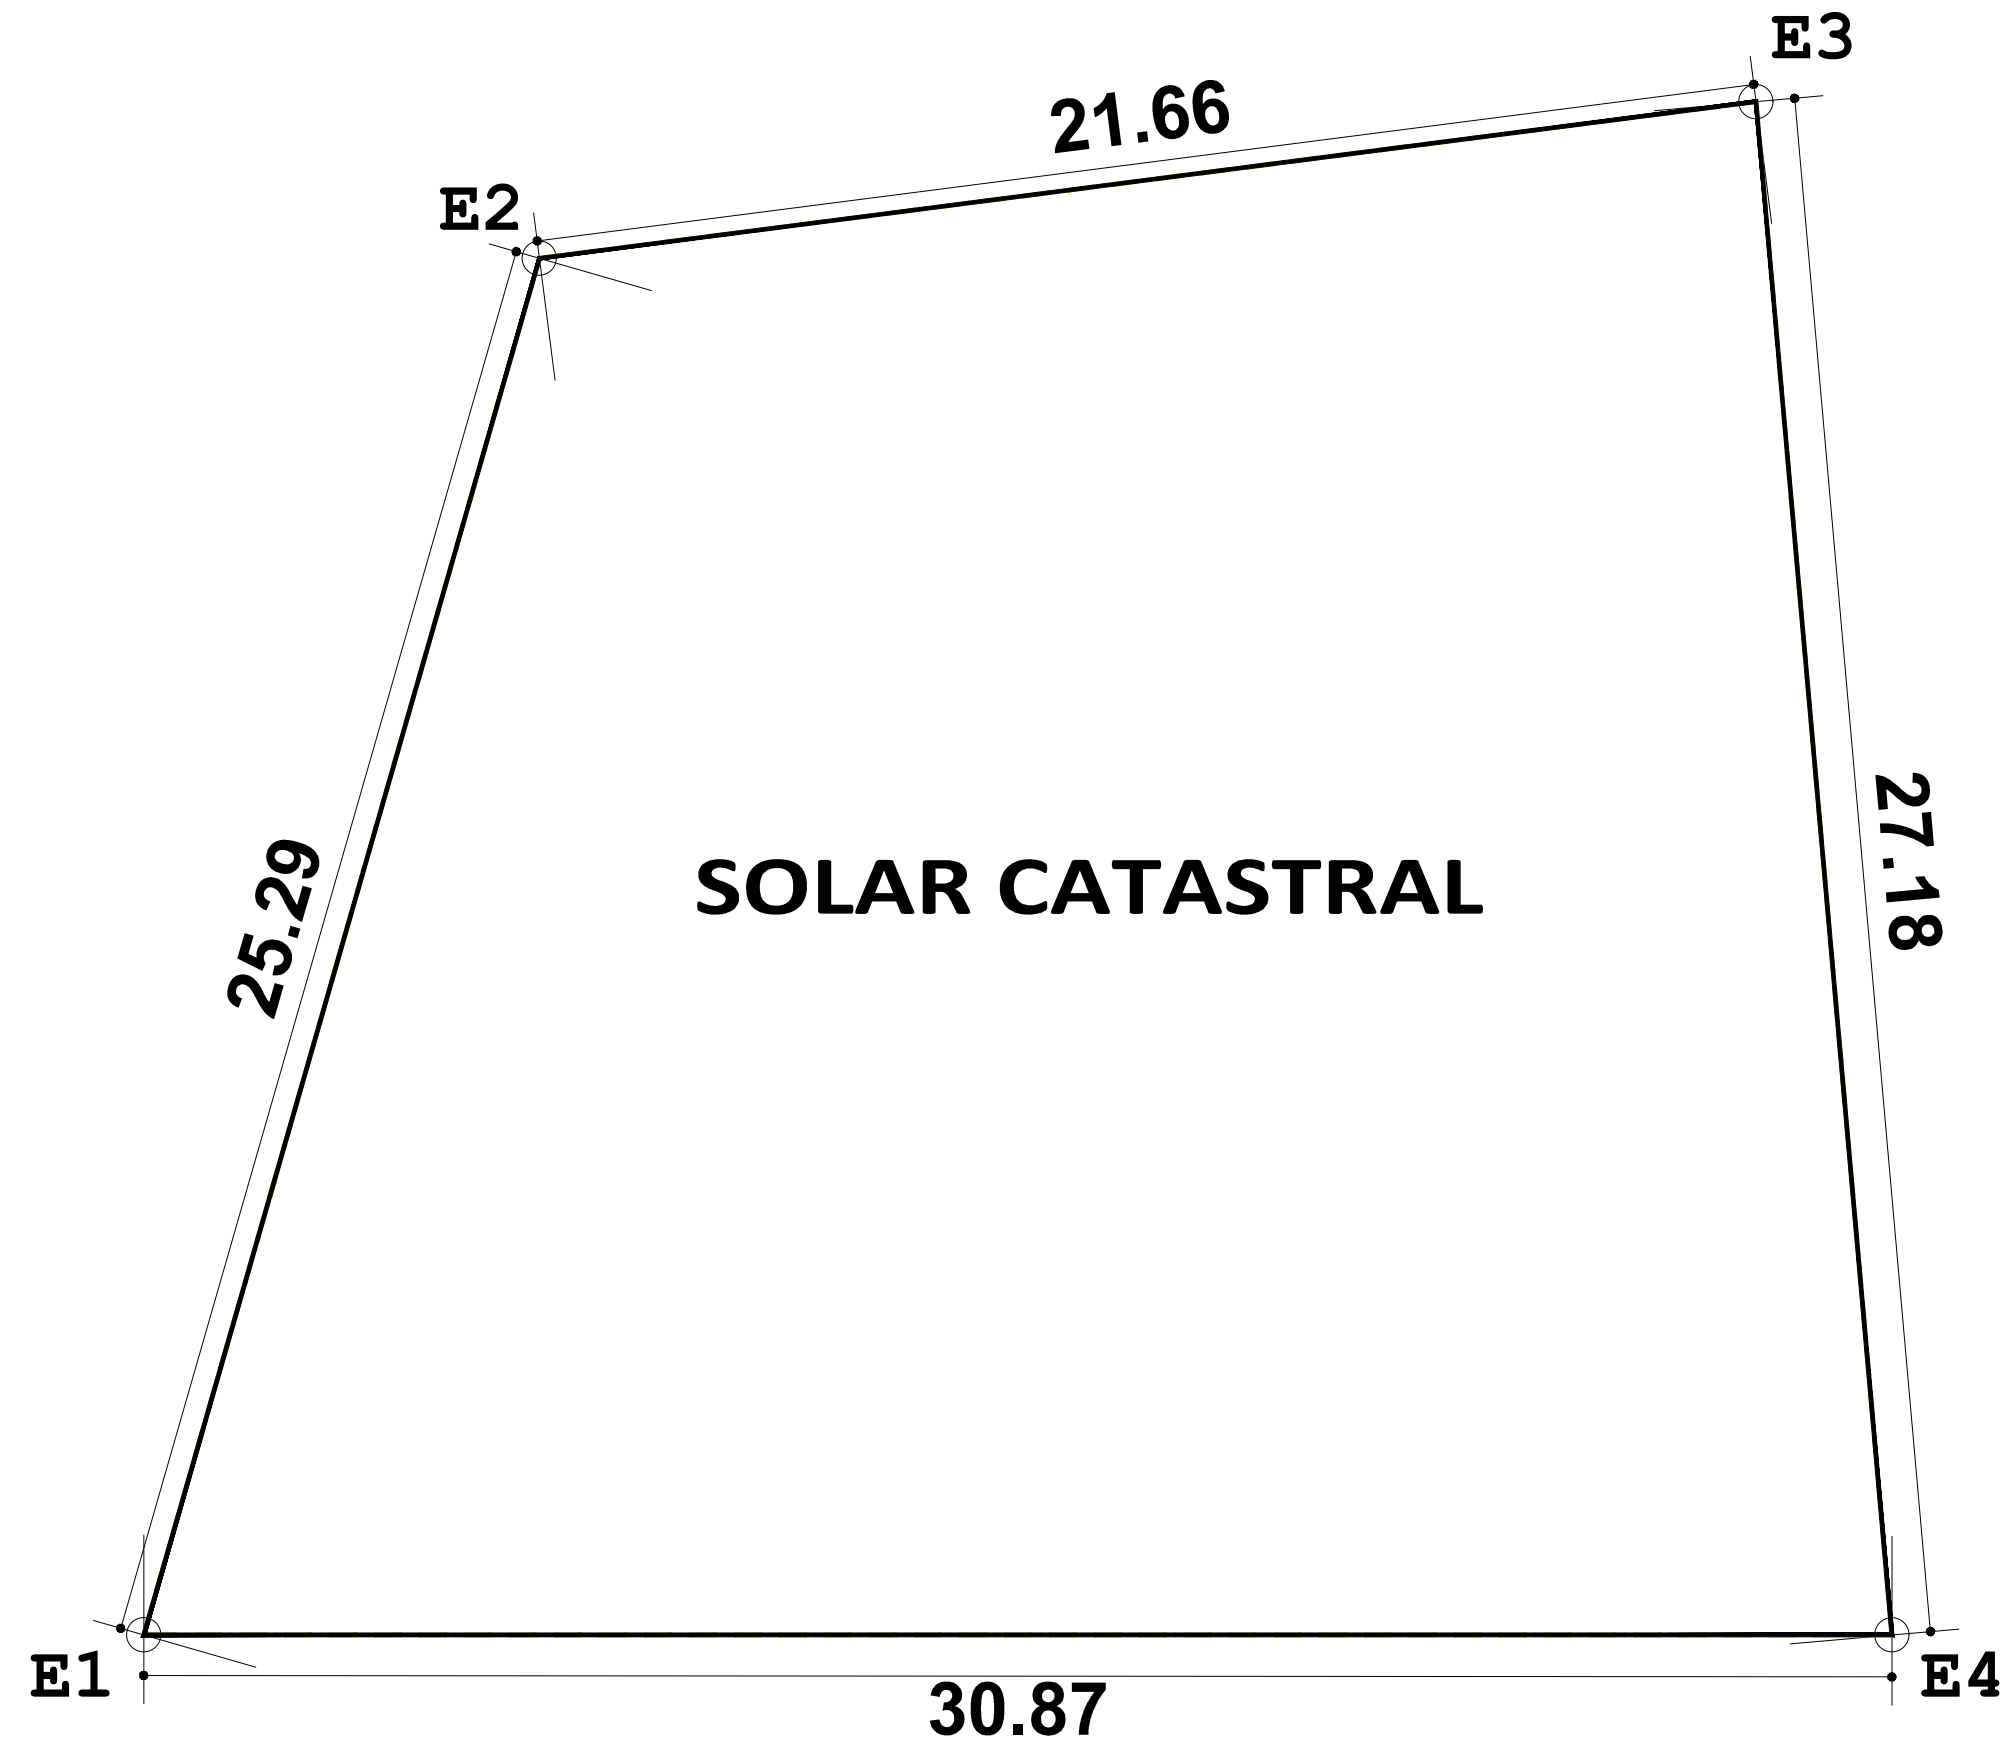

MENSURA CATASTRAL LEGAL

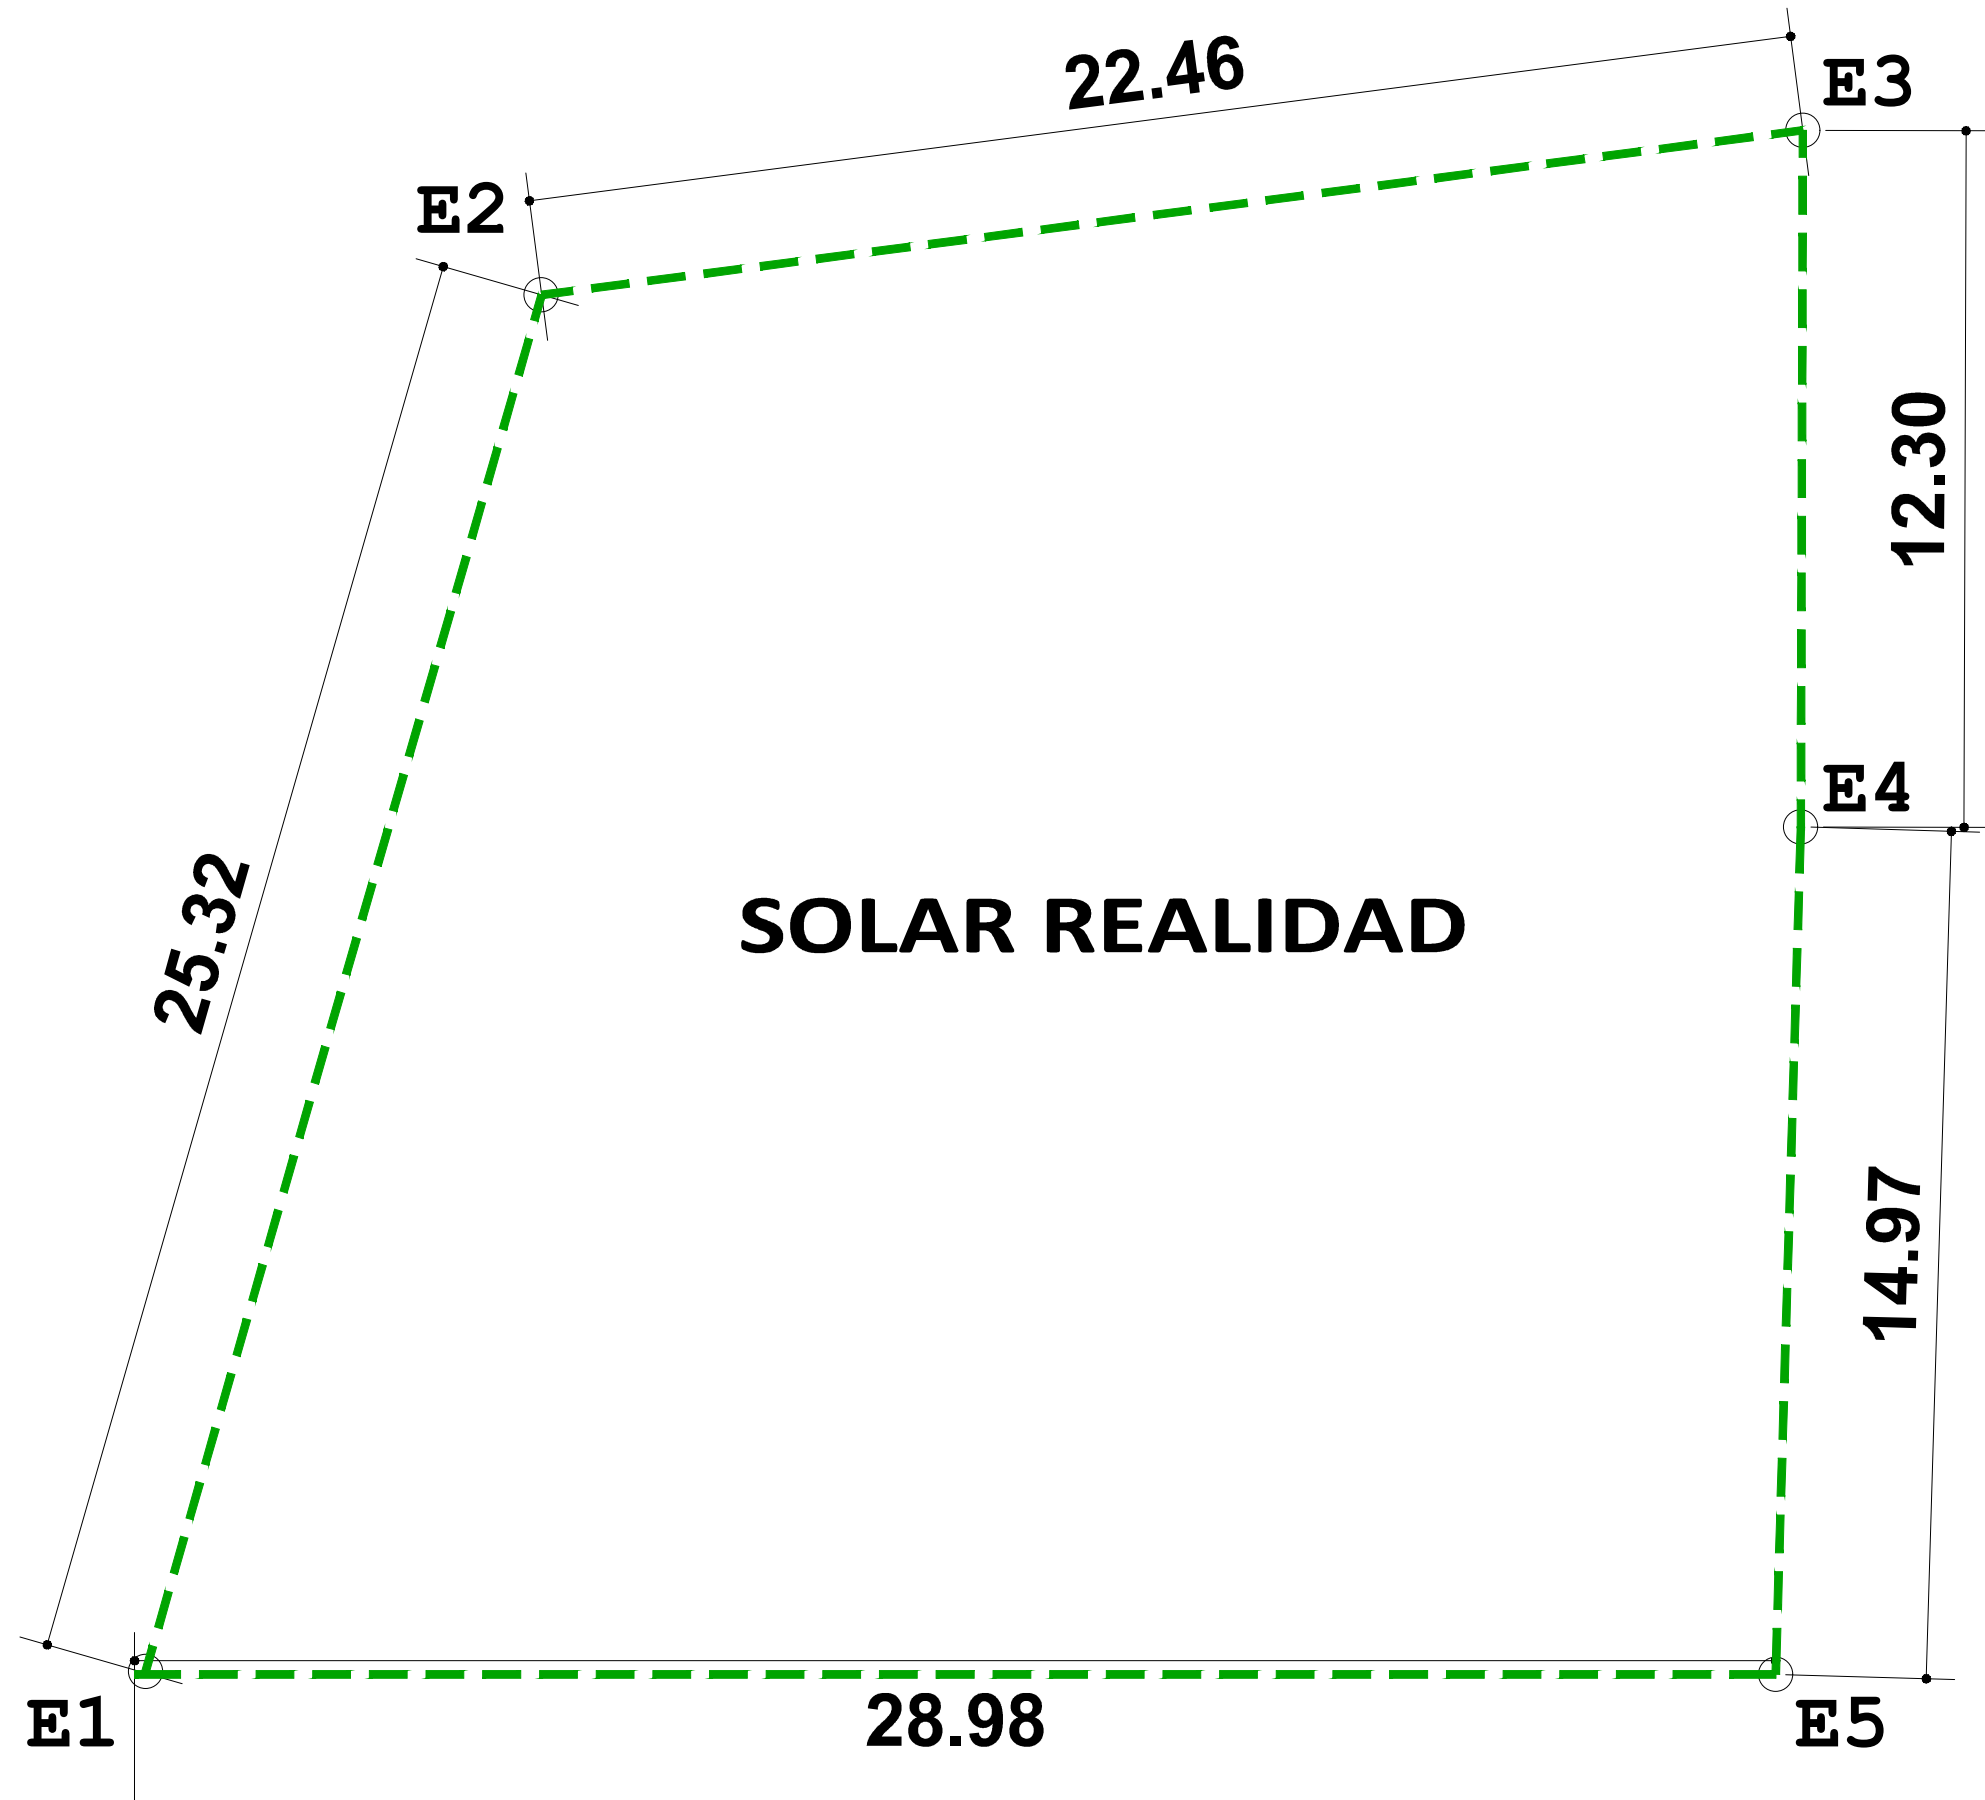


SOLAR REALIDAD


MENSURA DE LEVANTAMIENTO REAL

LEYENDA DE MENSURAS

- MENSURA LEGAL
- MENSURA REAL

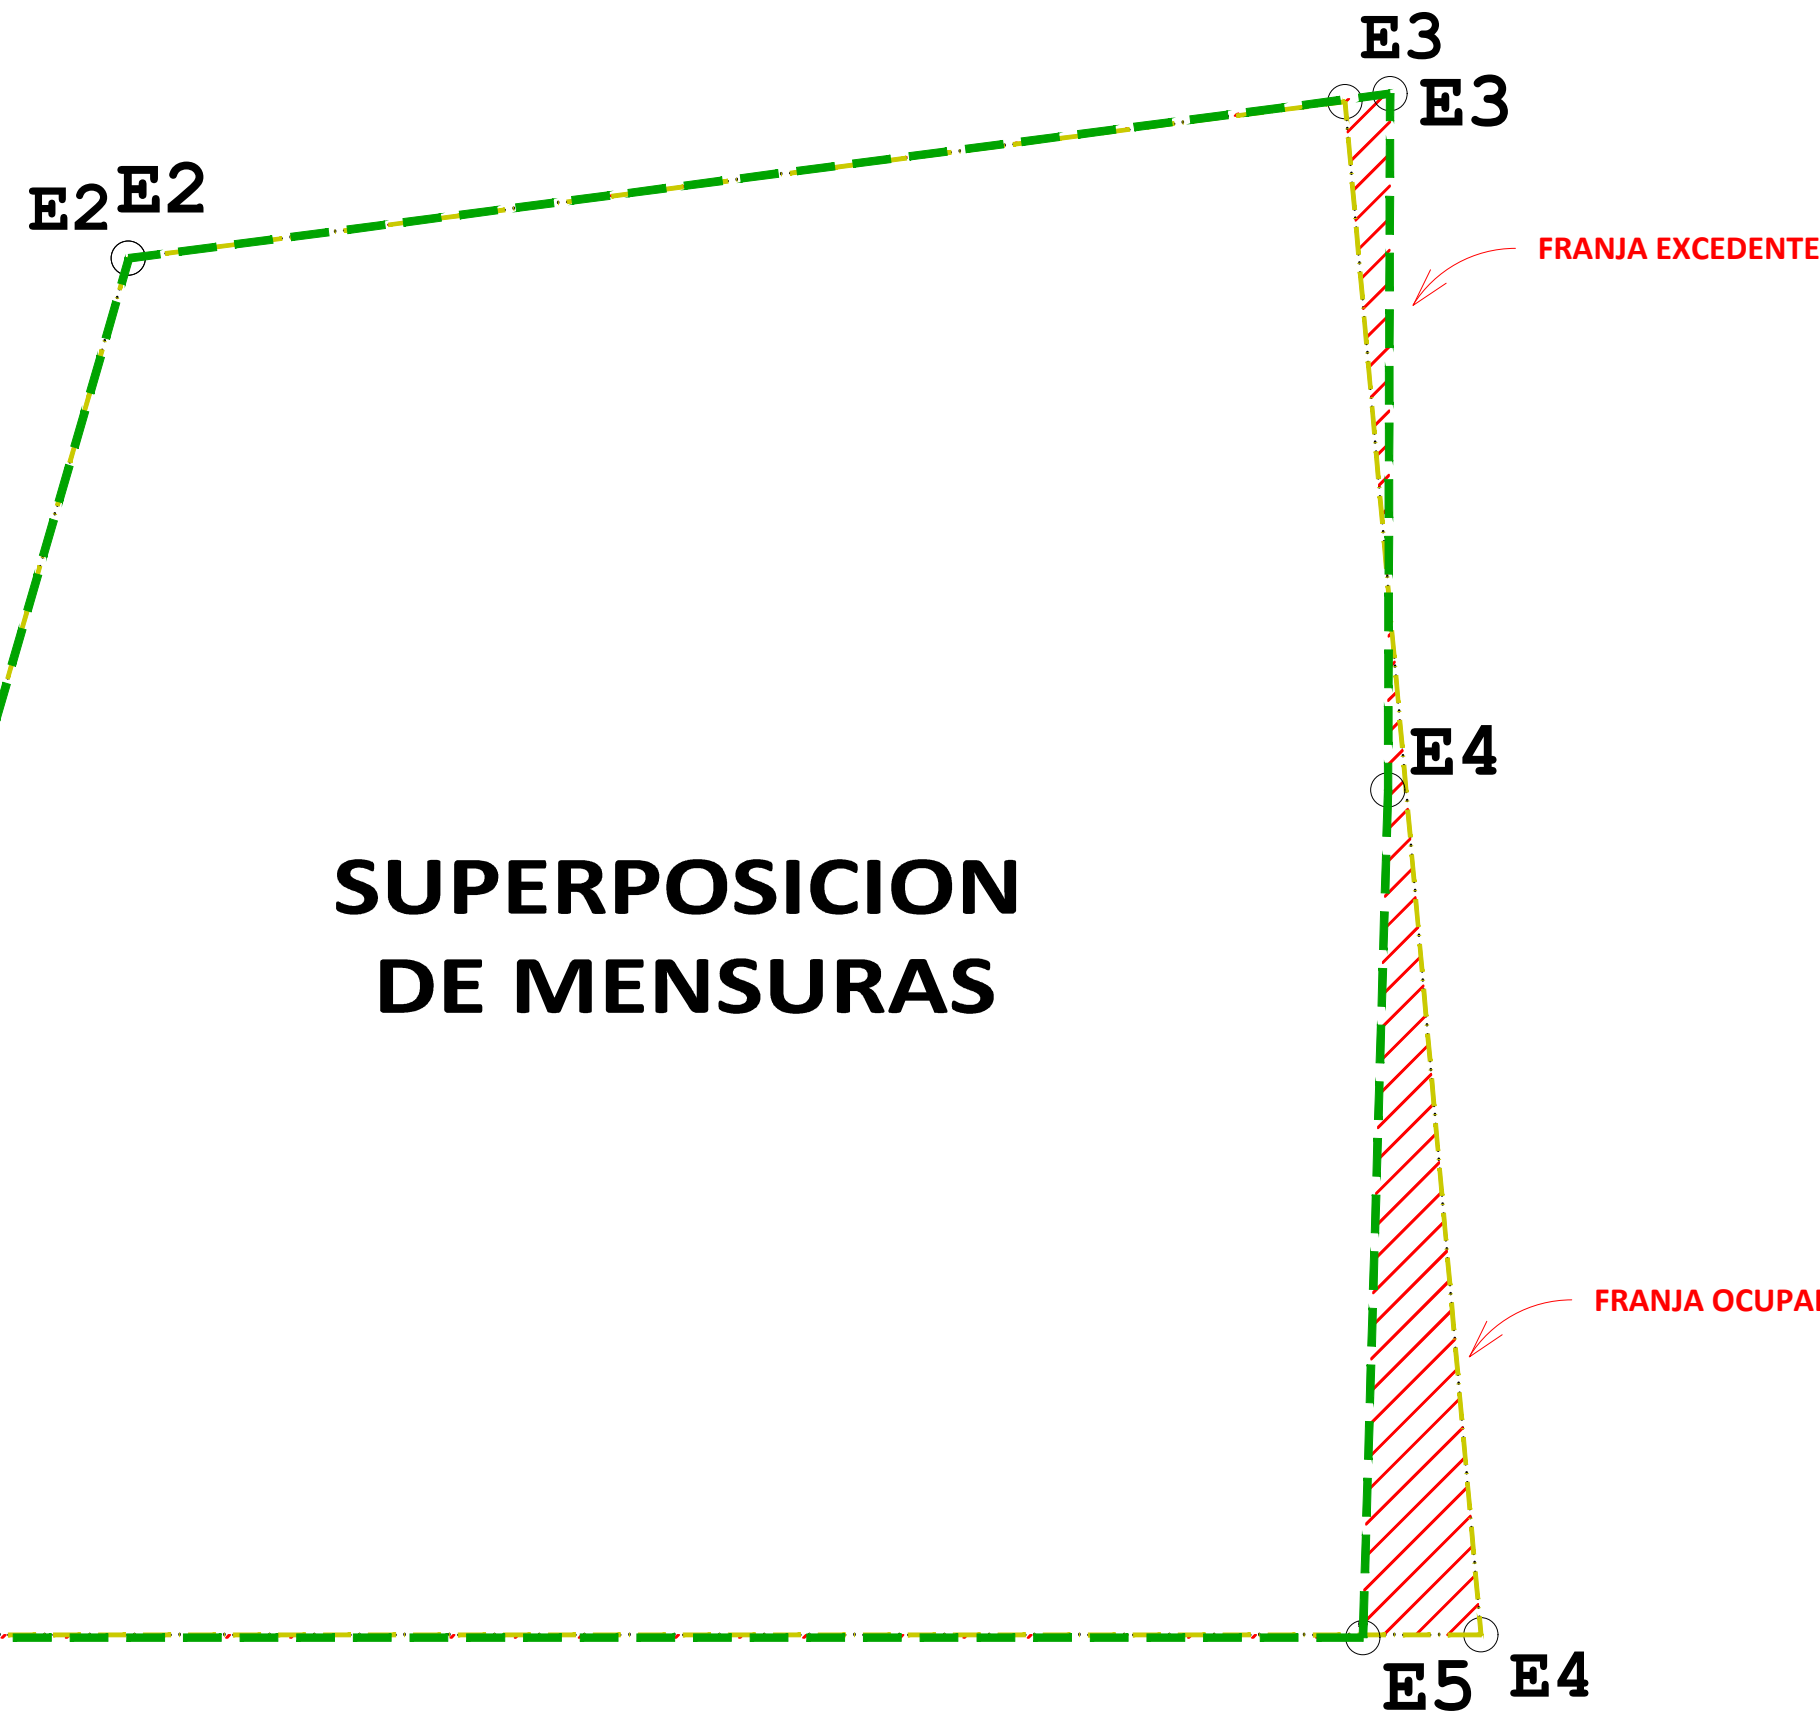


MENSURA CATASTRAL LEGAL + LEVANTAMIENTO REAL

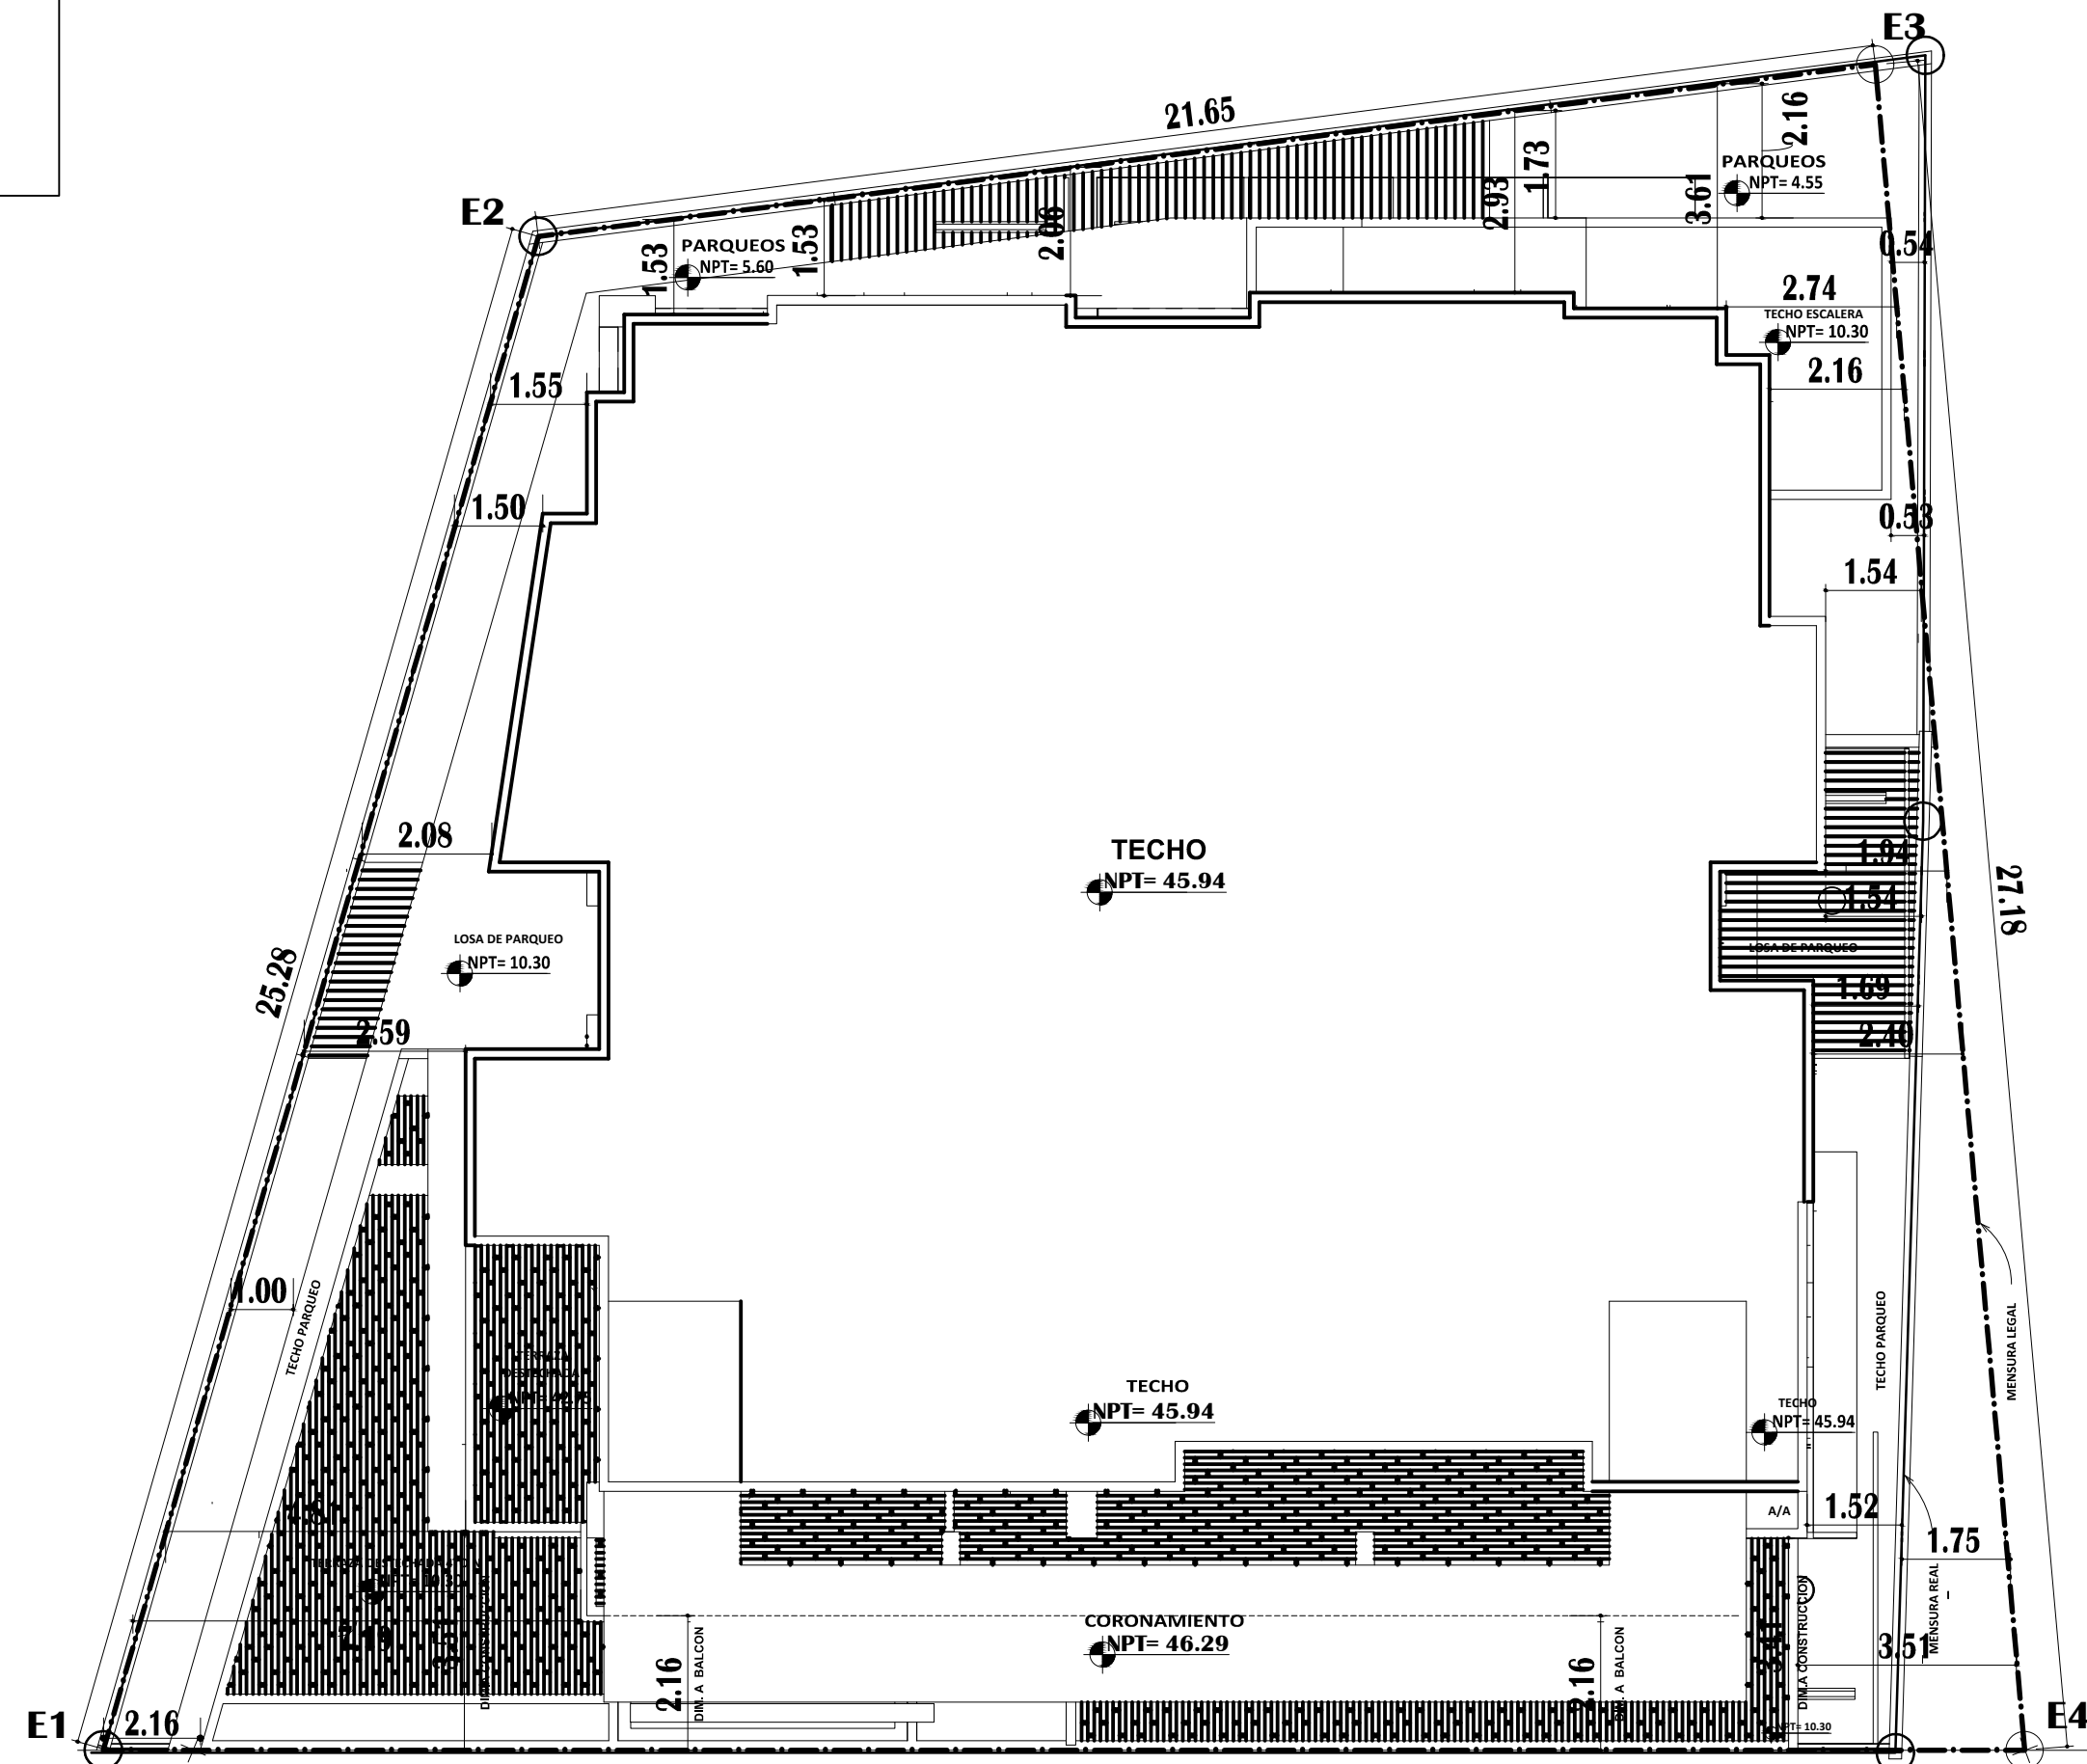


PLANTA DE SUPERPOSICION DE SOLARES CON LINDEROS

EST.	RUMBO	DIST.	COORDENADAS UTM:
1-	N 21°-28 E	25.28	18.479059,
2-	N 88°-06 E	21.66	-69.831177
3-	S 00°-22 W	27.18	
4-	N 84°-34 W	30.87	COORDENADAS GPS:
SOLAR= 669.17 M ²			18°28'44.6"N
			69°49'52.2"W

INDICE	
PLANO	NO
INDICE Y PORTADA	01
PLANTA ARQ. Y DIM. SEMI SOTANO	02
PLANTA ARQ. Y DIM. NIVEL 1	03
PLANTA ARQ. Y DIM. NIVEL 2	04
PLANTA ARQ. Y DIM. NIVEL 3	05
PLANTA ARQ. Y DIM. NIVEL 4	06
PLANTA ARQ. Y DIM. NIVELES TIPO 5-8	07
PLANTA ARQ. Y DIM. NIVELES TIPO 9-12	08
PLANTA ARQ. Y DIM. NIVEL 13 TIPO PH	09
PLANTA ARQ. Y DIM. NIVEL 14 TIPO PH Y A.S.	10
PLANTA ARQ. Y DIM. TECHO	11
ELEVACION FRONTAL Y LATERAL DER.	12
ELEVACION POSTERIOR Y LATERAL IZQ.	13
SECCIONES L1 Y T1	14
DETALLE DE ESCALERA	15


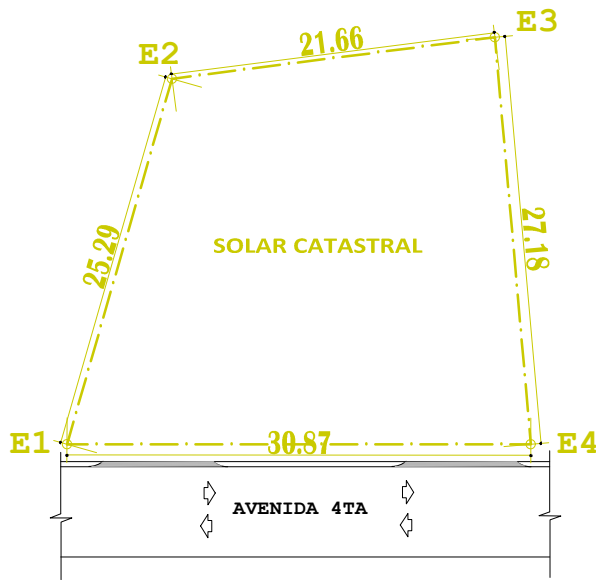


NPT .	
NIVEL	NPT
Semi Sotano	-1.40
Nivel 1	0.00
Nivel 2	3.05
Nivel 3	5.60
Nivel 4	10.30
Nivel 5	13.54
Nivel 6	16.78
Nivel 7	20.02
Nivel 8	23.26
Nivel 9	26.50
Nivel 10	29.74
Nivel 11	32.98
Nivel 12	36.22
Nivel 13	39.46
Nivel 14	42.70
Techo	45.94

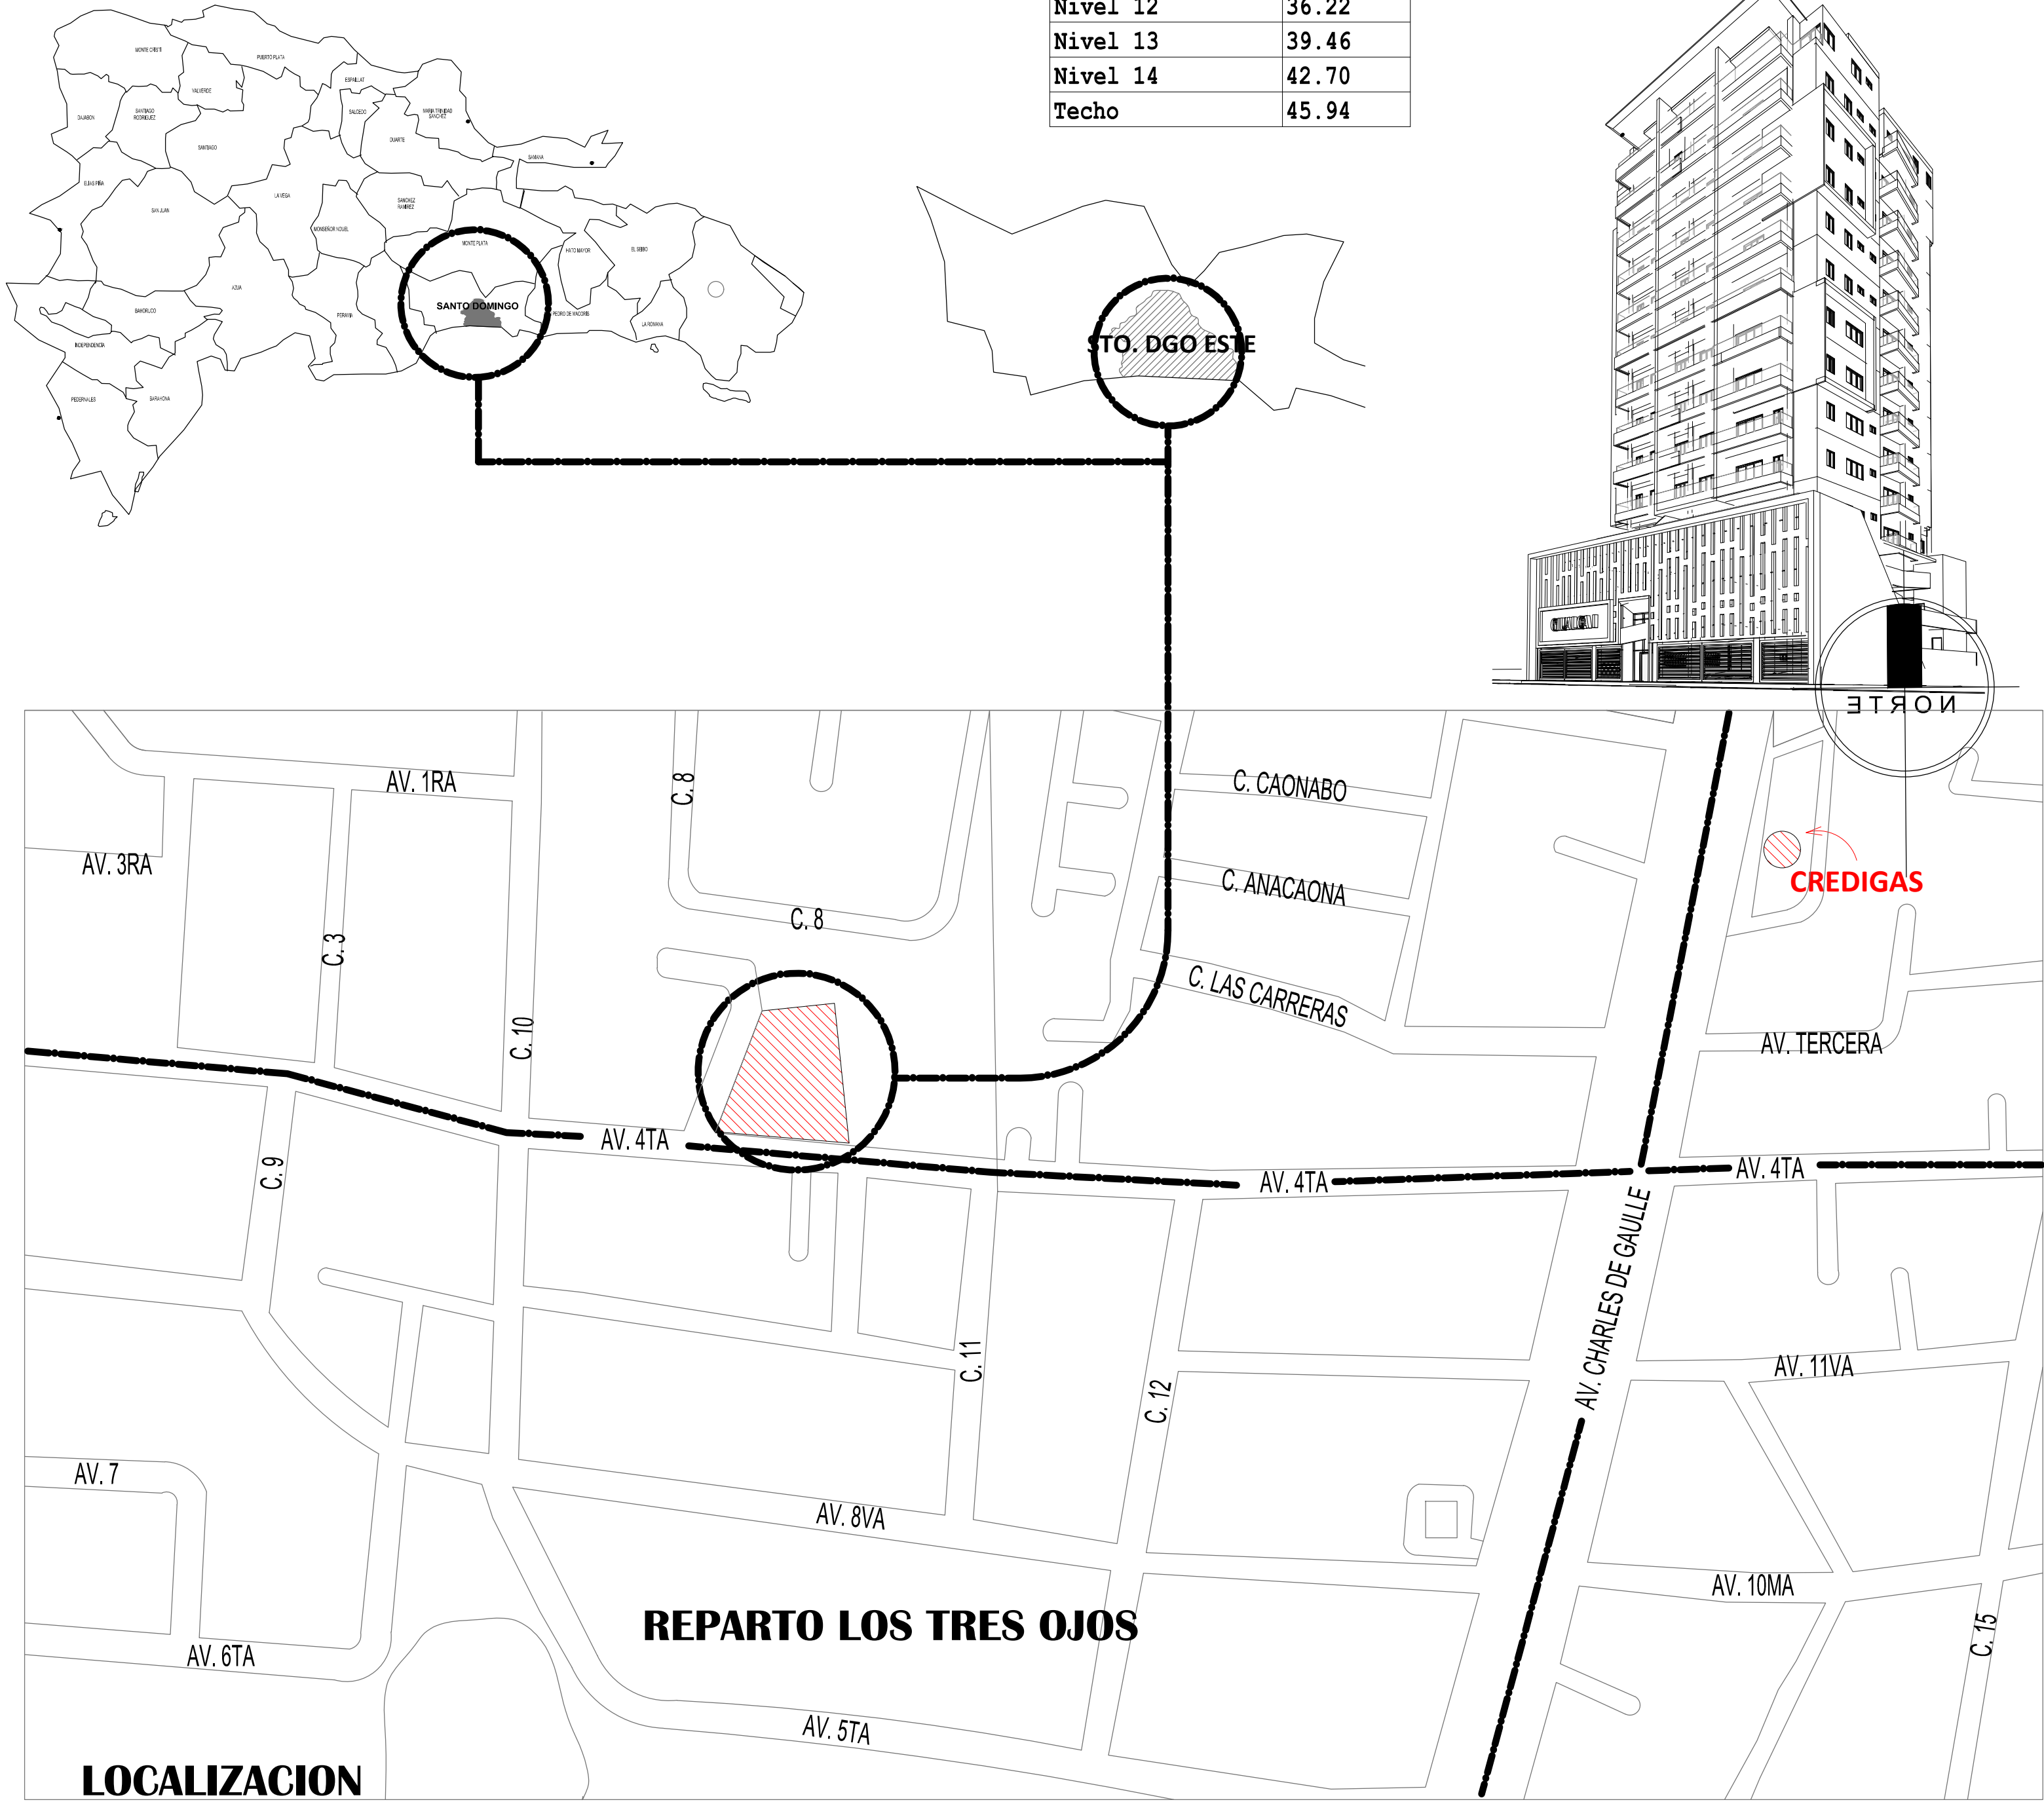

LOCALIZACION

SIN ESCALA

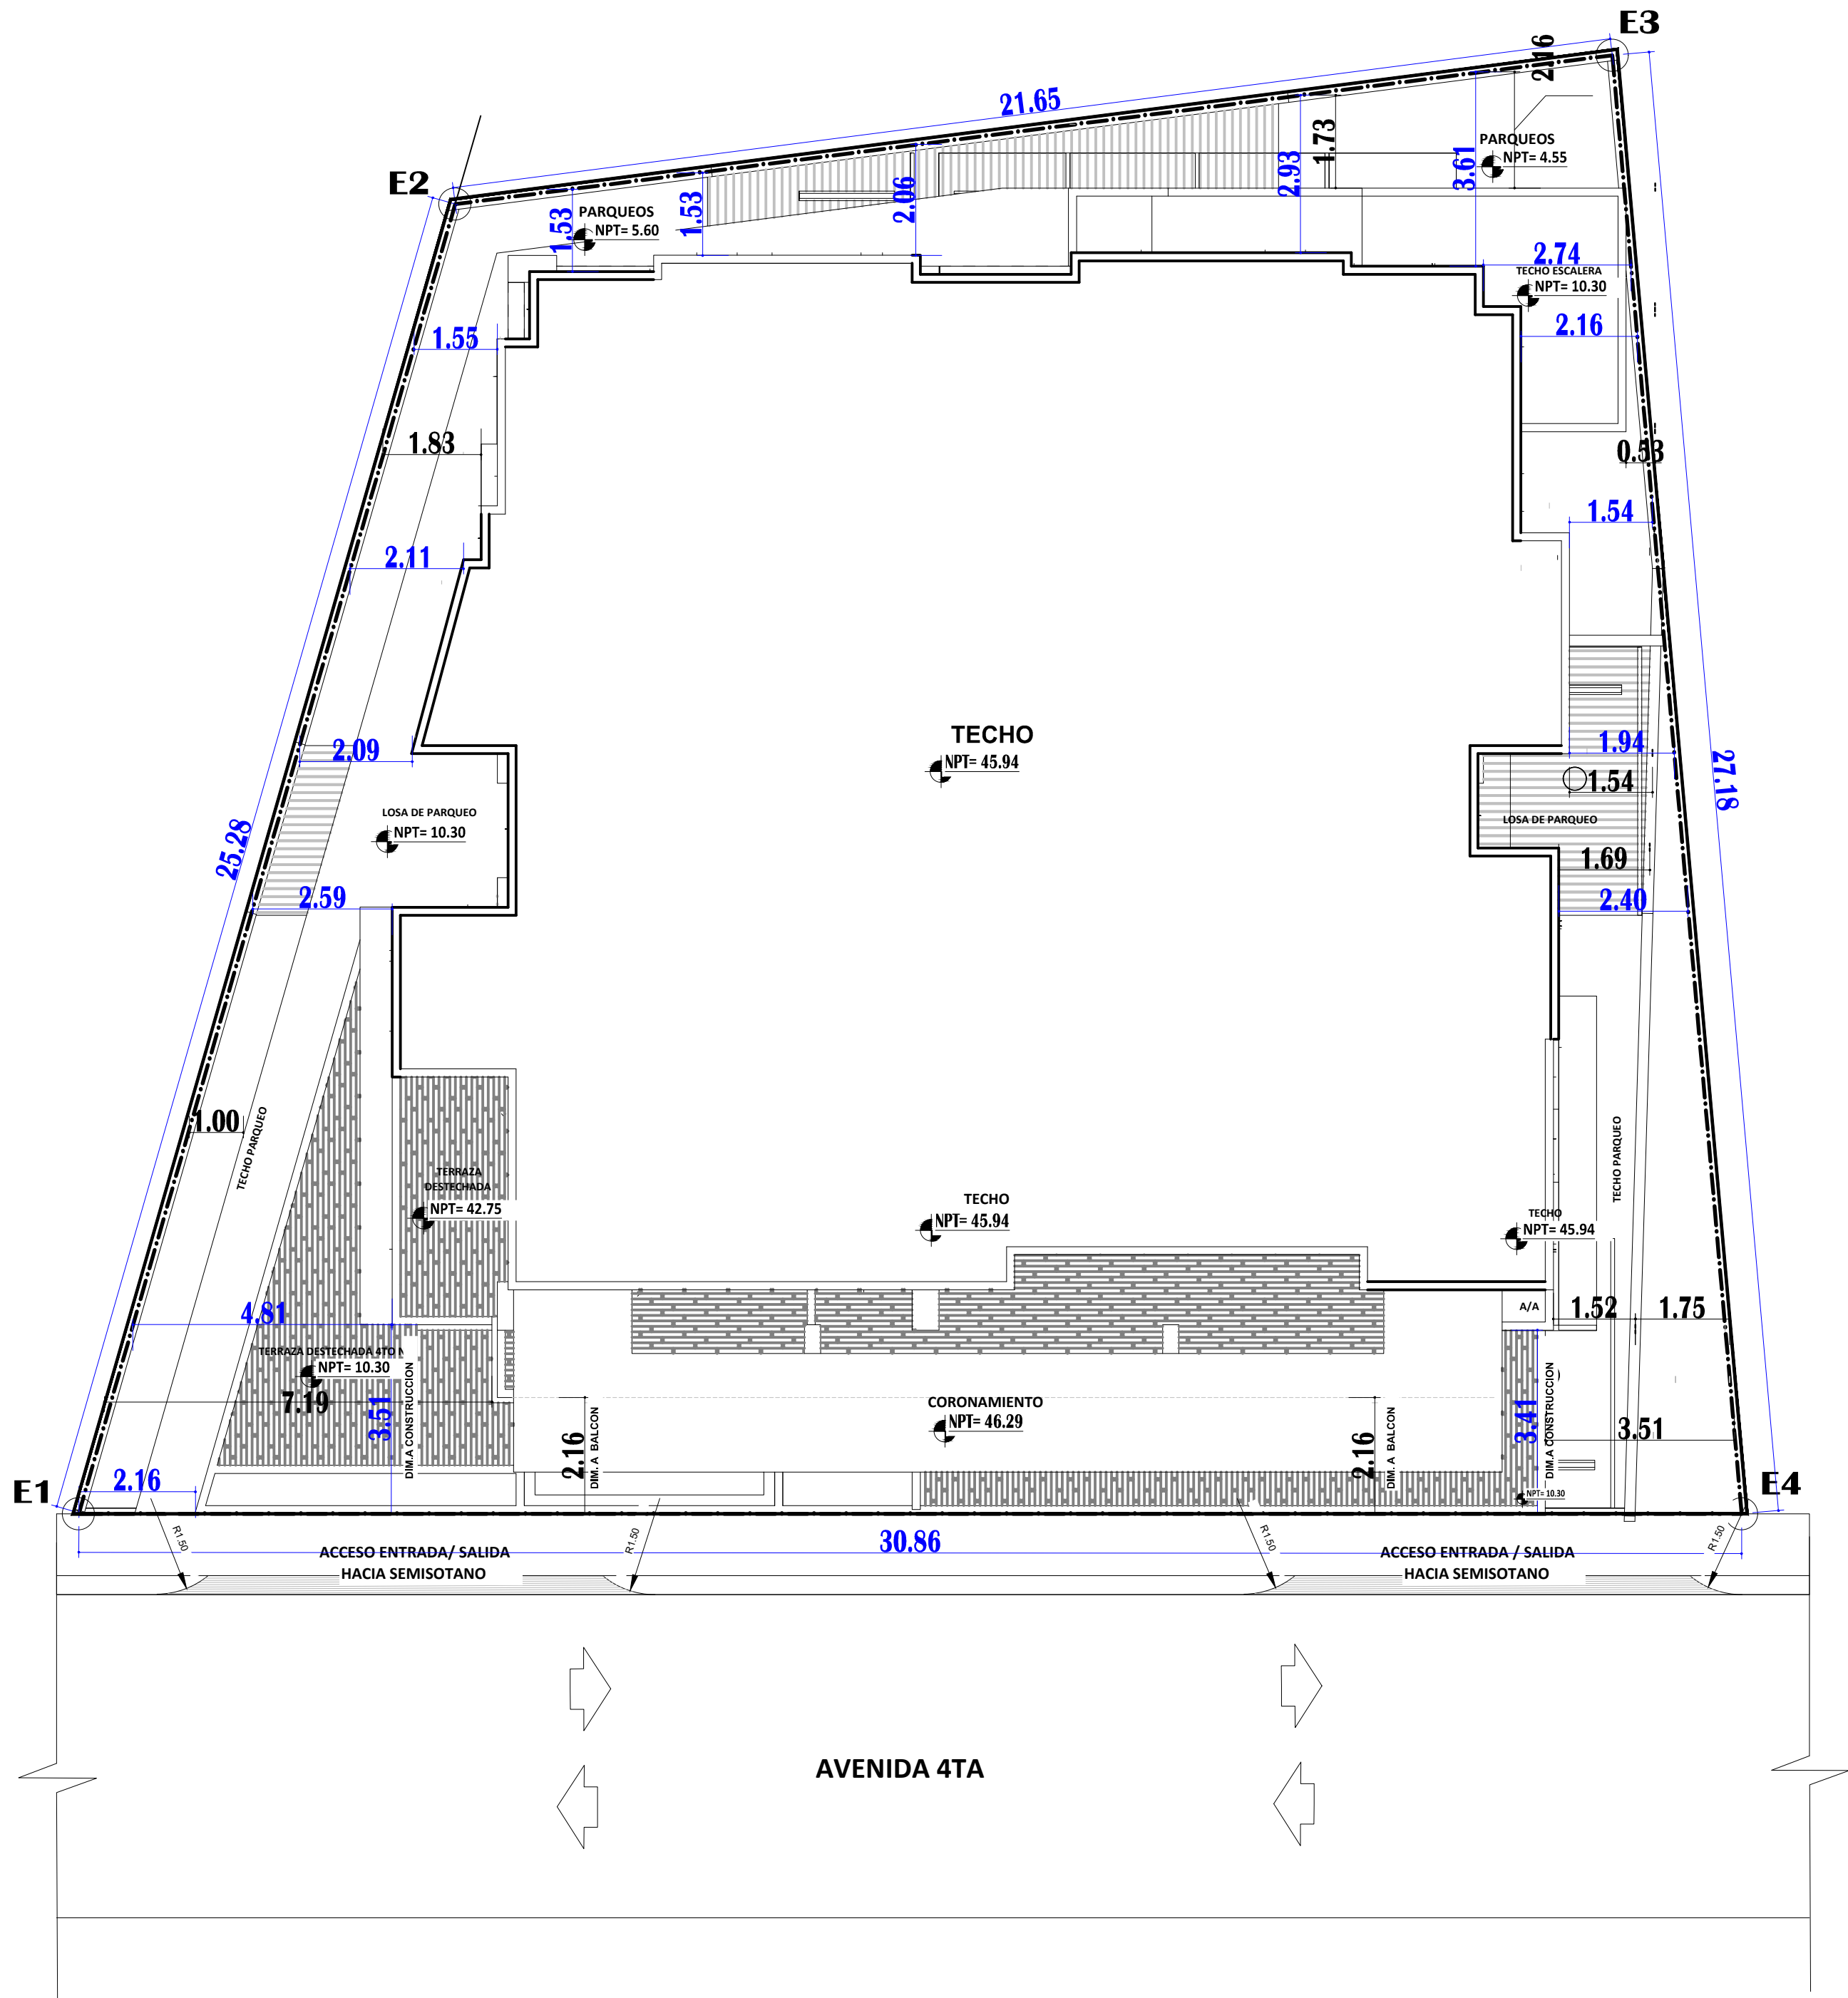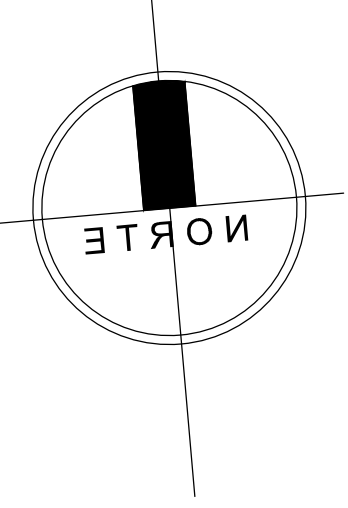

LEYENDA DIMENSIONES	
	DIMENSION RAMPAS
	DIMENSION GENERAL
	DIMENSION GENERAL DE LINDERO.
	DIMENSION A ELEM. ESTRUCTURALES

PLANTA DE UBICACION Y LINDEROS

ESCALA 1:100




PROPIETARIO
NEW AGE RD, SRL
1-32-61711-8



OBREGO ARQUITECTONICO
AXIOMA
ARQUITECTOS
ARQUITECTO: OBREGO N. 825-885-6001

NOMBRE DEL PROYECTO
TORRE GUALCA I

ARQUITECTONICO
ING. YESICA M. RAMIREZ DE JESUS
CODAL: 38584

EXP. AX-25-02
FEBRERO 2025
01

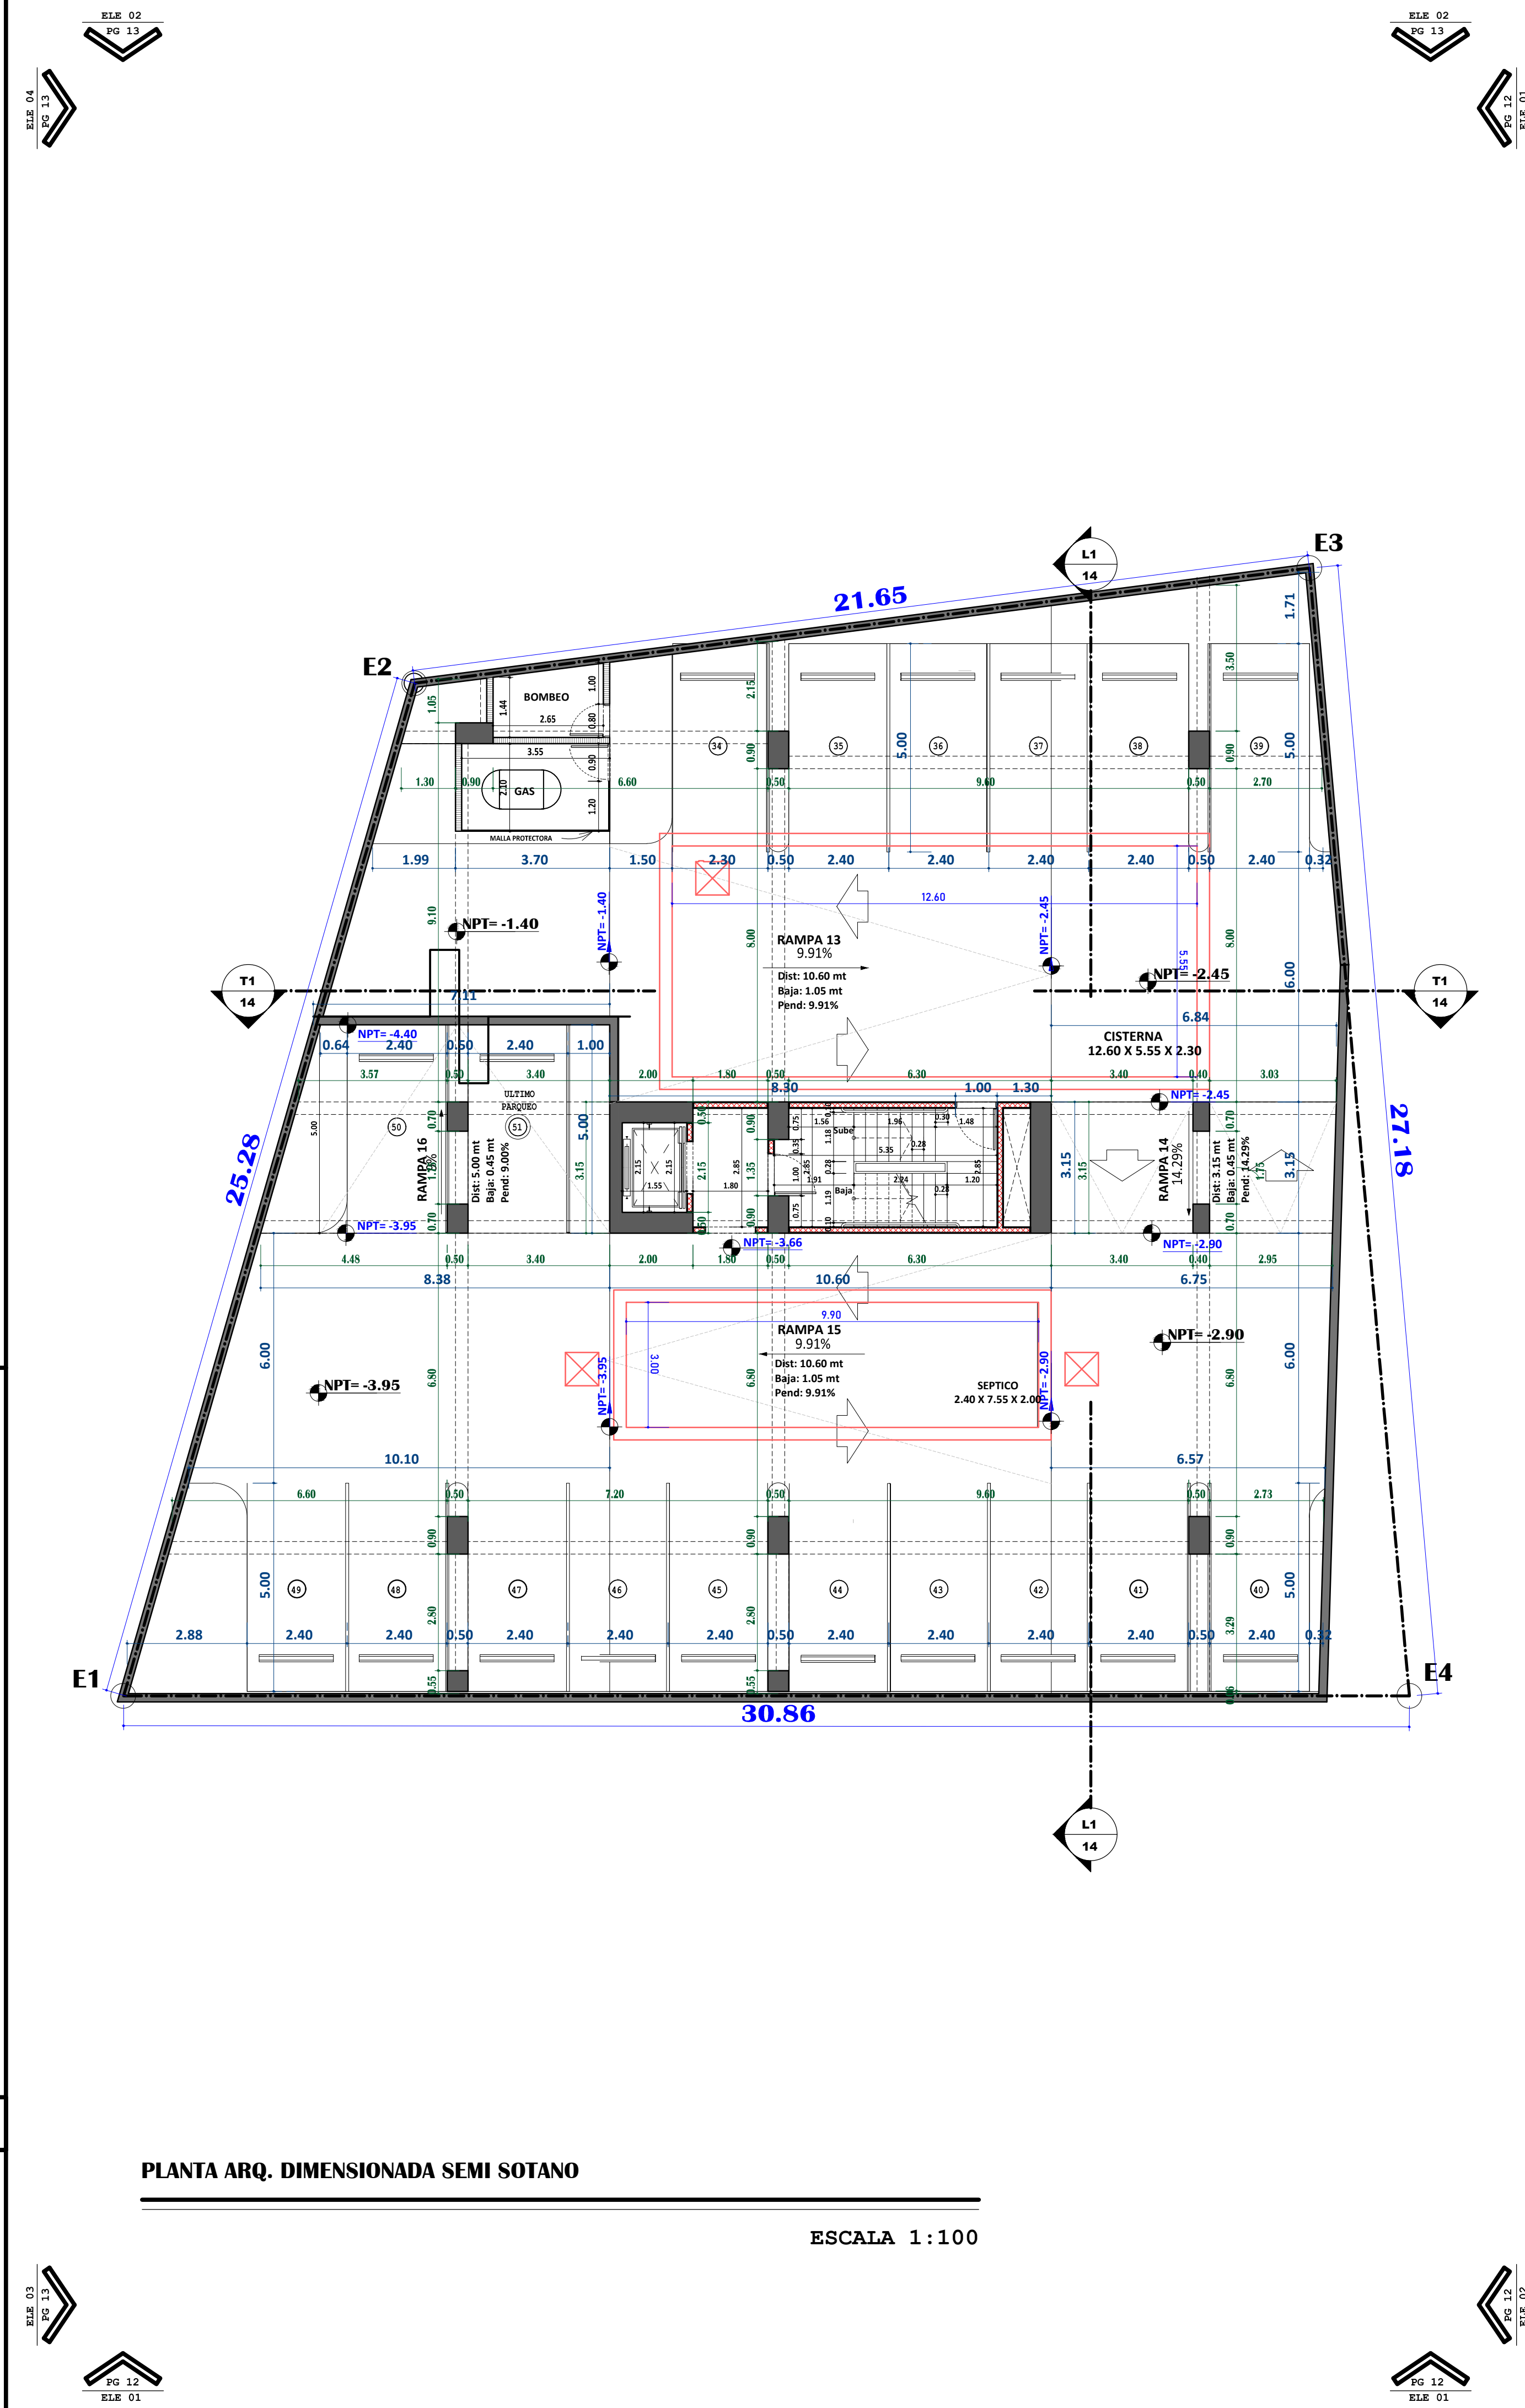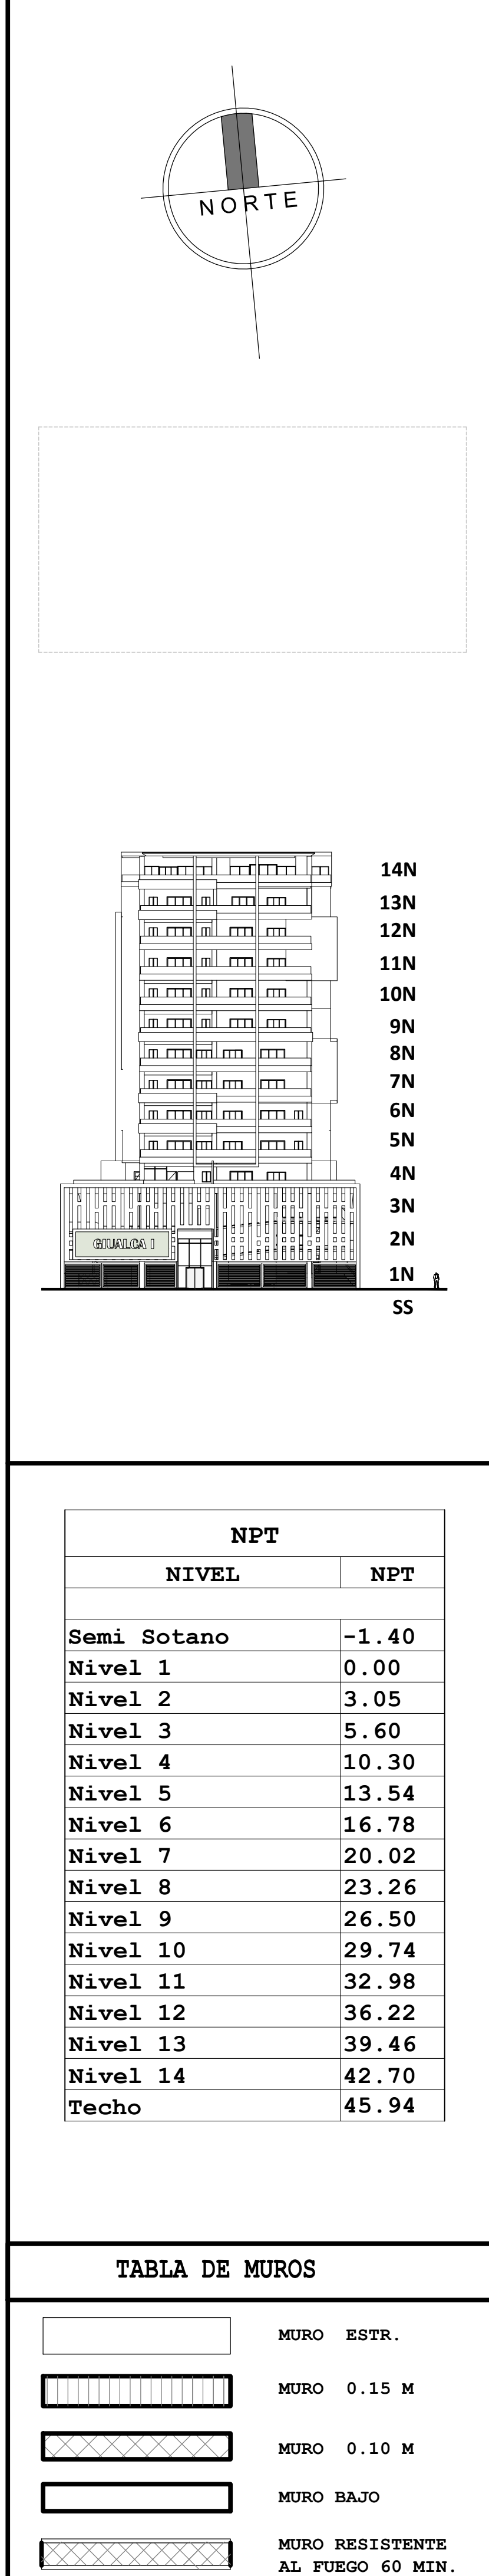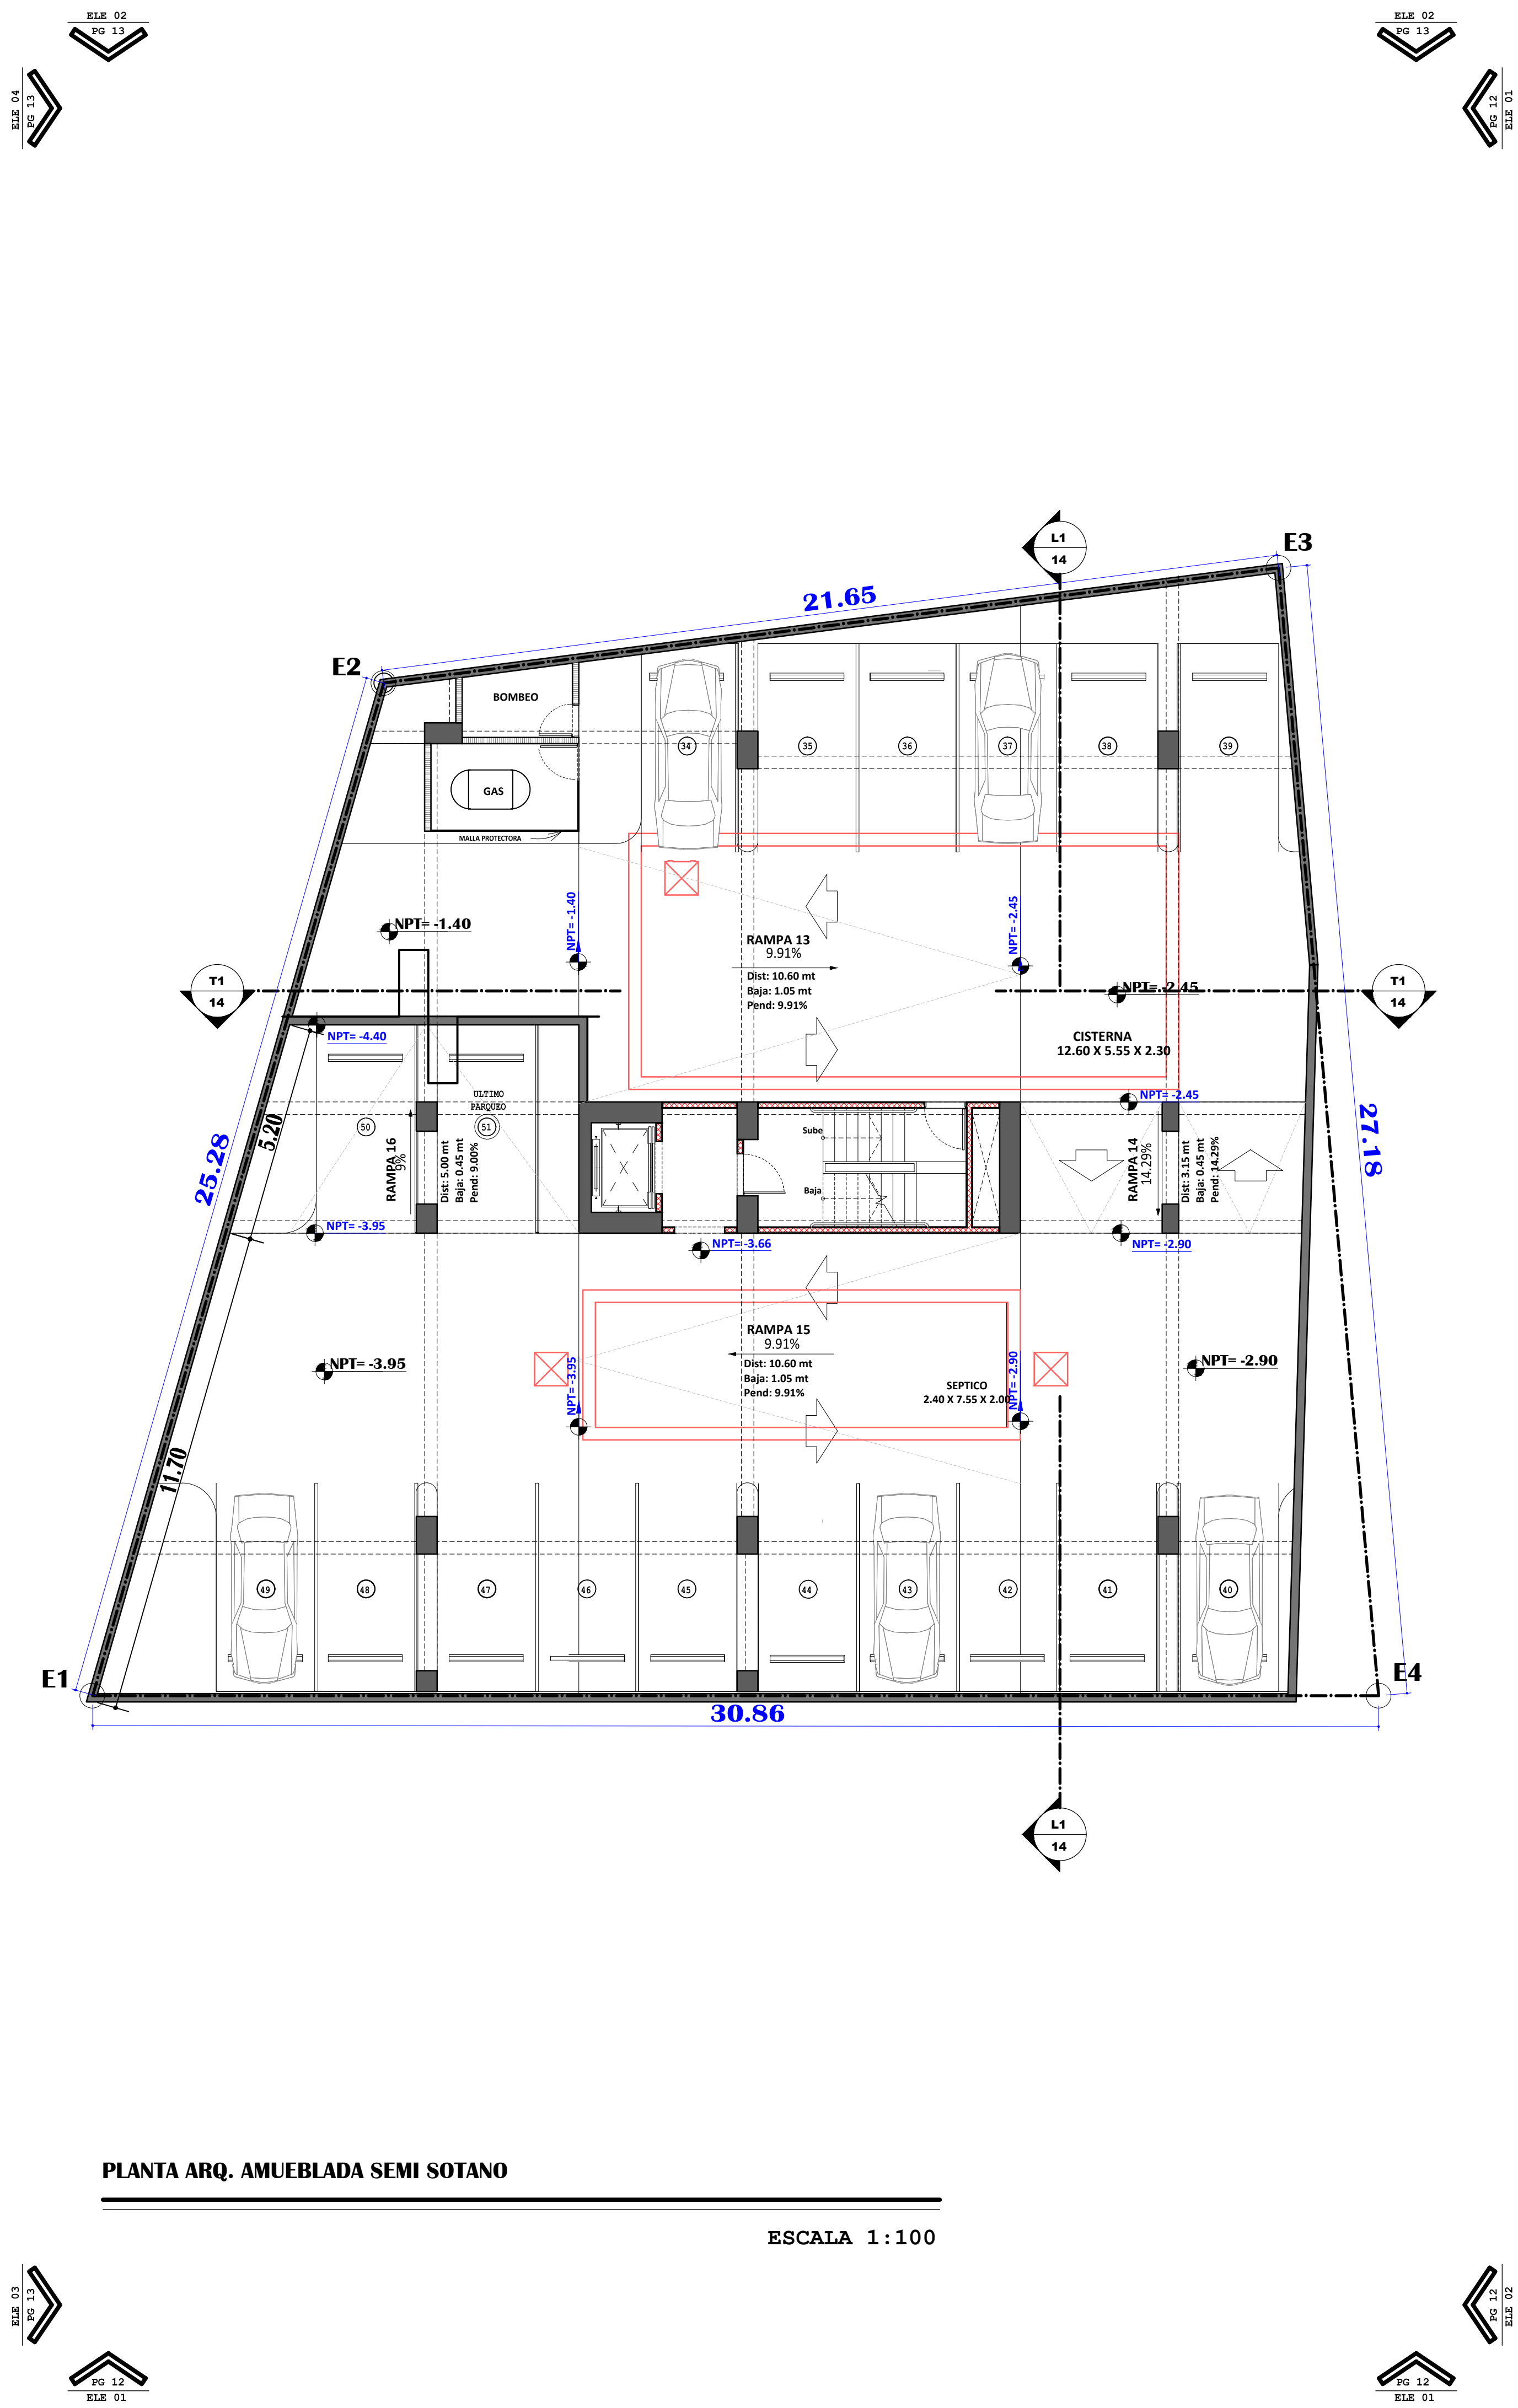

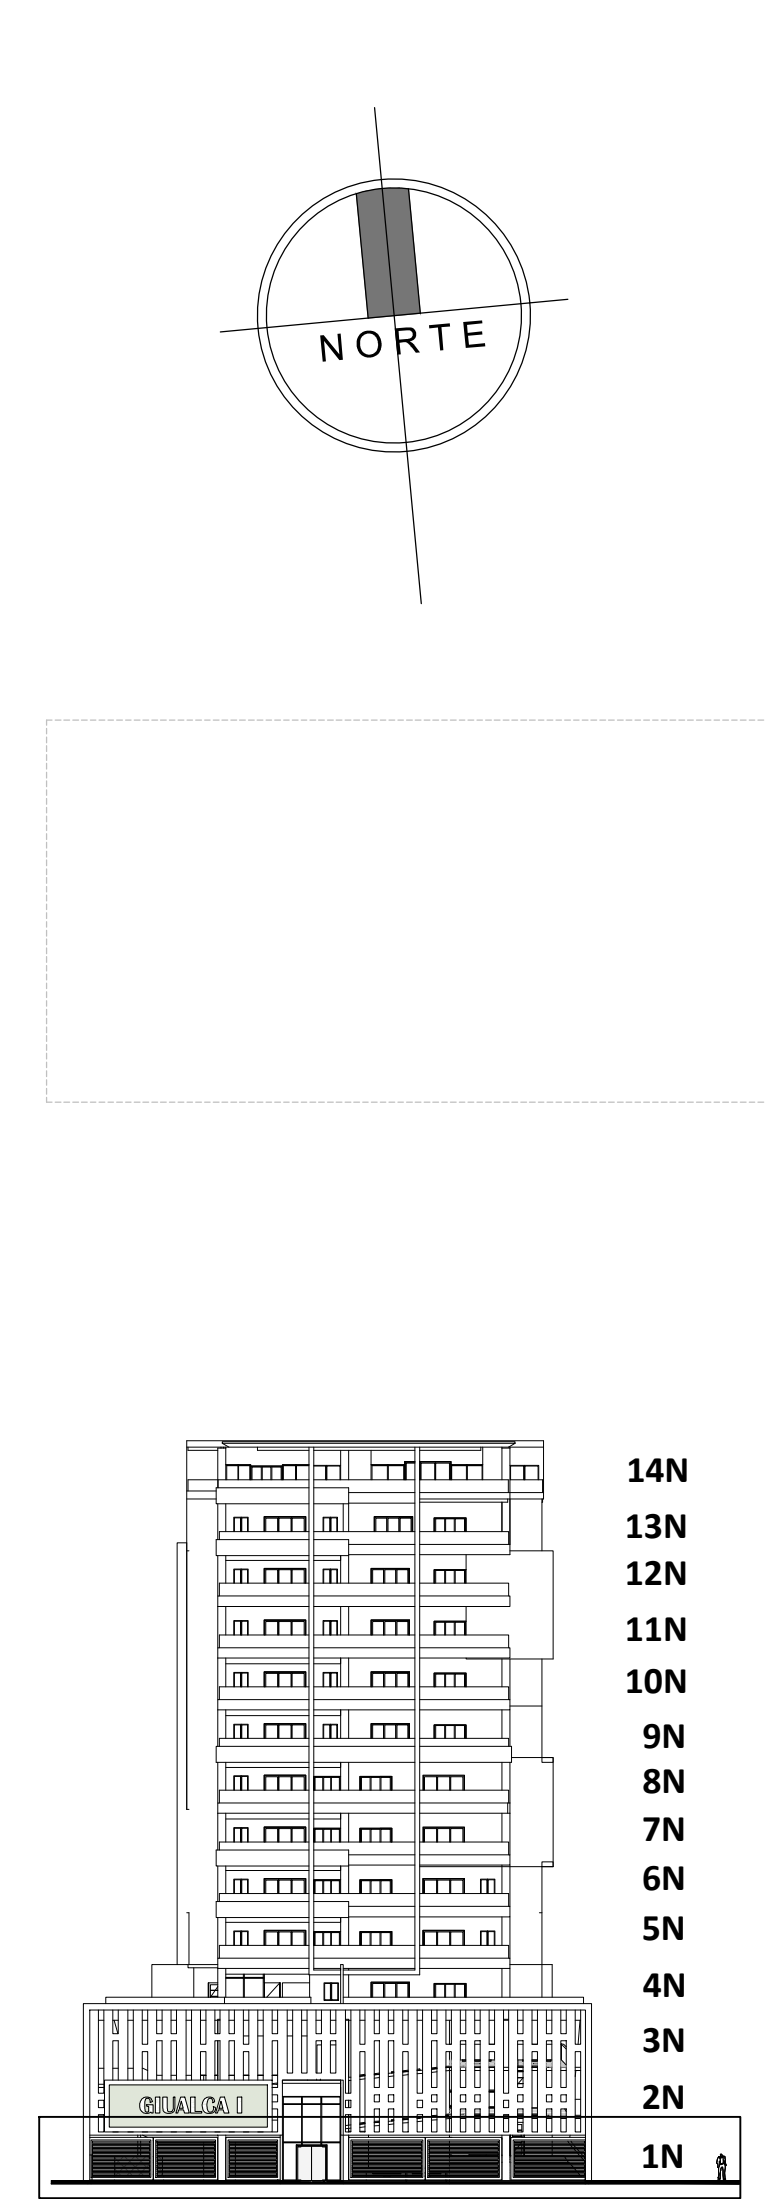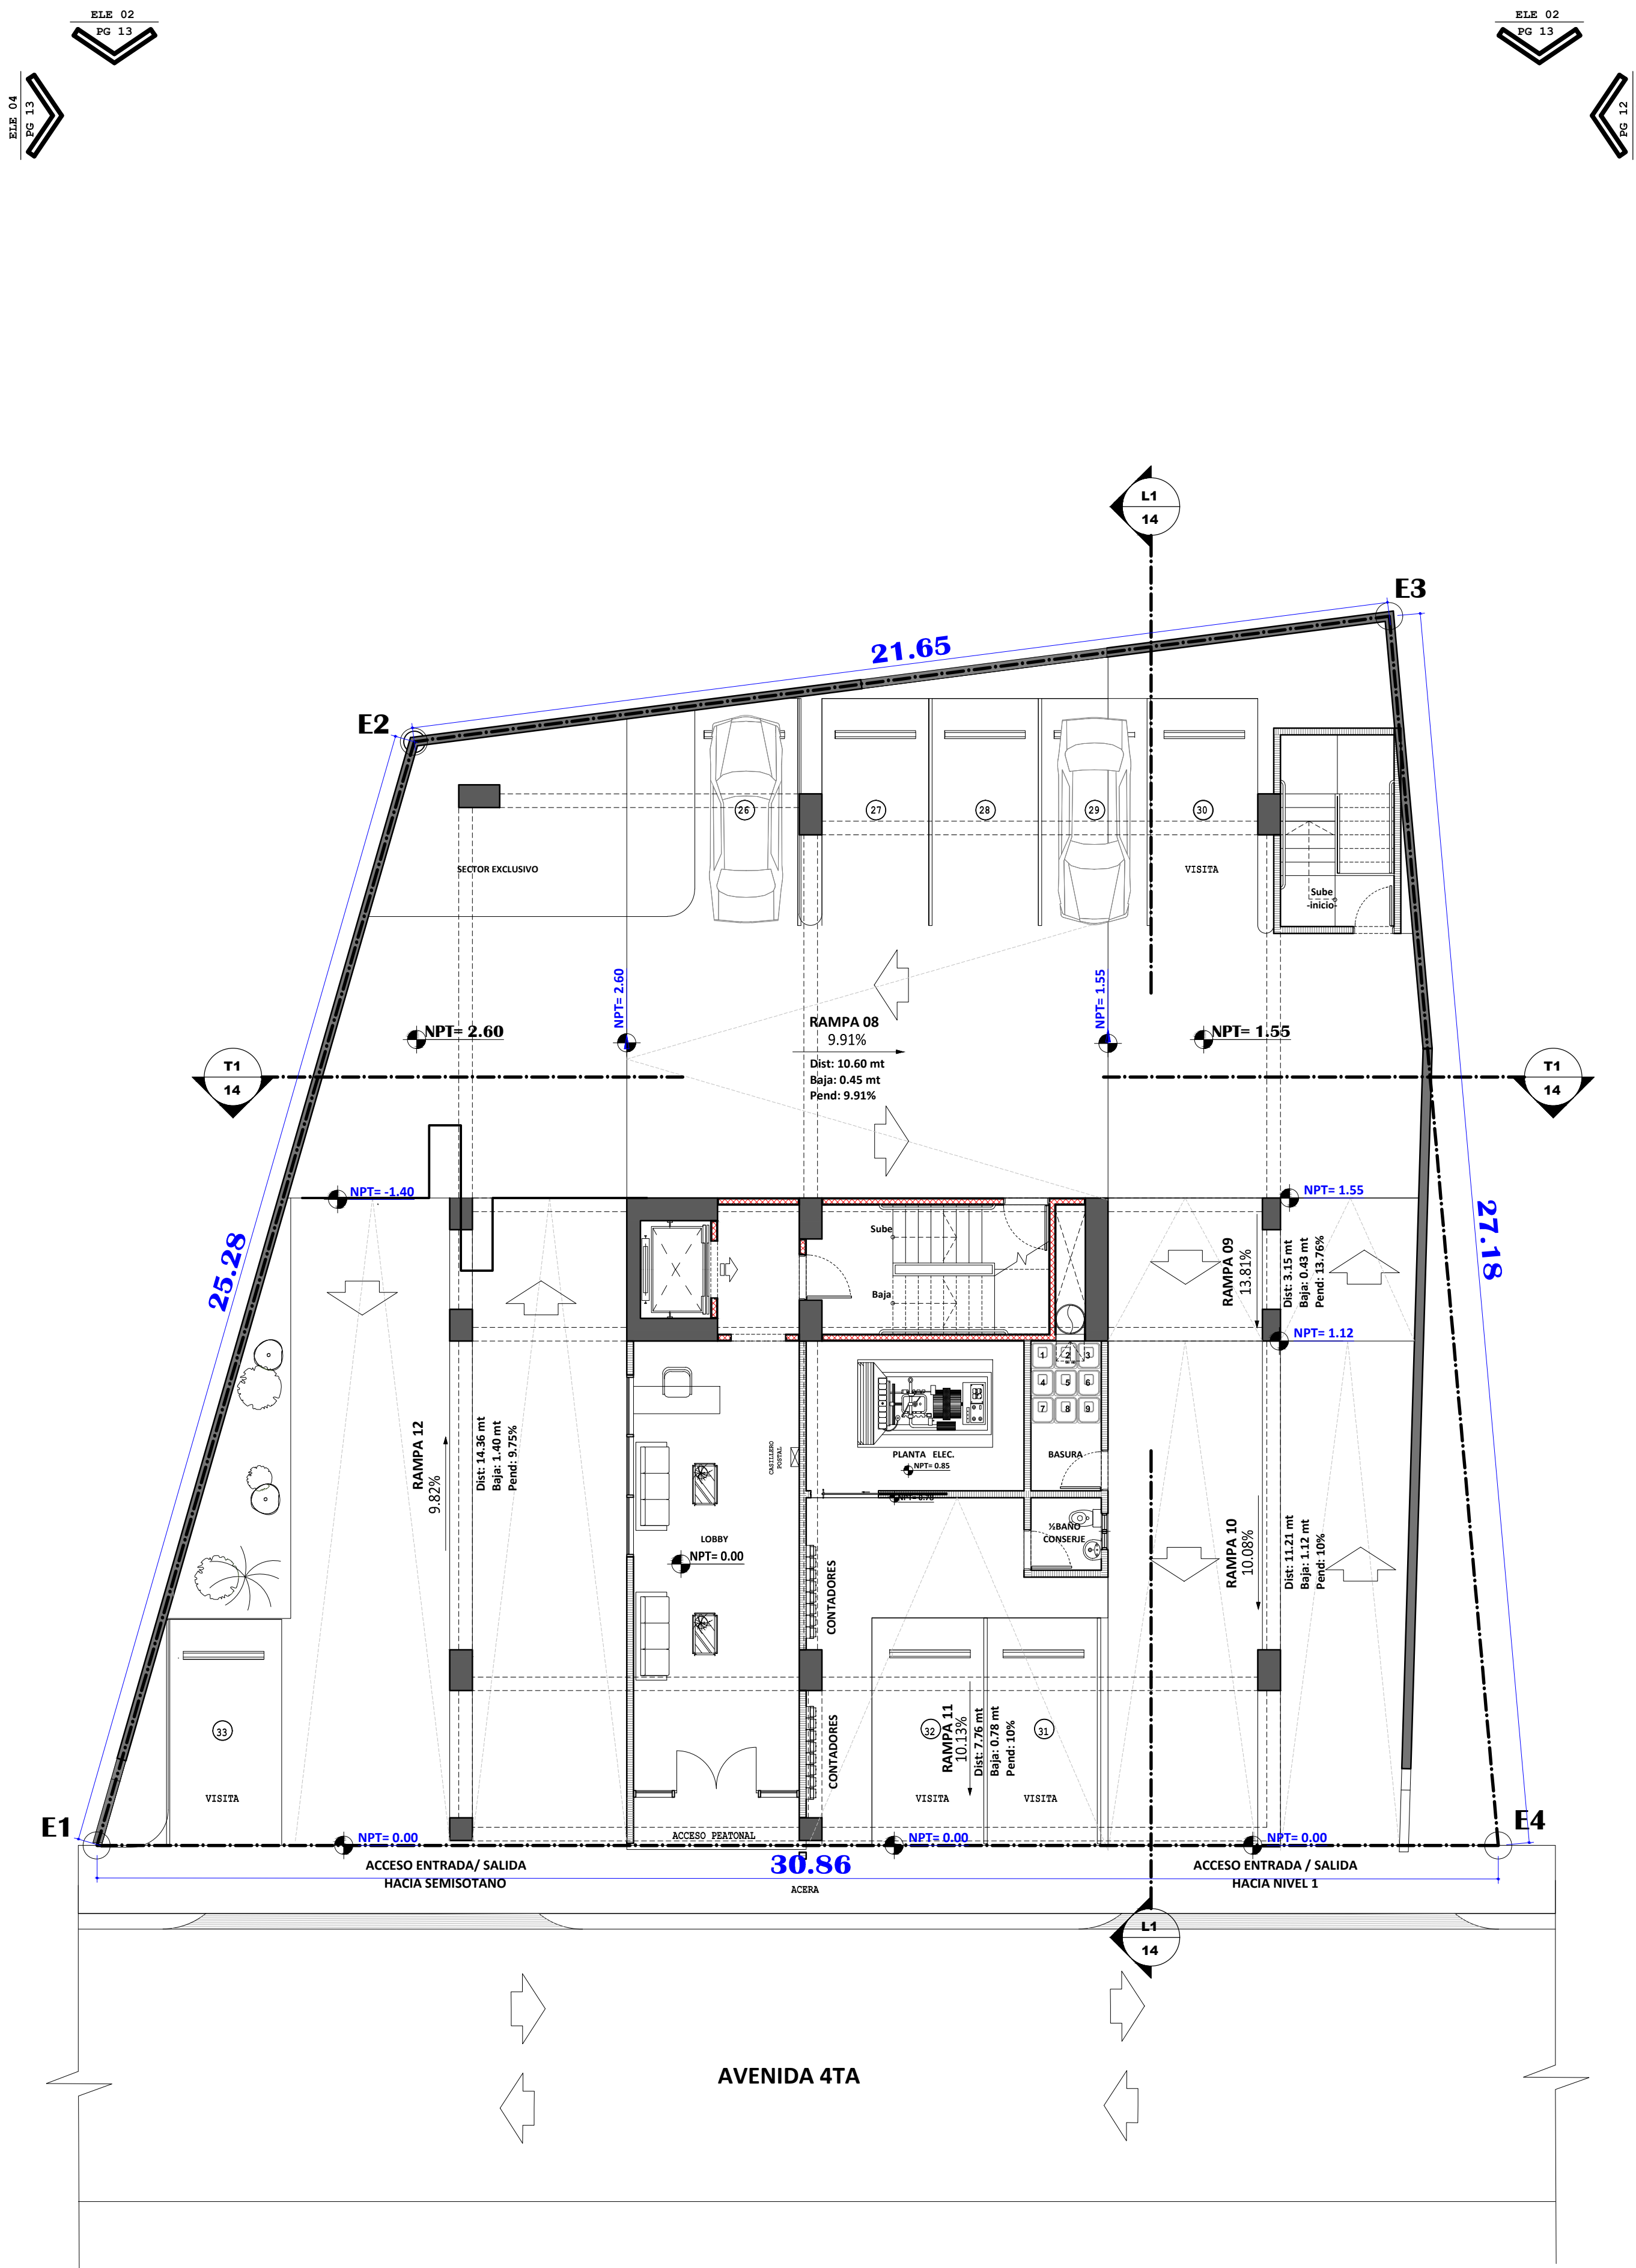

NPT	
NIVEL	NPT
Semi Sotano	-1.40
Nivel 1	0.00
Nivel 2	3.05
Nivel 3	5.60
Nivel 4	10.30
Nivel 5	13.54
Nivel 6	16.78
Nivel 7	20.02
Nivel 8	23.26
Nivel 9	26.50
Nivel 10	29.74
Nivel 11	32.98
Nivel 12	36.22
Nivel 13	39.46
Nivel 14	42.70
Techo	45.94

TABLA DE MUROS


	MURO ESTR.
	MURO 0.15 M
	MURO 0.10 M
	MURO BAJO
	MURO RESISTENTE AL FUEGO 60 MIN.

PLANTA ARQ. AMUEBLADA NIVEL 1

ESCALA 1:100


PLANTA ARQ. DIMENSIONADA NIVEL 1

ESCALA 1:100

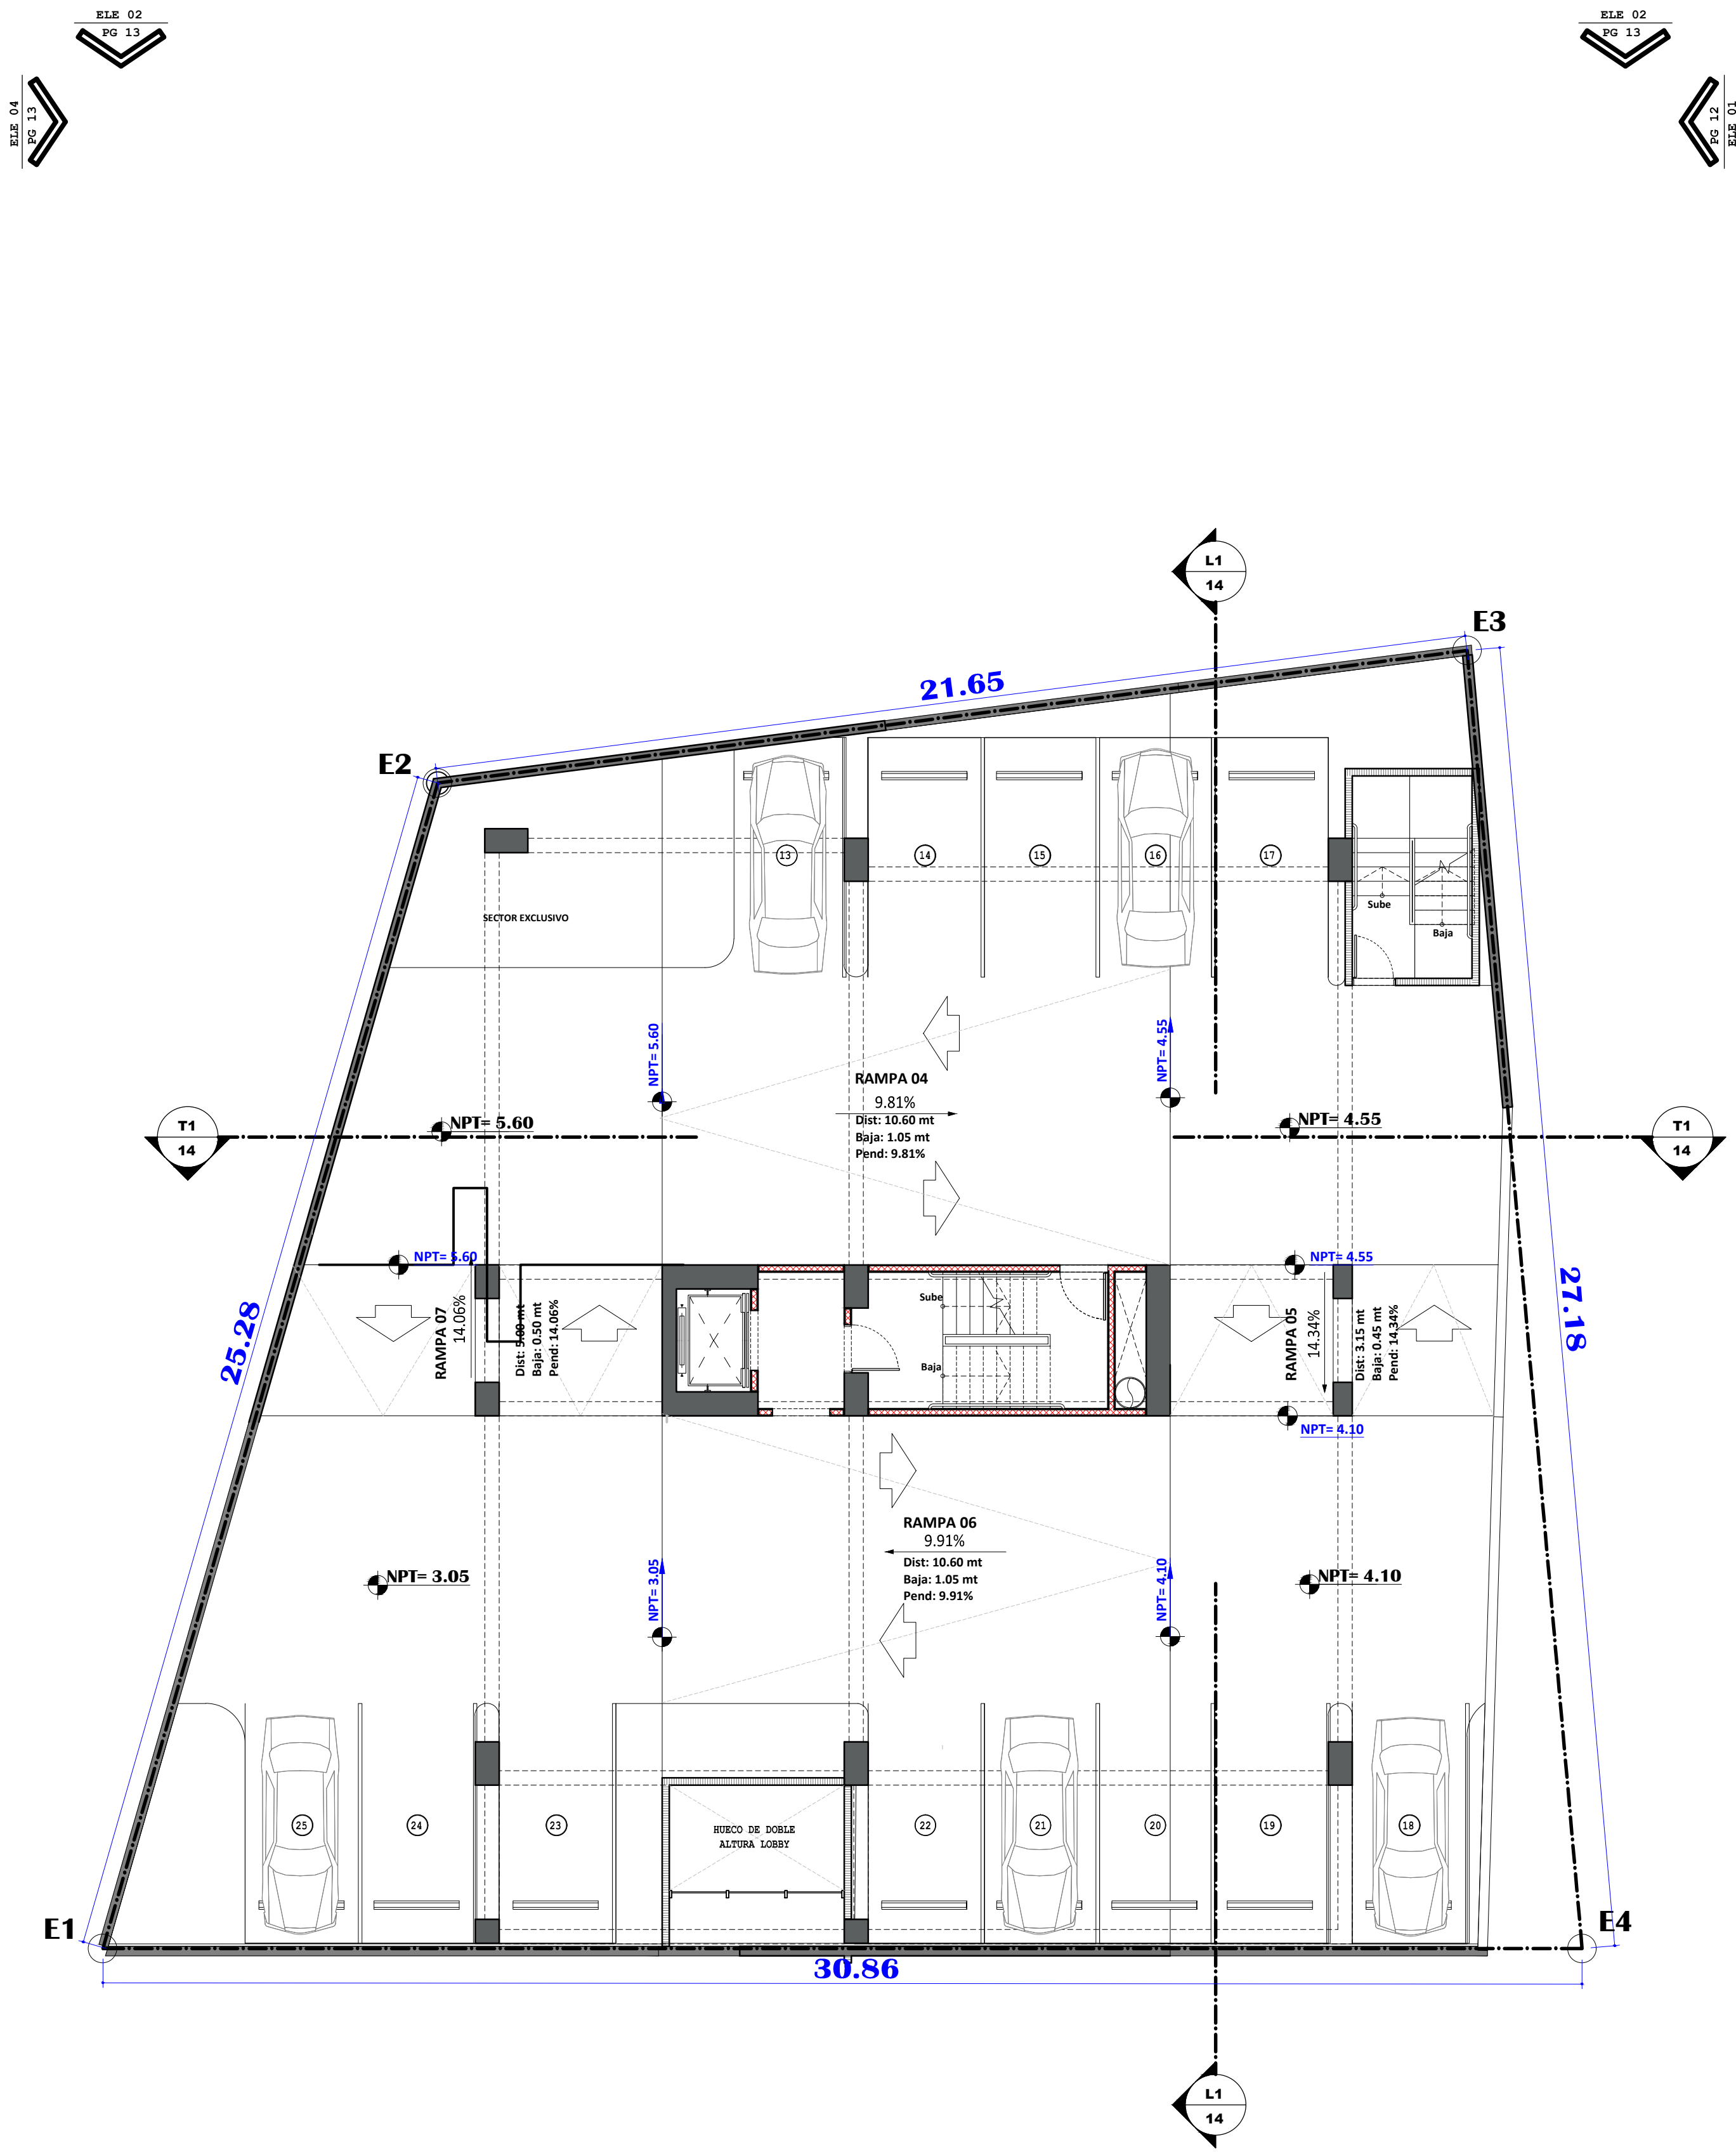

PLANTA ARQ. AMUEBLADA NIVEL 2


ESCALA 1:100

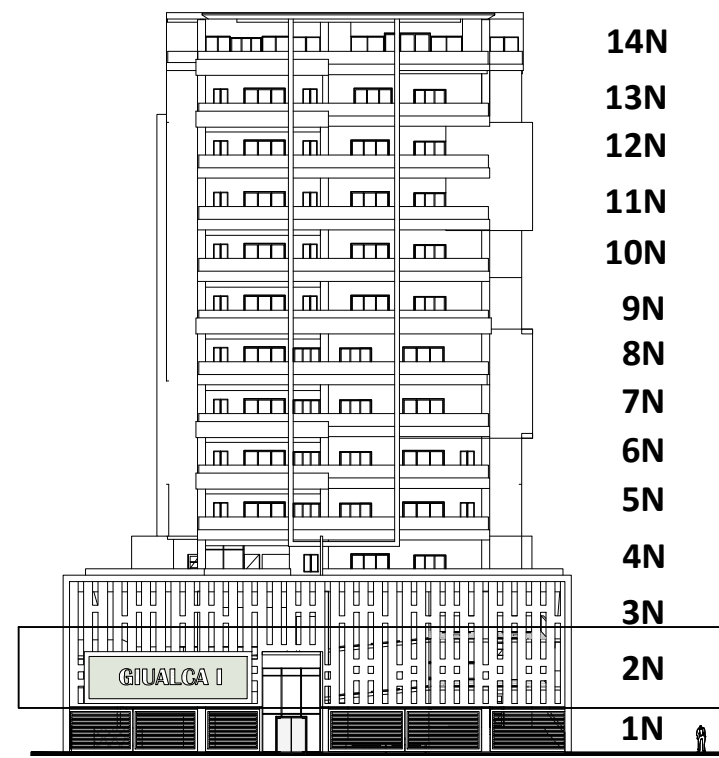

NPT	
NIVEL	NPT
Semi Sotano	-1.40
Nivel 1	0.00
Nivel 2	3.05
Nivel 3	5.60
Nivel 4	10.30
Nivel 5	13.54
Nivel 6	16.78
Nivel 7	20.02
Nivel 8	23.26
Nivel 9	26.50
Nivel 10	29.74
Nivel 11	32.98
Nivel 12	36.22
Nivel 13	39.46
Nivel 14	42.70
Techo	45.94




TABLA DE MUROS

	MURO ESTR.
	MURO 0.15 M
	MURO 0.10 M
	MURO BAJO
	MURO RESISTENTE AL FUEGO 60 MIN.

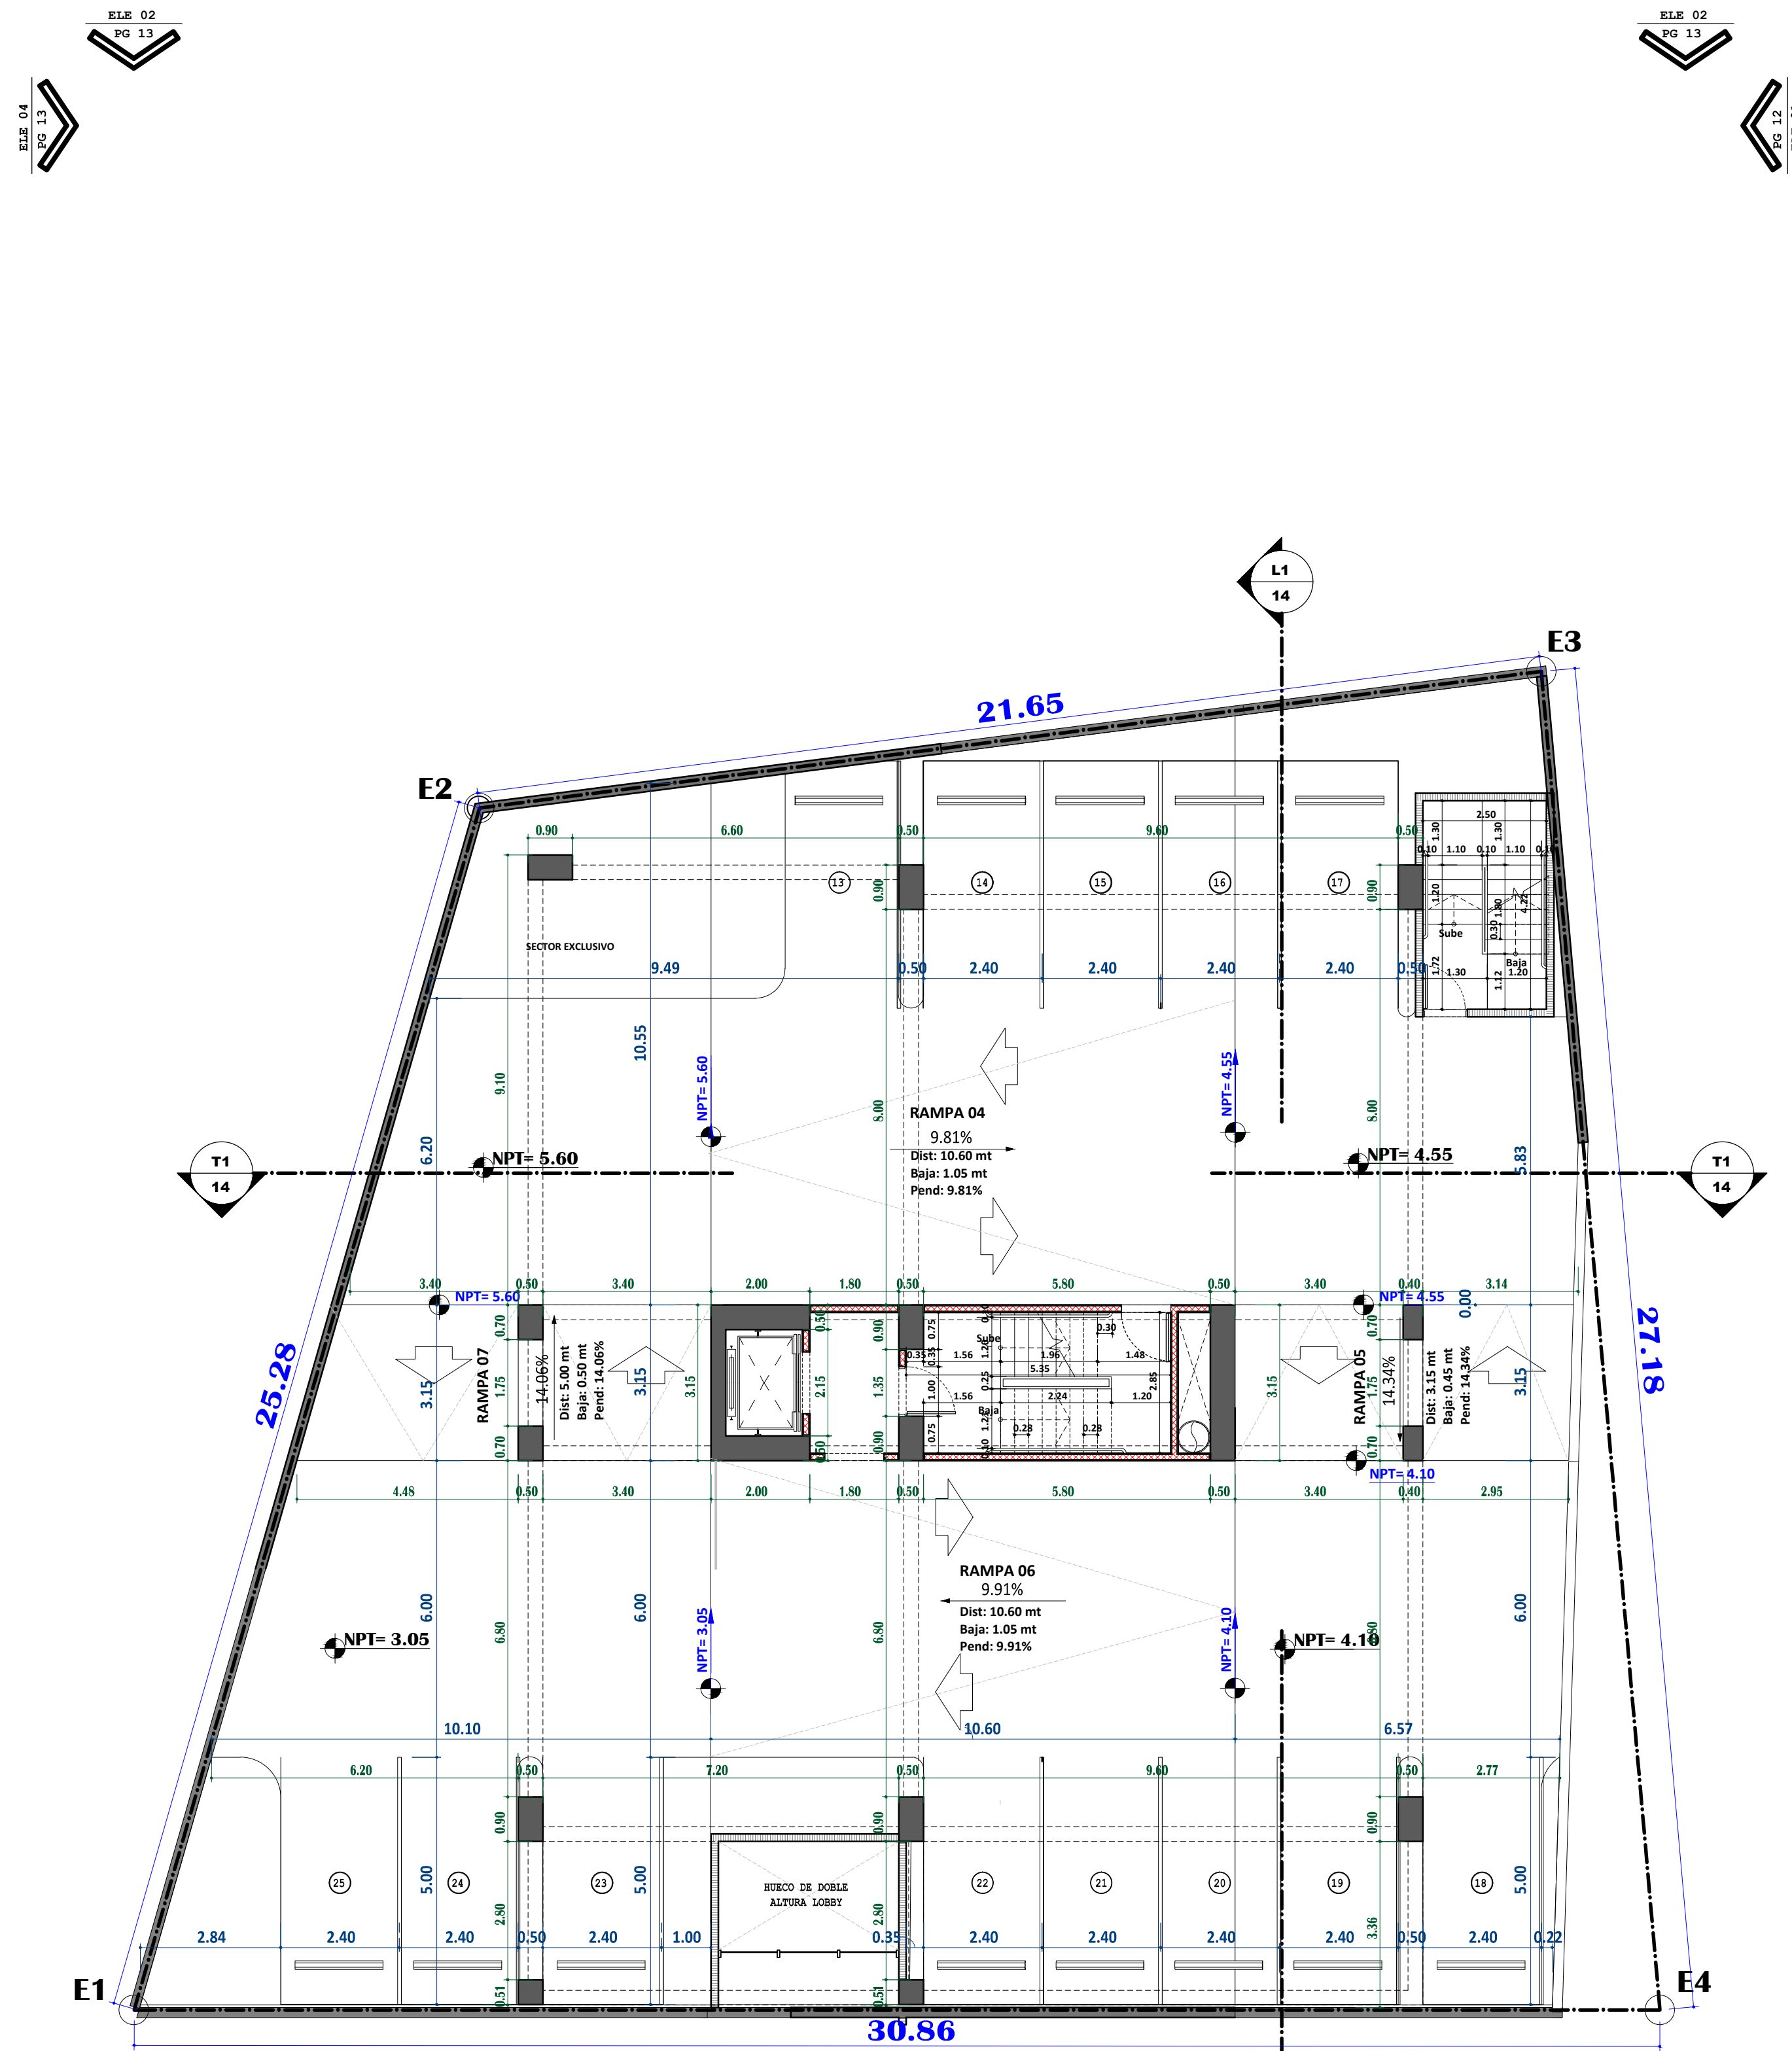


PLANTA ARQ. DIMENSIONADA NIVEL 2

ESCALA 1:100

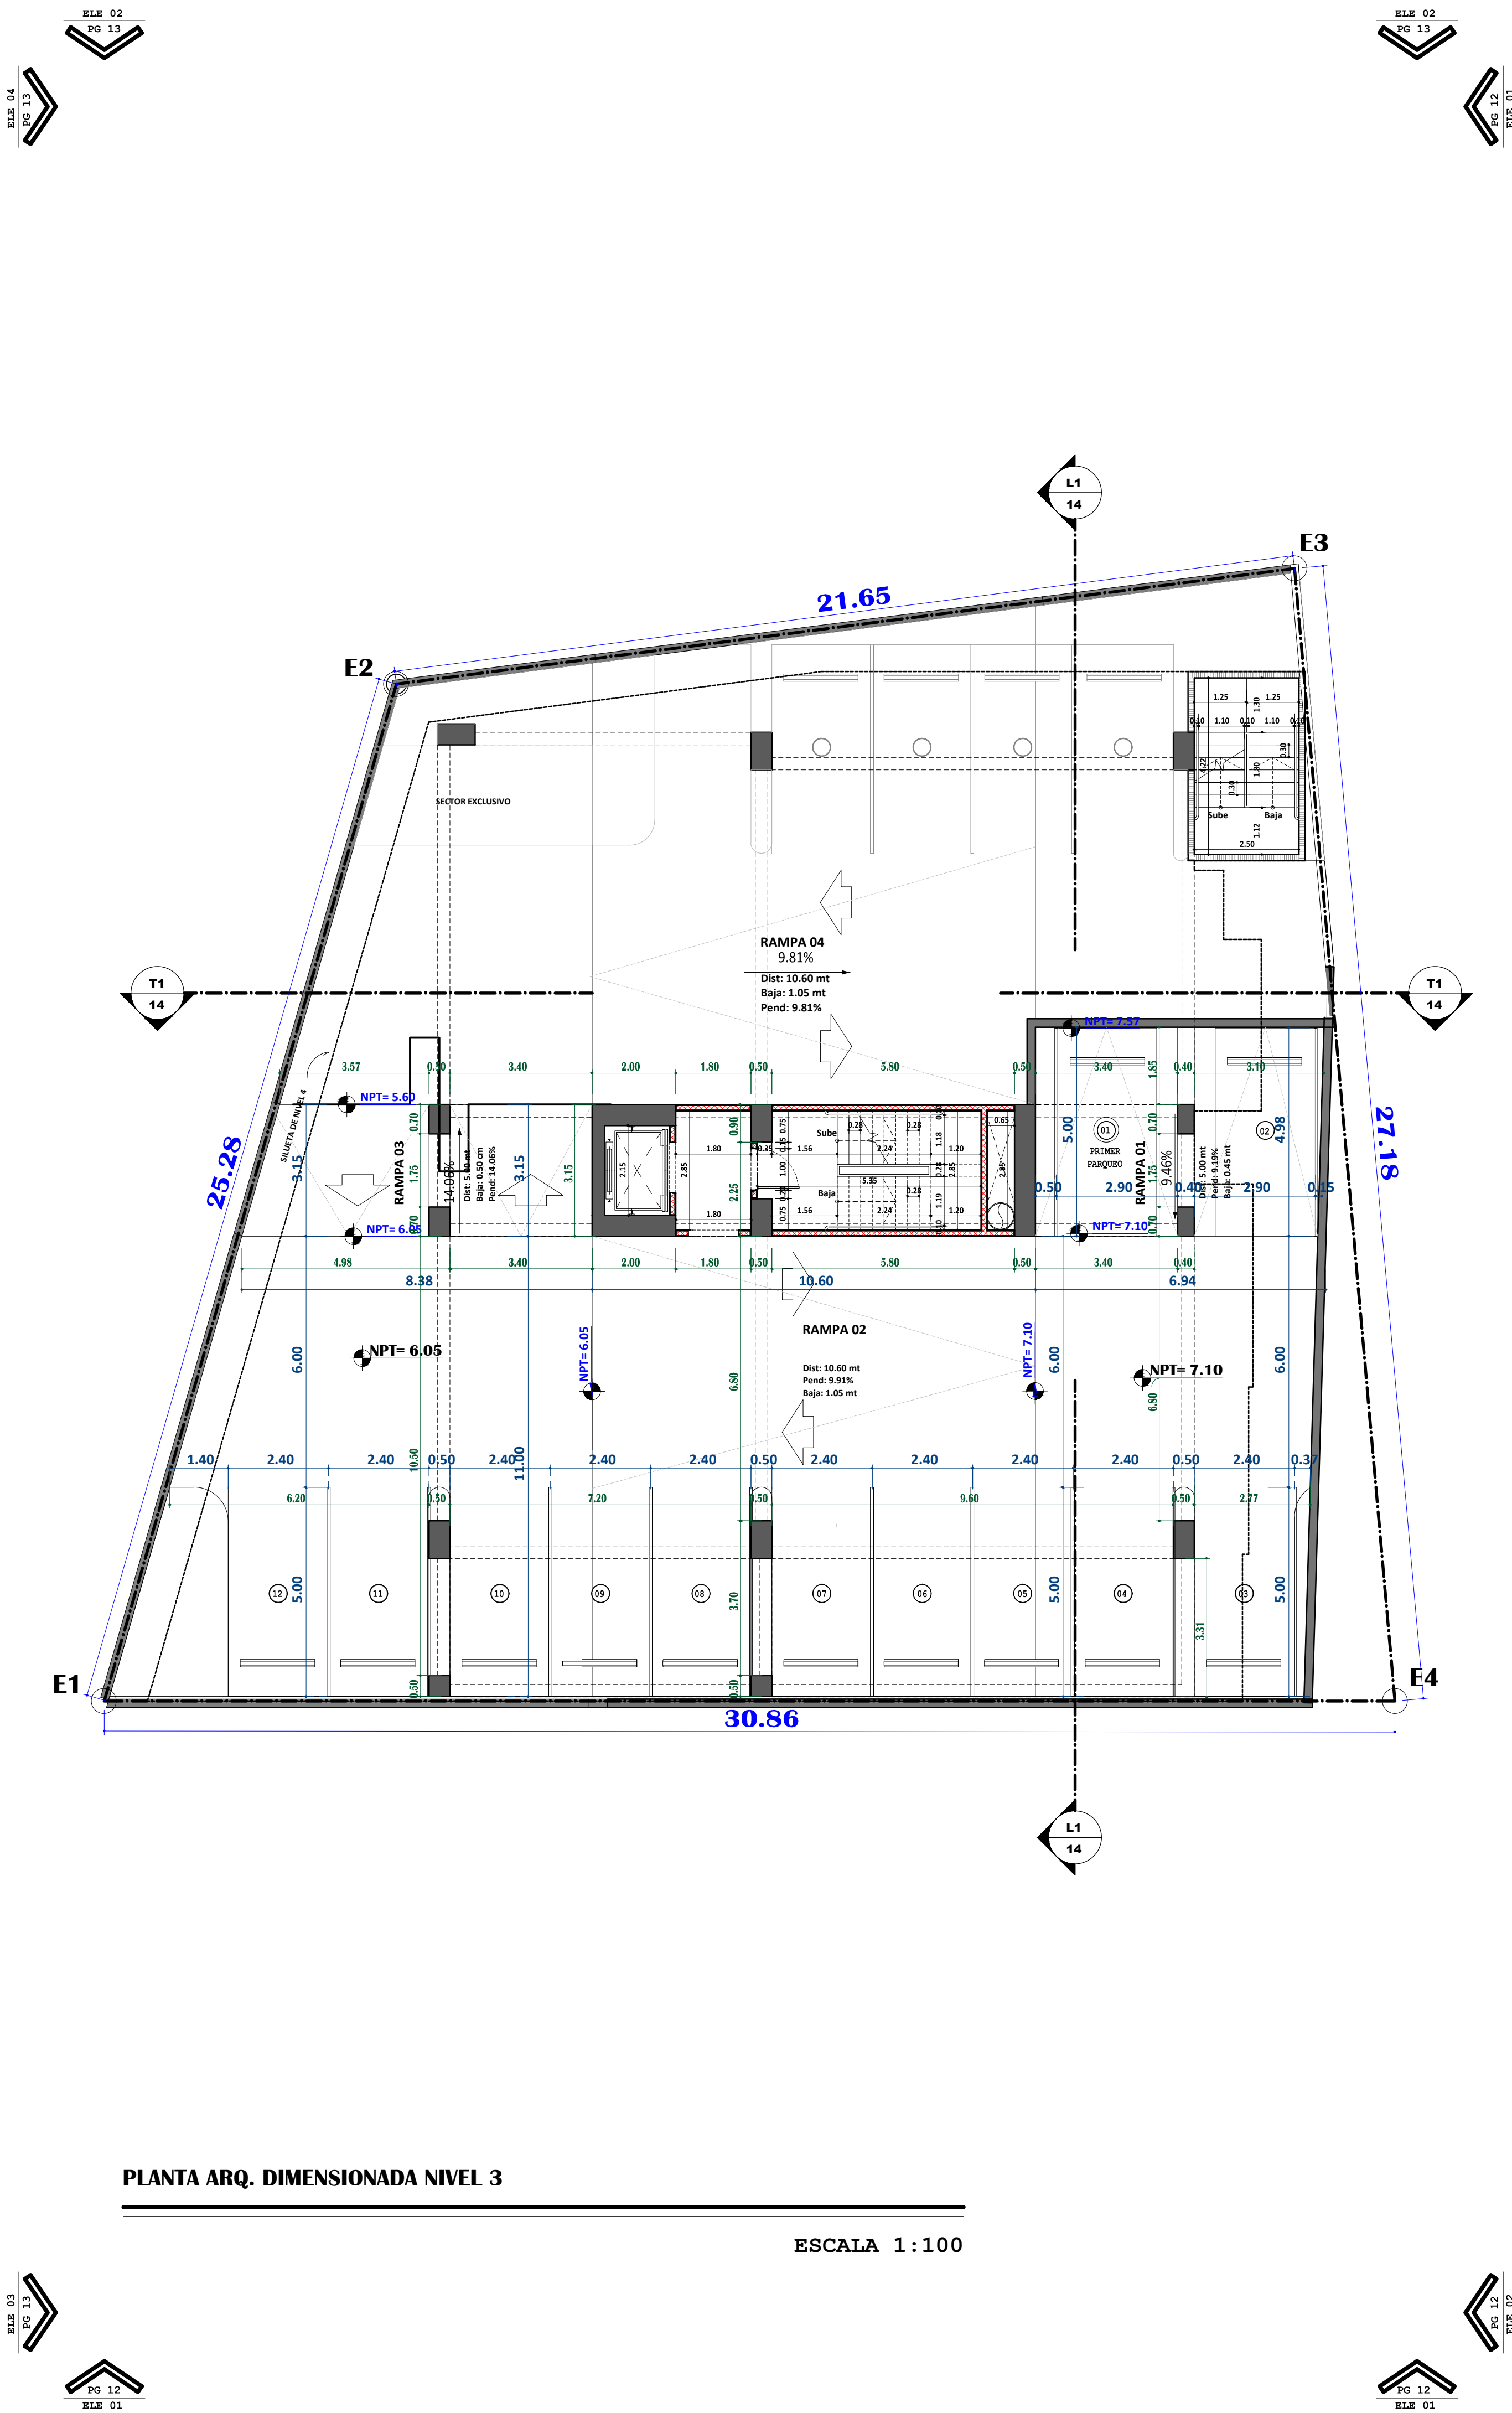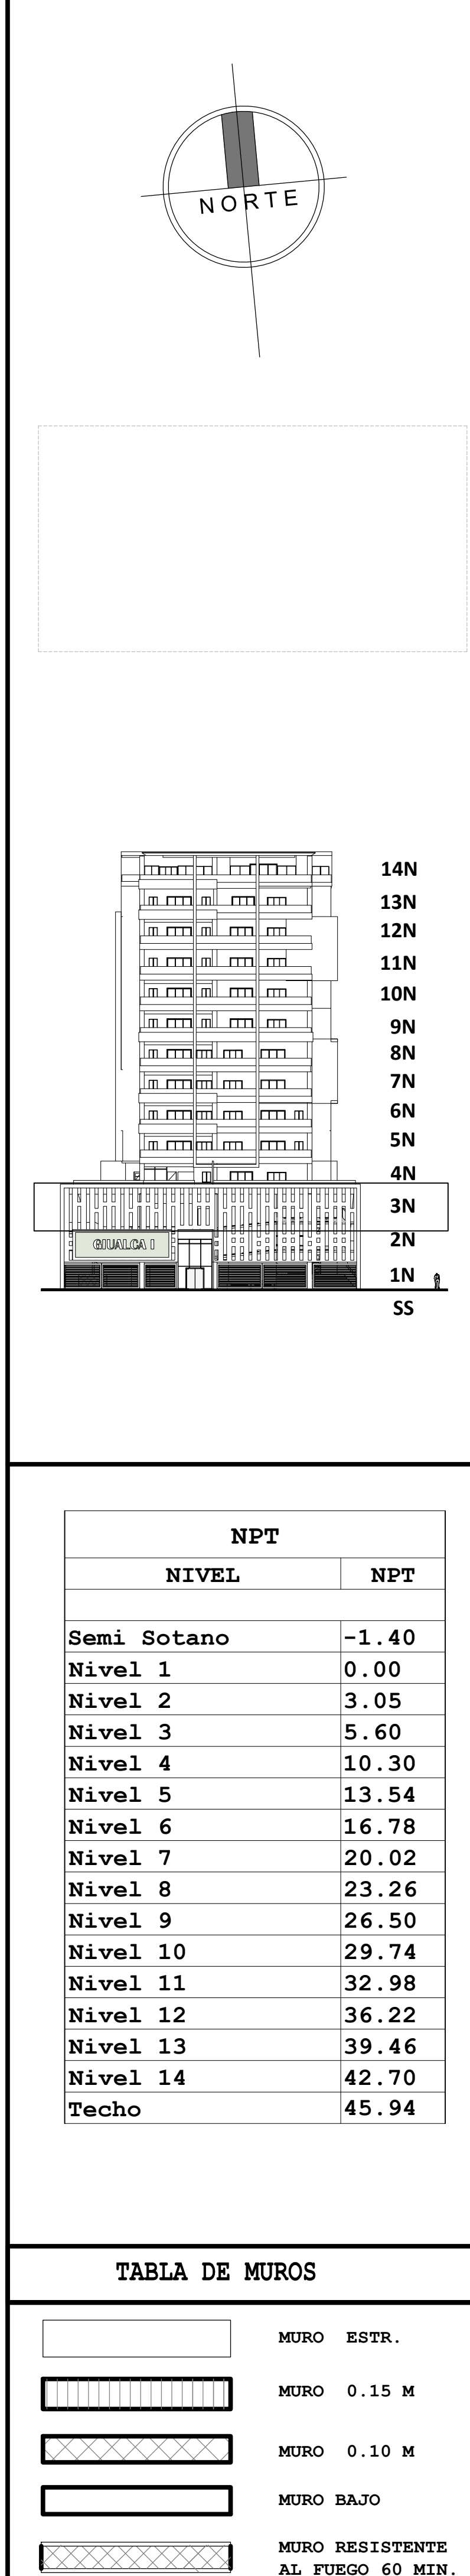
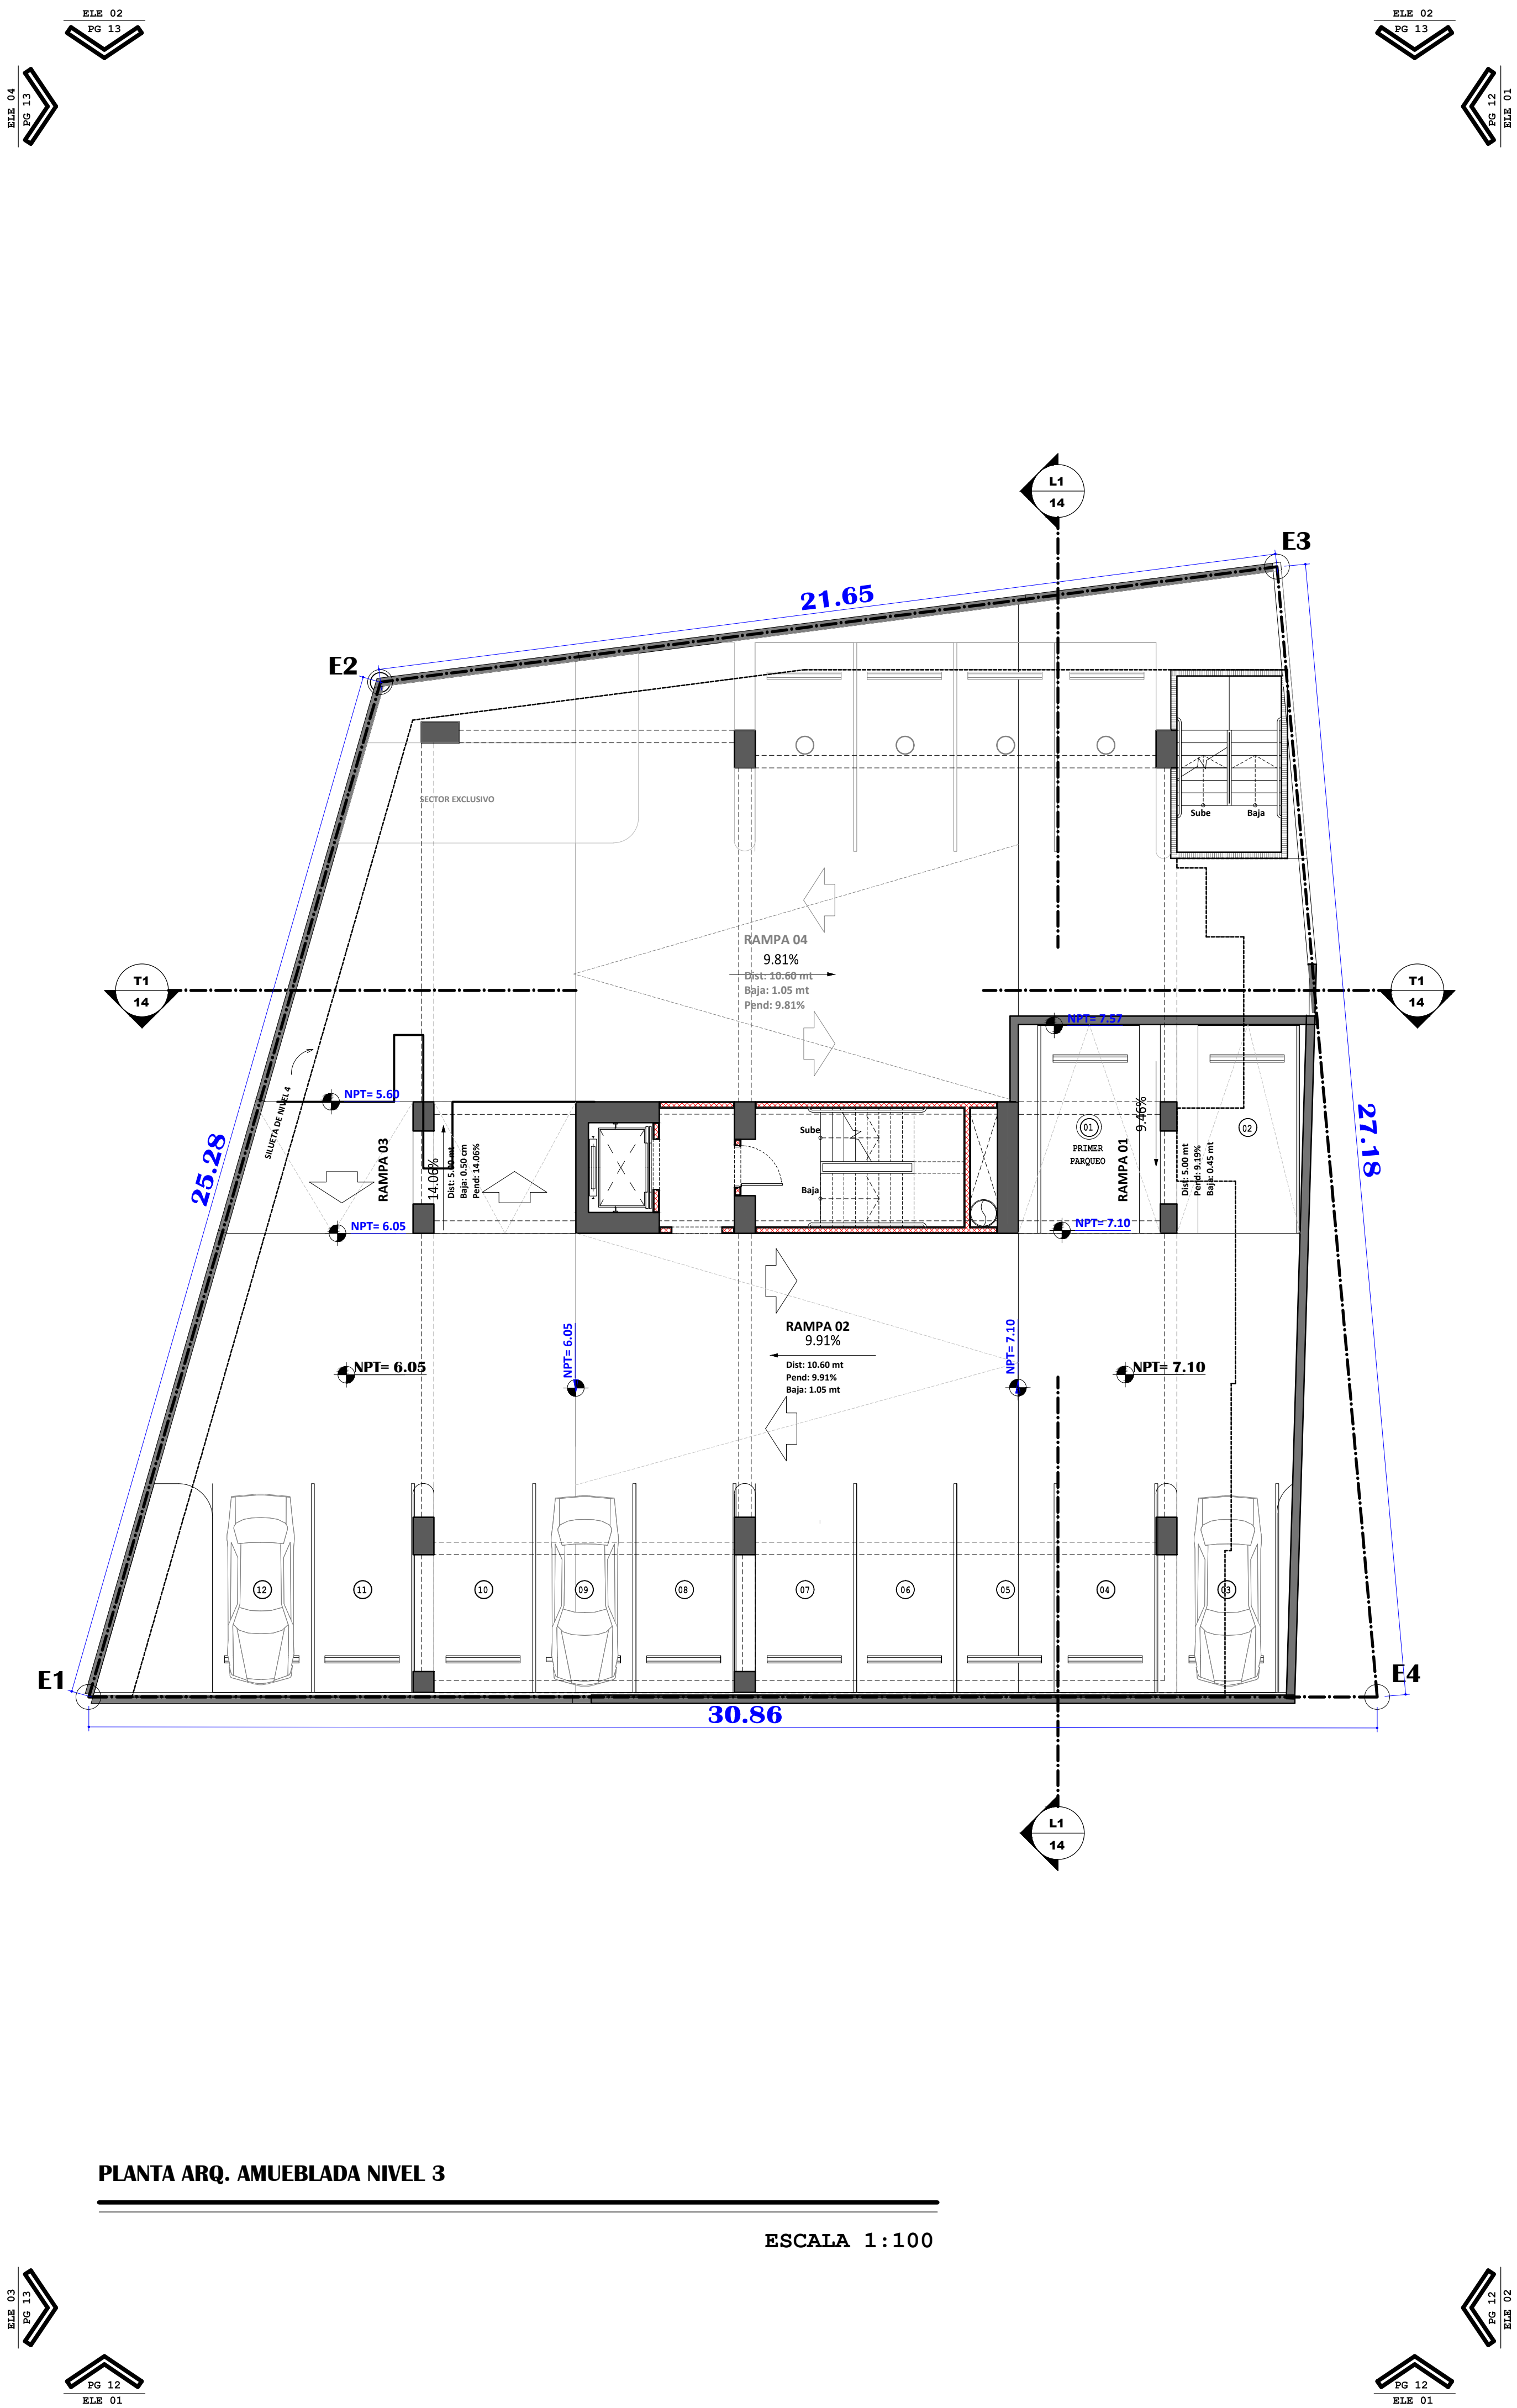



PLANTA ARQ. AMUEBLADA NIVEL 4

ESCALA 1:100

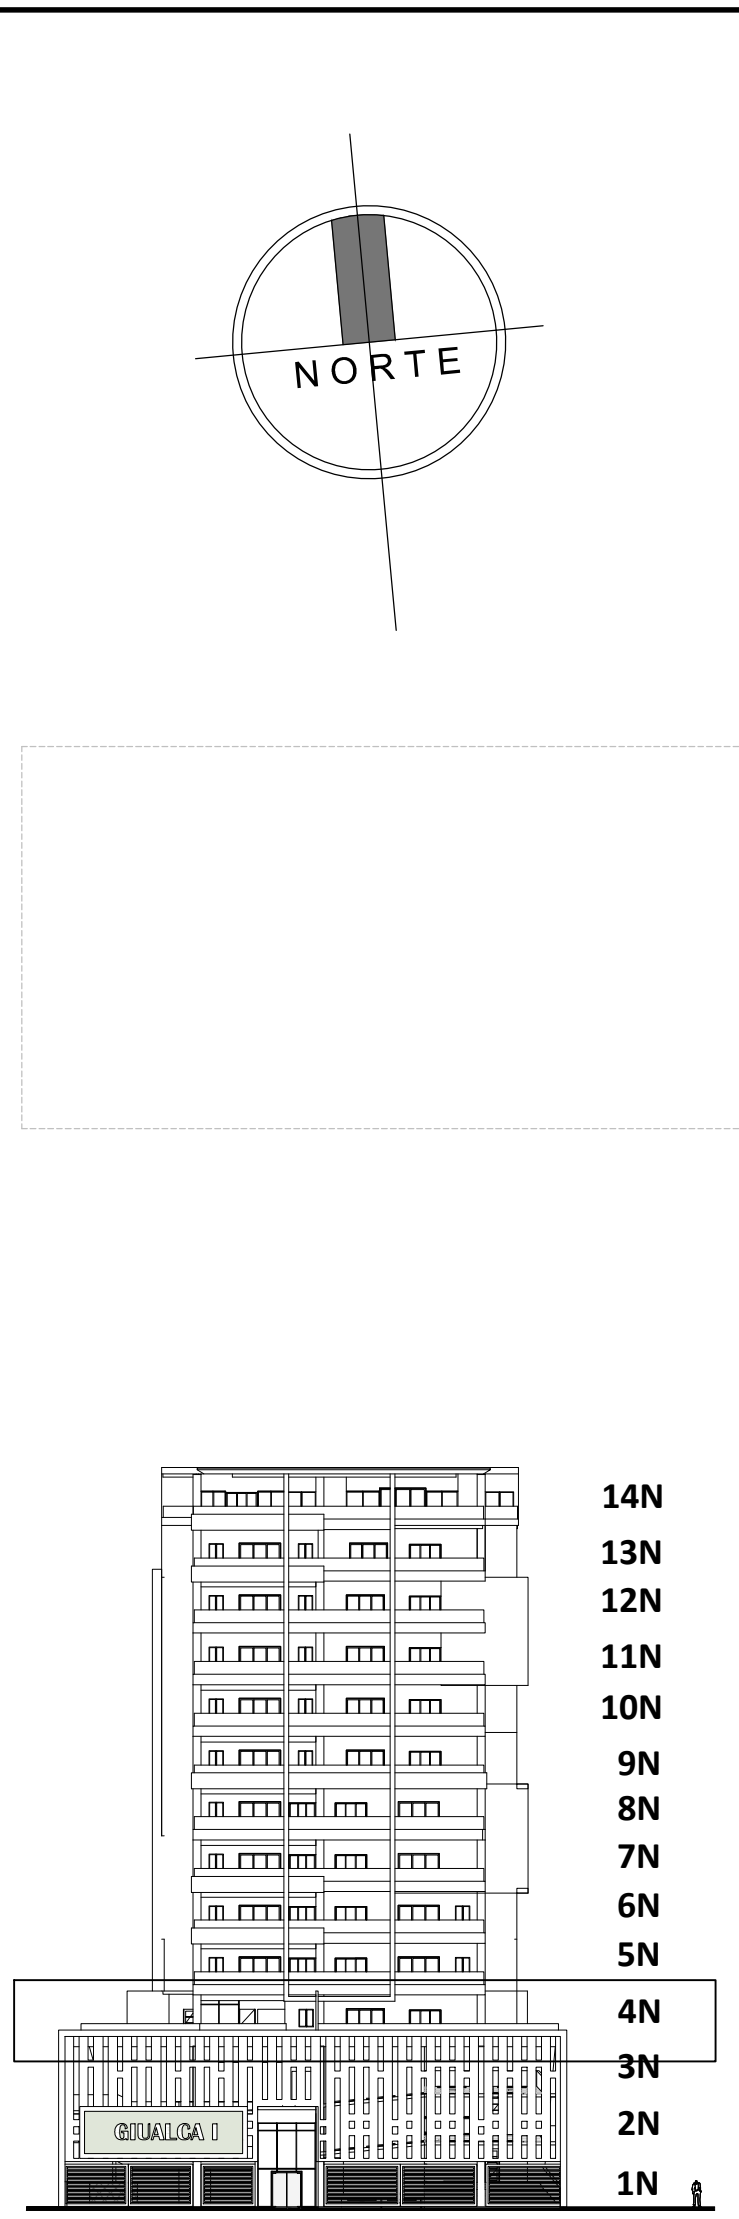


NPT	
NIVEL	NPT
Semi Sotano	-1.40
Nivel 1	0.00
Nivel 2	3.05
Nivel 3	5.60
Nivel 4	10.30
Nivel 5	13.54
Nivel 6	16.78
Nivel 7	20.02
Nivel 8	23.26
Nivel 9	26.50
Nivel 10	29.74
Nivel 11	32.98
Nivel 12	36.22
Nivel 13	39.46
Nivel 14	42.70
Techo	45.94

  TABLA DE MUROS	
	MURO ESTR.
	MURO 0.15 M
	MURO 0.10 M
	MURO BAJO
	MURO RESISTENTE AL FUEGO 60 MIN.

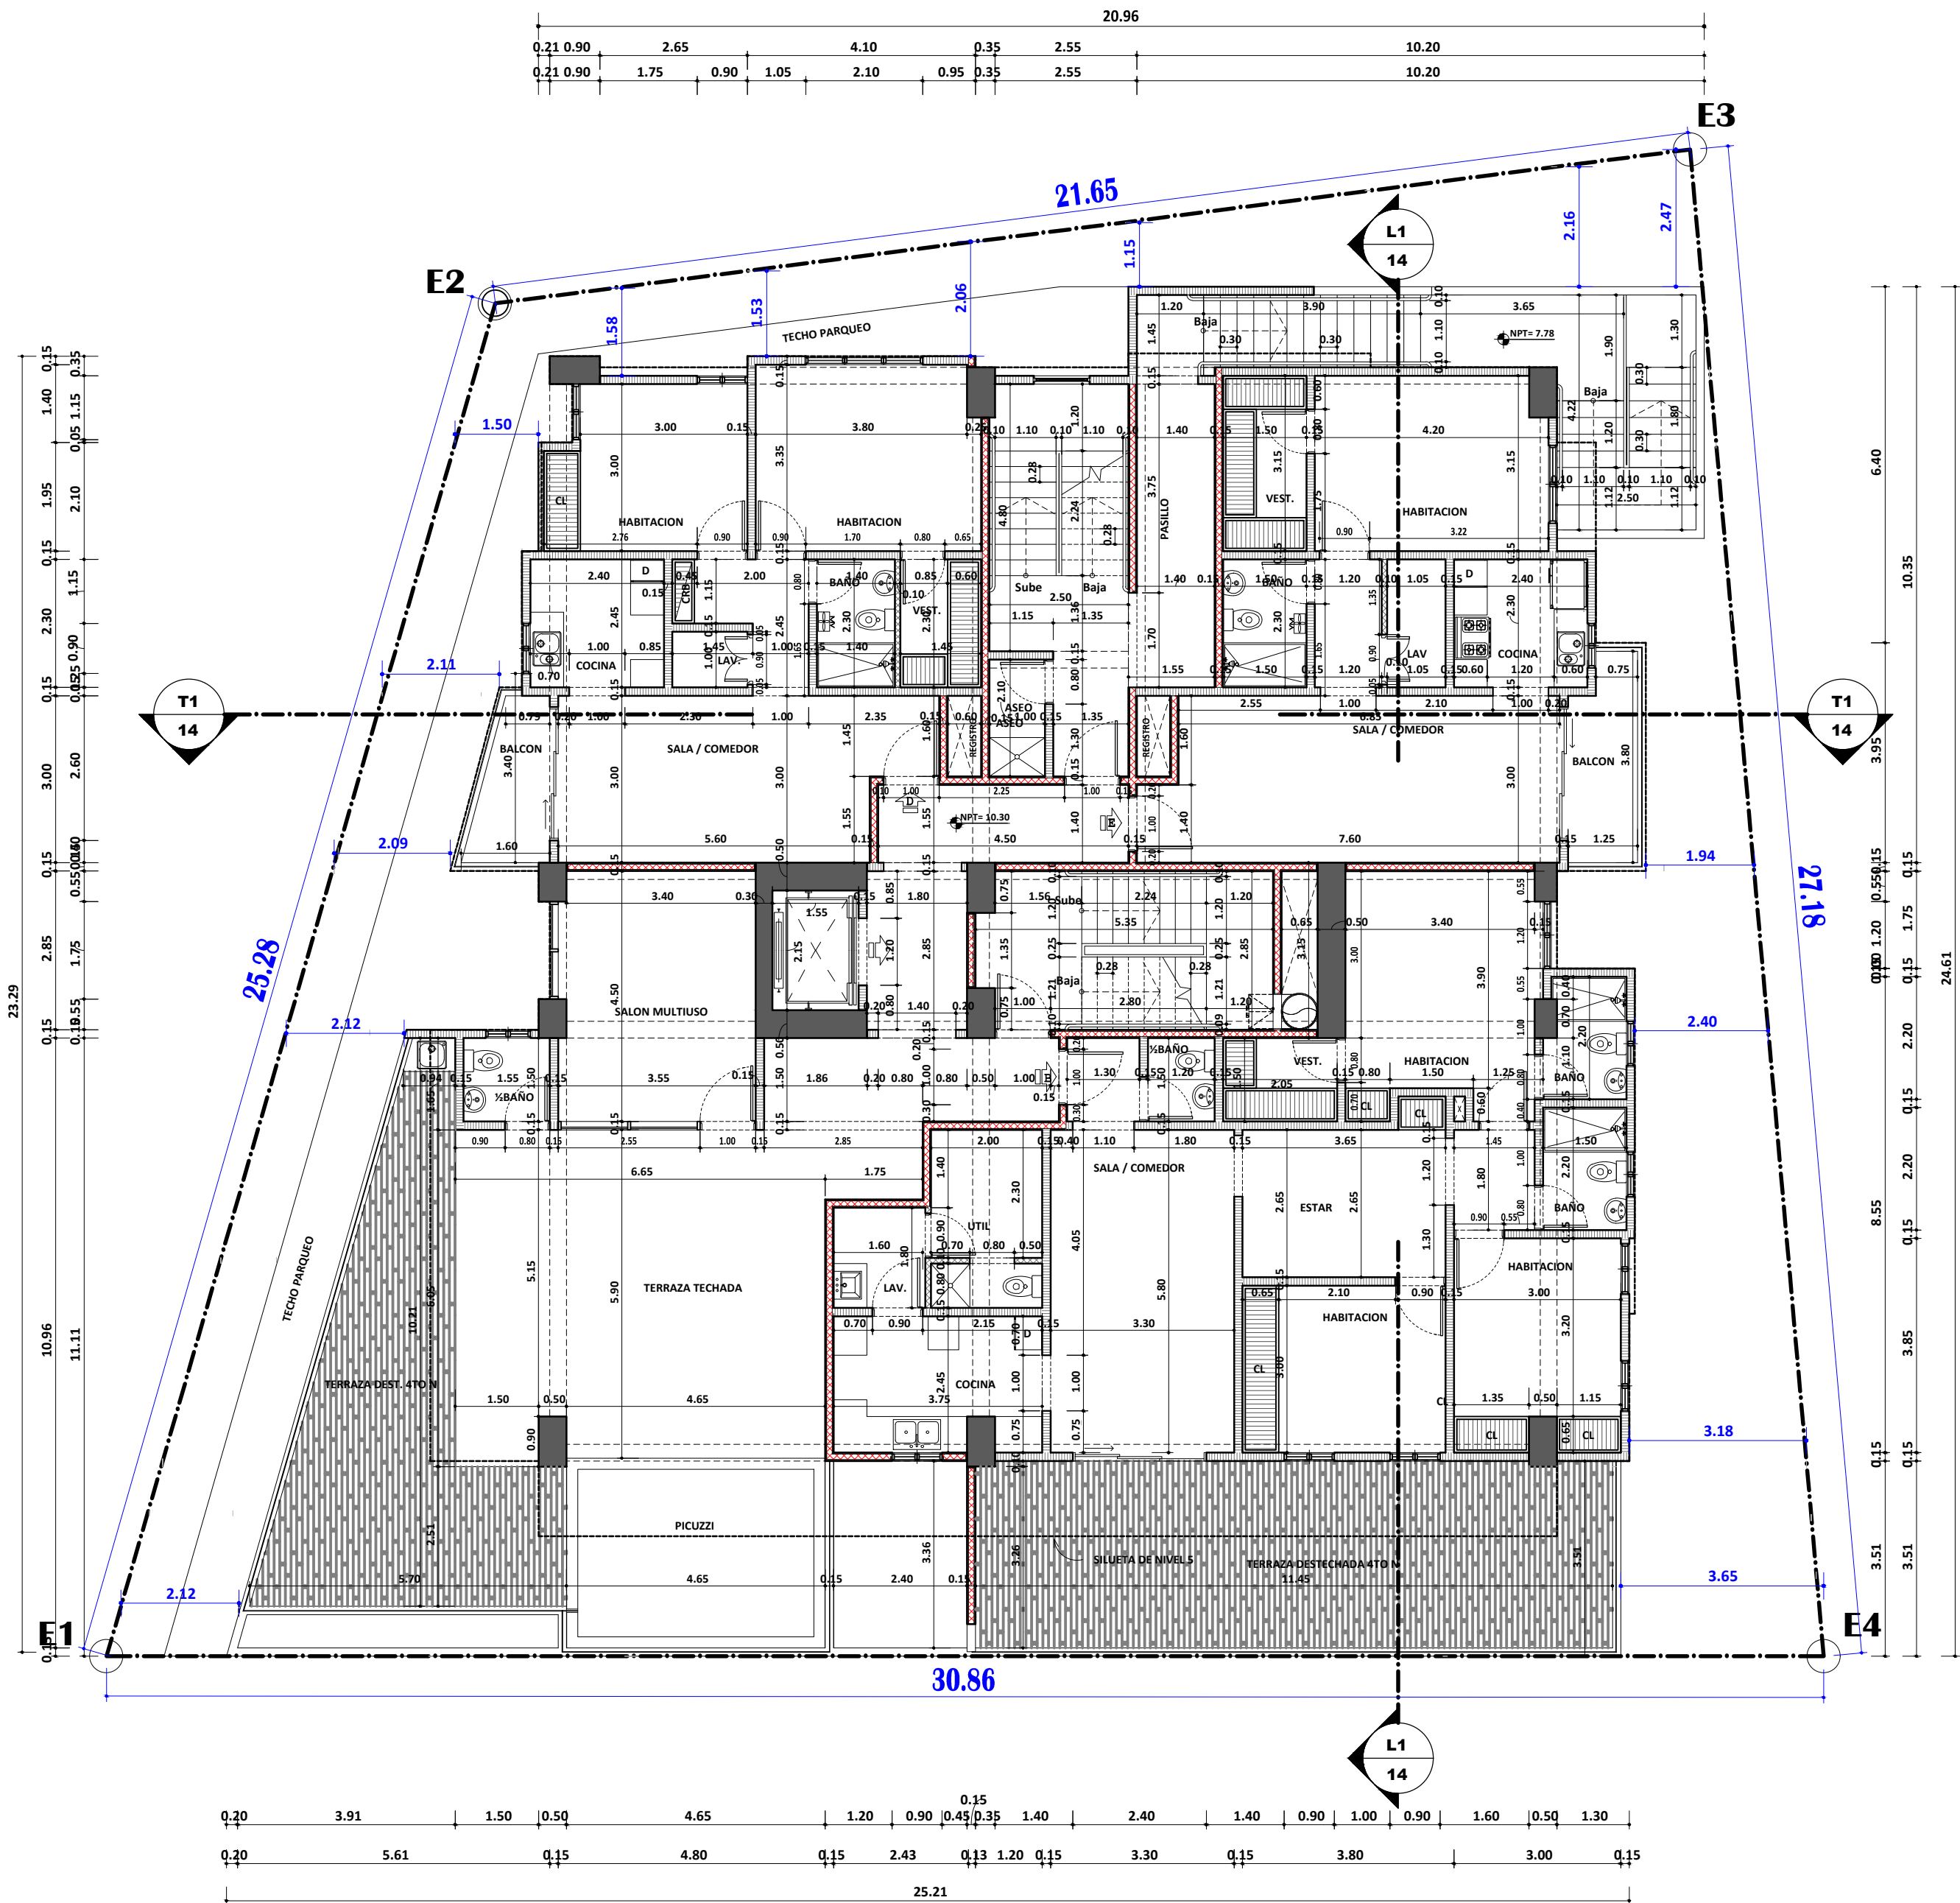




PLANTA ARQ. DIMENSIONADA NIVEL 4

ESCALA 1:100

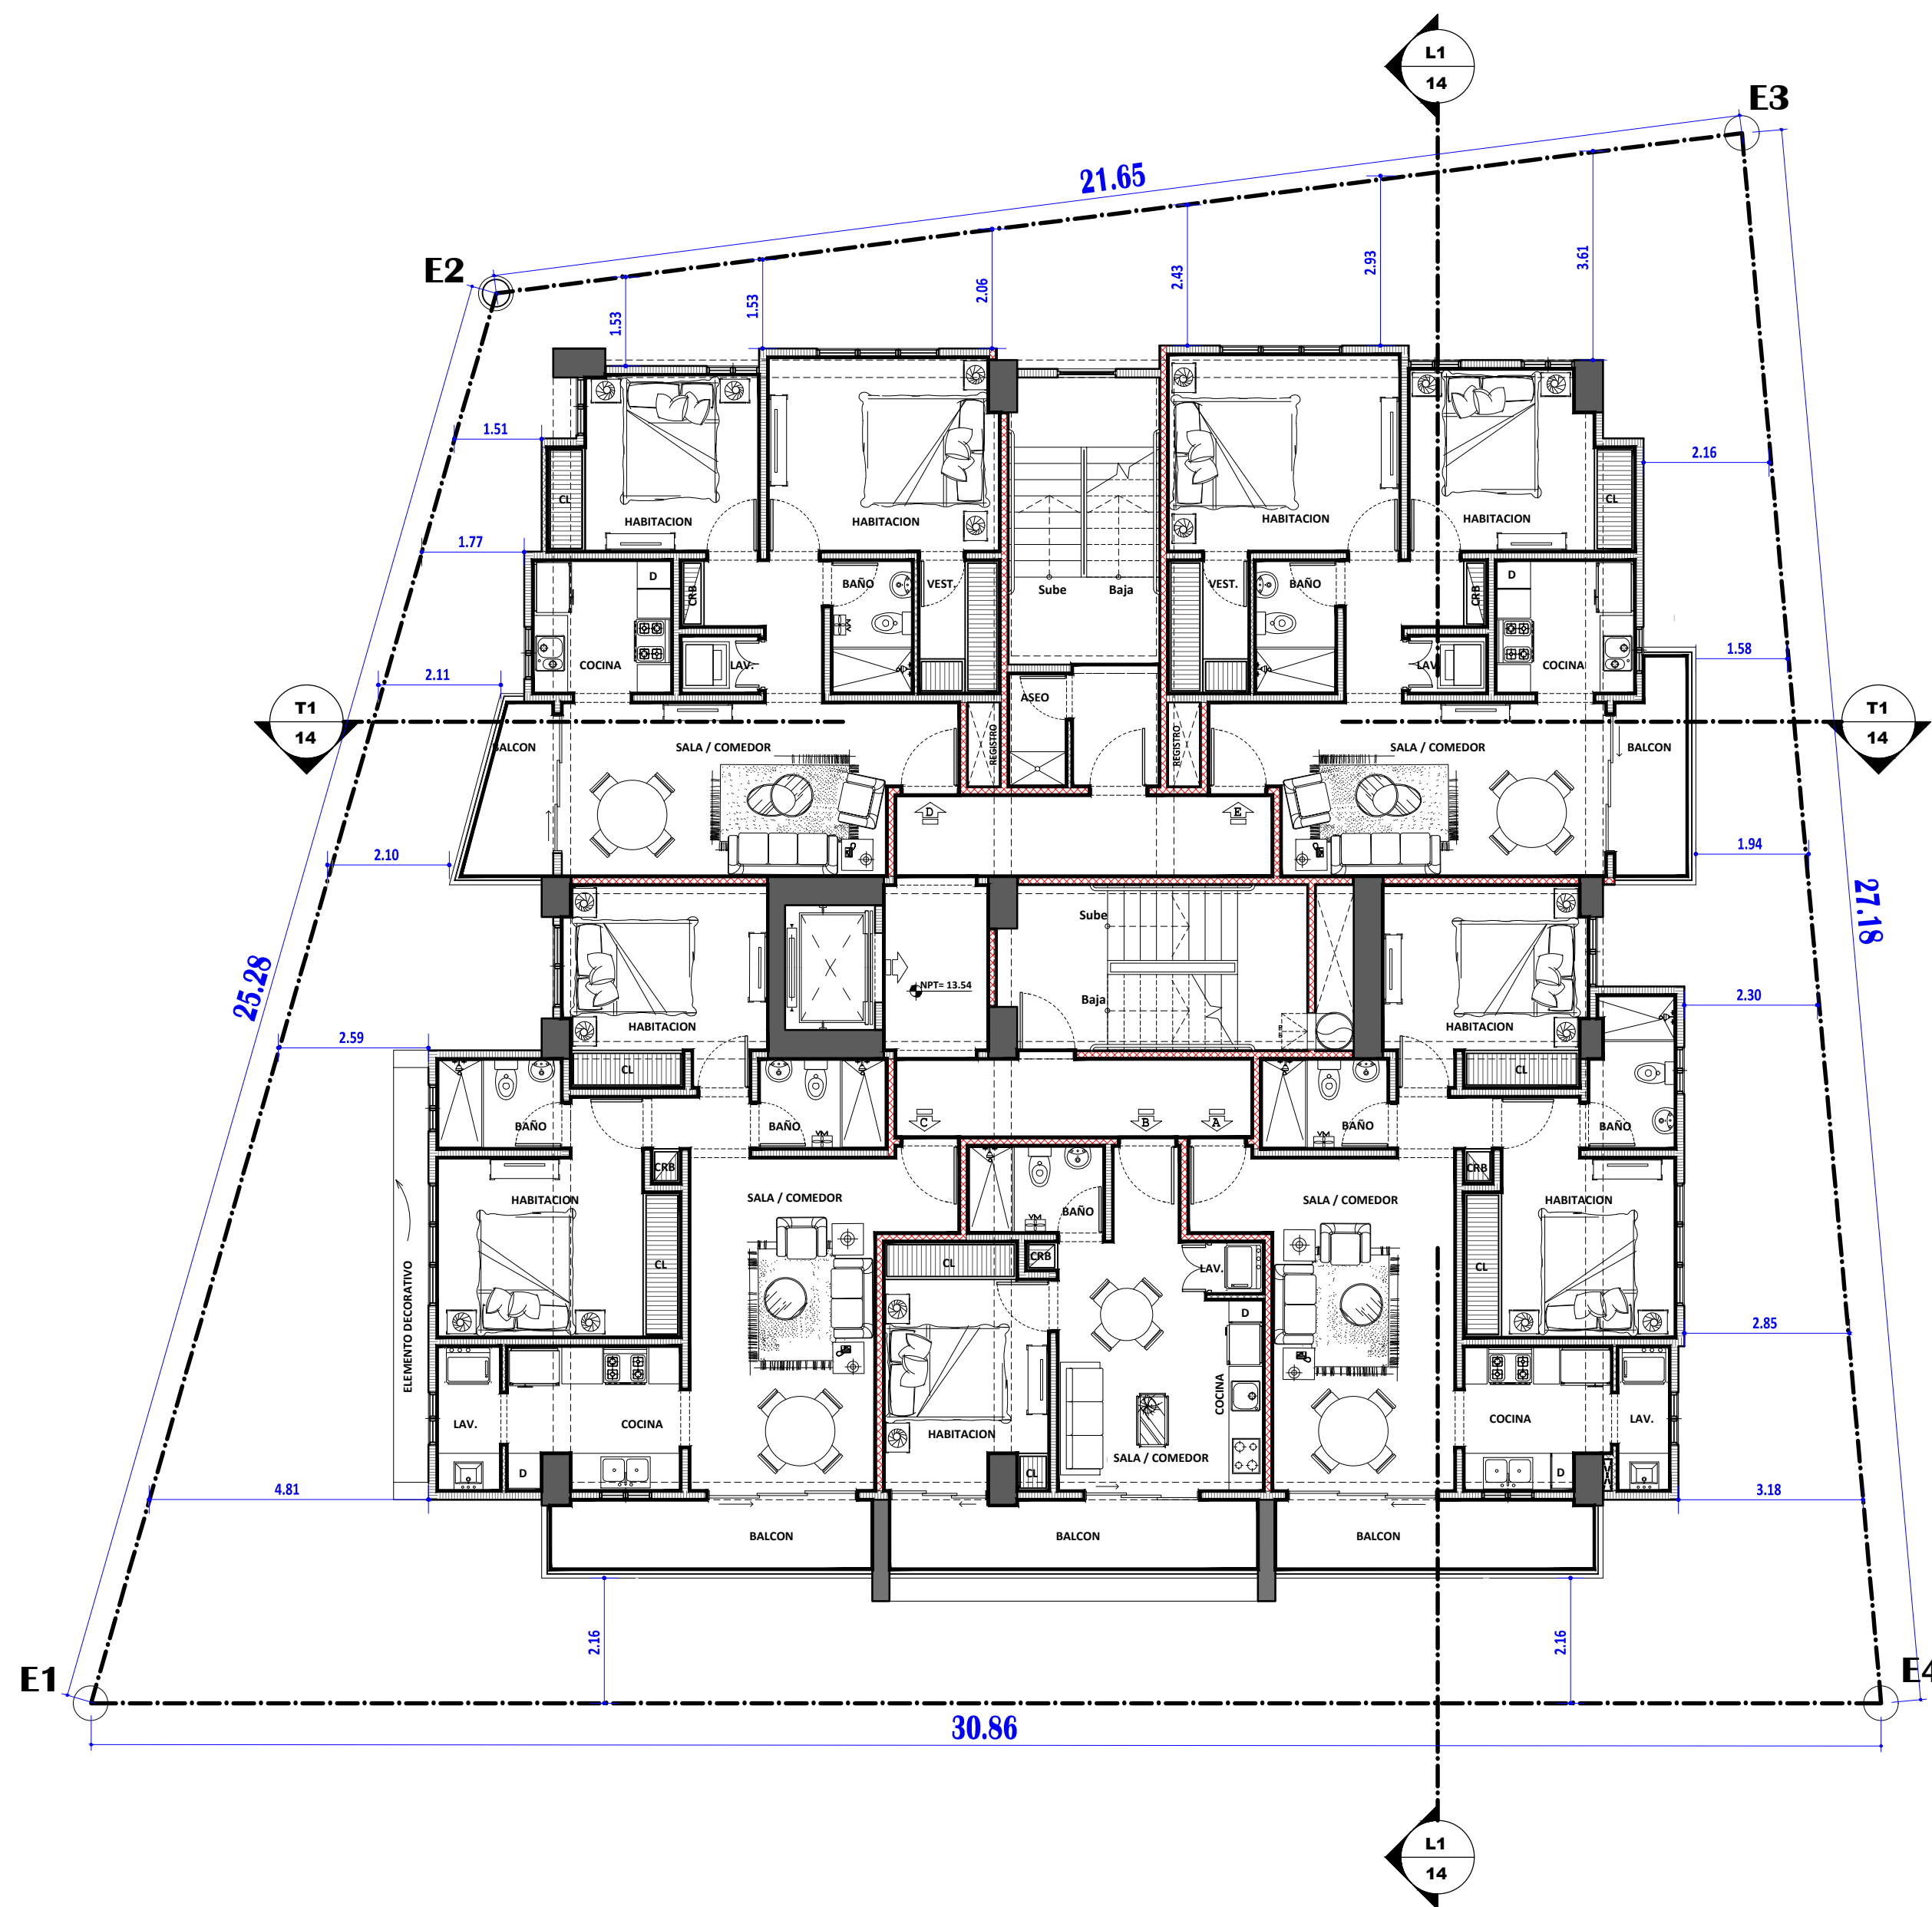

PLANTA ARQ. AMUEBLADA NIVELES TIPO 5-8


ESCALA 1:100

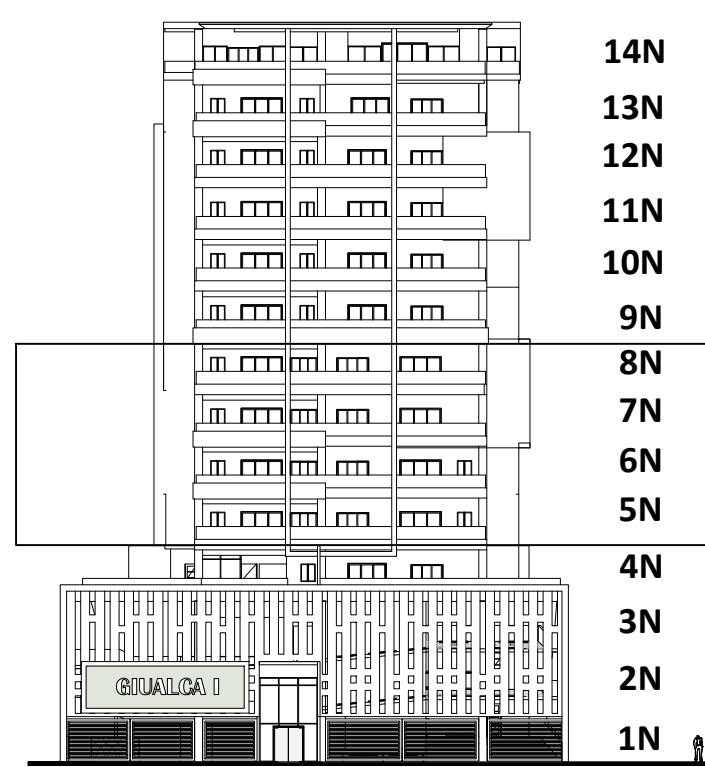 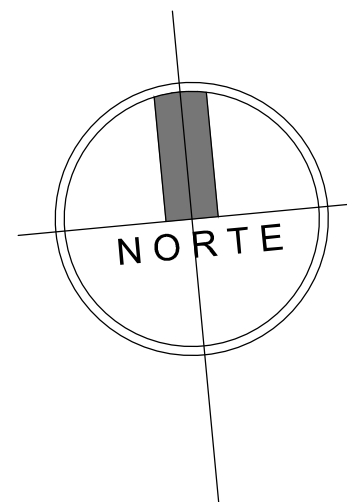

NPT	
NIVEL	NPT
Semi Sotano	-1.40
Nivel 1	0.00
Nivel 2	3.05
Nivel 3	5.60
Nivel 4	10.30
Nivel 5	13.54
Nivel 6	16.78
Nivel 7	20.02
Nivel 8	23.26
Nivel 9	26.50
Nivel 10	29.74
Nivel 11	32.98
Nivel 12	36.22
Nivel 13	39.46
Nivel 14	42.70
Techo	45.94


TABLA DE MUROS

	MURO ESTR.
	MURO 0.15 M
	MURO 0.10 M
	MURO BAJO
	MURO RESISTENTE AL FUEGO 60 MIN.

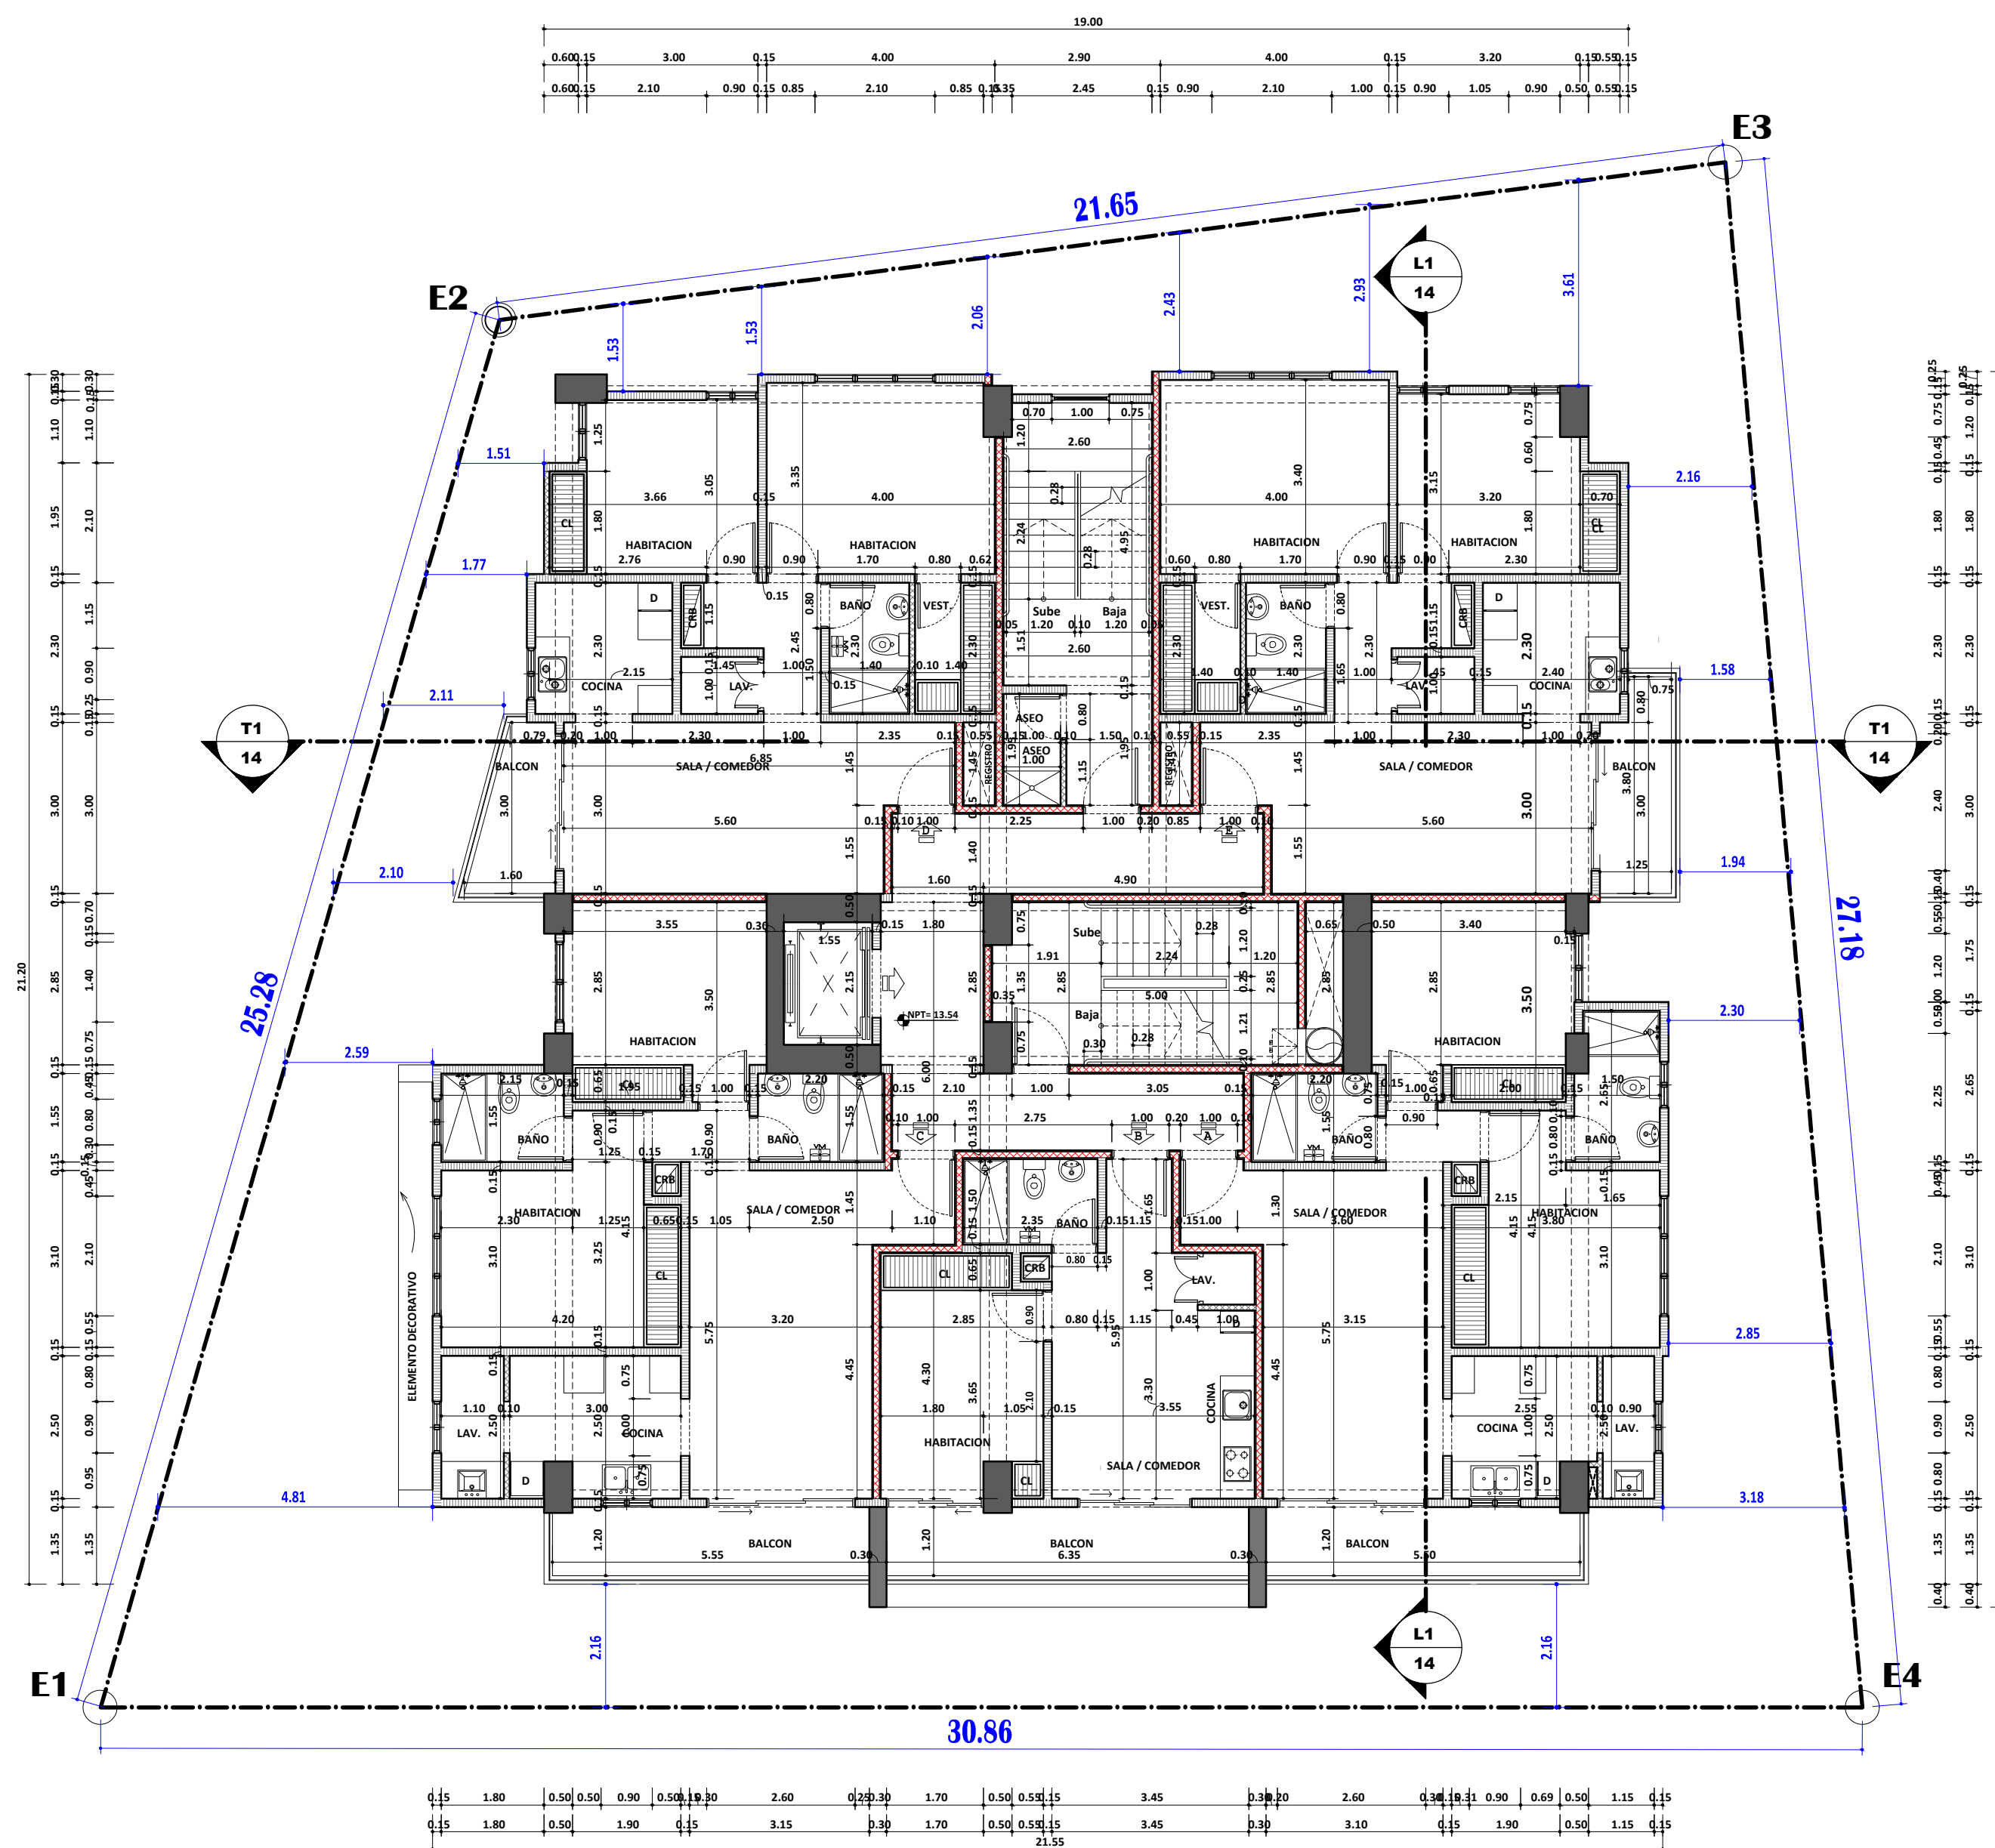

PLANTA ARQ. DIMENSIONADA NIVELES TIPO 5-8


ESCALA 1:100

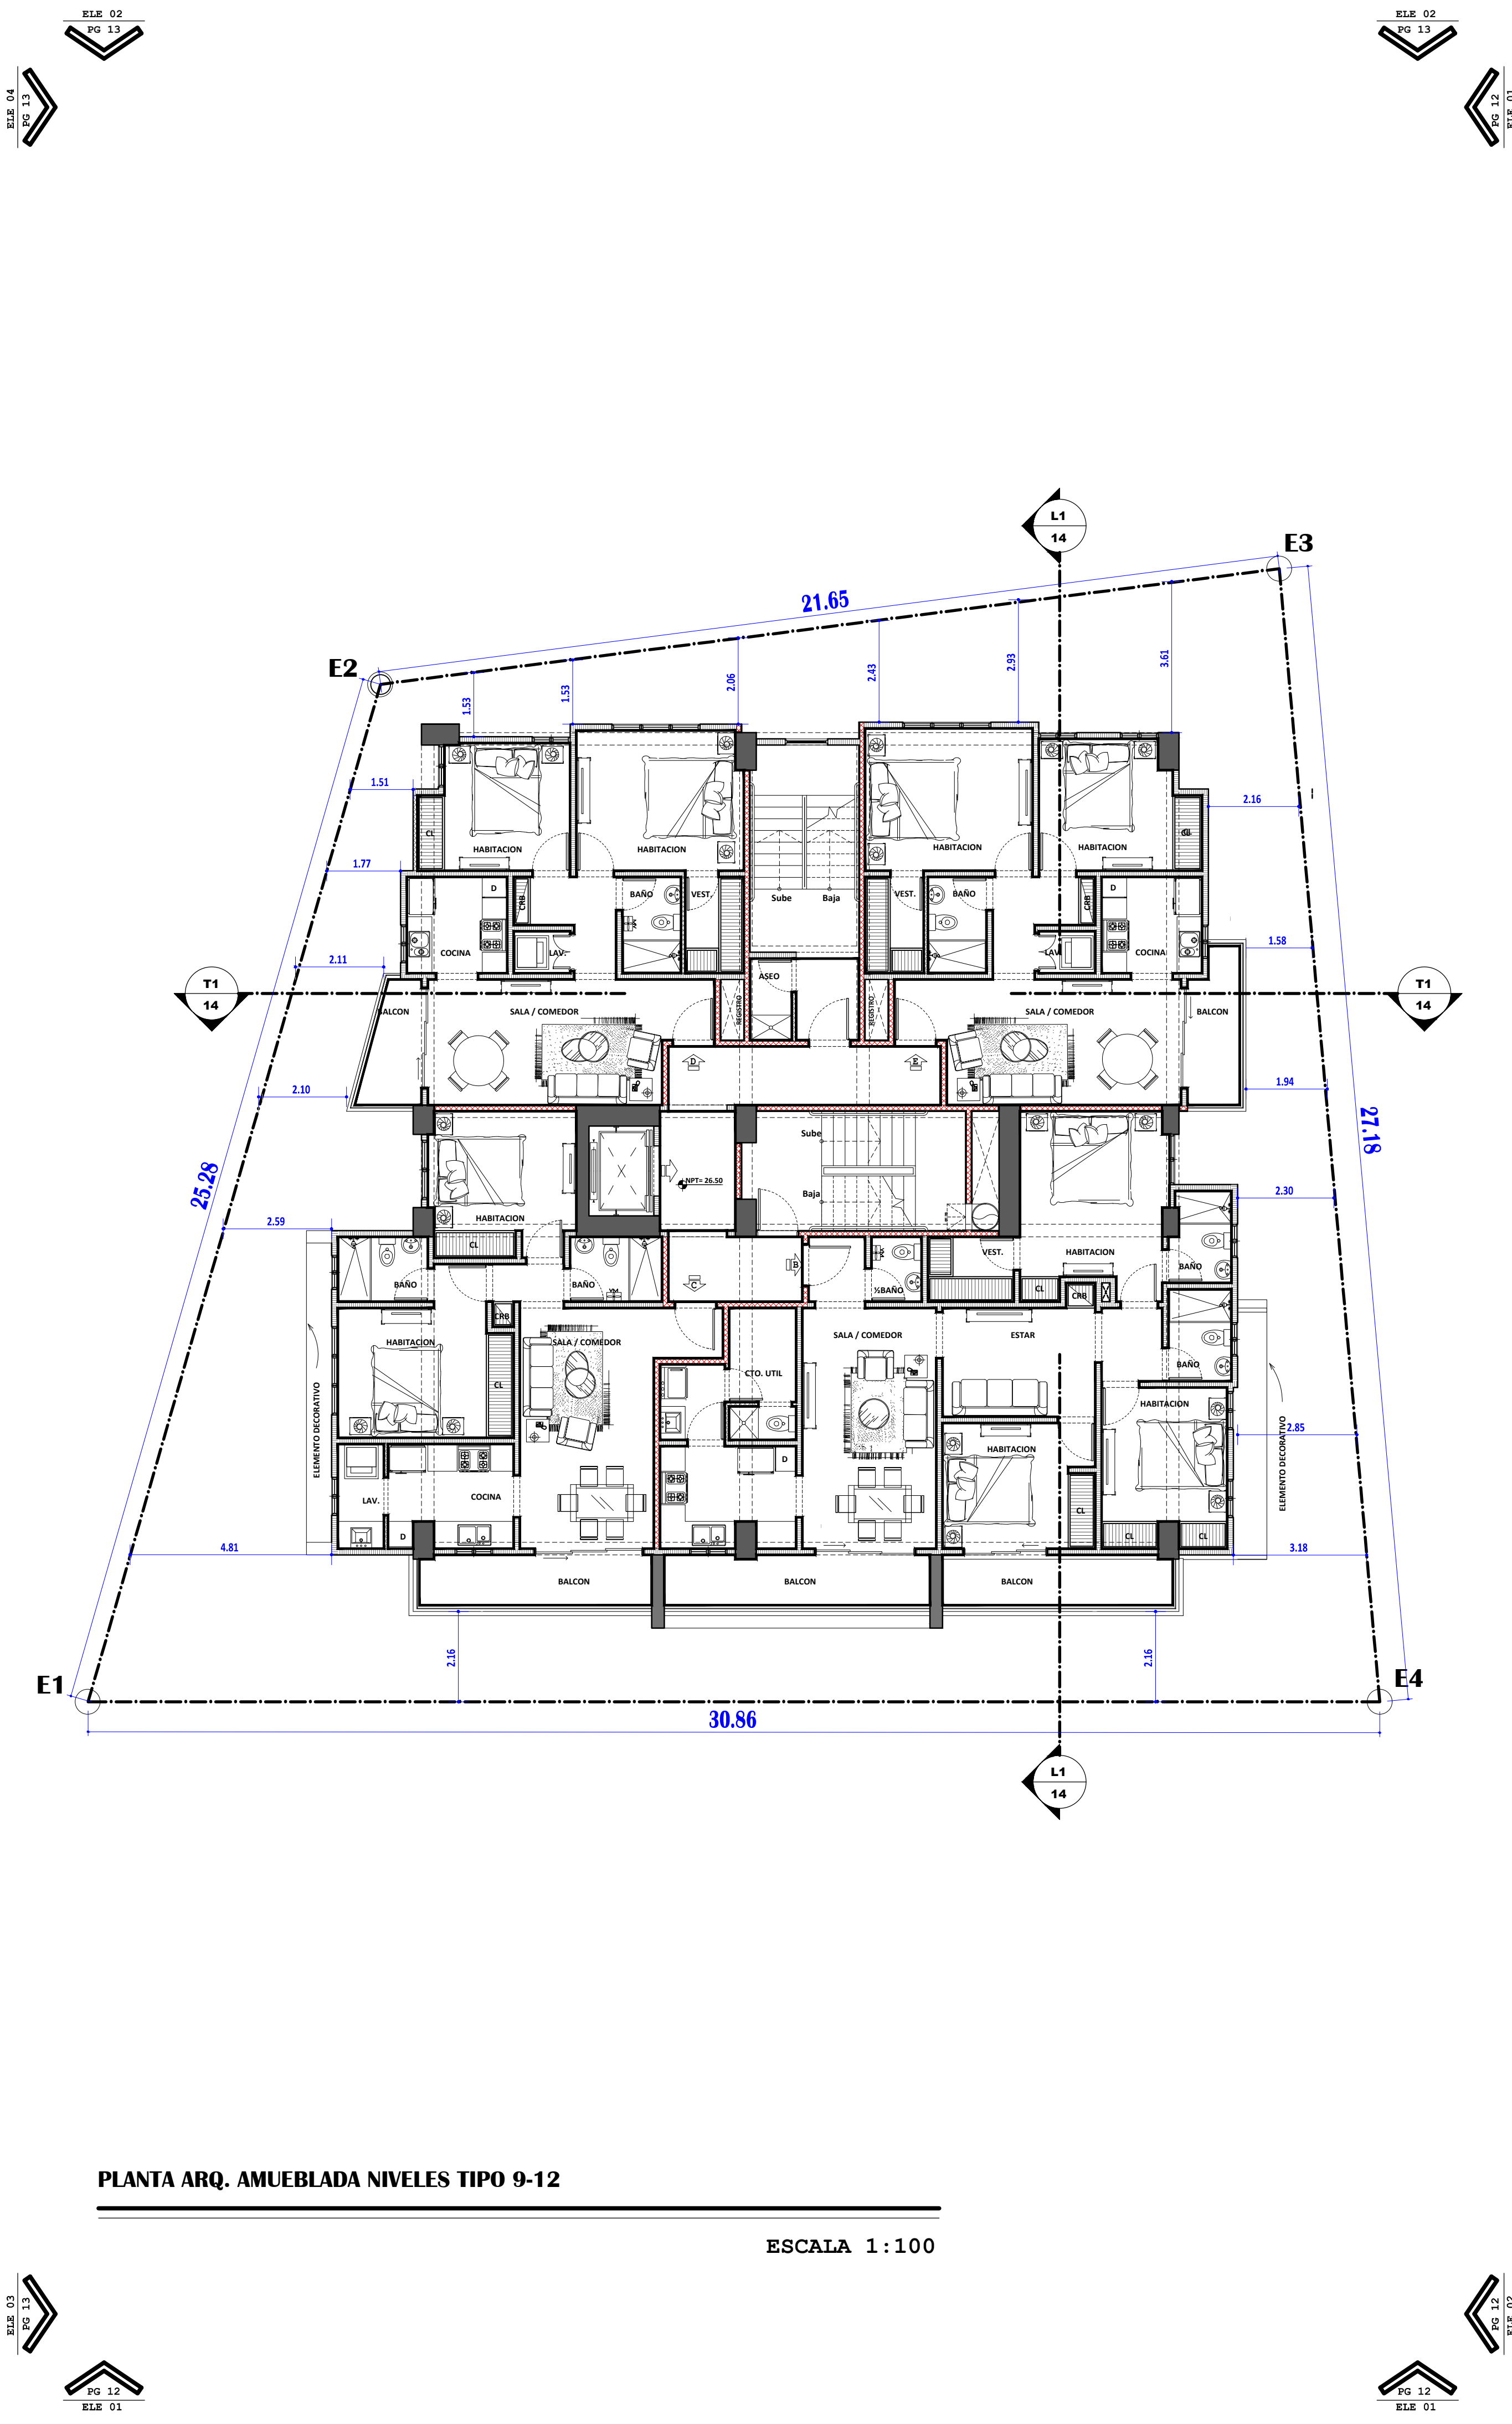


NORTE

NPT	
NIVEL	NPT
Semi Sotano	-1.40
Nivel 1	0.00
Nivel 2	3.05
Nivel 3	5.60
Nivel 4	10.30
Nivel 5	13.54
Nivel 6	16.78
Nivel 7	20.02
Nivel 8	23.26
Nivel 9	26.50
Nivel 10	29.74
Nivel 11	32.98
Nivel 12	36.22
Nivel 13	39.46
Nivel 14	42.70
Techo	45.94



TABLA DE MUROS	
	MURO ESTR.
	MURO 0.15 M
	MURO 0.10 M
	MURO BAJO
	MURO RESISTENTE AL FUEGO 60 MIN.

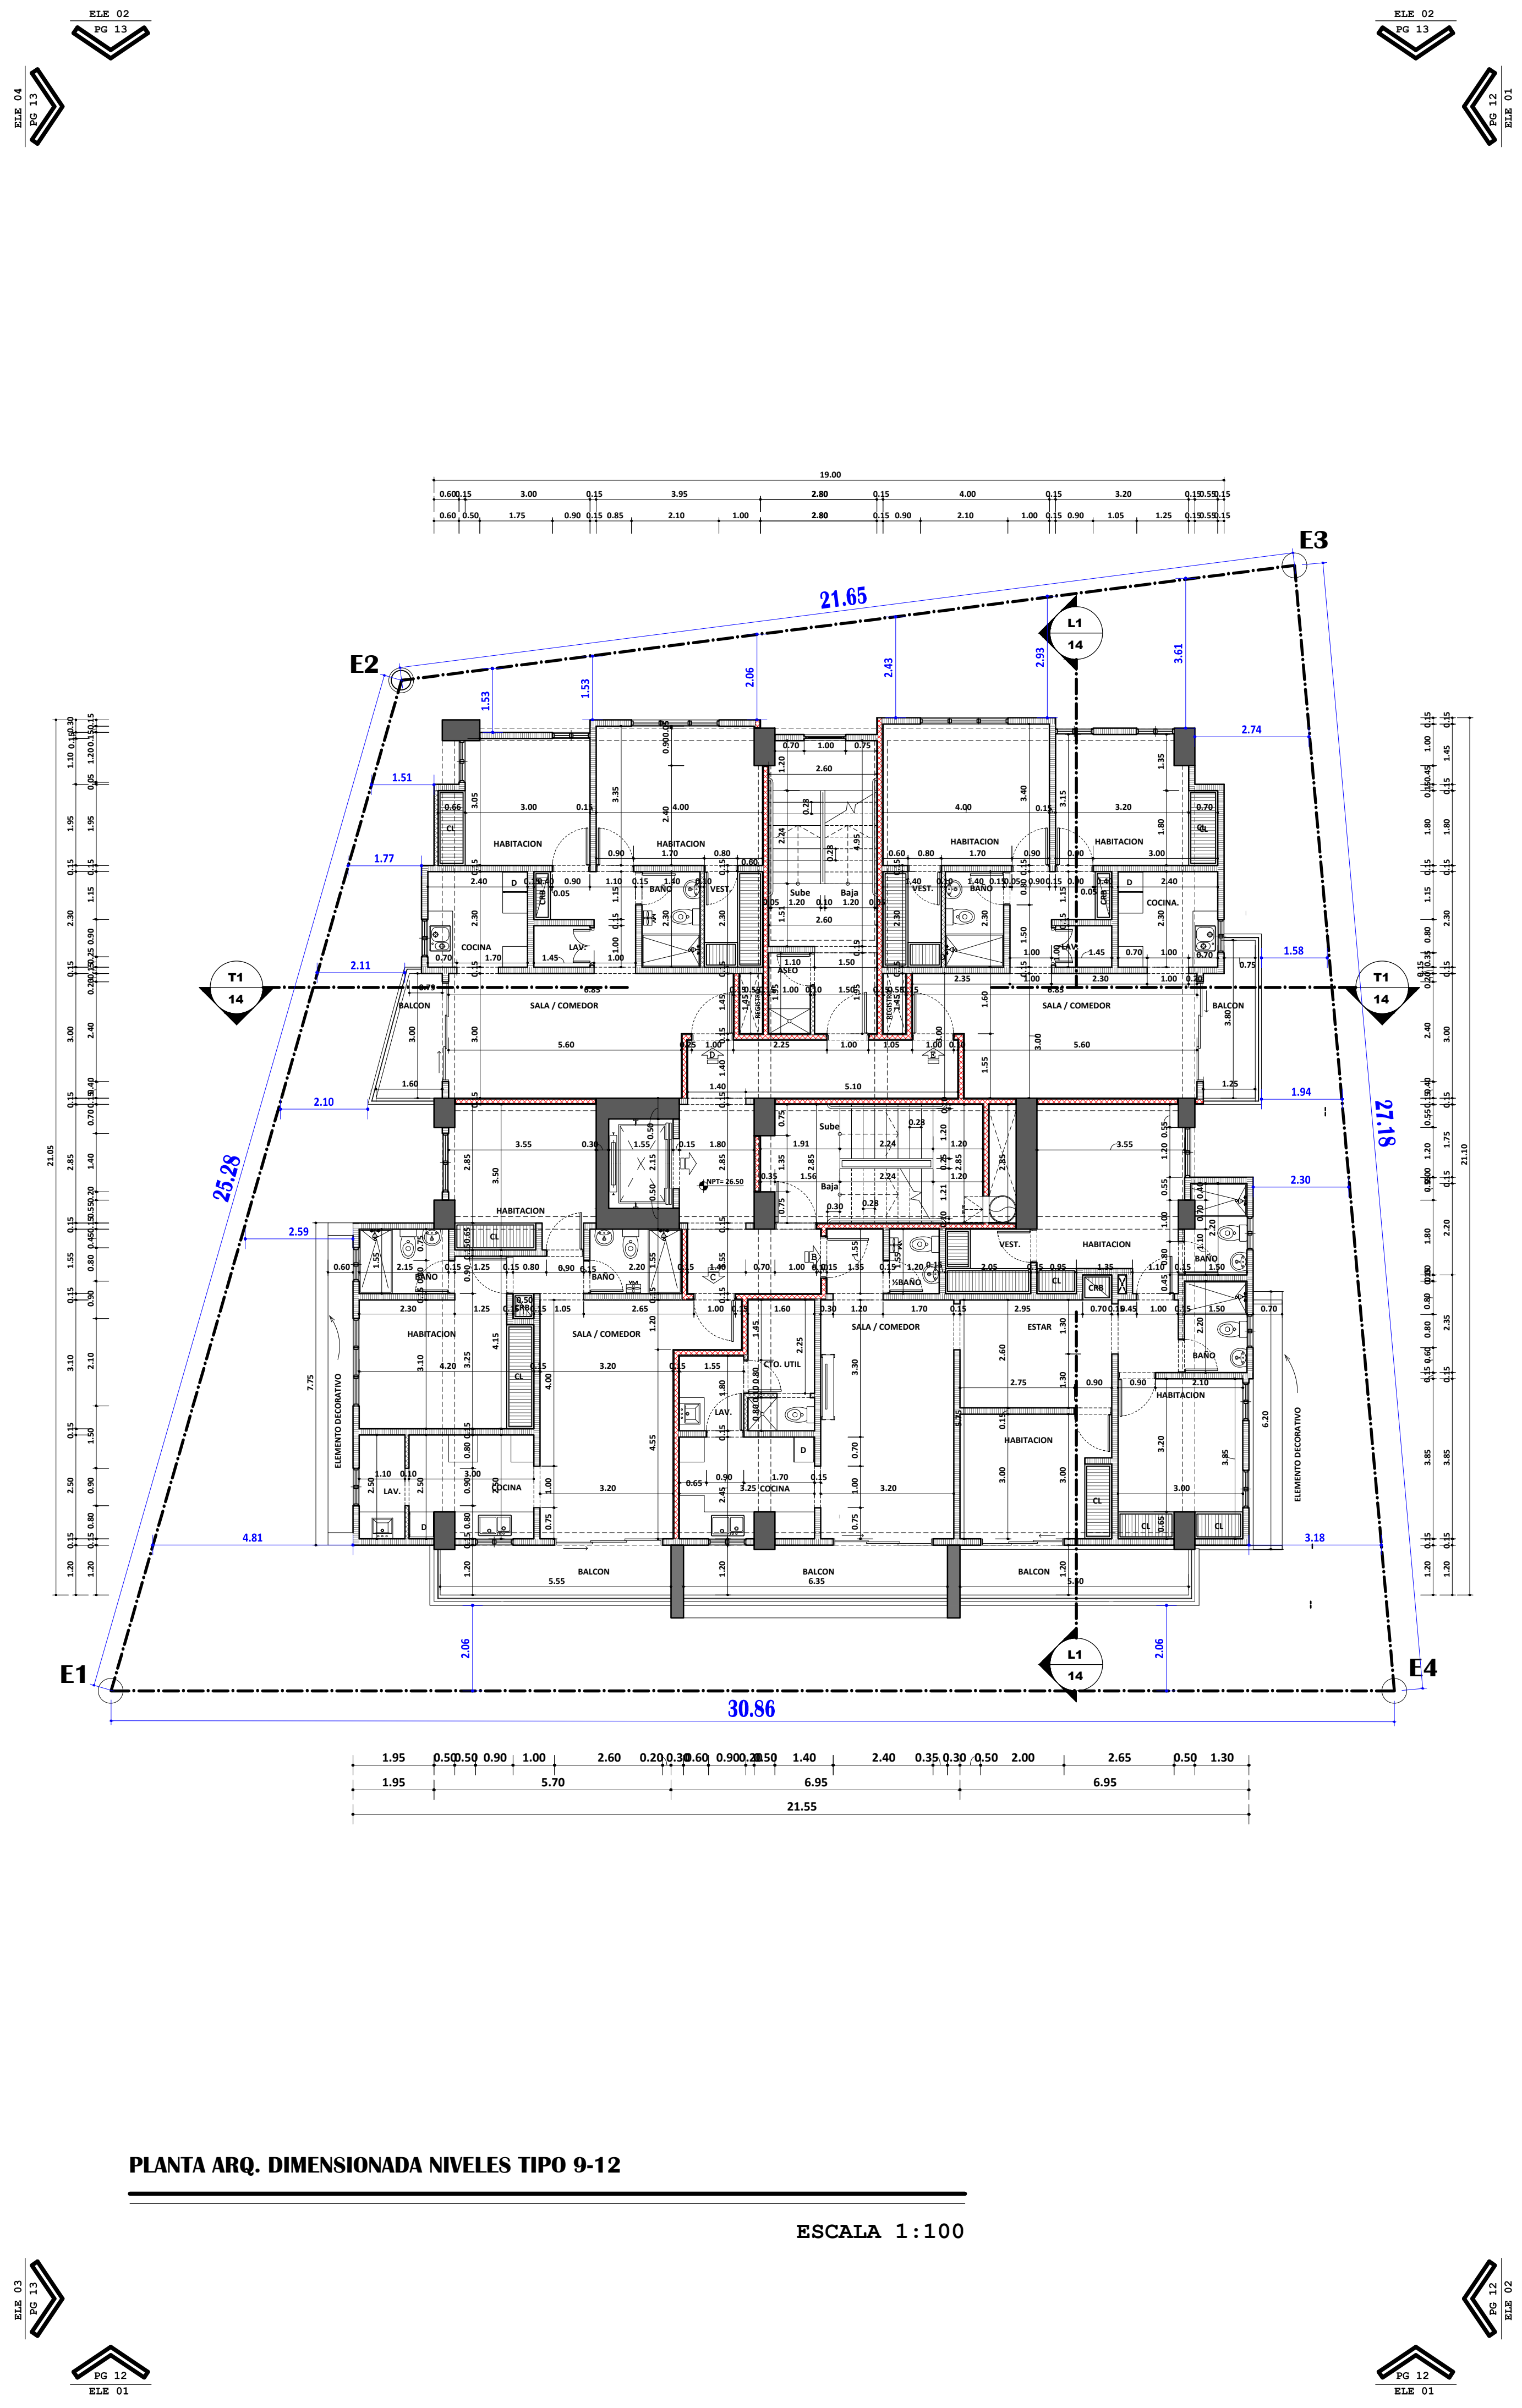

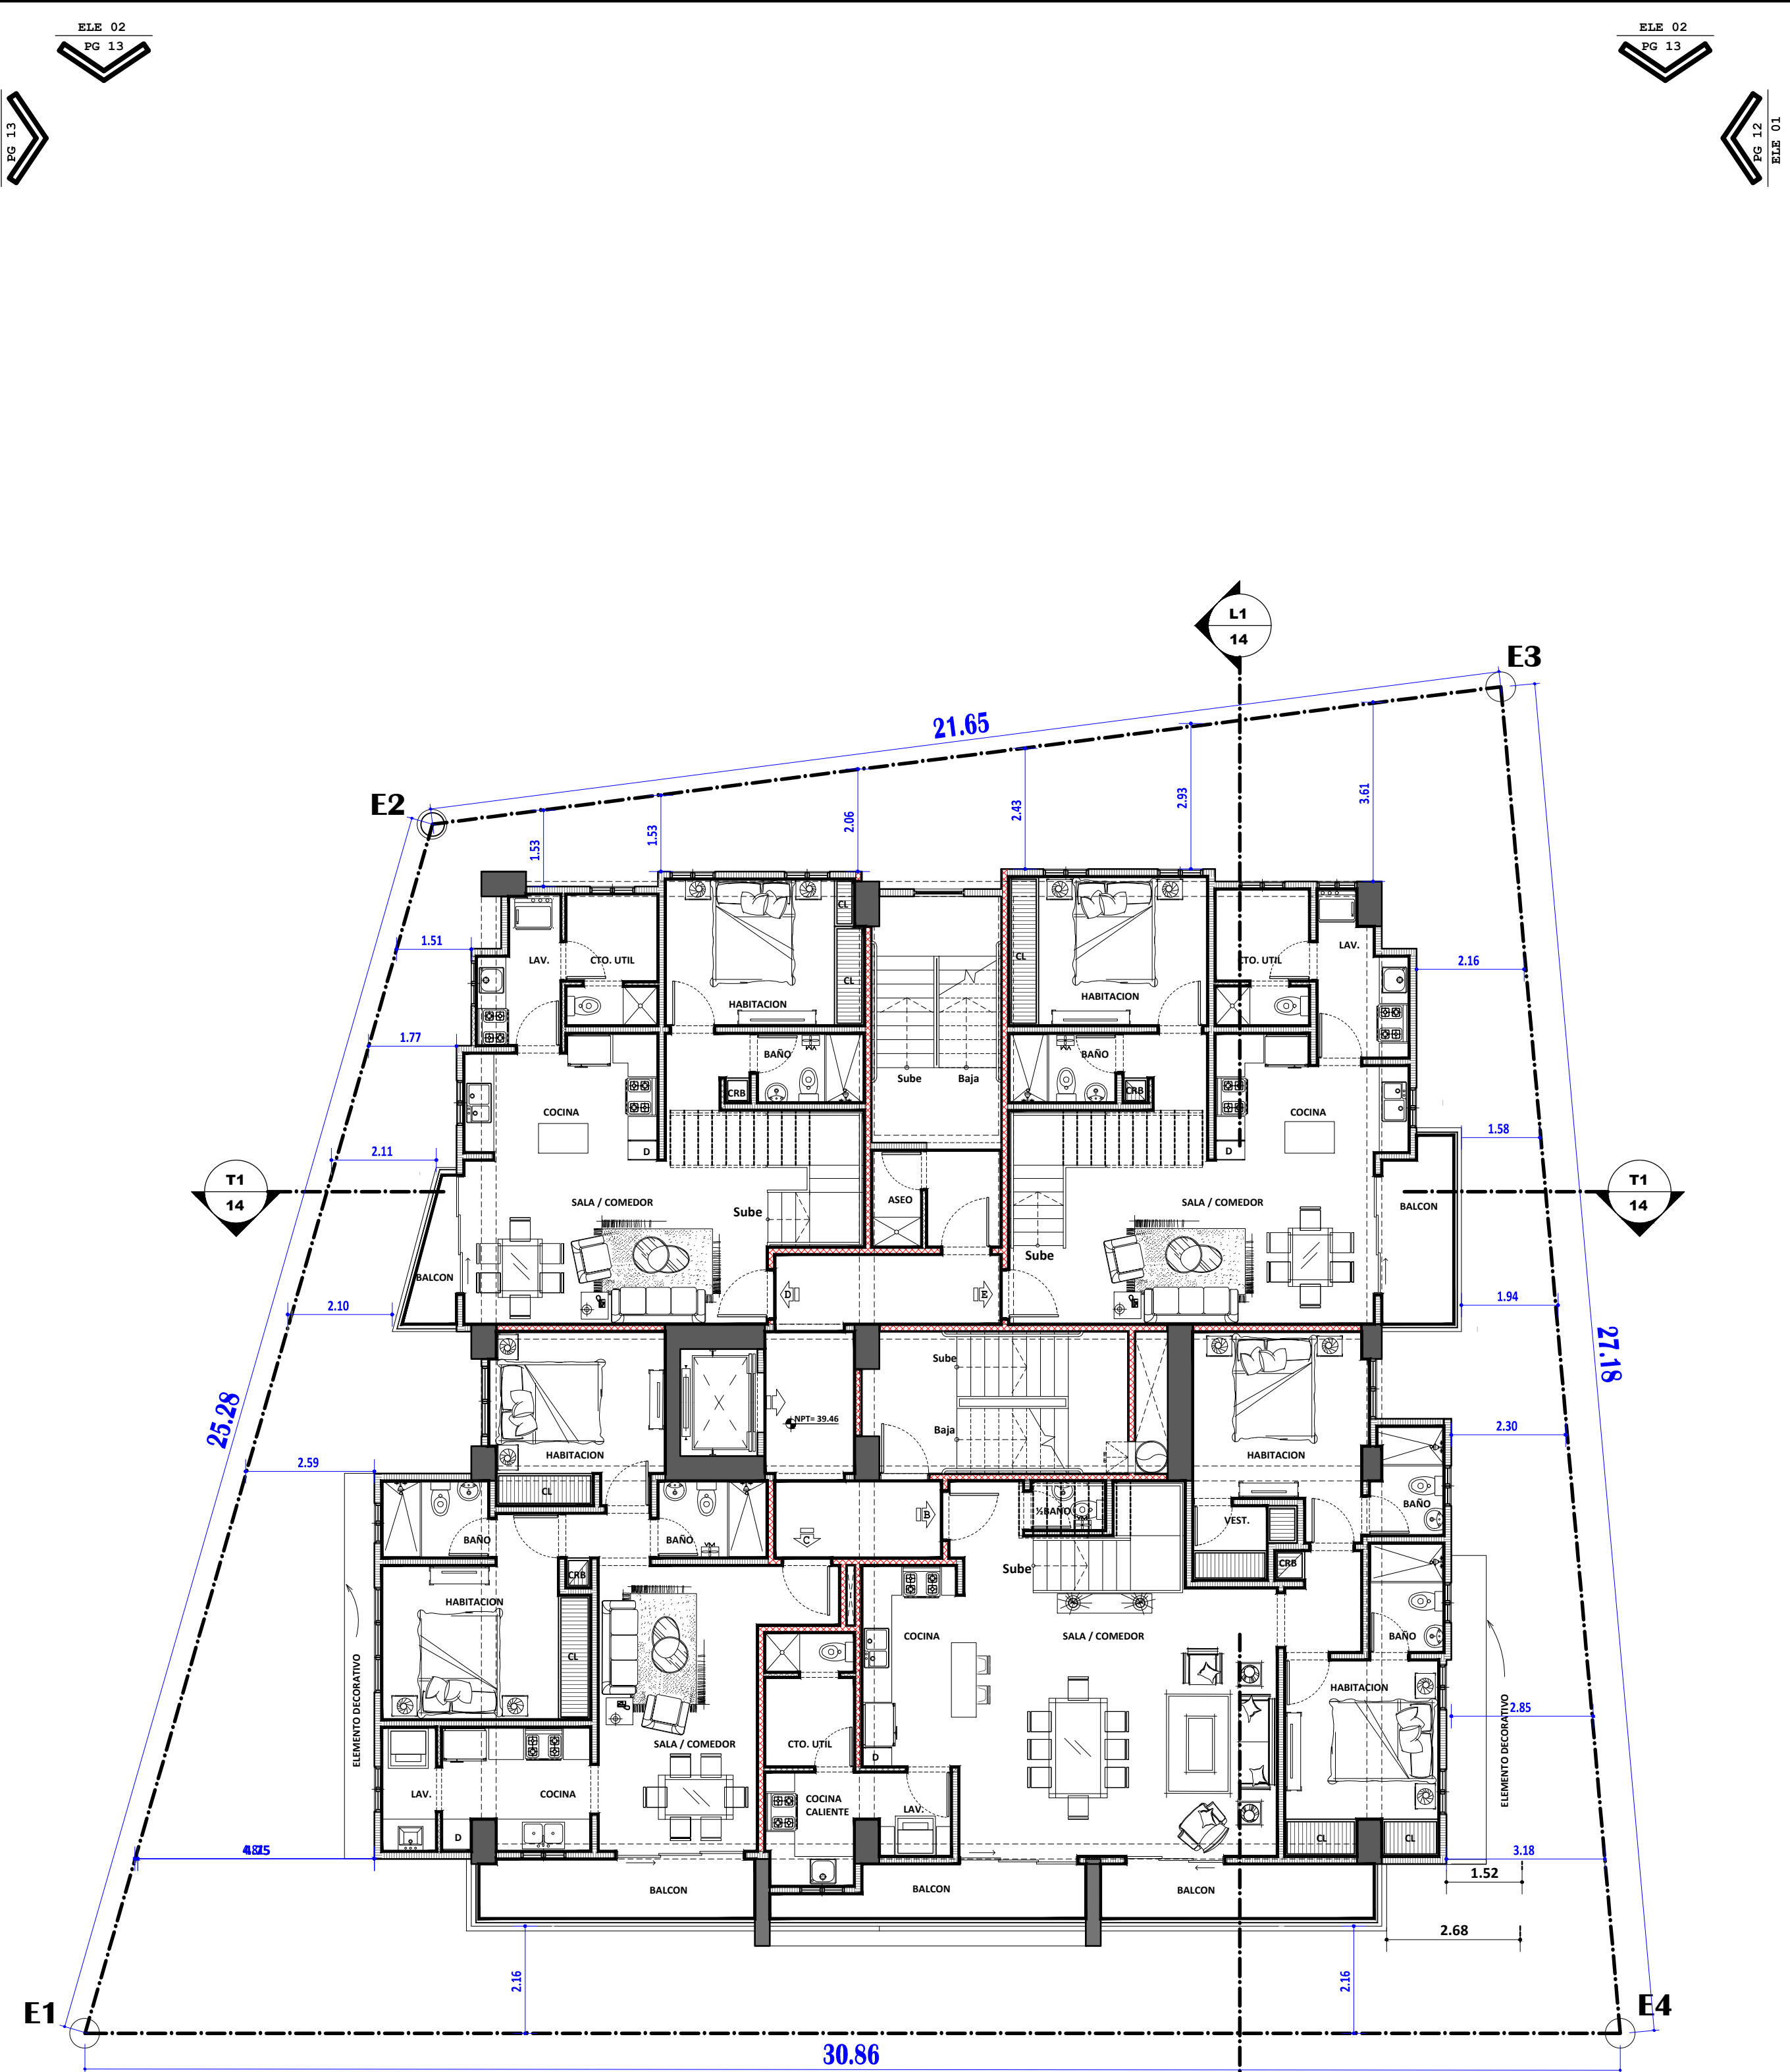

PLANTA ARQ. AMUEBLADA NIVEL 13 (1ER NIVEL DE PENTHOUSE)


ESCALA 1:100

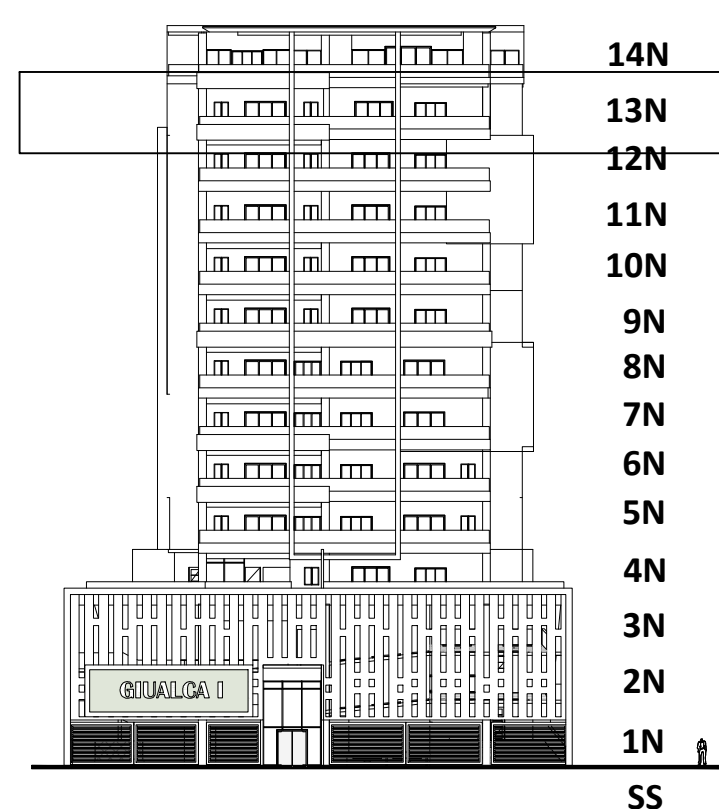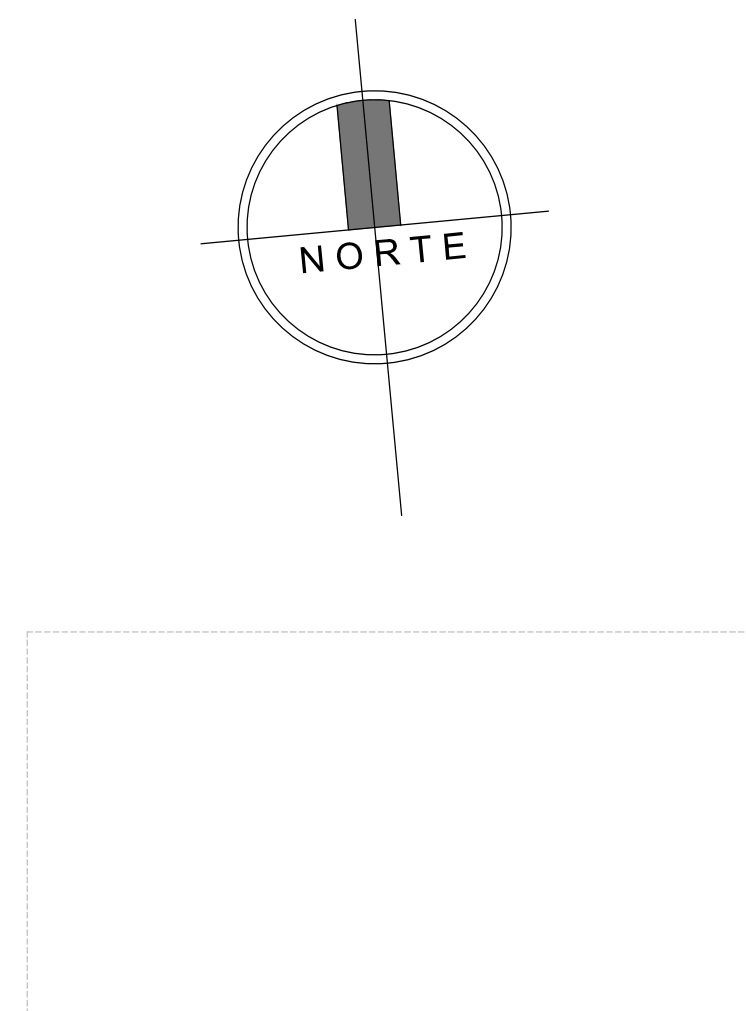

NPT	
NIVEL	NPT
Semi Sotano	-1.40
Nivel 1	0.00
Nivel 2	3.05
Nivel 3	5.60
Nivel 4	10.30
Nivel 5	13.54
Nivel 6	16.78
Nivel 7	20.02
Nivel 8	23.26
Nivel 9	26.50
Nivel 10	29.74
Nivel 11	32.98
Nivel 12	36.22
Nivel 13	39.46
Nivel 14	42.70
Techo	45.94




TABLA DE MUROS

	MURO ESTR.
	MURO 0.15 M
	MURO 0.10 M
	MURO BAJO
	MURO RESISTENTE AL FUEGO 60 MIN.

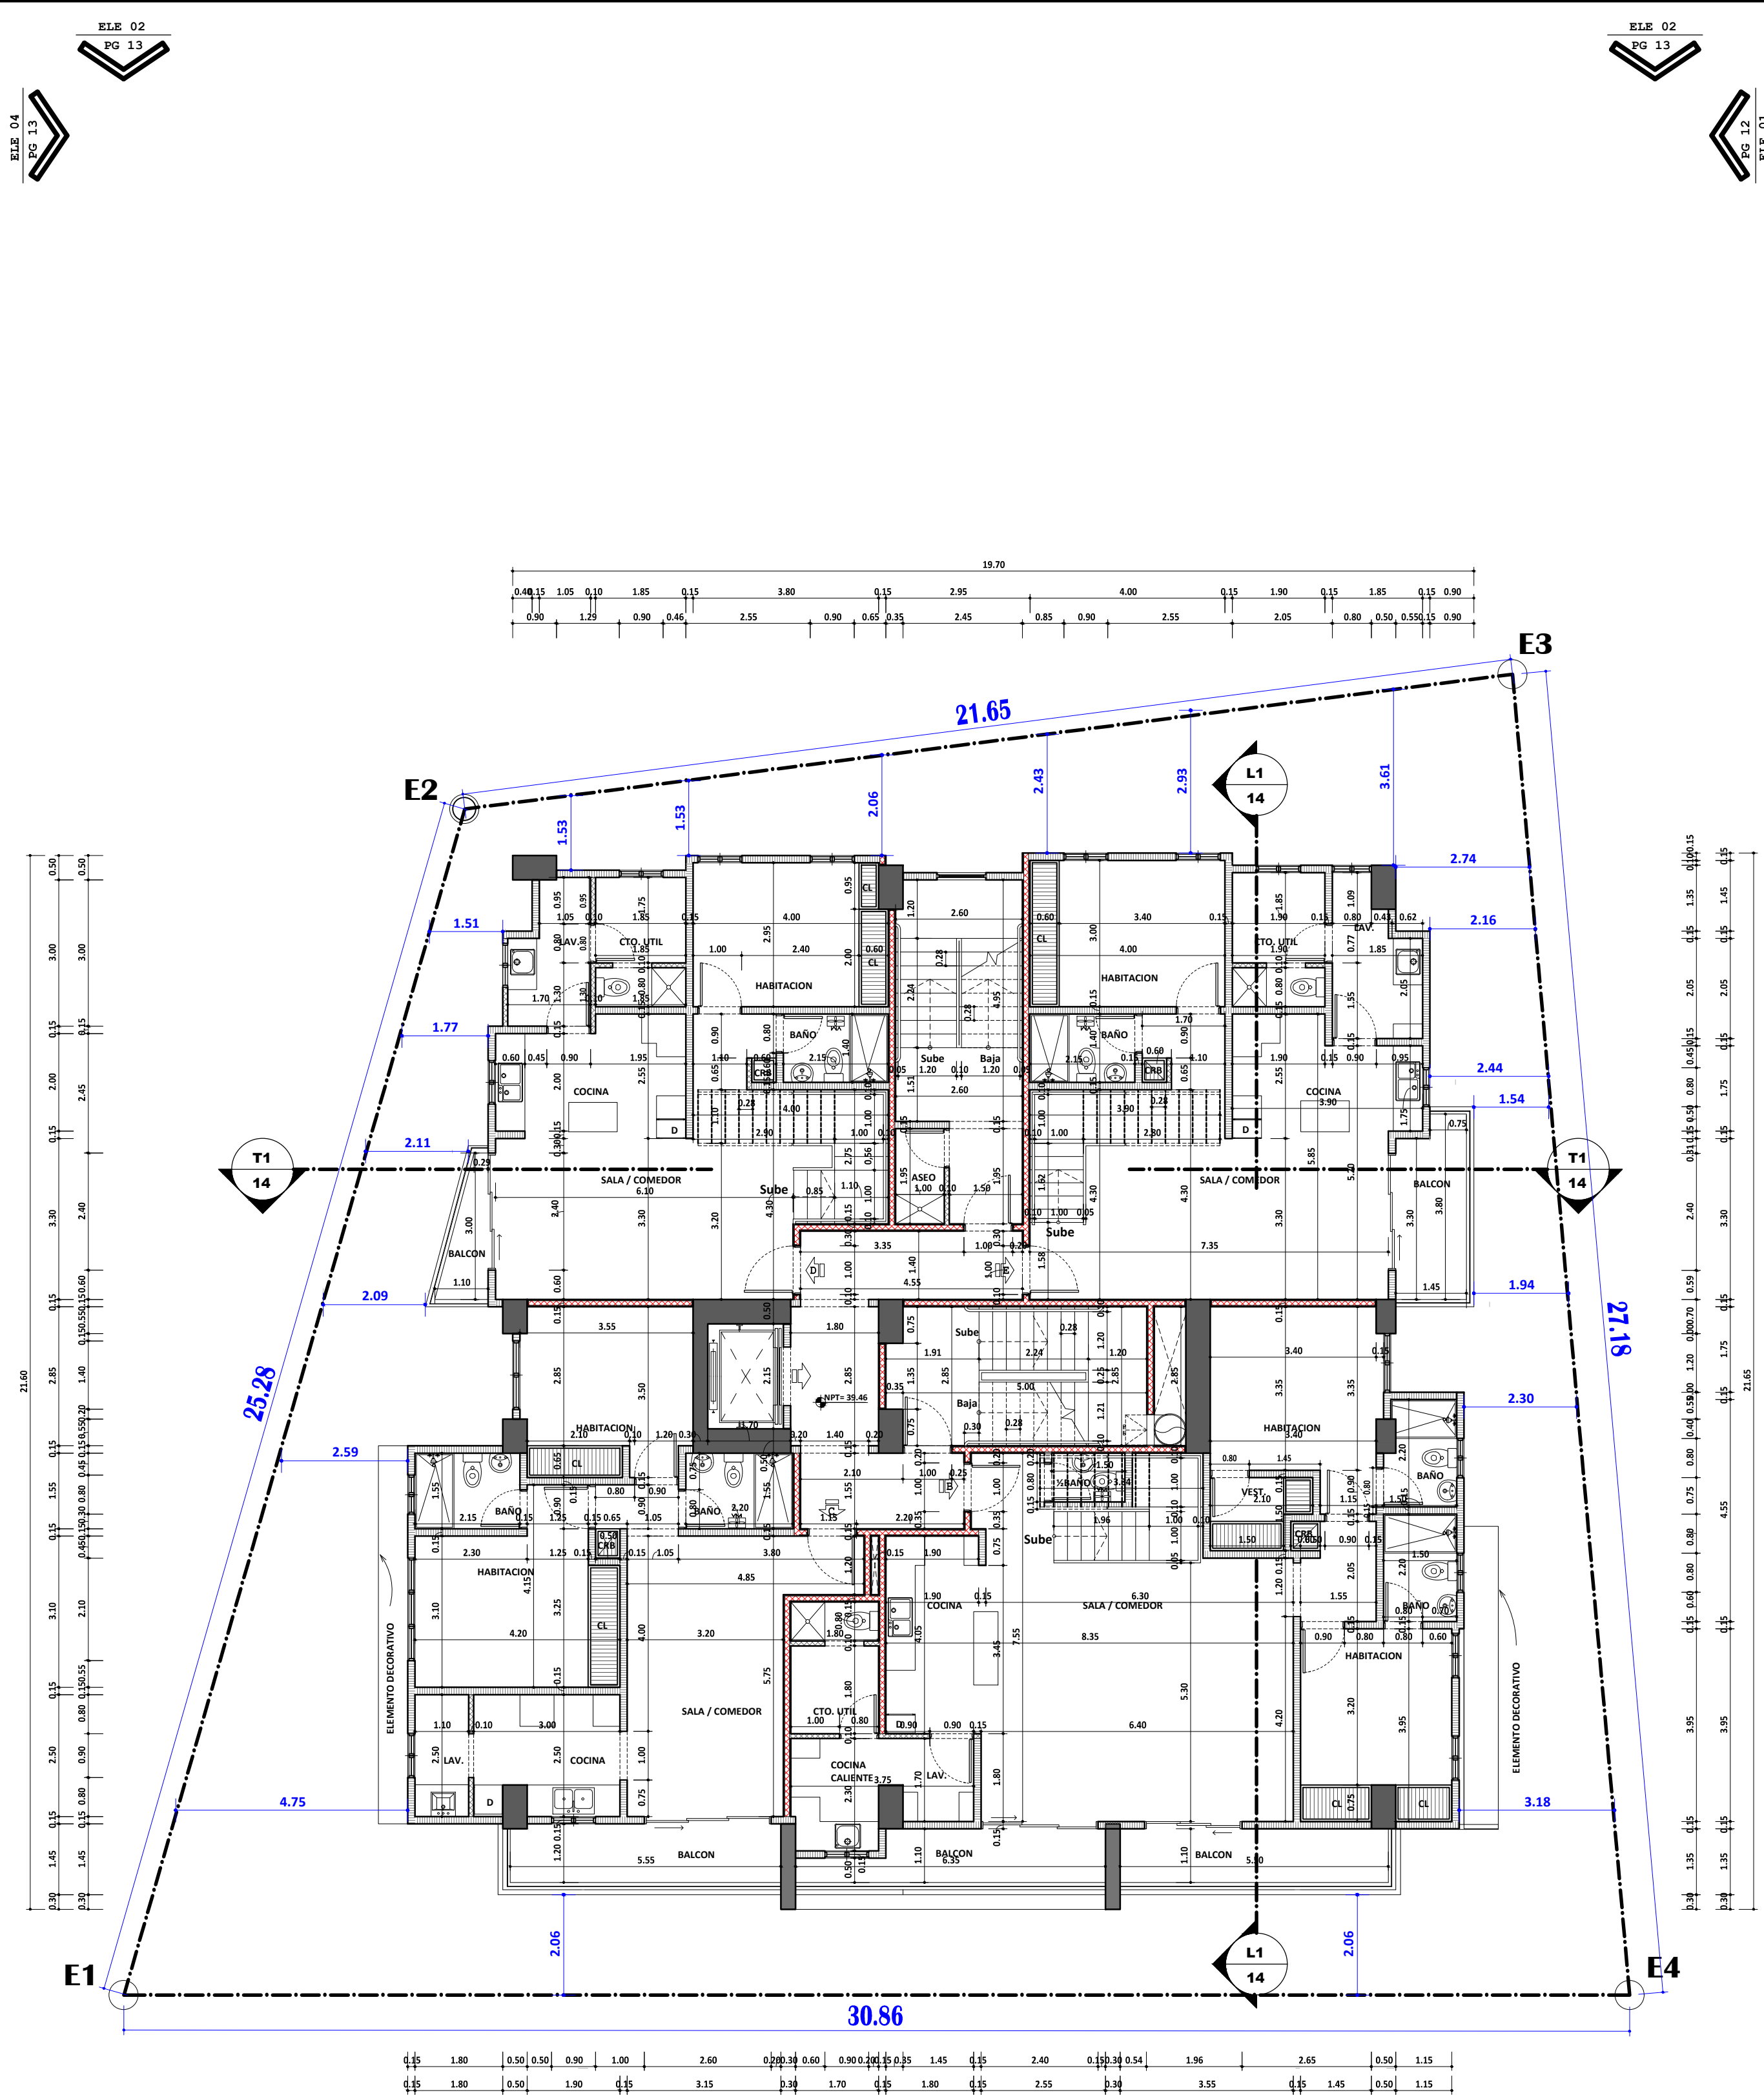

PLANTA ARQ. DIMENSIONADA NIVEL 13 TIPO (1ER NIVEL DE PENTHOUSE)


ESCALA 1:100

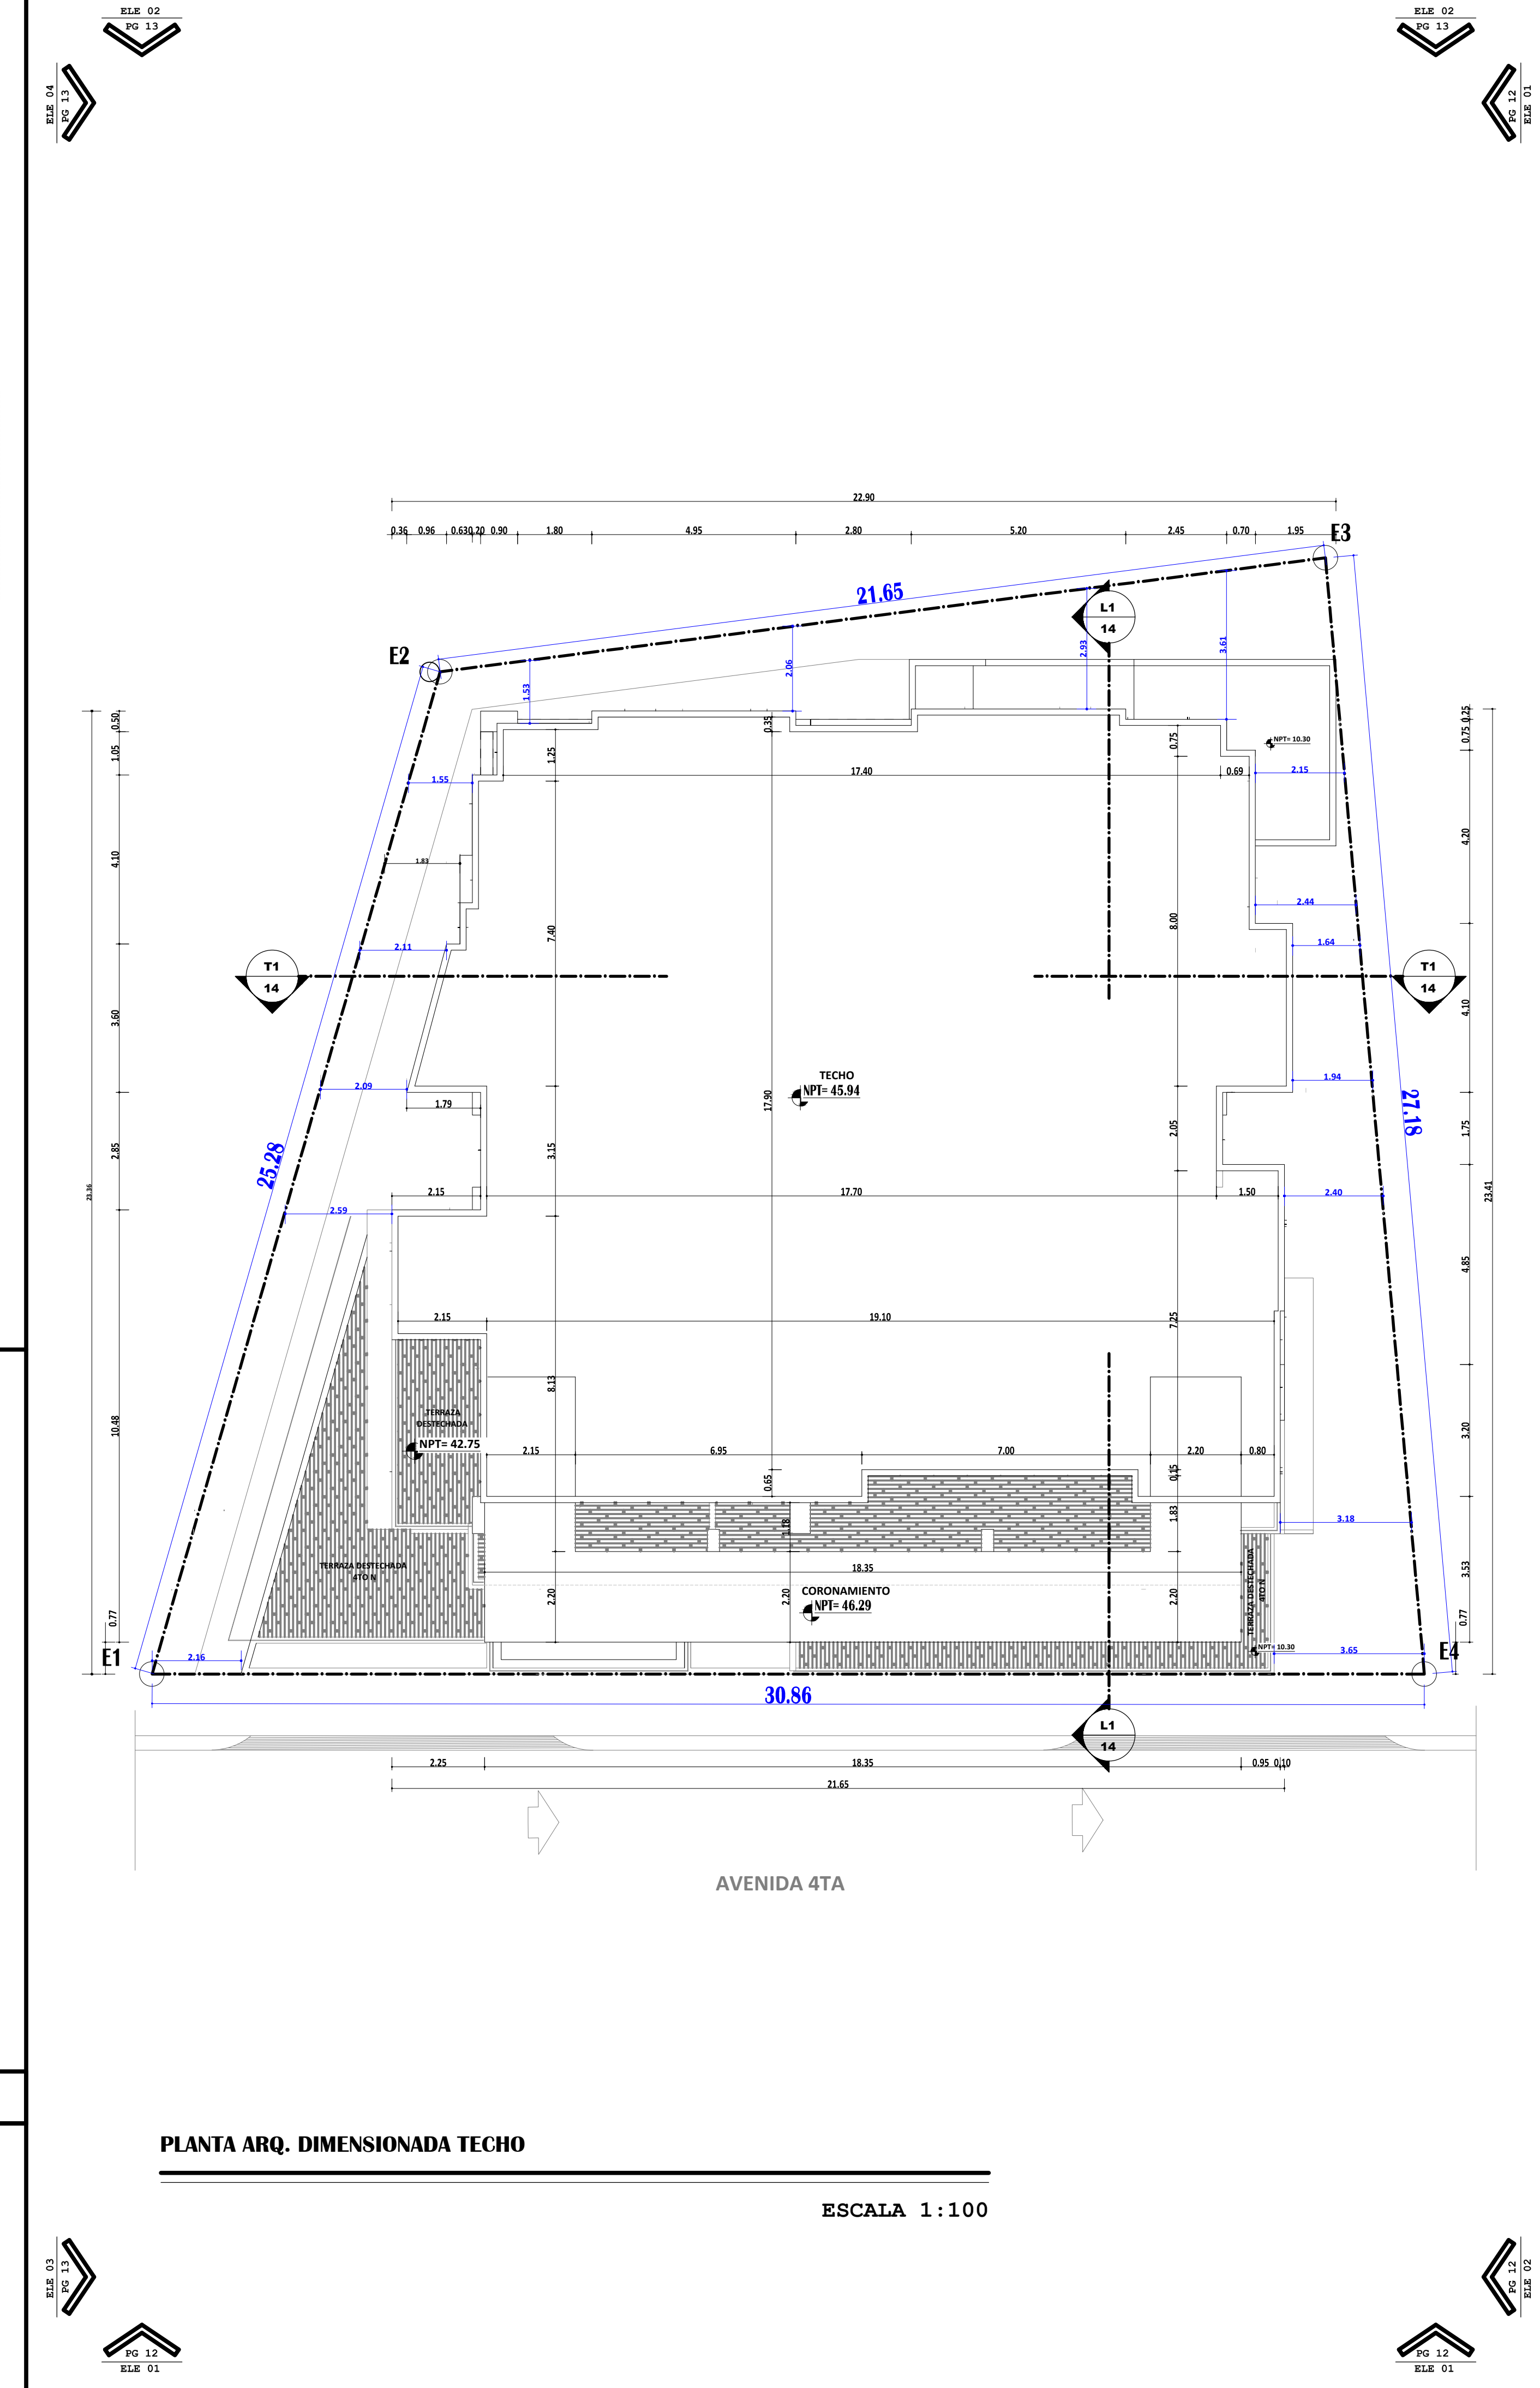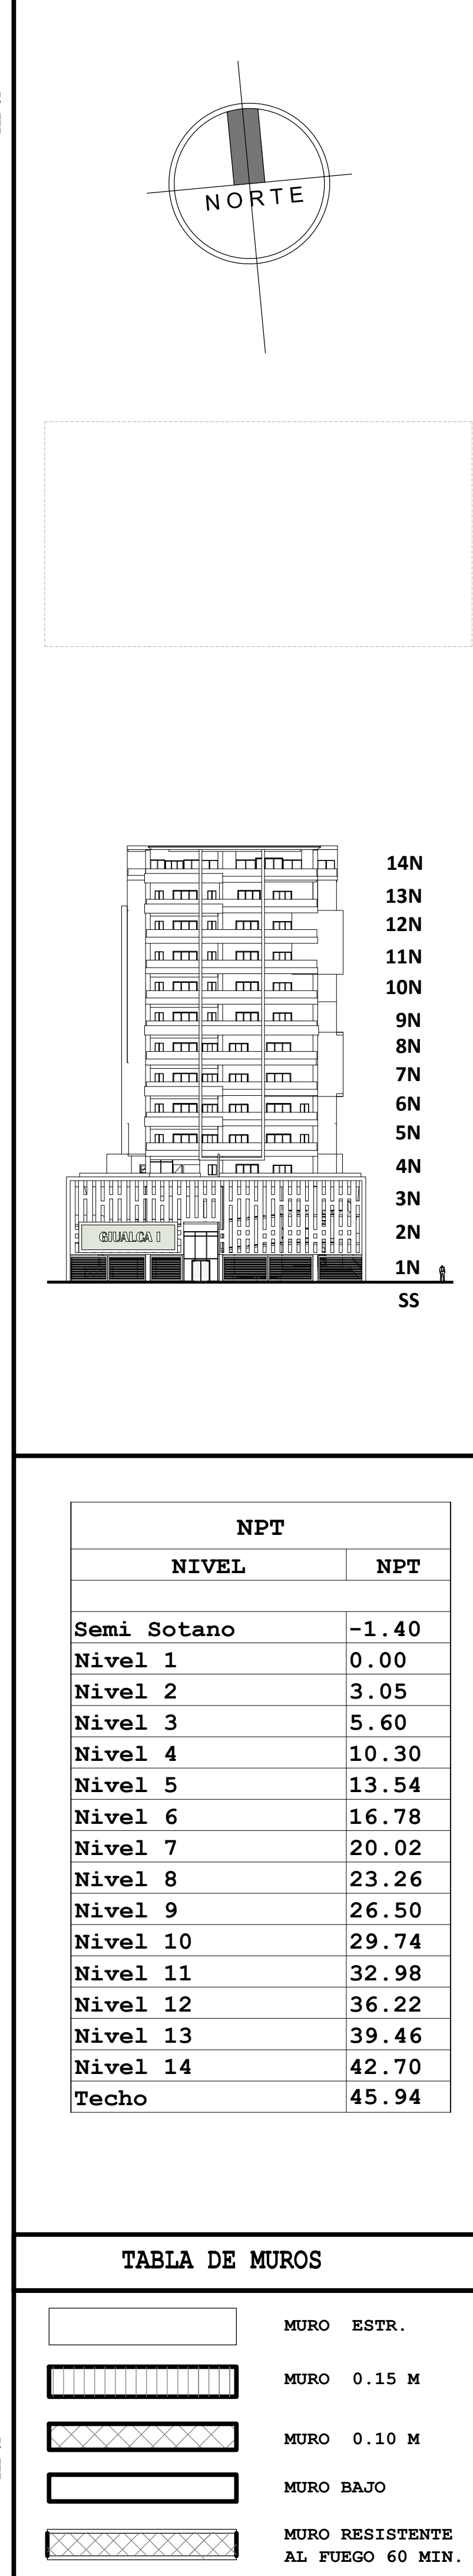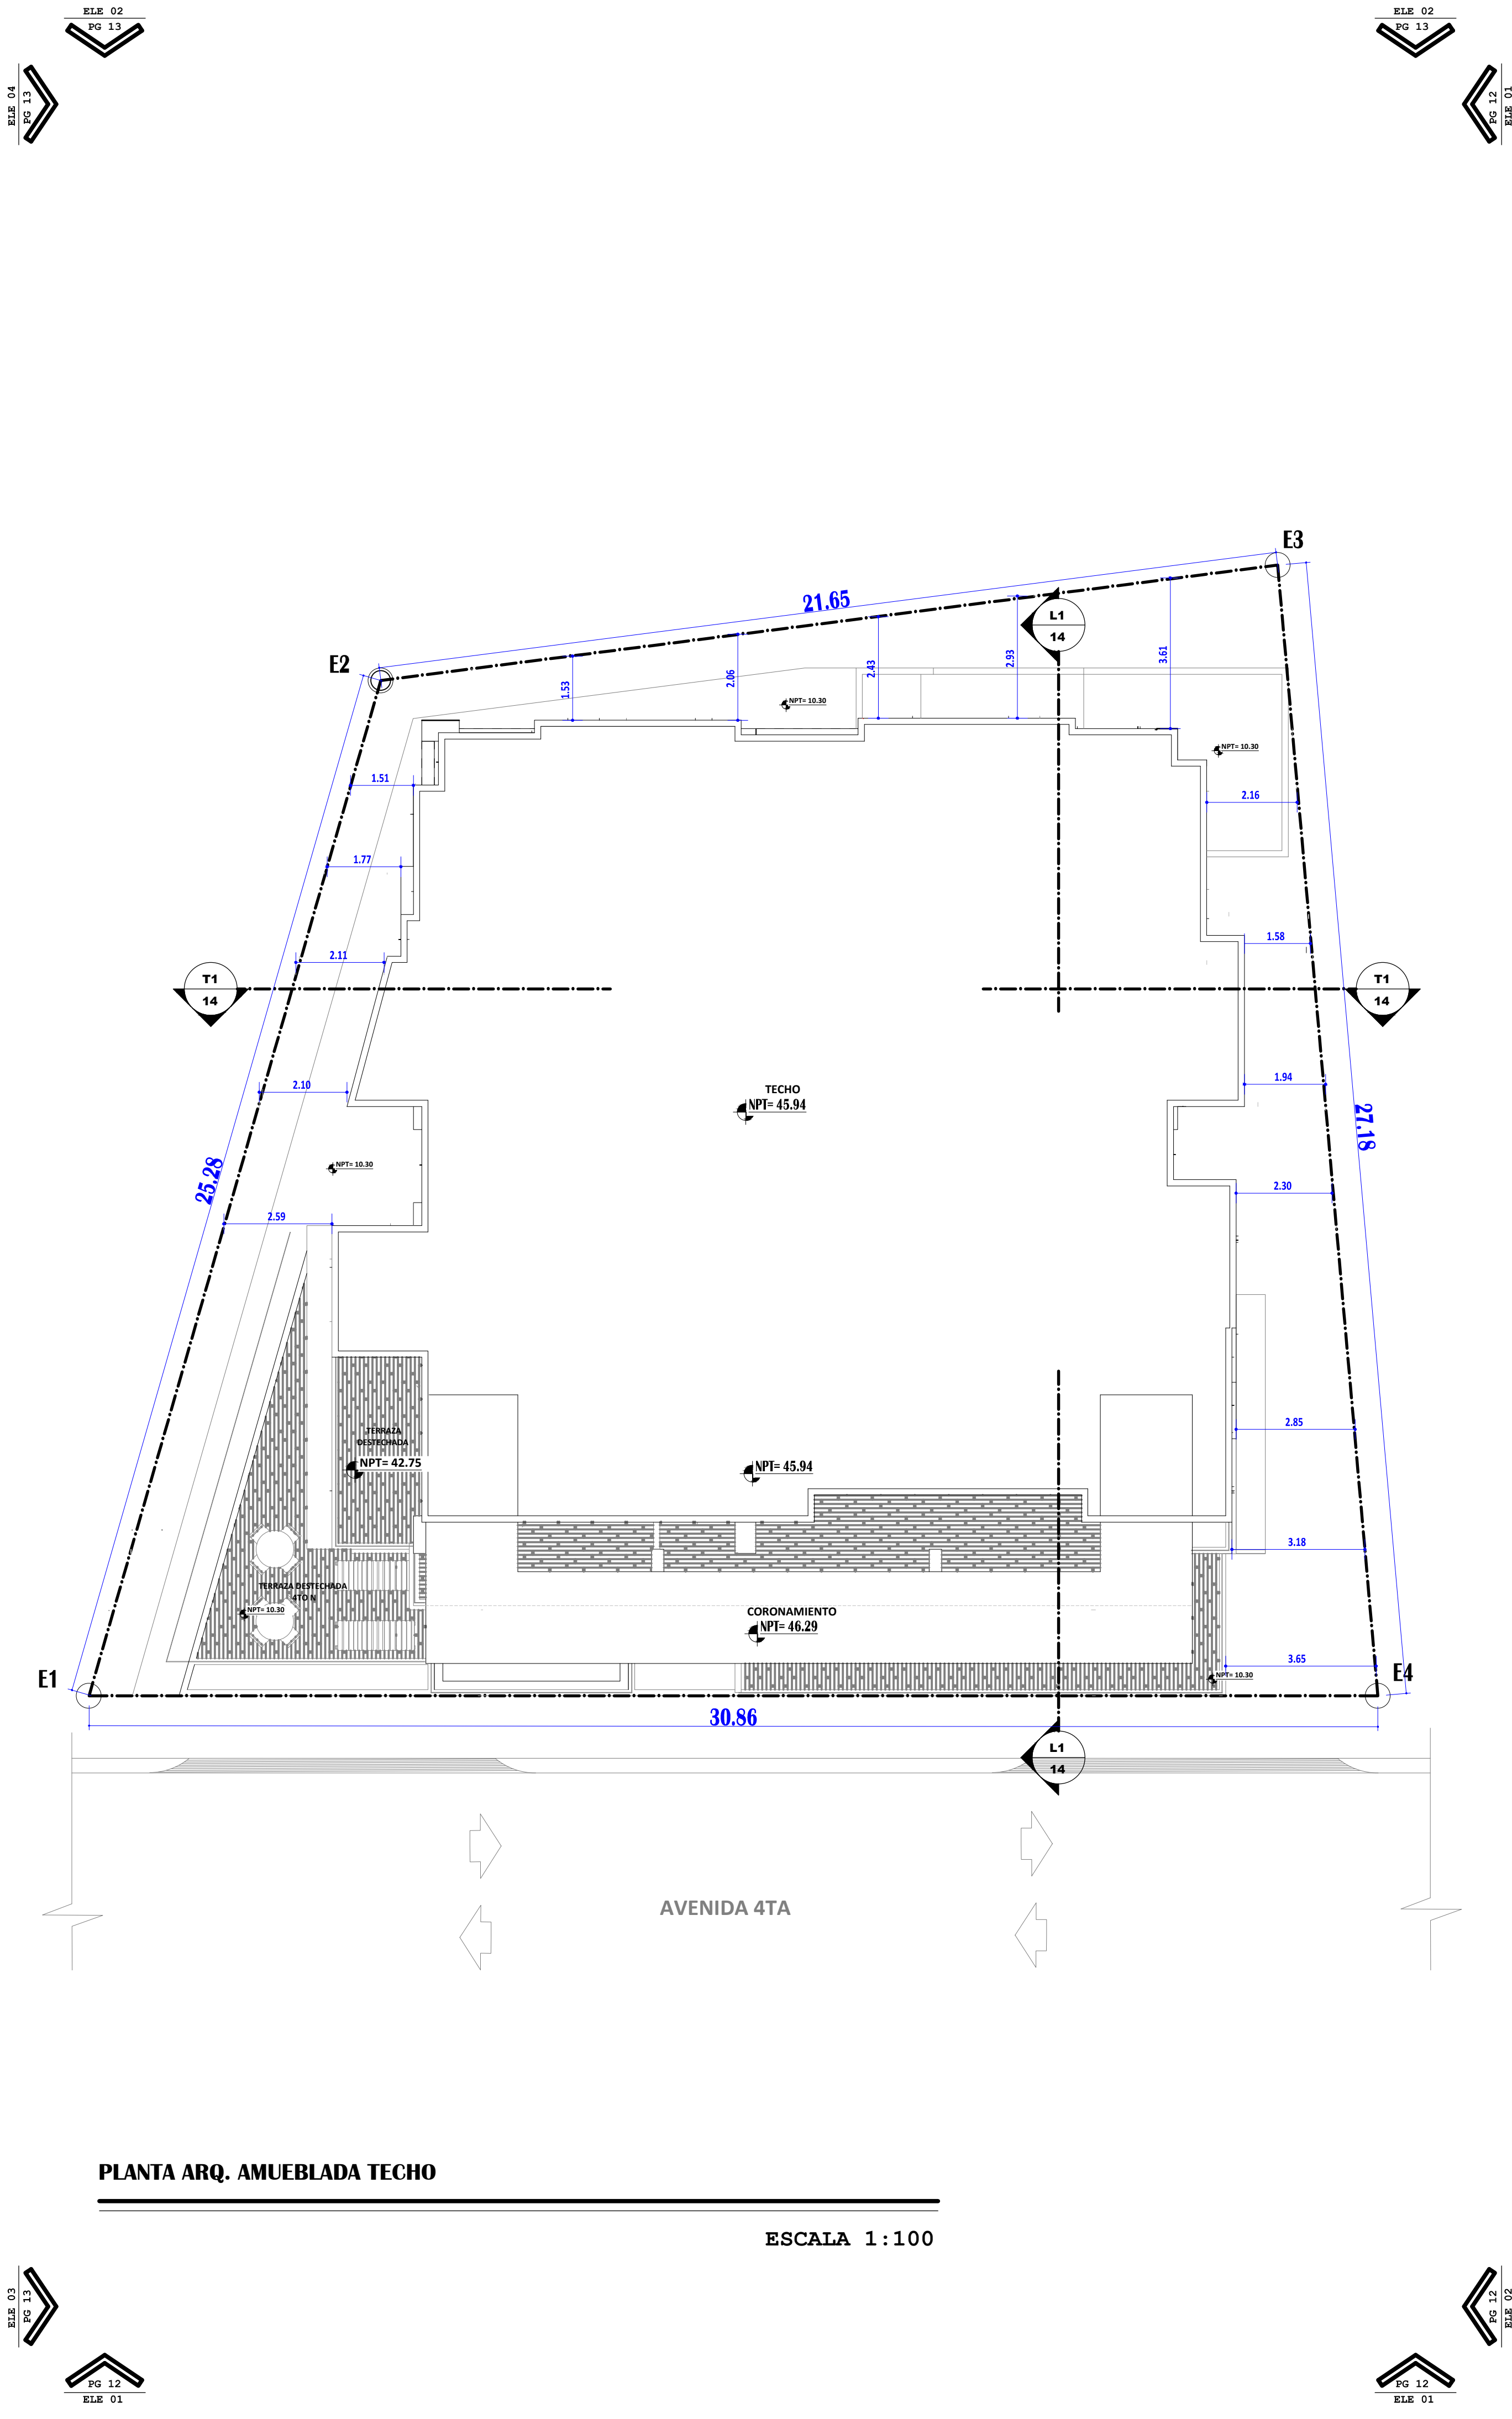

NPT	
NIVEL	NPT
Semi Sotano	-1.40
Nivel 1	0.00
Nivel 2	3.05
Nivel 3	5.60
Nivel 4	10.30
Nivel 5	13.54
Nivel 6	16.78
Nivel 7	20.02
Nivel 8	23.26
Nivel 9	26.50
Nivel 10	29.74
Nivel 11	32.98
Nivel 12	36.22
Nivel 13	39.46
Nivel 14	42.70
Techo	45.94


TABLA DE MUROS

	MURO ESTR.
	MURO 0.15 M
	MURO 0.10 M
	MURO BAJO
	MURO RESISTENTE AL FUEGO 60 MIN.

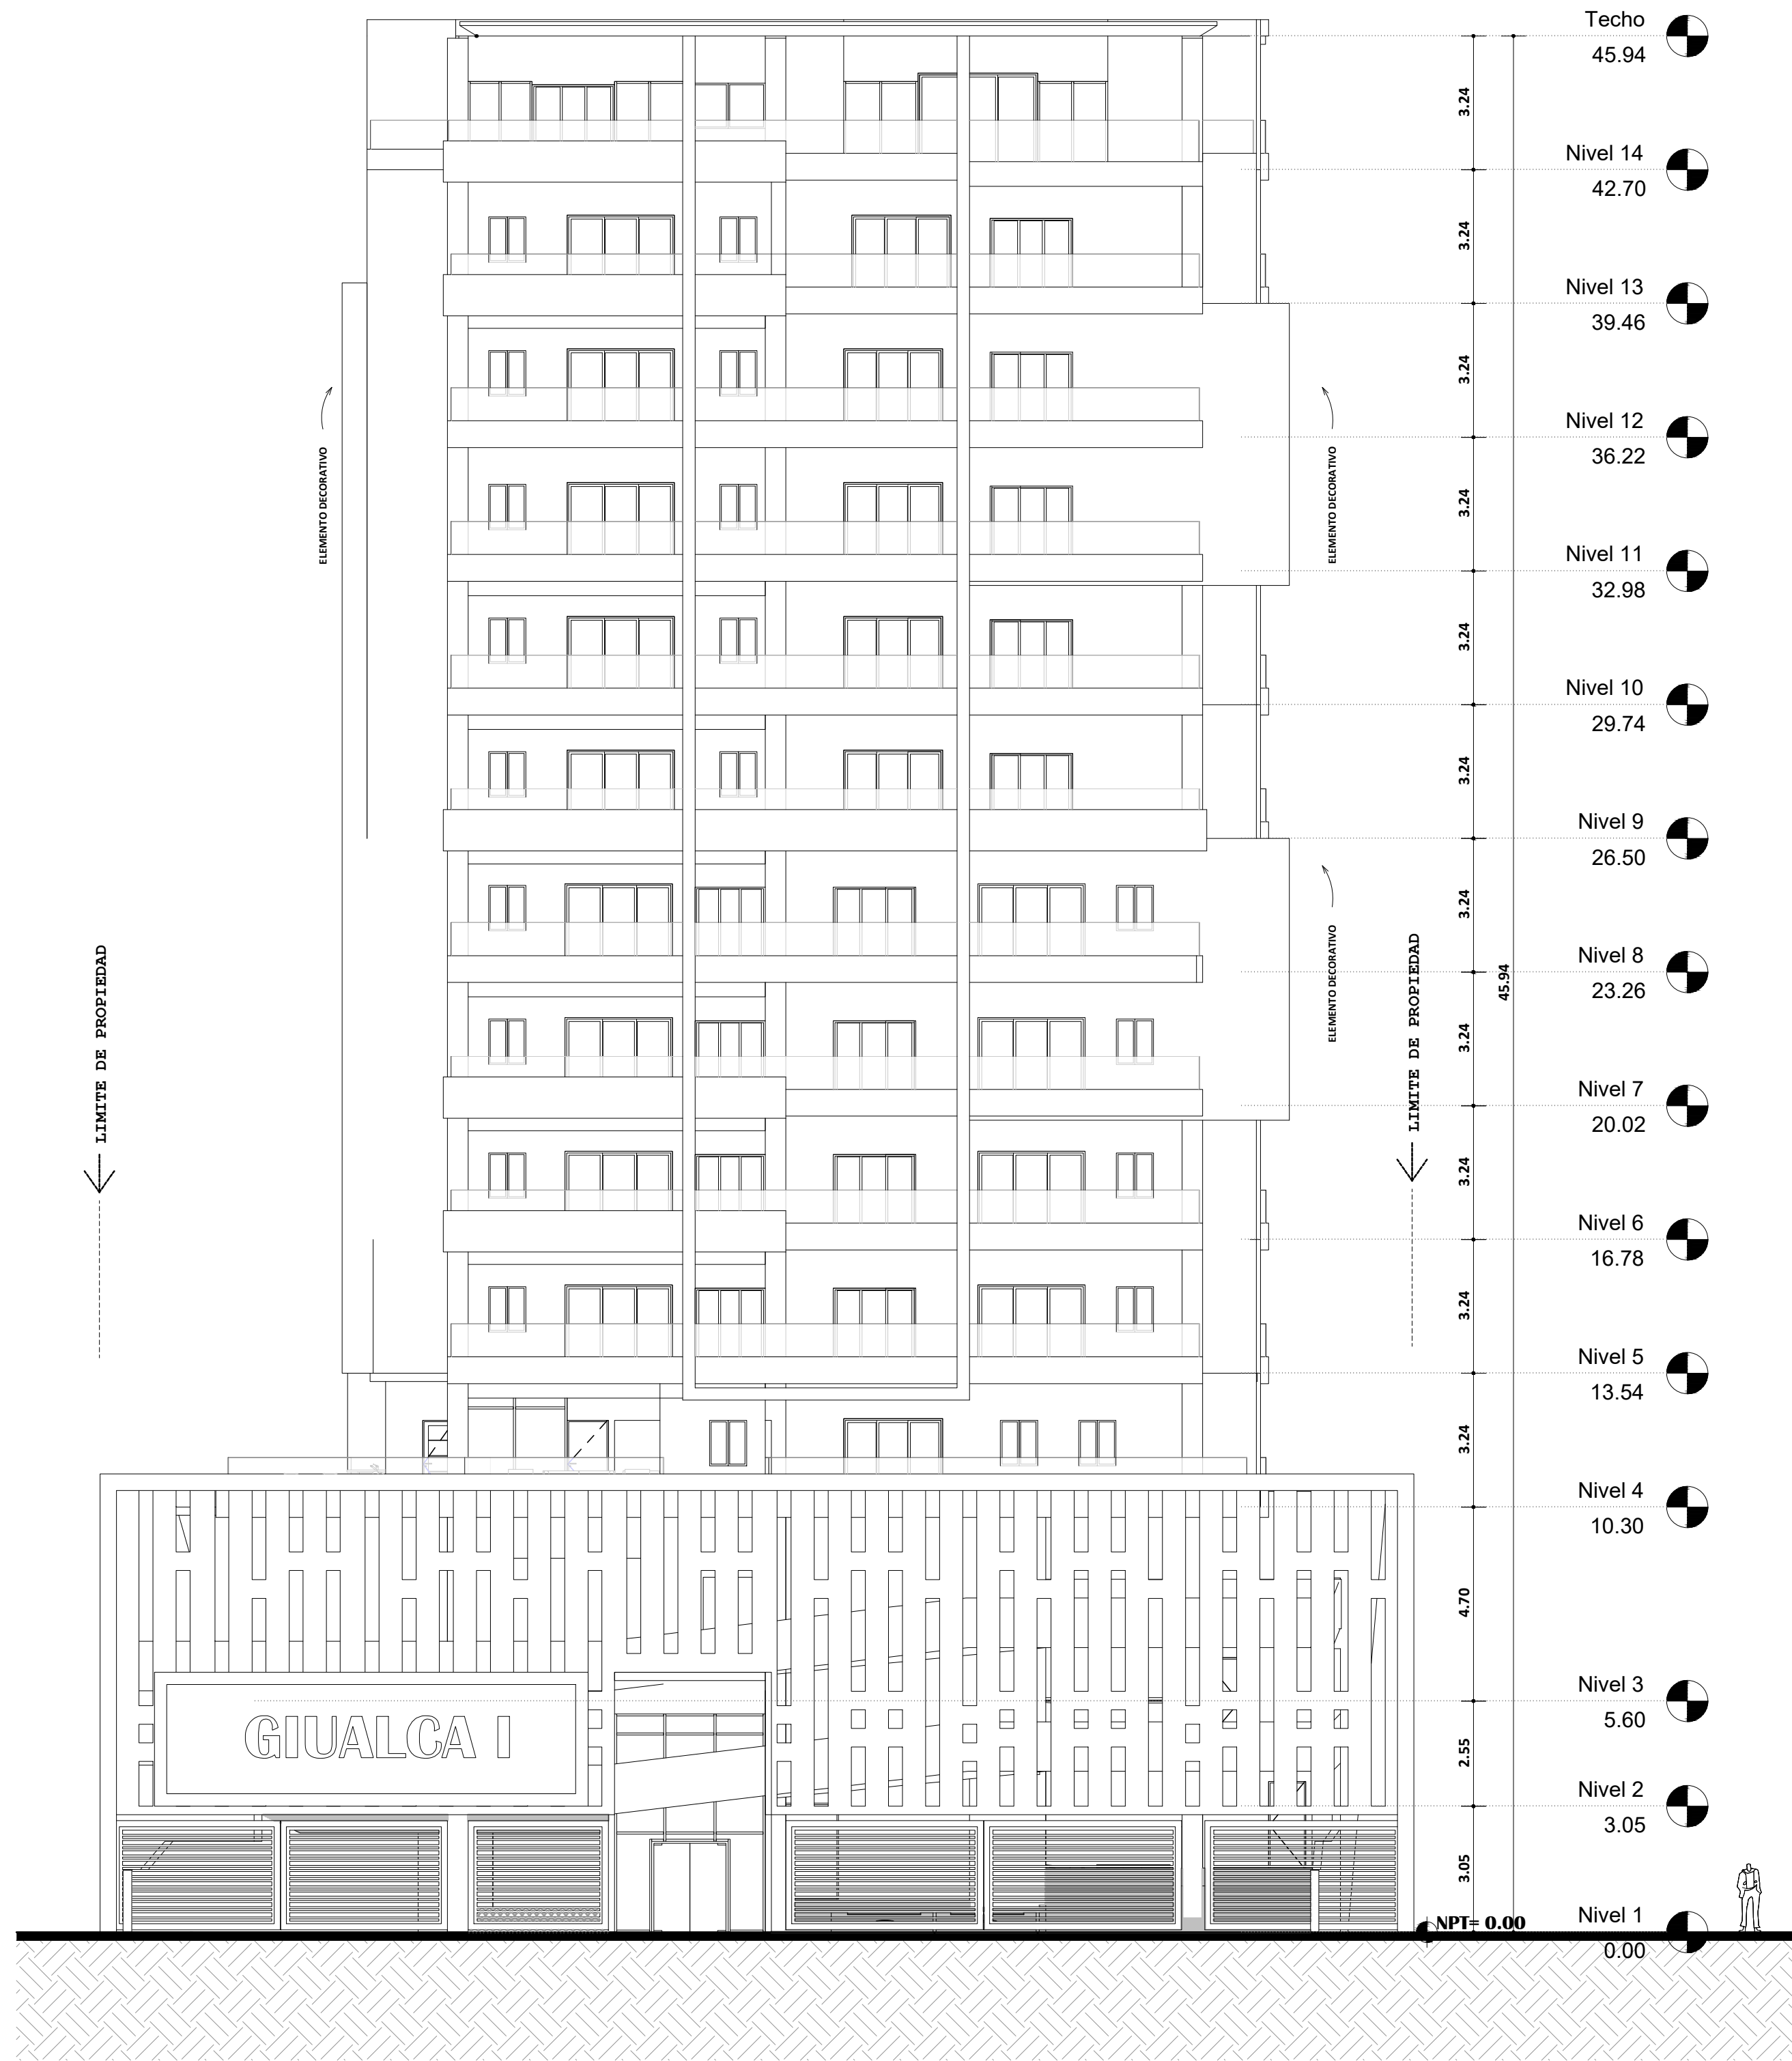

ELEVACION FRONTAL

ESCALA 1:125

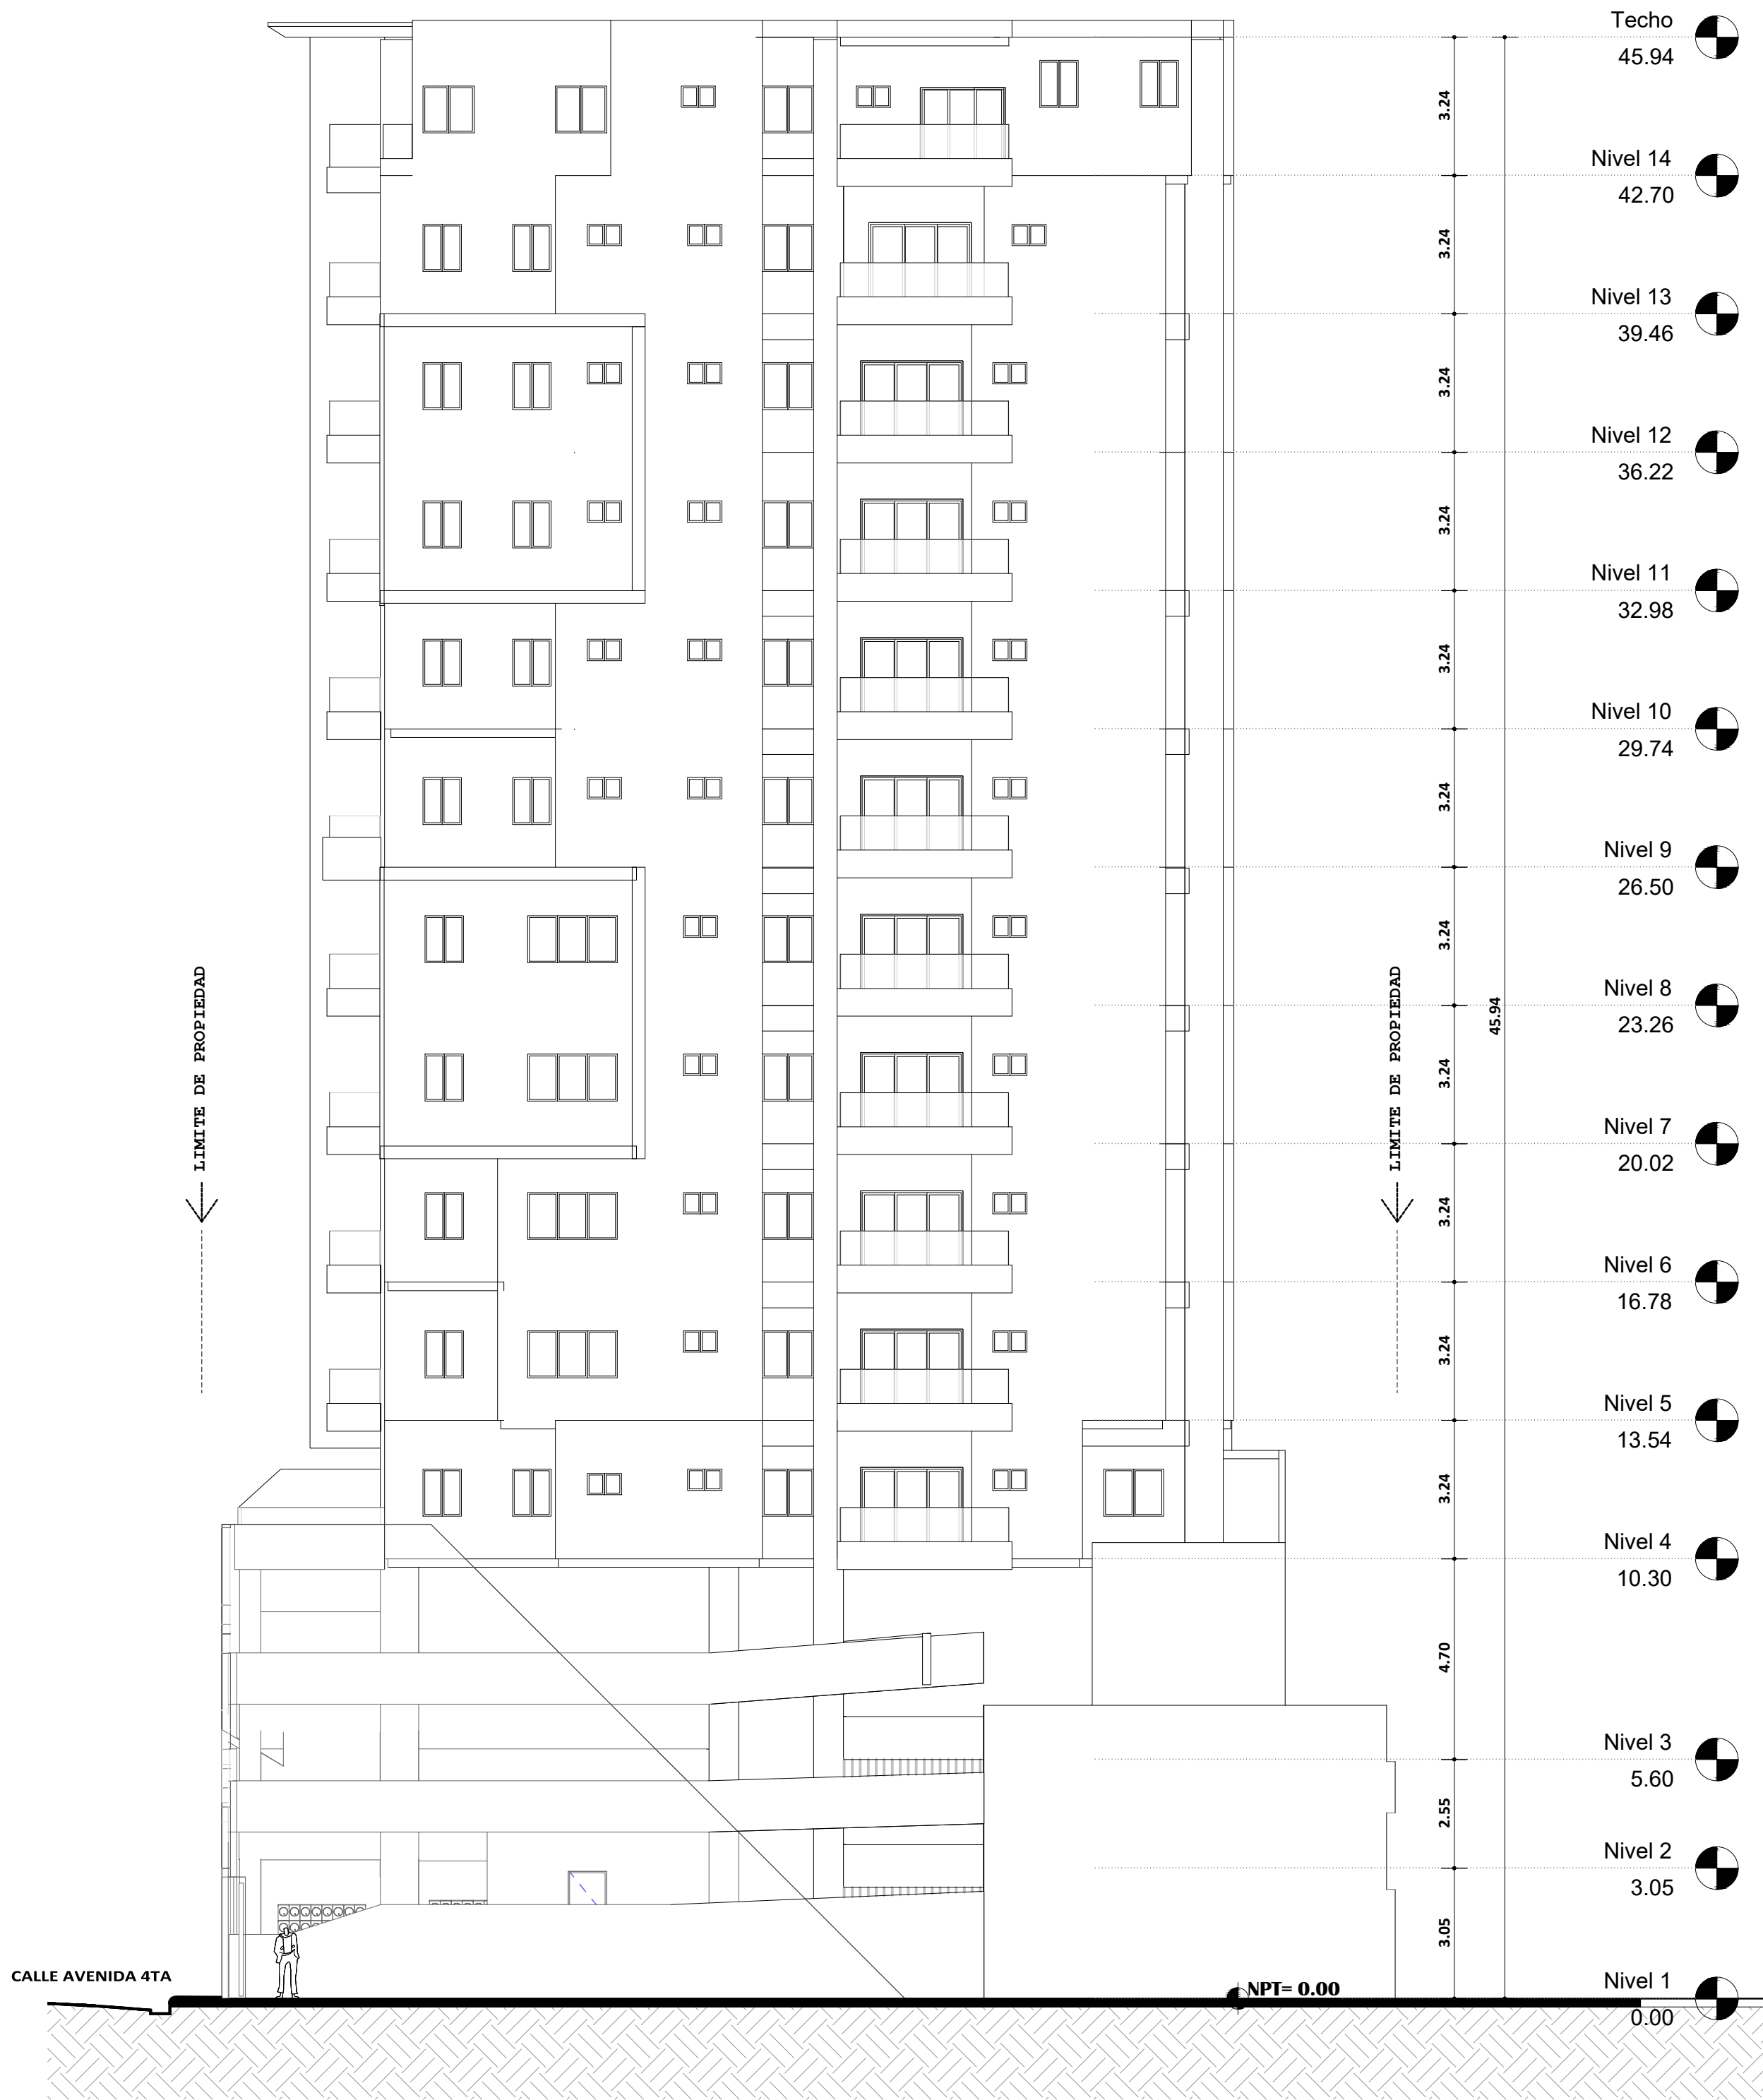


ELEVACION LATERAL DERECHA

ESCALA 1:125



ELEVACION POSTERIOR

ESCALA 1:125

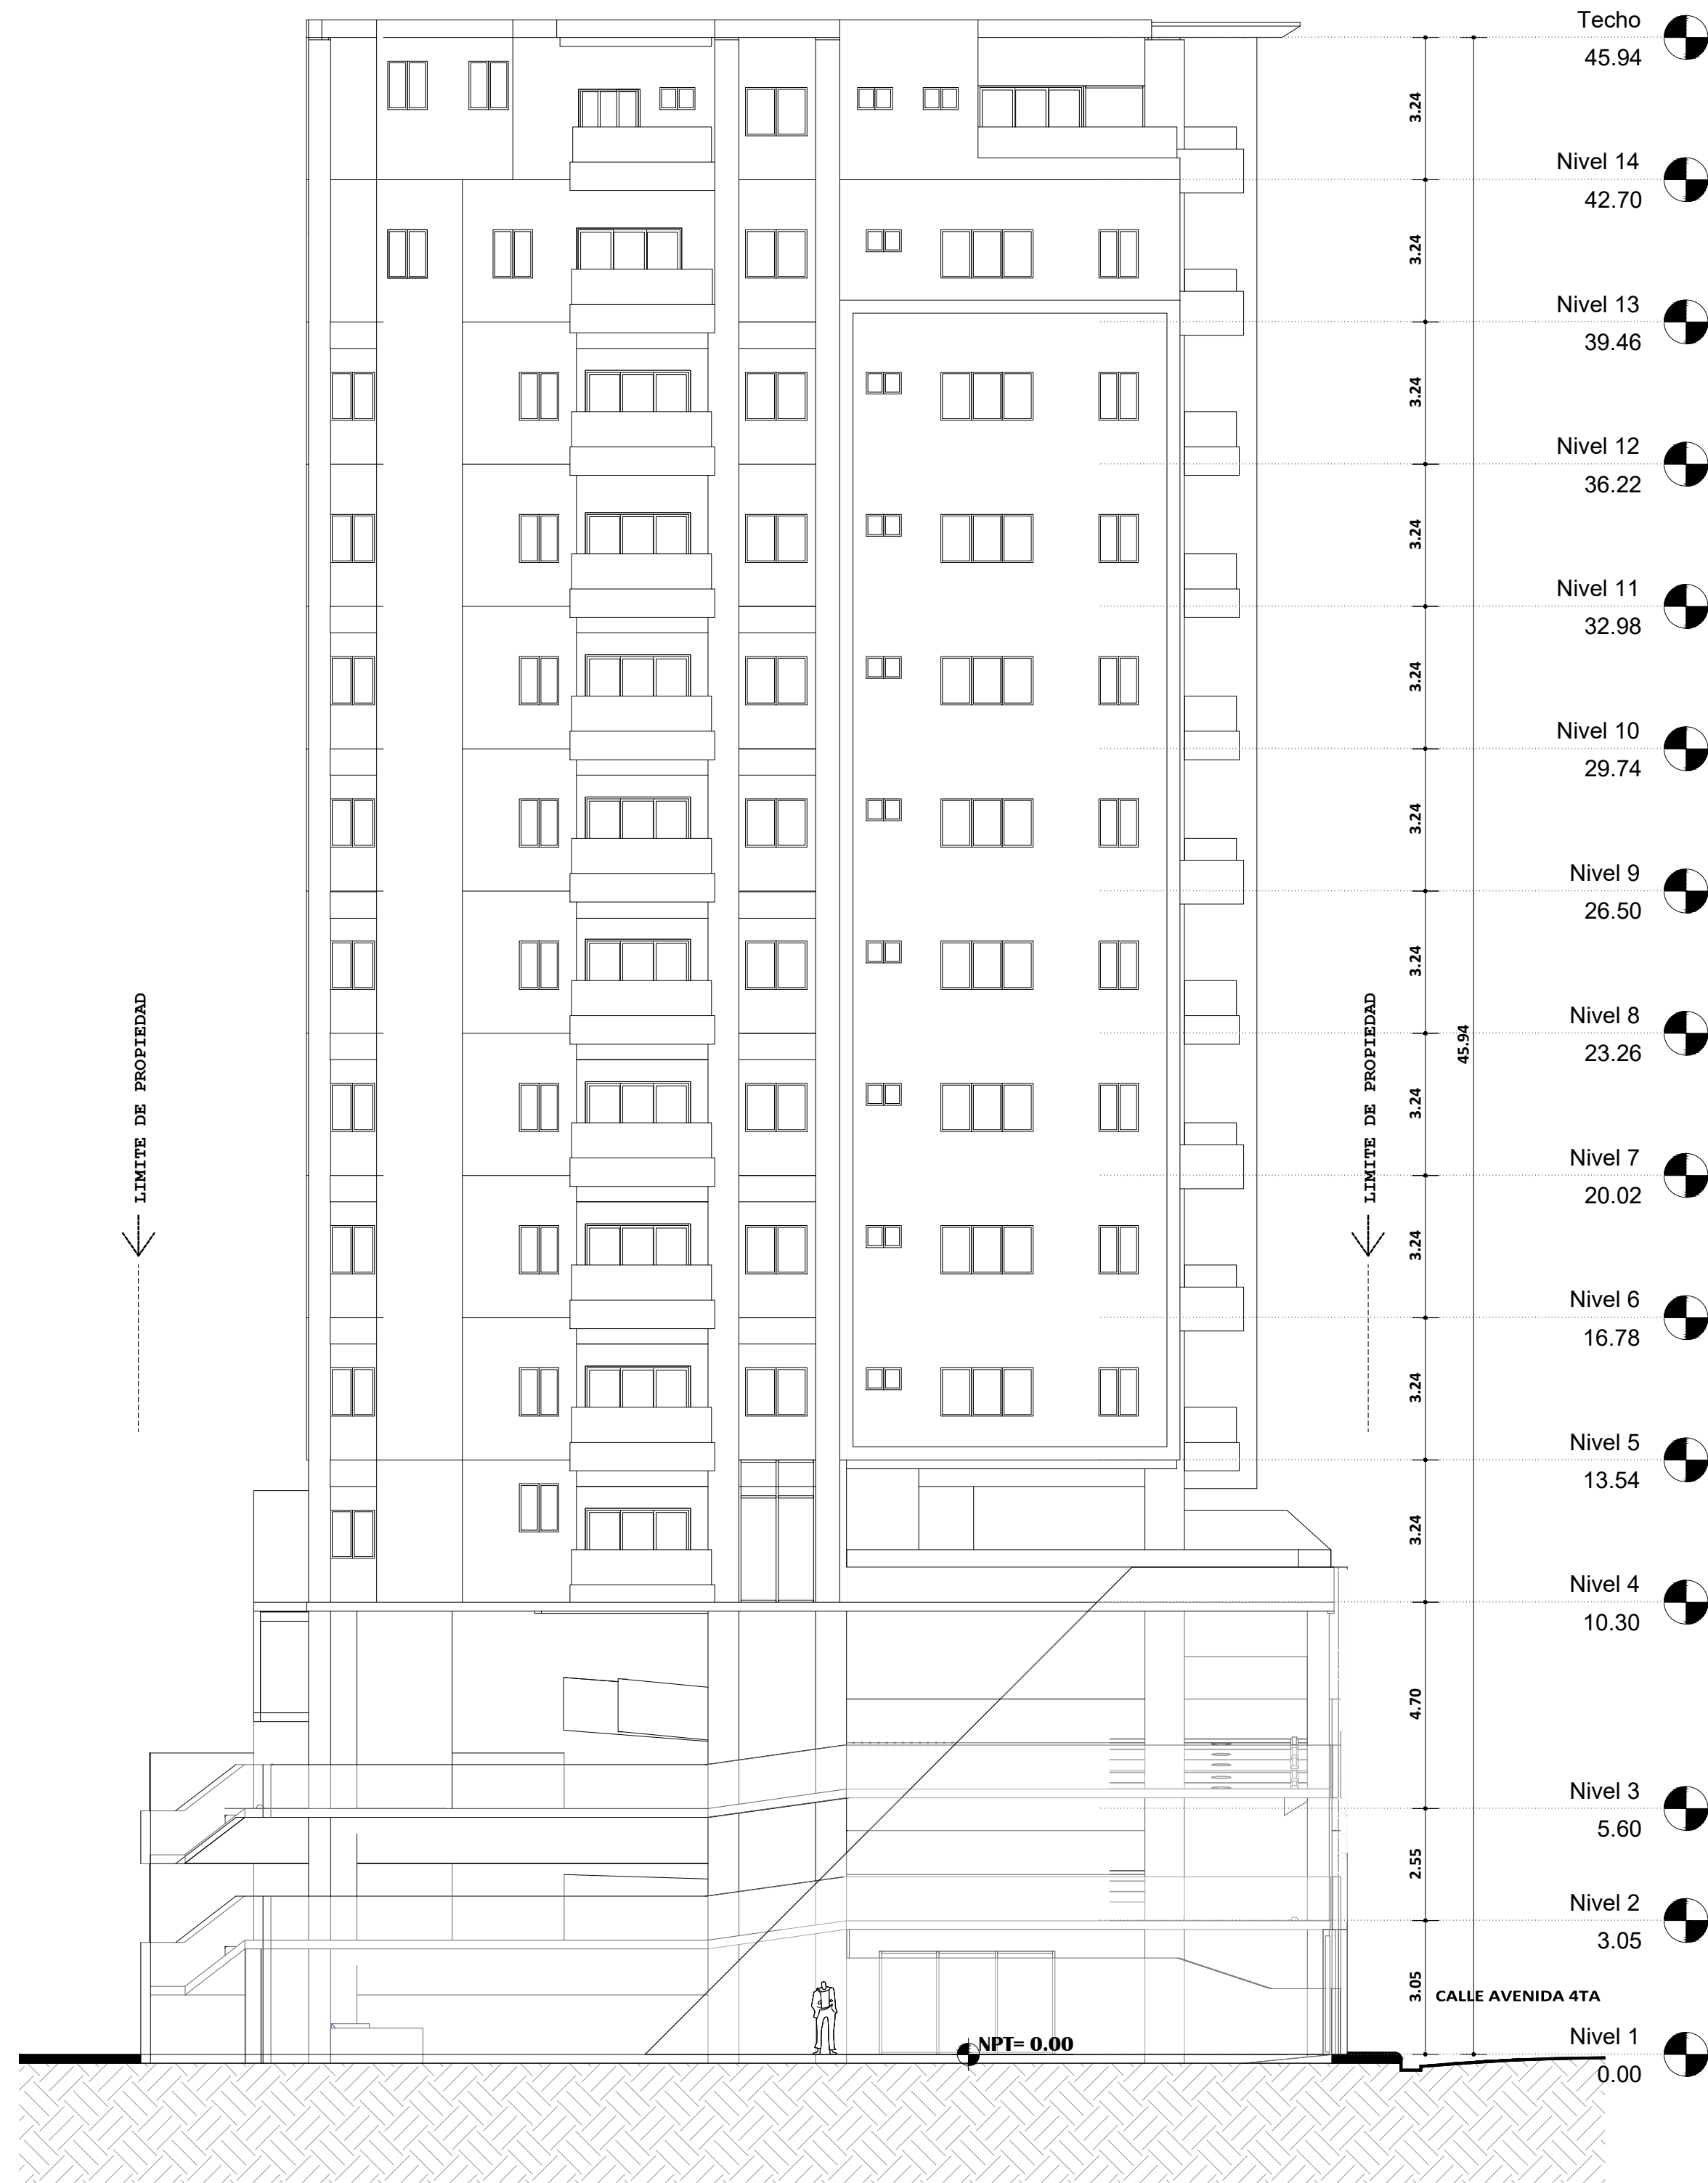

ELEVACION LATERAL IZQUIERDA

ESCALA 1:125